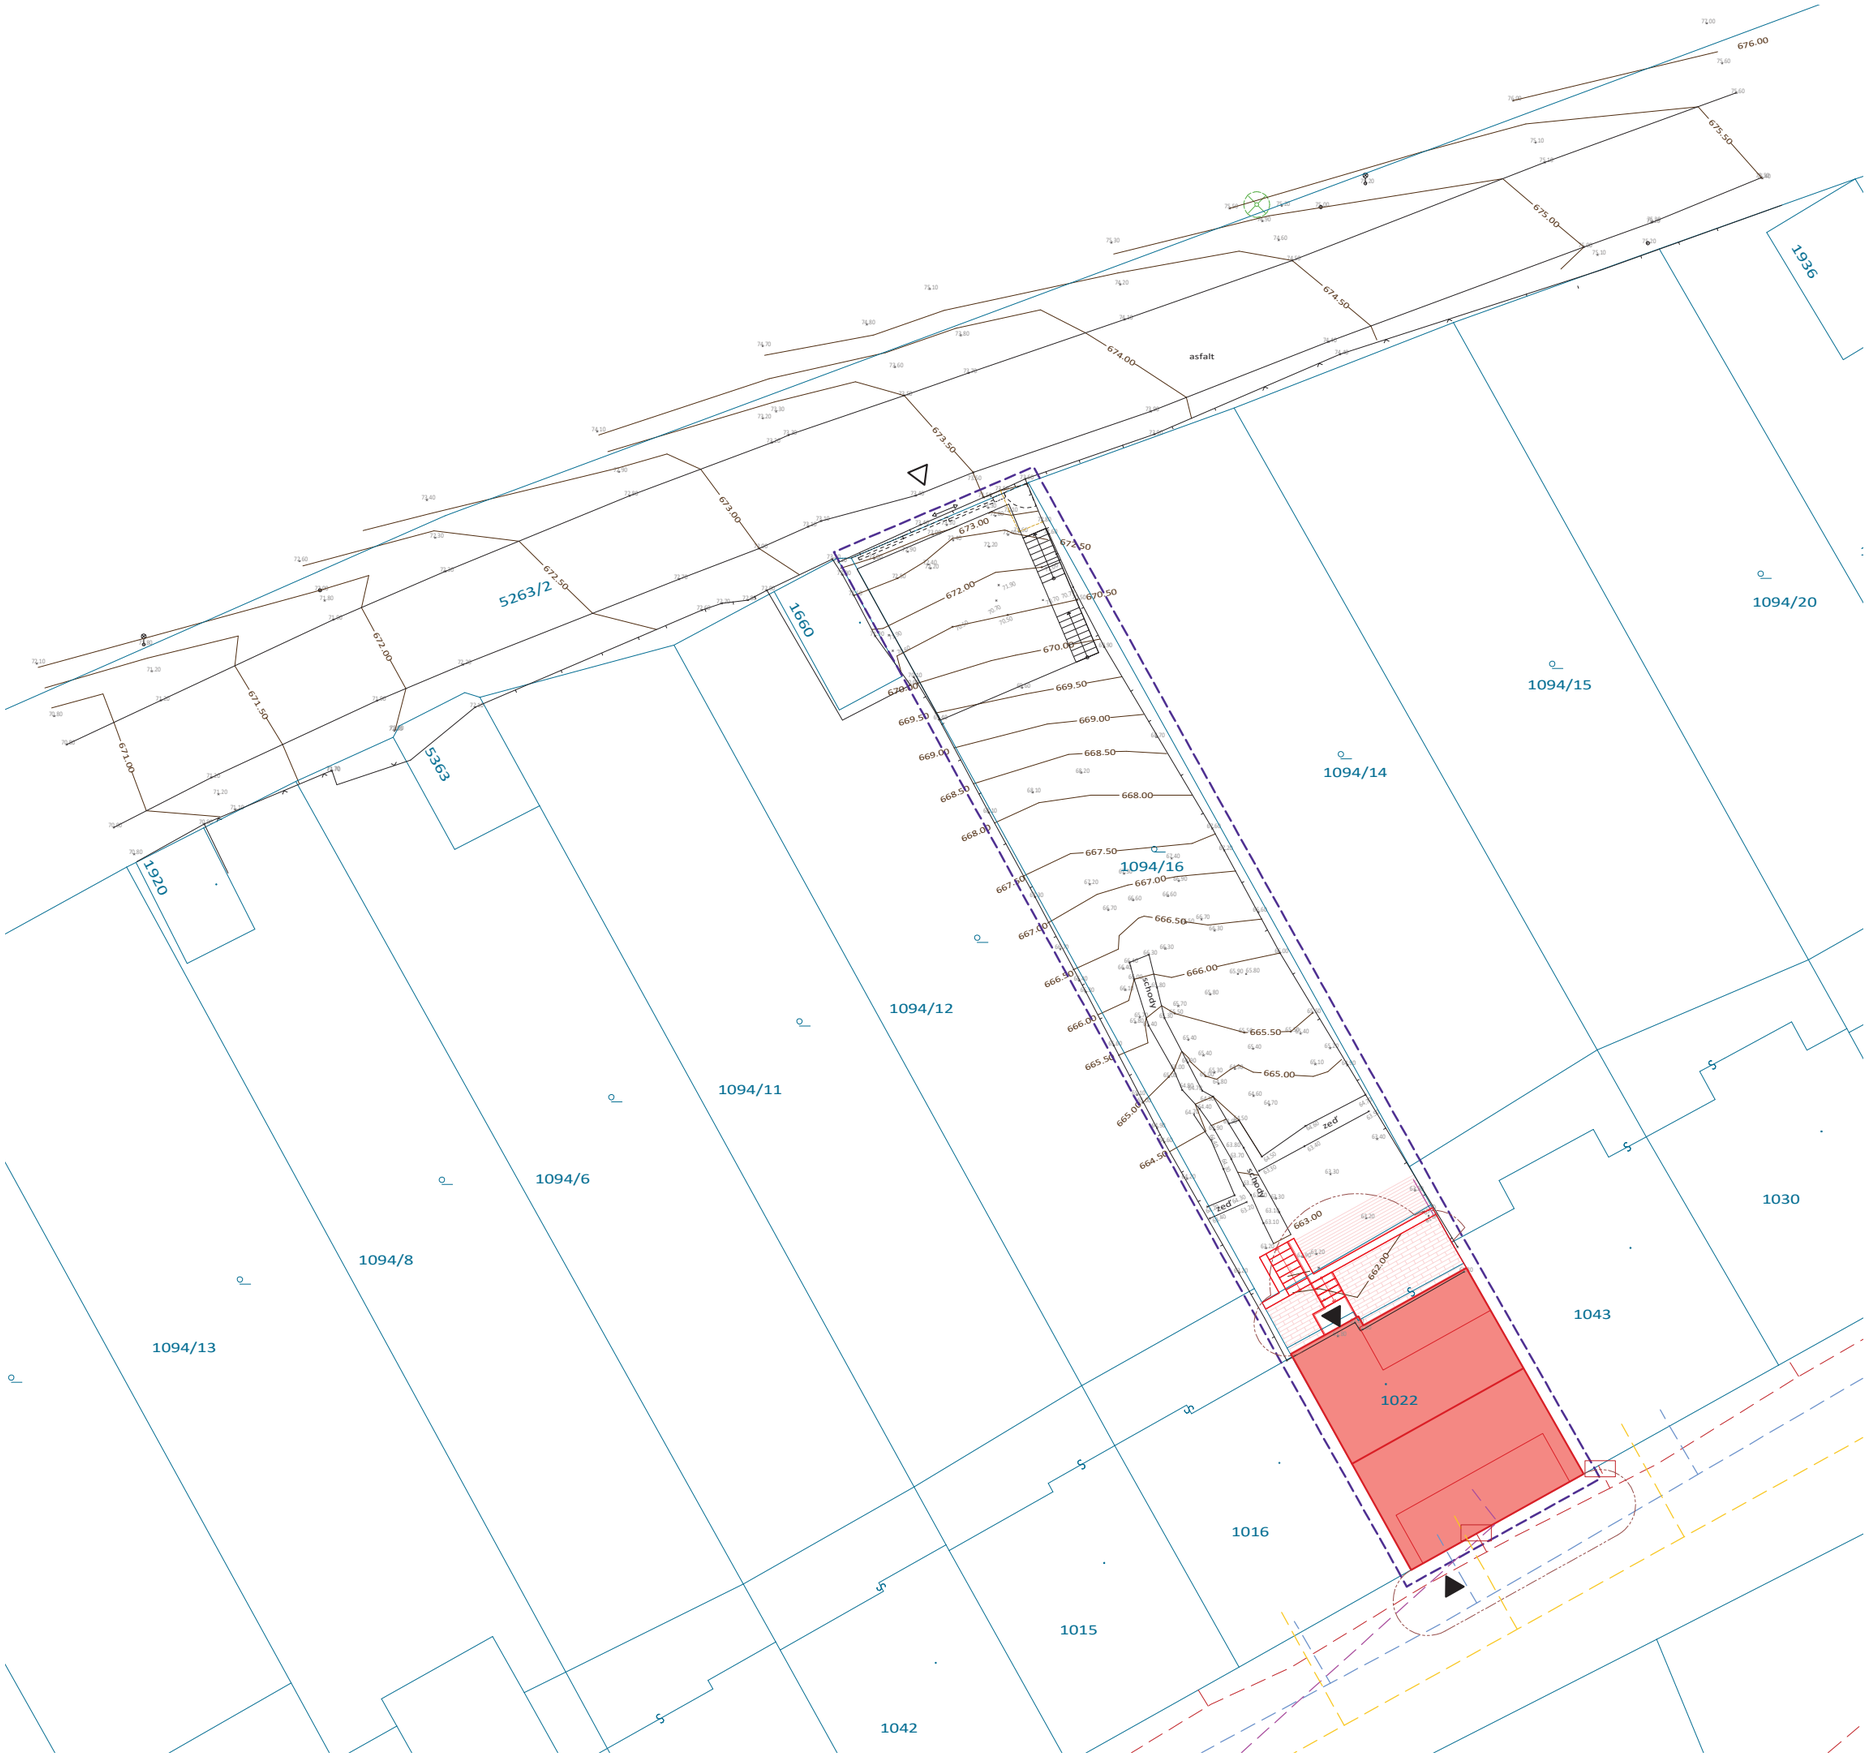

legenda

- stávající objekt RD - stavebně upravovaný
- dotčený pozemek
- katastrální mapa
- Ploty
- vstup / vjezd
- zpevněné plochy - dlažba
- zpevněné plochy - terasa
- požárně nebezpečný prostor

legenda - sítě

- silnoproud - stávající
- silnoproud - návrh
- EP elektroinstalační pilířek - stávající
- PS pojistková skříň - návrh
- RE rozvaděč elektroměrový - návrh
- vodovod - stávající
- vodovod - návrh
- vodovod - objekty na povrchu
- studna - stávající
- VŠ vodoměrná šachta - návrh
- kanalizace splašková - stávající
- kanalizace splašková - návrh
- AK akumulační nádrž / bezodtoková jímka - návrh
- Š revizní šachta - návrh
- kanalizace dešťová - stávající
- kanalizace dešťová - návrh
- AK akumulační nádrž na dešťovou vodu - návrh
- Š revizní šachta - návrh
- plynovod (GasNet) - stávající
- slaboproud (Cetin) - stávající

revize	datum	popis
02		
01		
00	12/2025	vydání dokumentace

Stavební úpravy

Řadový rodinný dům Fibichova č.p. 733

parc. č. 1094/16, st.1022, k.ú. Jáchymov [656437]

razítko/podpis
autorizovaný projektant

Ing. arch. Marek Smolka
tel.: +420 732 618 505, email: smolka@smasharch.cz
autorizace: 05394

Digitálně podepsal Ing. arch. Marek Smolka
Datum: 2026.02.20 22:48:08 +01'00'

paré

investor
Volný Jindřich Mgr.
Fibichova 733, 36251 Jáchymov

zpracovatel projektové dokumentace/generální projektant
SMASH architekti s.r.o.
Vodňanského 1008/2, Břevnov, 169 00 Praha 6
IČO: 17666902

projektový stupeň
dokumentace pro povolení záměru

část
C Situační výkresy

projektant části
Ing. arch. Marek Smolka
tel.: +420 732 618 505, email: smolka@smasharch.cz

název výkresu
Koordinační situační výkres

datum	měřítko	číslo výkresu
12/2025	1:200	**C.3**