



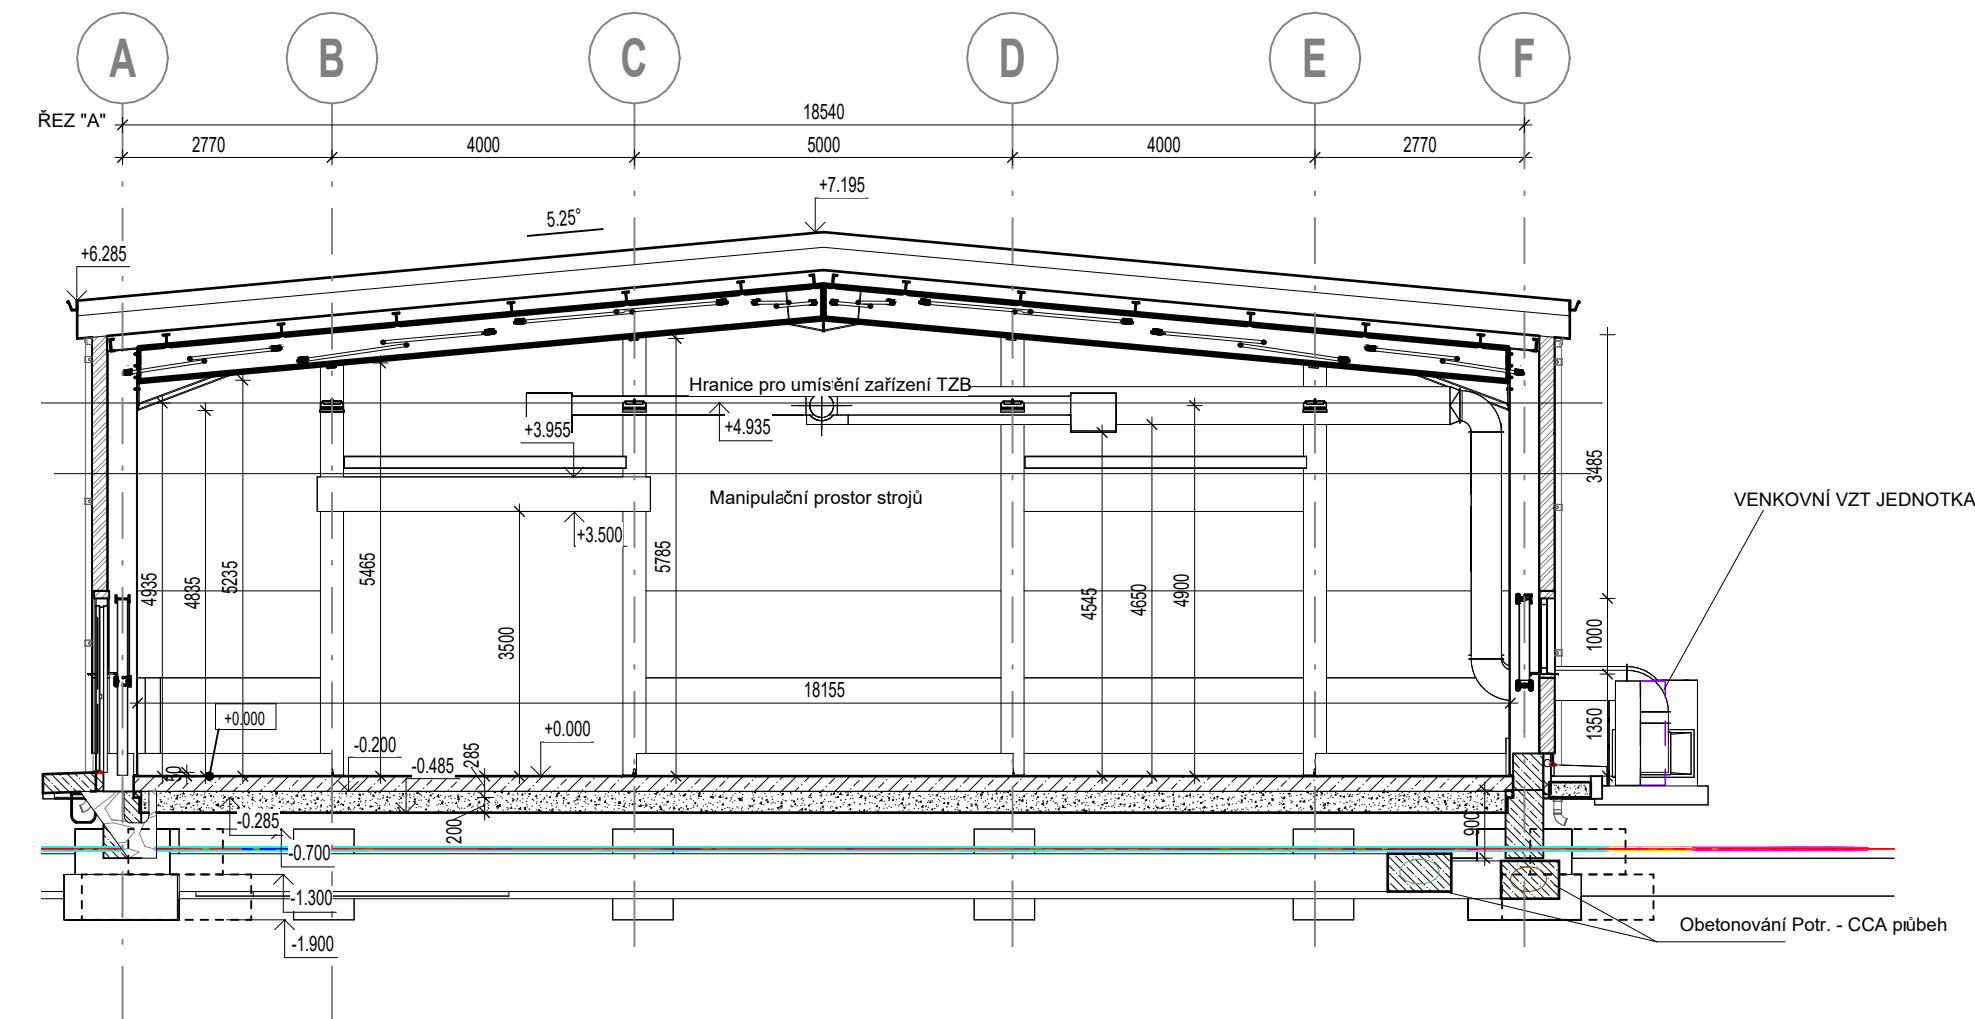

ŘEZ "B"

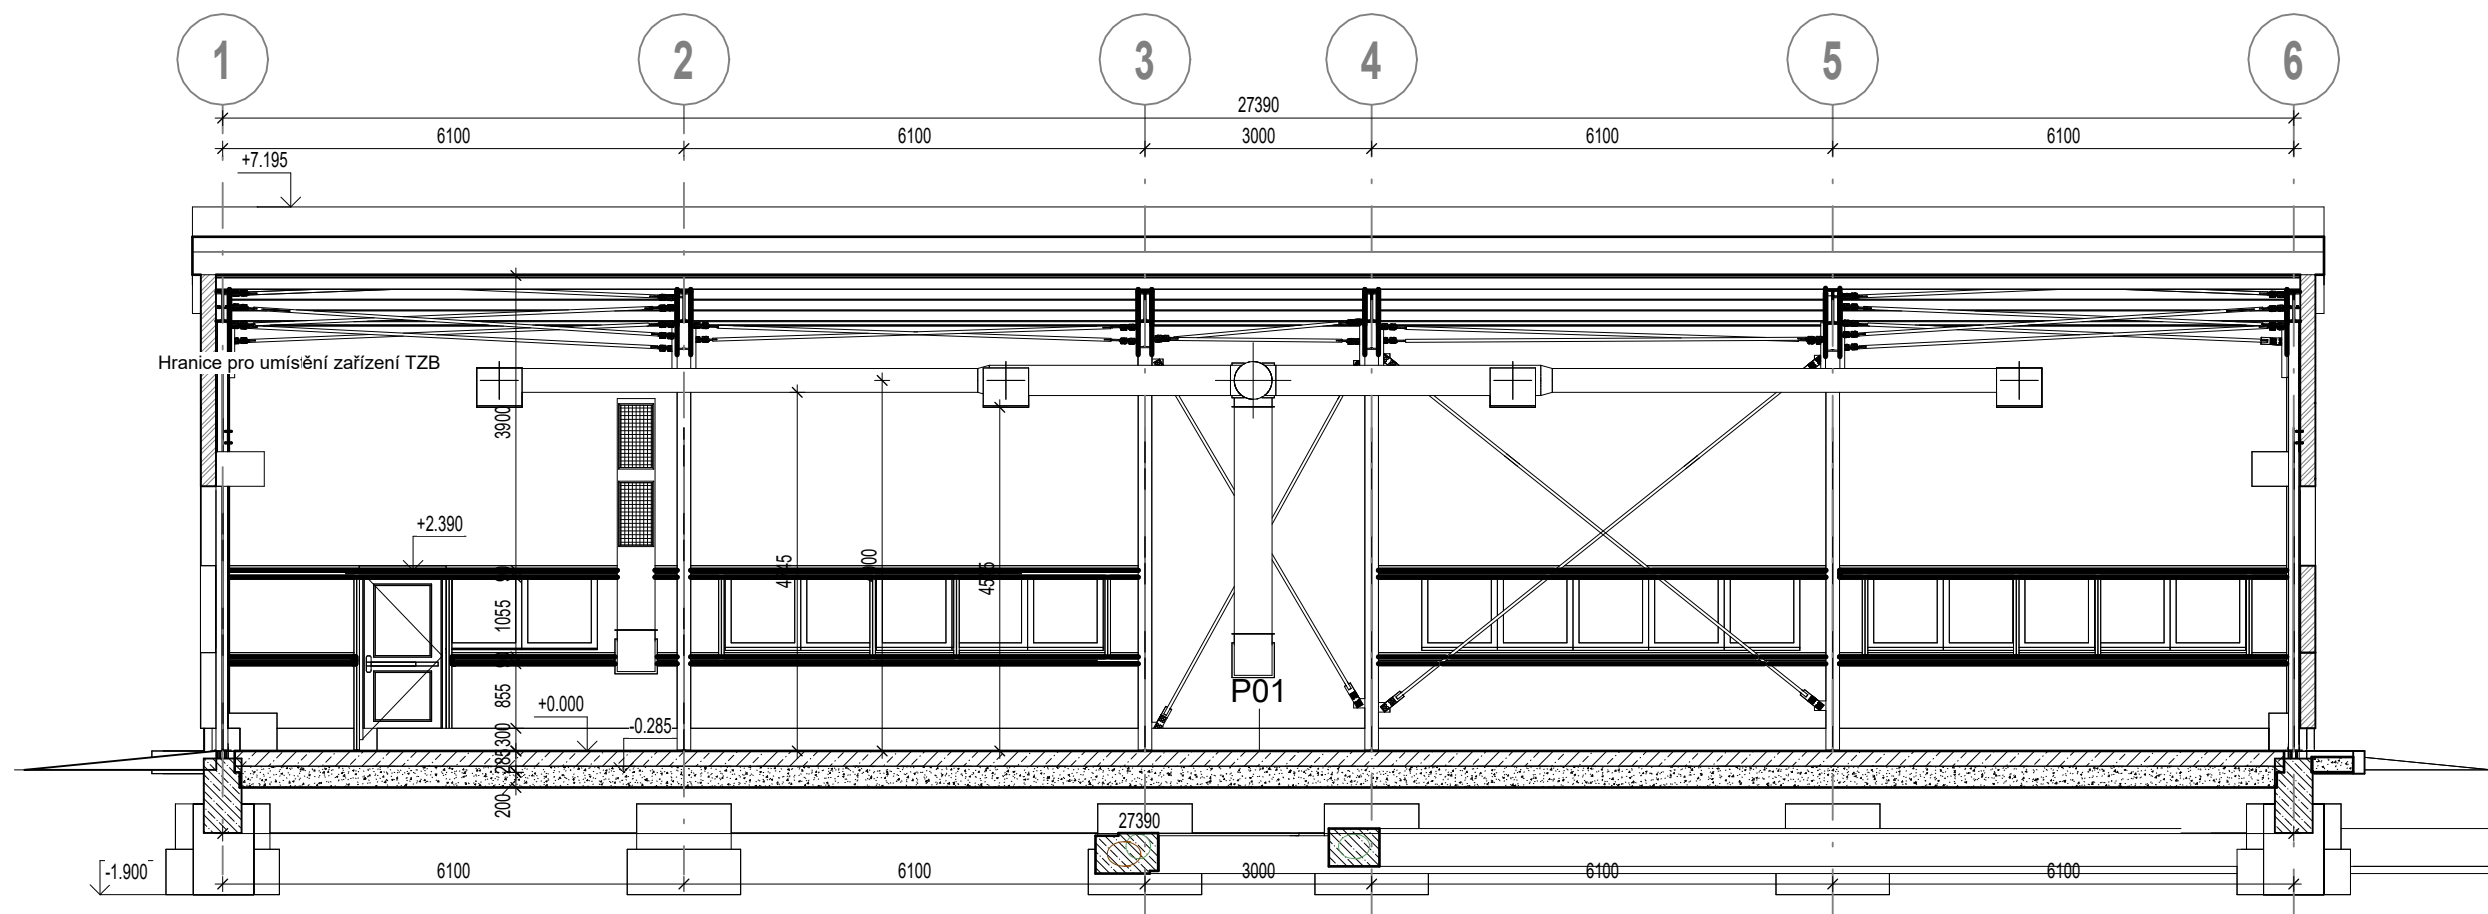

LEGENDA MATERIÁLŮ:

- Obvodový plášť - panely Kingspan s požární odolností EW 15 DP1
- Železobeton
- Beton prostý

HALA HRADEC KRÁLOVÉ

Vážní 857, 50003 Hradec Králové - Slezské
Předměstí

STUPEŇ PROJEKTU +0,000 = +234,690 mm Bpv

DOKUMENTACE PRO POVOLENÍ ZÁMĚRU (DPZ)

ODPOVĚDNÝ PROJEKTANT

Ing.arch. Jakub Volka, ČKA 03947
733 575 363, jakub.volka@basepoint.cz

VYPRACOVAL

Ing. arch. Jakub Volka
Anna Abrahámová
Kristián Pócsik
INVESTOR

SOLAR DISPOREC s.r.o., Praha IČO 19546220
Malostranské náměstí 5/28, Malá Strana (Praha 1),
118 00 Praha

DÍL

D

ČÁST DOKUMENTACE

D.1.1.3

OBSAH VÝKRESU

ŘEZ A, B

MĚŘÍTKO

1:100

DATUM

07/2025

STUPEŇ

DPZ

FORMÁT

2 X A4

1.VYDÁNÍ

07/2025

REVIZE

R01

ZPRACOVATEL ČÁSTI

basepoint s.r.o.
V Benátkách 2350/6
149 00, Praha 4
www.basepoint.cz

GENERÁLNÍ PROJEKTANT

basepoint s.r.o.
V Benátkách 2350/6
149 00, Praha 4
www.basepoint.cz

