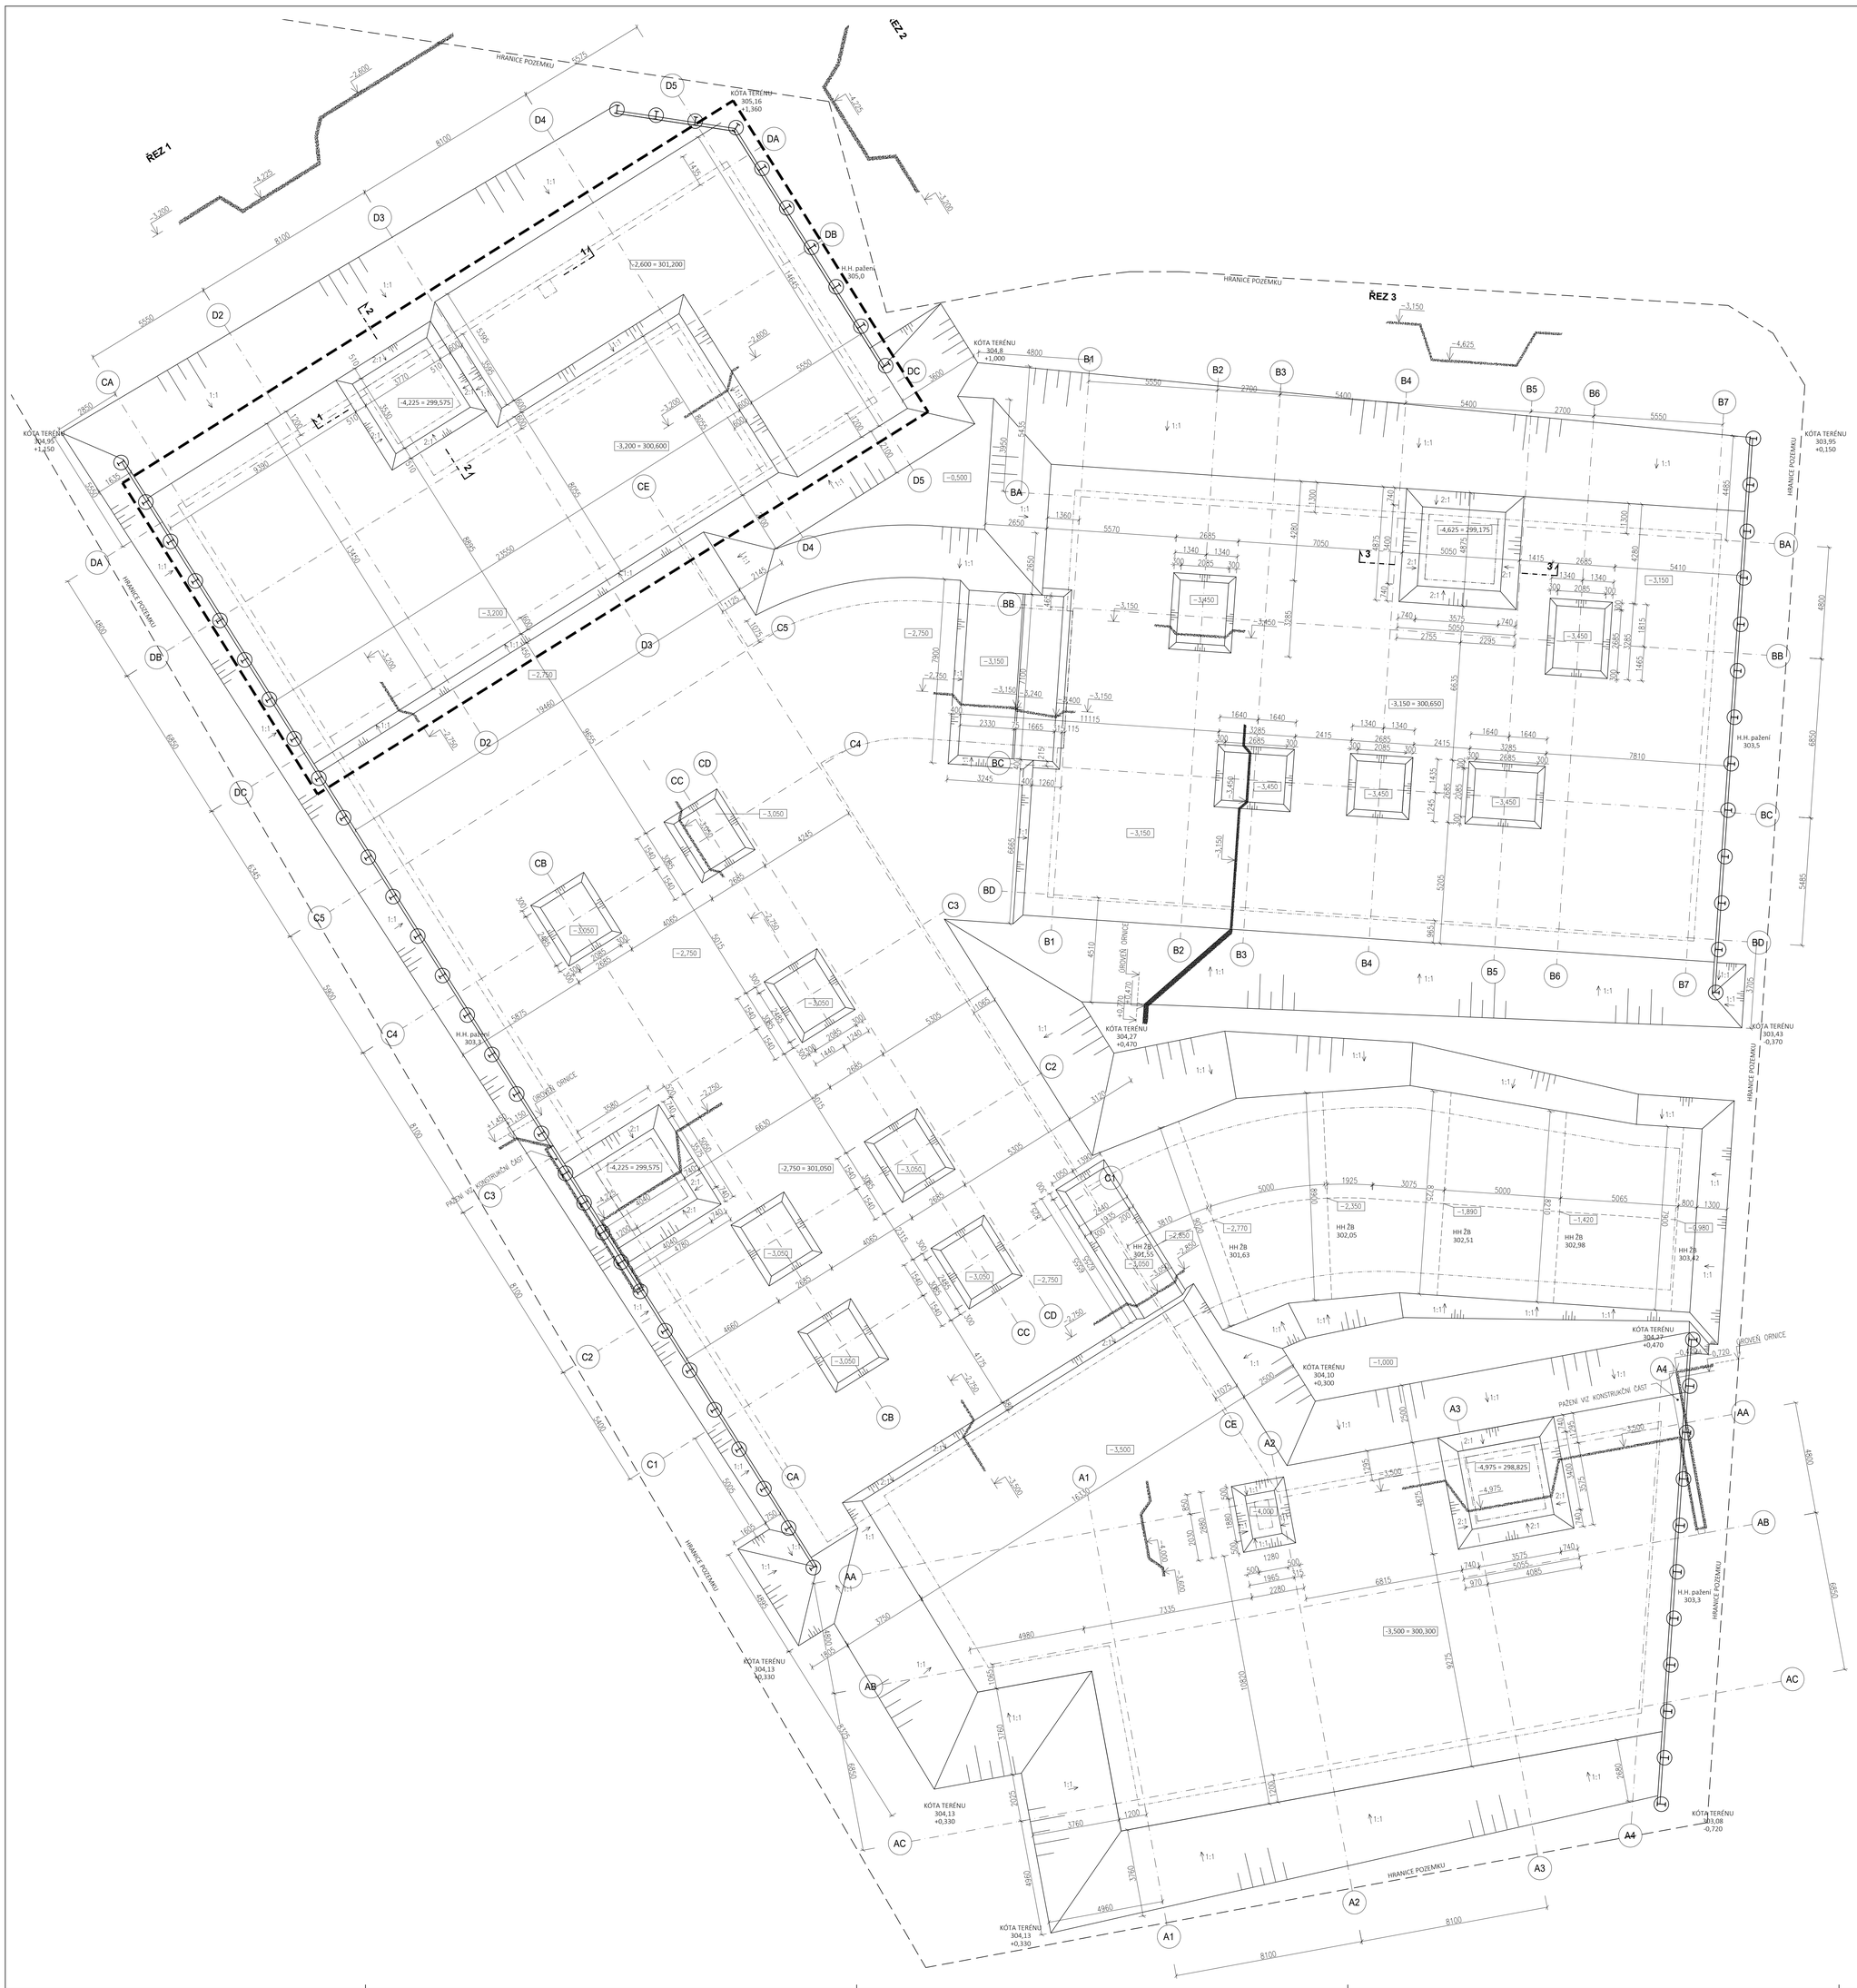

LEGENDA MATERIÁLŮ

ROSTLÝ TERÉN

OBLAST S KONTAMINOVANOU ZEMINOU ROPNÝMI LÁTKAMI

POZN.:
VŠECHNY ČÁSTI PROJEKTOVÉ DOKUMENTACE A REALIZACE JEDNOTLIVÝCH PROFESNÍCH ČÁSTÍ (ARCHITEKTONICKÁ, STAVEBNĚ KONSTRUKČNÍ, TZB A DALŠÍ) PODLÉHAJÍ KOORDINACI GENERÁLNÍHO PROJEKTANTA. V PŘÍPADĚ JAKÝCHKOLIV ROZPORŮ V PROJEKTOVÉ DOKUMENTACI NEBO V PRŮBĚHU REALIZACE JSOU ZHOTOVITELÉ/DODAVATELÉ JEDNOTLIVÝCH ČÁSTÍ POVINNI VYŽÁDAT SI STANOVISKO AUTORIZOVANÉ OSOBY A ARCHITEKTA.

UVEDENÉ ROZMĚRY A POZICE KONSTRUKCÍ, INSTALAČNÍCH ROZVODŮ, KONCOVÝCH PRVKŮ APOD. JSOU JEN ORIENTAČNÍ, ZHOTOVITEL/DODAVATEL JE POVINEN ZAMĚŘIT SKUTEČNÝ STAV NA MÍSTĚ STAVBY. V PŘÍPADĚ ZMĚNY PODKLADŮ Č. VZNIKU NOVÝCH SKUTEČNOSTÍ JE NUTNÉ INFORMOVAT GP A DÁLE POSTUPOVAT AŽ PO KOORDINACI, VYDÁNÍ A SCHválení ZMĚNY V PROJEKTOVÉ DOKUMENTACI.

DODAVATEL STAVBY MUSÍ DBÁT NA DODRŽOVÁNÍ MONTÁŽNÍCH A TECHNOLOGICKÝCH POKYNŮ Č PŘÍLUŽÁNÍCH VÝROBCŮ STAVEBNÍCH PRVKŮ A KONSTRUKCÍ UVEDENÝCH V TÉTO DOKUMENTACI.

DOKUMENTACI JE MOŽNÉ UŽÍVAT VÝHRADNĚ A BEZ VÝJIMKY VE SMYSLU SMLOUVY O DÍLO. DOKUMENTACE JE POVAŽOVÁNA ZA RELEVANTNÍ JEN JAKO CELEK PODLE PLATNÉHO SEZNAMU DOKUMENTACE.

TATO PROJEKTOVÁ DOKUMENTACE BYLA ZPRACOVÁNA NA ZÁKLADĚ INFORMACÍ, PODKLADŮ A ZNALOSTÍ PLATNÝCH KE DNI JEJÍHO VYDÁNÍ A SLOUŽÍ VÝHRADNĚ PRO POTŘEBY UVEDENÉHO STUPNĚ DOKUMENTACE (NENAHRAZUJE PŘEDCHOZÍ NEBO NÁSLEDUJÍCÍ STUPNĚ). V PŘÍPADĚ ROZPORU MEZI JEDNOTLIVÝMI PŘÍLOHAMI NEBO PROFESNÍMI DÍLY JE POTŘEBNÉ NA TENTO ROZPOR UPOZORNIT A VYŽÁDAT SI OFICIÁLNÍ STANOVISKO GENERÁLNÍHO PROJEKTANTA.

SPÁDOVÁNÍ VŠECH VÝKOPŮ JE 1:1 POKUD NENÍ NA VÝKRESE UVEDENO JINAK.
OBLAST S KOTAMINOVANOU ZEMINOU ROPNÝMI LÁTKAMI NUTNO ODTĚŽIT AŽ NA NEZASAŽENÝ TERÉN. DOPORUČENA PŘÍTOMNOST EKOLOGICKÉHO DOZORU

N

±0,000 = 303,800 m n. m.
výškový systém: Bpv
souřadný systém: JTSK

projekt / project	*číslo zakázky / project number:* 185-01
BYTOVÝ SOUBOR LIBUŠE	
stupeň dokumentace / design stage	
DOKUMENTACE PRO PROVEDENÍ STAVBY	DPS
DETAIL DESIGN DOCUMENTATION	DDD
klient / client	VELTON REAL ESTATE Na Strži 2102/63a 140 00, Praha 4 - Krč
architekt / architect	A.D.N.S. architekti s.r.o. Na Příkopě 853/12 110 00 Praha 1 - Nové Město
generální projektant / general designer	ABMV world s.r.o. Prosecká 527/24 180 00 Praha 8
projektant / designer	ABMV world s.r.o. Prosecká 527/24 180 00 Praha 8
	odpovědný projektant / designer Ing. arch. Zdeněk Vávra
	vypracoval / drawn by Ing. Martin Projek
	kontroloval / checked by Ing. Marek Veselý

revize / revision	*popis / description*	*datum / date*

část dokumentace / documentation part
D | DOKUMENTACE OBJEKTŮ A TECHNICKÝCH A TECHNOLOGICKÝCH ZAŘÍZENÍ
stavební objekt / building object
S001 | BYTOVÝ DŮM
profesní díl / specialist part
100 | ARCHITEKTONICKO-STAVEBNÍ ŘEŠENÍ

název výkresu / drawing title
PŮDORYS VÝKOPŮ

datum revize 00 / revision date 00	*měřítko / scale*	*počet A4 / A4 count*	*paré*
15.09.2021	1:100	9 x A4	

číslo výkresu / sheet number 4010
kód výkresu / sheet code 185D1_DPS_D_S001_100_4010_R00