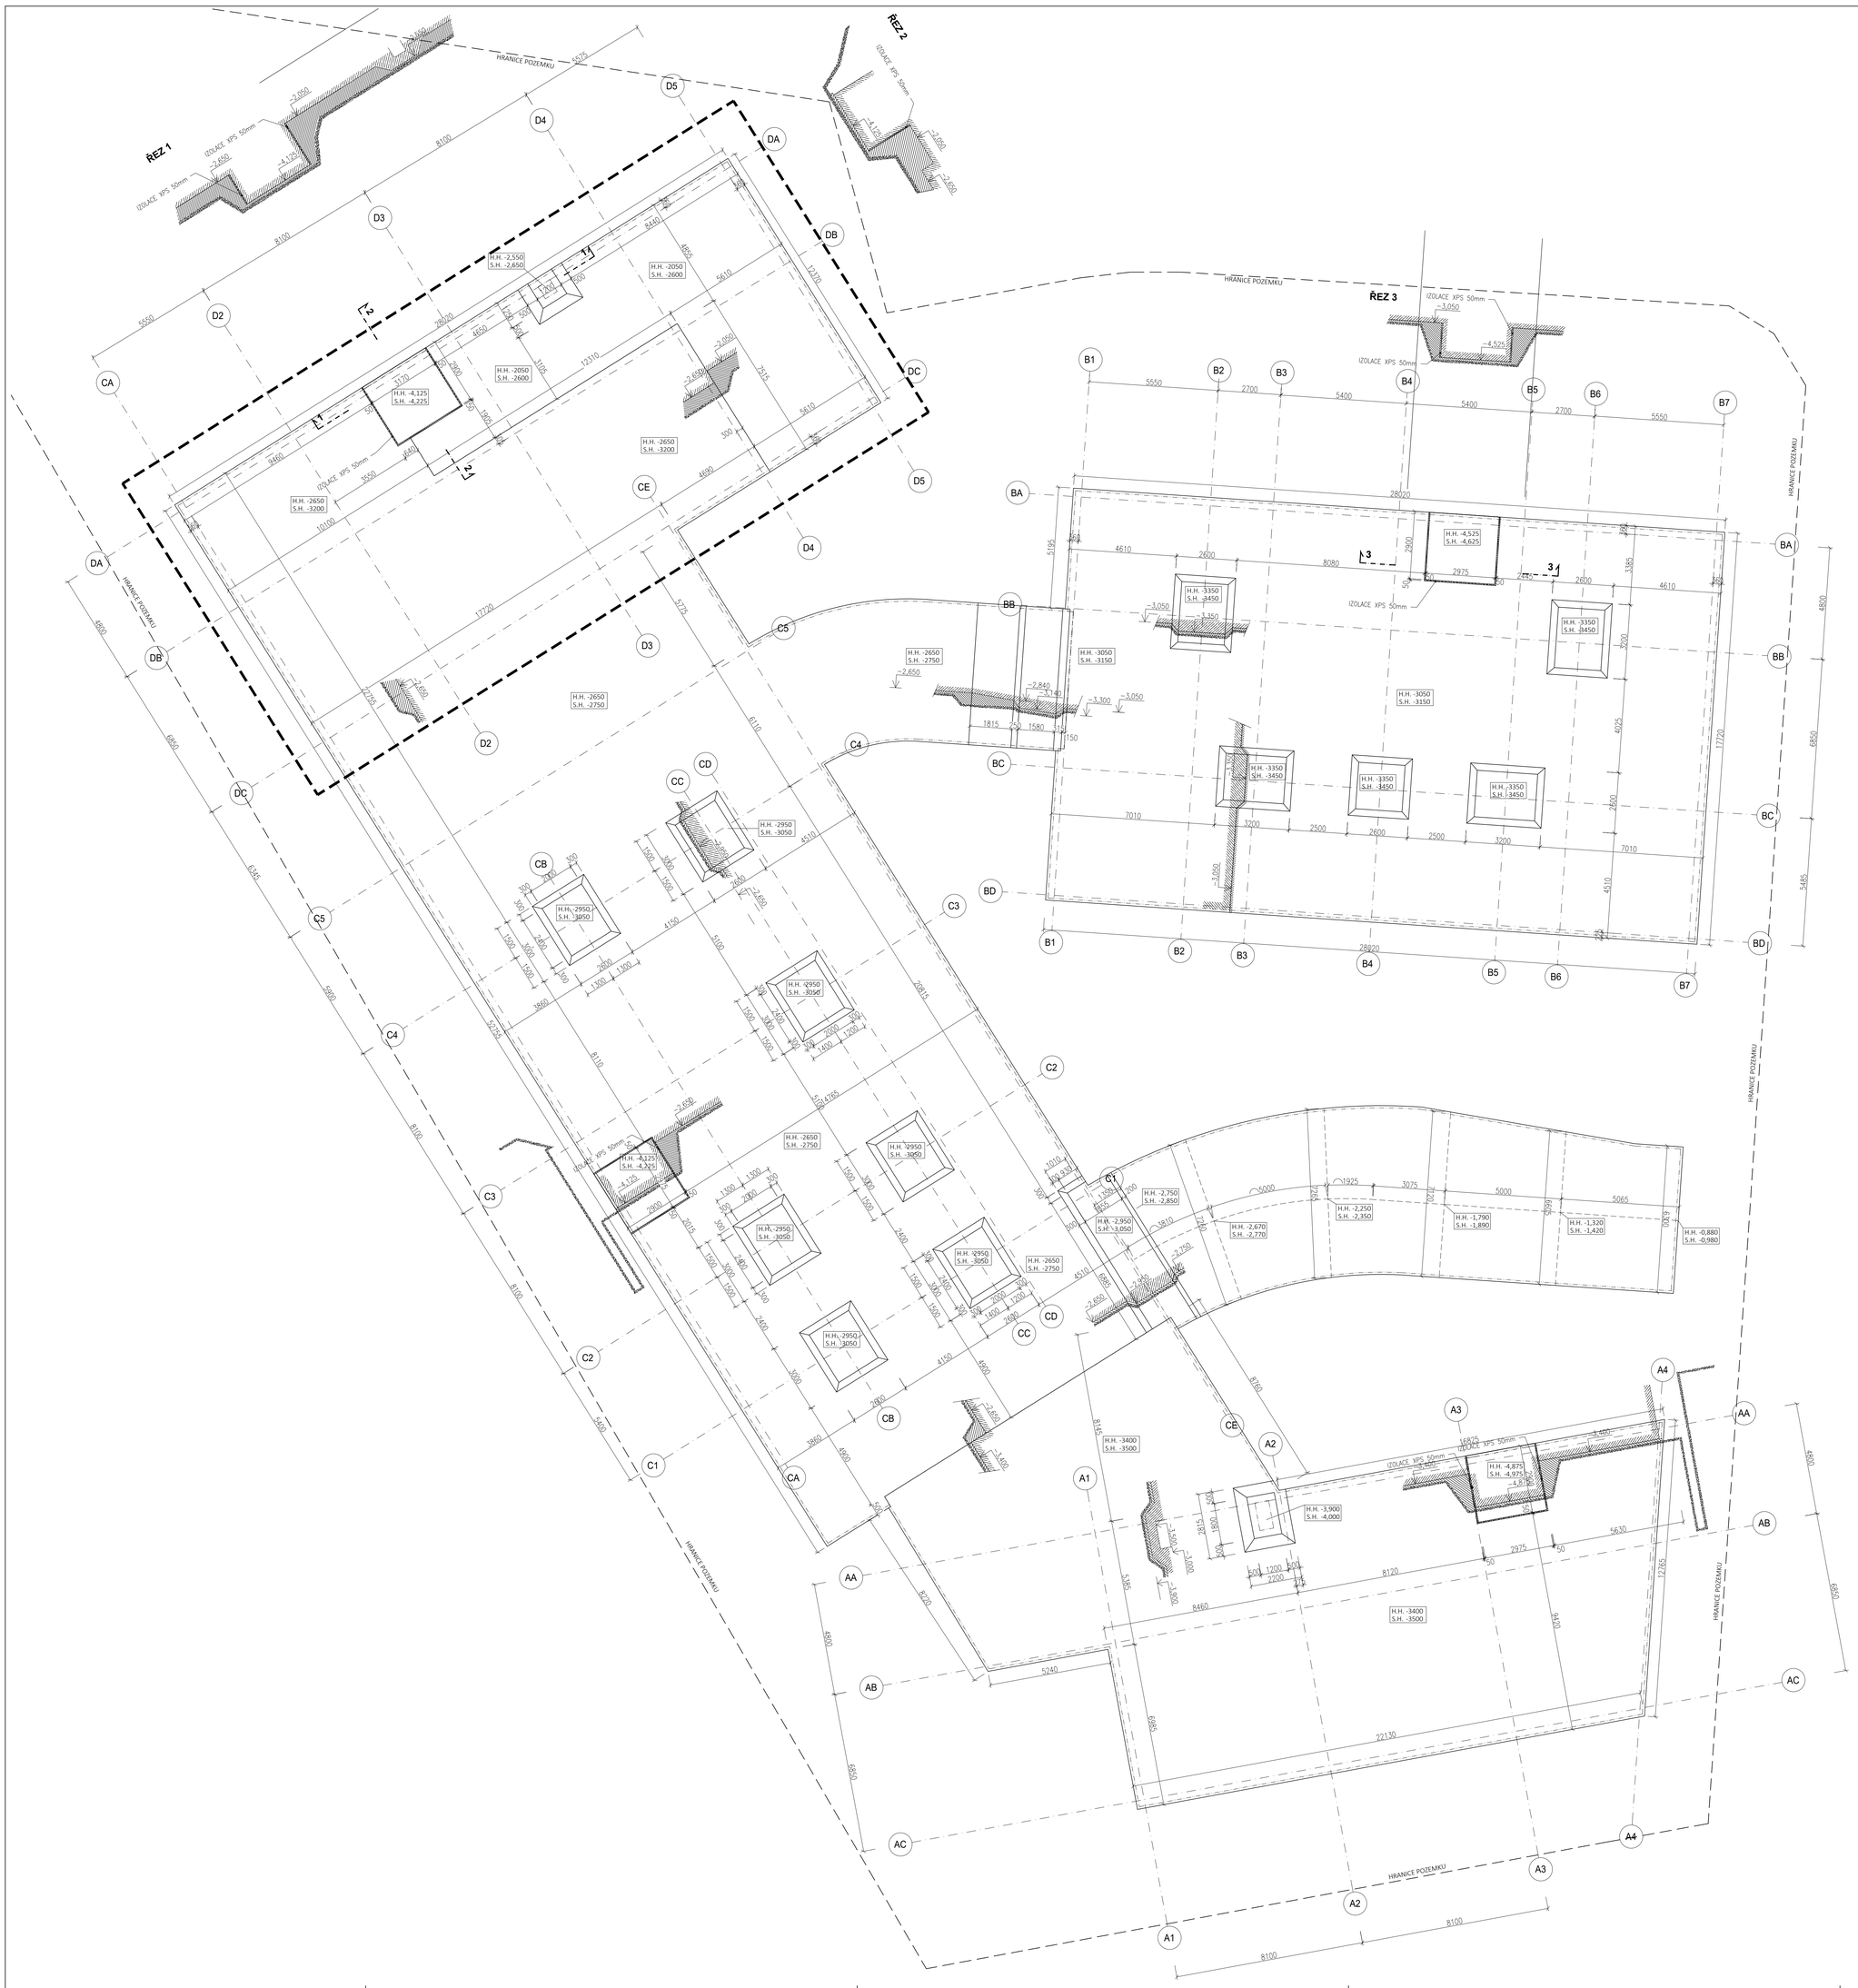


## LEGENDA MATERIÁLŮ

- ŽELEZOBETON
- PODKLADNÍ BETON C12/15
- EXTRUDOVANÝ POLYSTYRÉN TL.50 MM
- ROSTLÝ TERÉN
- OBLAST S KONTAMINOVANOU ZEMINOU ROPNÝMI LÁTKAMI

POZN.:
VŠECHNY ČÁSTI PROJEKTOVÉ DOKUMENTACE A REALIZACE JEDNOTLIVÝCH PROFESNÍCH ČÁSTÍ (ARCHITEKTONICKÁ, STAVEBNĚ KONSTRUKČNÍ, TZB A DALŠÍ) PODLÉHAJÍ KOORDINACI GENERÁLNÍHO PROJEKTANTA. V PŘÍPADĚ JAKÝCHKOLIV ROZPORŮ V PROJEKTOVÉ DOKUMENTACI NEBO V PRŮBĚHU REALIZACE JSOU ZHOTOVITELÉ/DODAVATELÉ JEDNOTLIVÝCH ČÁSTÍ POVINNI VYŽÁDAT SI STANOVISKO AUTORIZOVANÉ OSOBY A ARCHITEKTA.

UVEDENÉ ROZMĚRY A POZICE KONSTRUKCÍ, INSTALAČNÍCH ROZVODŮ, KONCOVÝCH PRVKŮ APOD. JSOU JEN ORIENTAČNÍ, ZHOTOVITEL/DODAVATEL JE POVINEN ZAMĚŘIT SKUTEČNÝ STAV NA MÍSTĚ STAVBY. V PŘÍPADĚ ZMĚNY PODKLADŮ Č. VZNIKLI NOVÝCH SKUTEČNOSTÍ JE NUTNÉ INFORMOVAT GP A DÁLE POSTUPOVAT AŽ PO KOORDINACI, VYDÁNÍ A SCHválení ZMĚNY V PROJEKTOVÉ DOKUMENTACI.

DODAVATEL STAVBY MUSÍ DBÁT NA DODRŽOVÁNÍ MONTÁŽNÍCH A TECHNOLOGICKÝCH POKYNŮ Č. PŘÍLOŽENÝCH VÝROBCŮ STAVEBNÍCH PRVKŮ A KONSTRUKCÍ UVEDENÝCH V TÉTO DOKUMENTACI.

DOKUMENTACI JE MOŽNÉ UŽÍVAT VÝHRADNĚ A BEZ VÝJIMKY VE SMYSLU SMLOUVY O DÍLO. DOKUMENTACE JE POVAŽOVÁNA ZA RELEVANTNÍ JEN JAKO CELEK PODLE PLATNÉHO SEZNAMU DOKUMENTACE.

TATO PROJEKTOVÁ DOKUMENTACE BYLA ZPRACOVÁNA NA ZÁKLADĚ INFORMACÍ, PODKLADŮ A ZNALOSTÍ PLATNÝCH KE DNI JEJÍHO VYDÁNÍ A SLOUŽÍ VÝHRADNĚ PRO POTŘEBY UVEDENÉHO STUPNĚ DOKUMENTACE (NENAHRAZUJE PŘEDCHOZÍ NEBO NÁSLEDUJÍCÍ STUPNĚ). V PŘÍPADĚ ROZPORU MEZI JEDNOTLIVÝMI PŘÍLOHAMI NEBO PROFESNÍMI DÍLY JE POTŘEBNÉ NA TENTO ROZPOR UPOZORNIT A VYŽÁDAT SI OFICIÁLNÍ STANOVISKO GENERÁLNÍHO PROJEKTANTA.

DO PODKLADNÍCH BETONŮ BUDE VLOŽENO UZEMNĚNÍ, VIZ. 18501_DPS_D_S001_010_4010

| | |
|---|---|
| *projekt / project* | *číslo zakázky / project number:* 18S-01 |
| BYTOVÝ SOUBOR LIBUŠE | |
| *stupeň dokumentace / design stage* | |
| DOKUMENTACE PRO PROVEDENÍ STAVBY<br>DETAIL DESIGN DOCUMENTATION | DPS<br>DDD |
| *klient / client* | VELTON REAL ESTATE<br>Na Strži 2102/63a<br>140 00, Praha 4 - Krč |
| *architekt / architect* | A.D.N.S. architekti s.r.o.<br>Na Příkopě 853/12<br>110 00 Praha 1 - Nové Město |
| *generální projektant / general designer* | ABMV world s.r.o.<br>Prosecká 527/24<br>180 00 Praha 8 |
| *projektant / designer* | ABMV world s.r.o.<br>Prosecká 527/24<br>180 00 Praha 8 |
| | *odpovědný projektant / designer*<br>Ing. arch. Zdeněk Vávra |
| | *vypracoval / drawn by*<br>Ing. Martin Proječ |
| | *kontroloval / checked by*<br>Ing. Marek Veselý |

| *revize / revision* | *popis / description* | *datum / date* |
|---|---|---|
| | | |

*část dokumentace / documentation part*
D | DOKUMENTACE OBJEKTŮ A TECHNICKÝCH A TECHNOLOGICKÝCH ZAŘÍZENÍ
*stavební objekt / building object*
S001 | BYTOVÝ DŮM
*profesní díl / specialist part*
100 | ARCHITEKTONICKO-STAVEBNÍ ŘEŠENÍ

*název výkresu / drawing title*
PODKLADNÍ BETONY

| *datum revize 00 / revision date 00* | *měřítko / scale* | *počet A4 / A4 count* | *paré* |
|---|---|---|---|
| 15.09.2021 | 1:100 | 9 x A4 | |

*číslo výkresu / sheet number* 4020
*kód výkresu / sheet code* 18501_DPS_D_S001_100_4020_R00

±0,000 = 303,800 m n. m.
výškový systém: Bpv
souřadný systém: JTSK