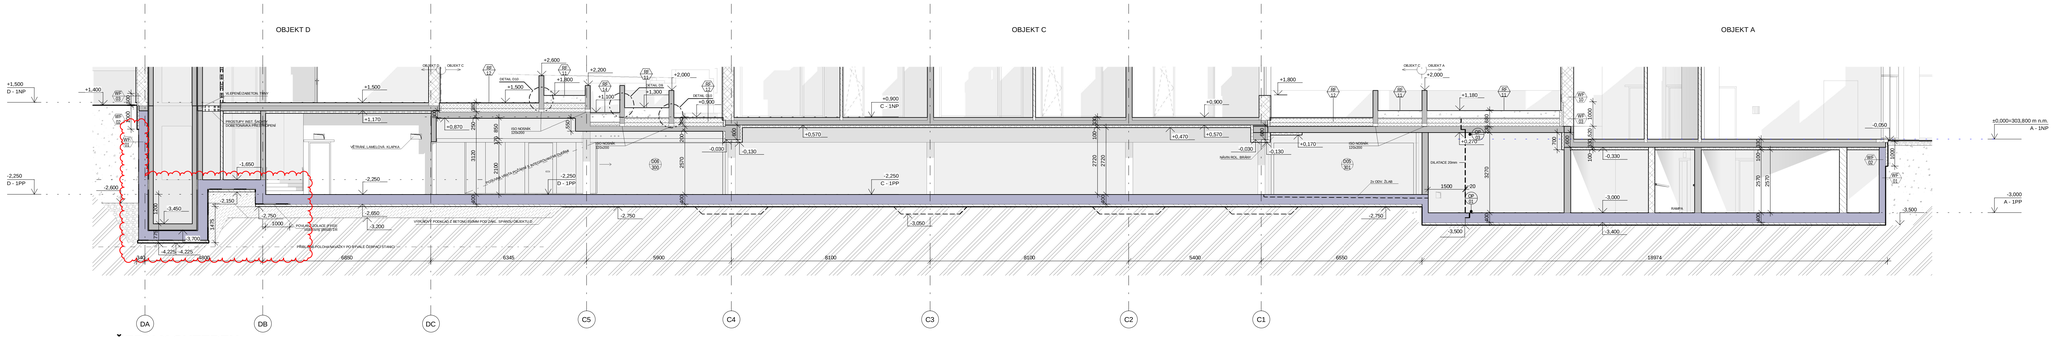

ŘEZ X-X SUTEREN

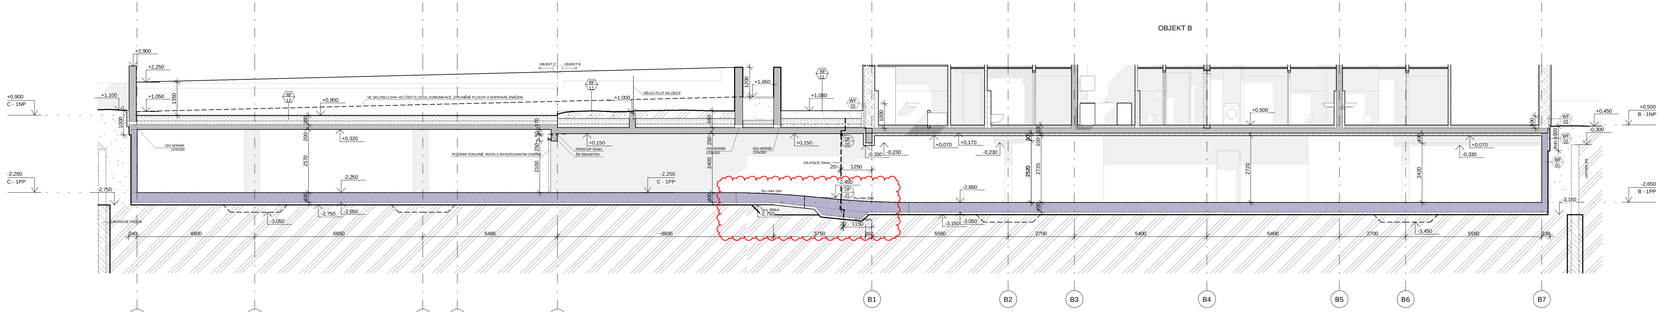

ŘEZ Y-Y SUTEREN

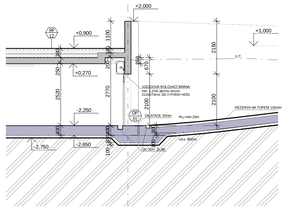

ŘEZ Z-Z SUTEREN

LEGENDA MATERIÁLŮ

- ŽELEZOBETON
- VODOSTAVEBNÍ BETON
- PROSTÝ BETON
- NOSNÉ ZDIVO - KERAMICKÁ TVÁRNICE
- PŘÍČKY - KERAMICKÁ TVÁRNICE
- SÁDROKARTON
- TEPELNÁ IZOLACE - MINERÁLNÍ VATA
- TEPELNÁ IZOLACE - EXTRUDOVANÝ POLYSTYREN
- LEPENÝ OBKLAD - CIH, PÁSKY / STŘEŠNÍ KRYTINA
- ROSTLÝ TERÉN
- NÁSYP
- HUTNĚNÉ KAMENIVO

LEGENDA TAGŮ

- XF 01 — Označení specifikace skladby a povrchu; značení CF, WF, RF, Viz D_01_0100_030 - Tabulka specifikace skladeb a povrchů
- DO1 001 — Označení dveří Viz D_01_100_041 - Tabulka dveří
- LP 01 — Označení zámečnických prvků Viz D_01_100_050 - Tabulka zámečnických prvků
- TP 01 — Označení klempířských prvků Viz D_01_100_060 - Tabulka klempířských prvků
- OP 001 — Označení ostatních prvků Viz D_01_100_080 - Tabulka ostatních prvků
- W 01 015 — Označení oken Viz D_01_100_040 - Tabulka výplně otvorů
- F 01 — Označení povrchů Viz D_01_0100_030 - Tabulka specifikace skladeb a povrchů

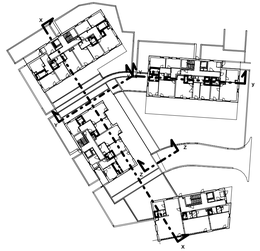

PŘÍPADNÉ ZMĚNY VŮČI ČÁSTI D_01_02 KONKURENCE - ZPŘÍZENÍ PLOCHY A DOPRAVNÍ ZNAČENÍ

PŘÍPADNÉ PODLAHÁ VRAVA S INTEGROVANÝM OHŘEVEM

VÝKOPOVÉ PODKLADÍ Z BETONU DOBAN POD ZÁKL. SPARÁDU DEKORITU C

PŘÍPADNÉ DVOUKŘÍDLÝ PO PŘÍPADĚ ZDOBNÝ STYRNO

ISO NOSNÉ ZDIVO

DILATACE 20mm

PŘEJEZDNÁ NK TOPNÉ DRÁHY

PODLAHA - ŽULAB

PODLAHA - DEKORITU

PODLAHA - ŽULAB

PODLAHA - DEKORITU

PODLAHA - ŽULAB

PODLAHA - DEKORITU