PŮDORYS 1PP - KOORDINAČNÍ VÝKRES - ČÁST A
1:50

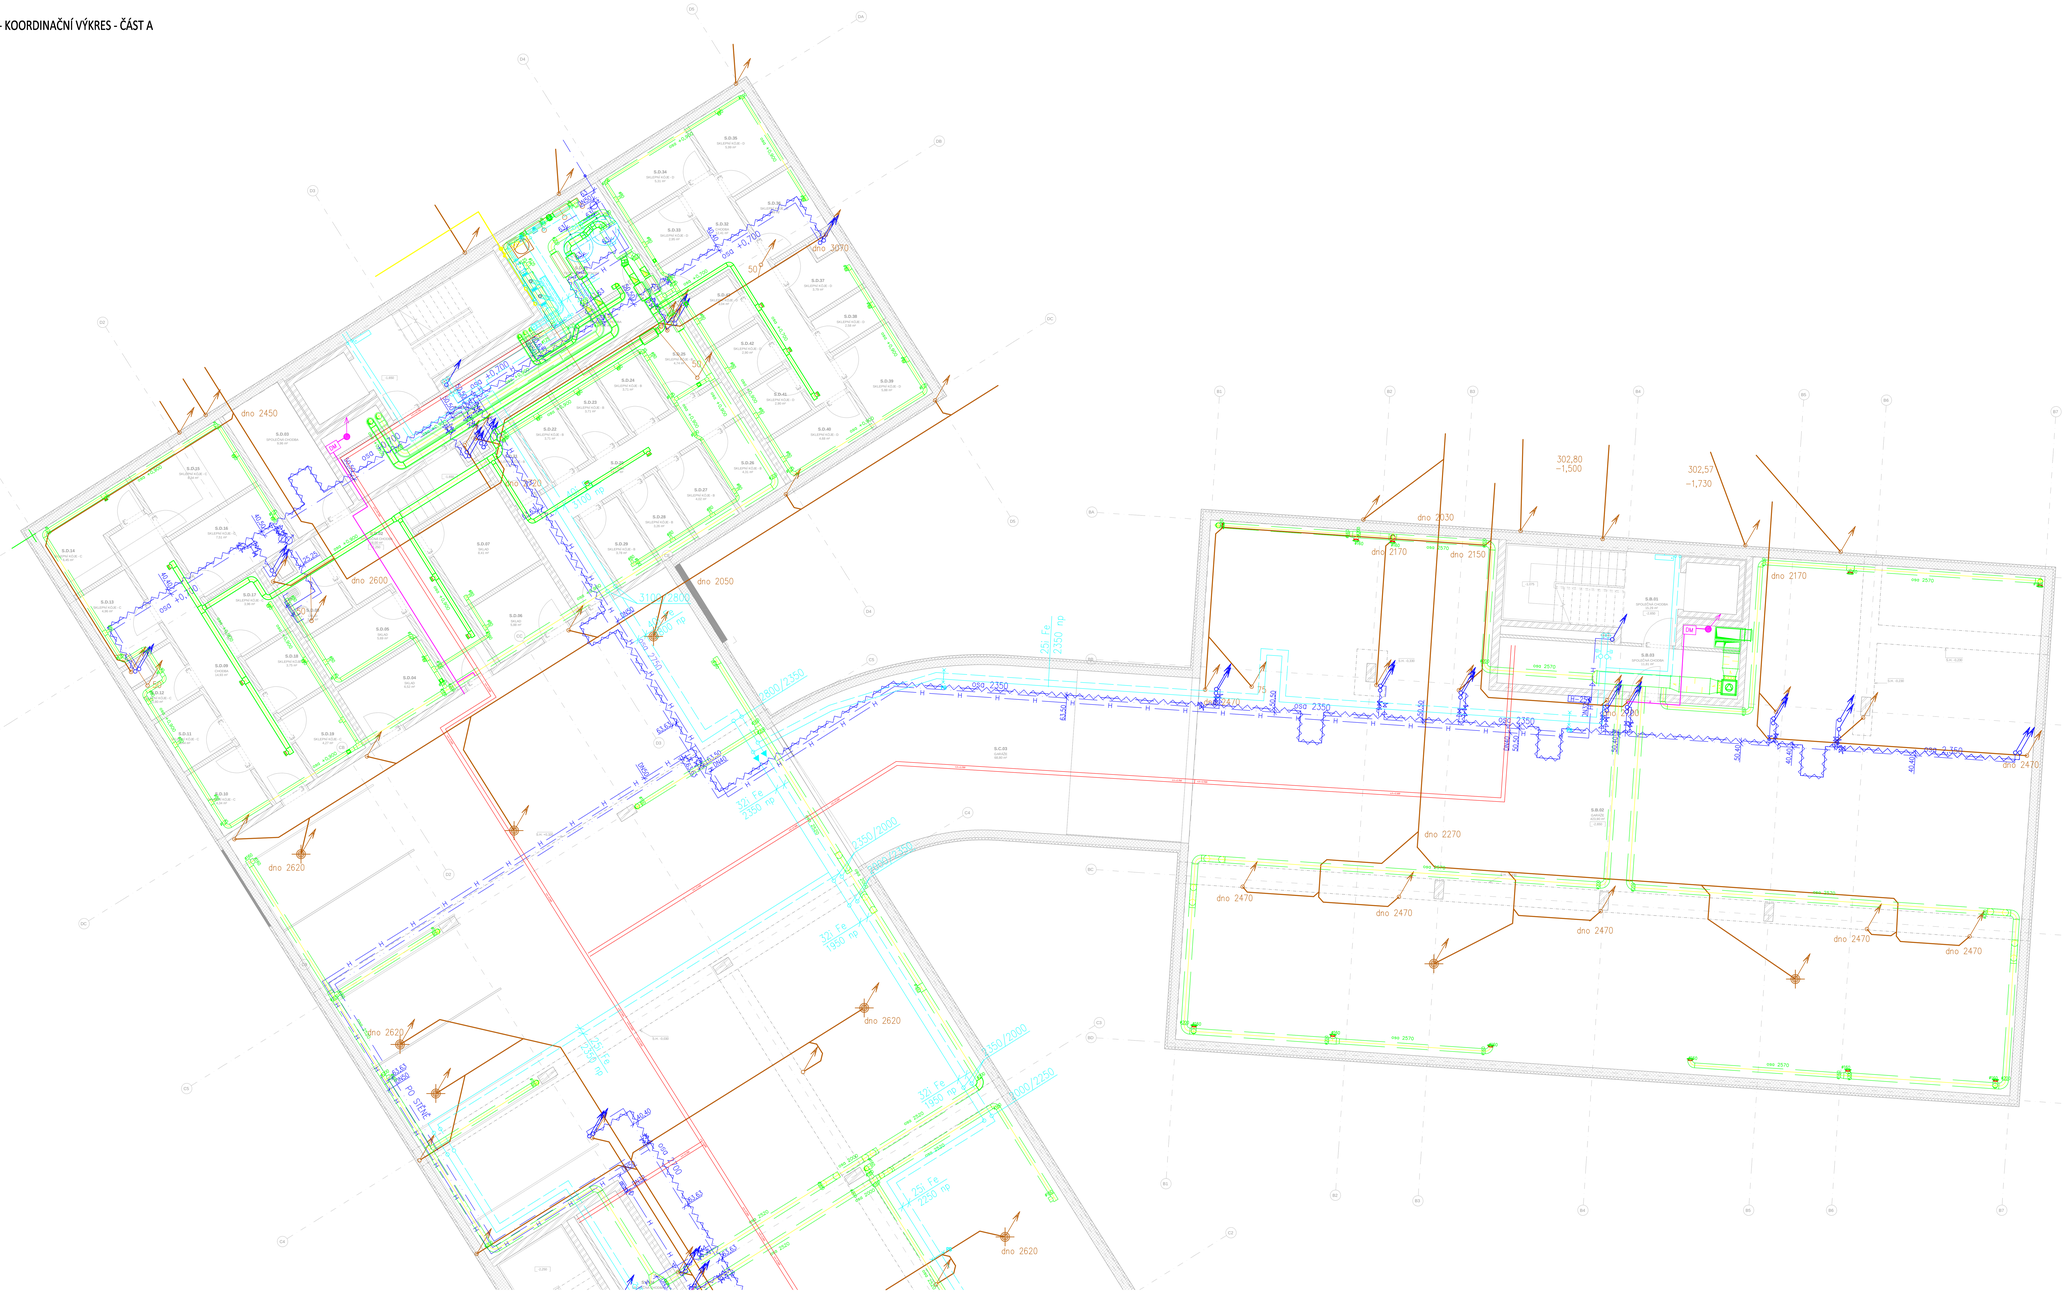
dno 2450
dno 2600
dno 2620
dno 2050
dno 3070
dno 2030
dno 2170
dno 2150
dno 2270
dno 2470
dno 2570
dno 2350
dno 2800/2350
dno 2800/2350
dno 2350/2000
dno 2000/2250
dno 2000/2250
dno 2250
dno 2250
dno