


PŮDORYS V ÚROVNI PODCHODU (ŘEZ 2-2)
1:100

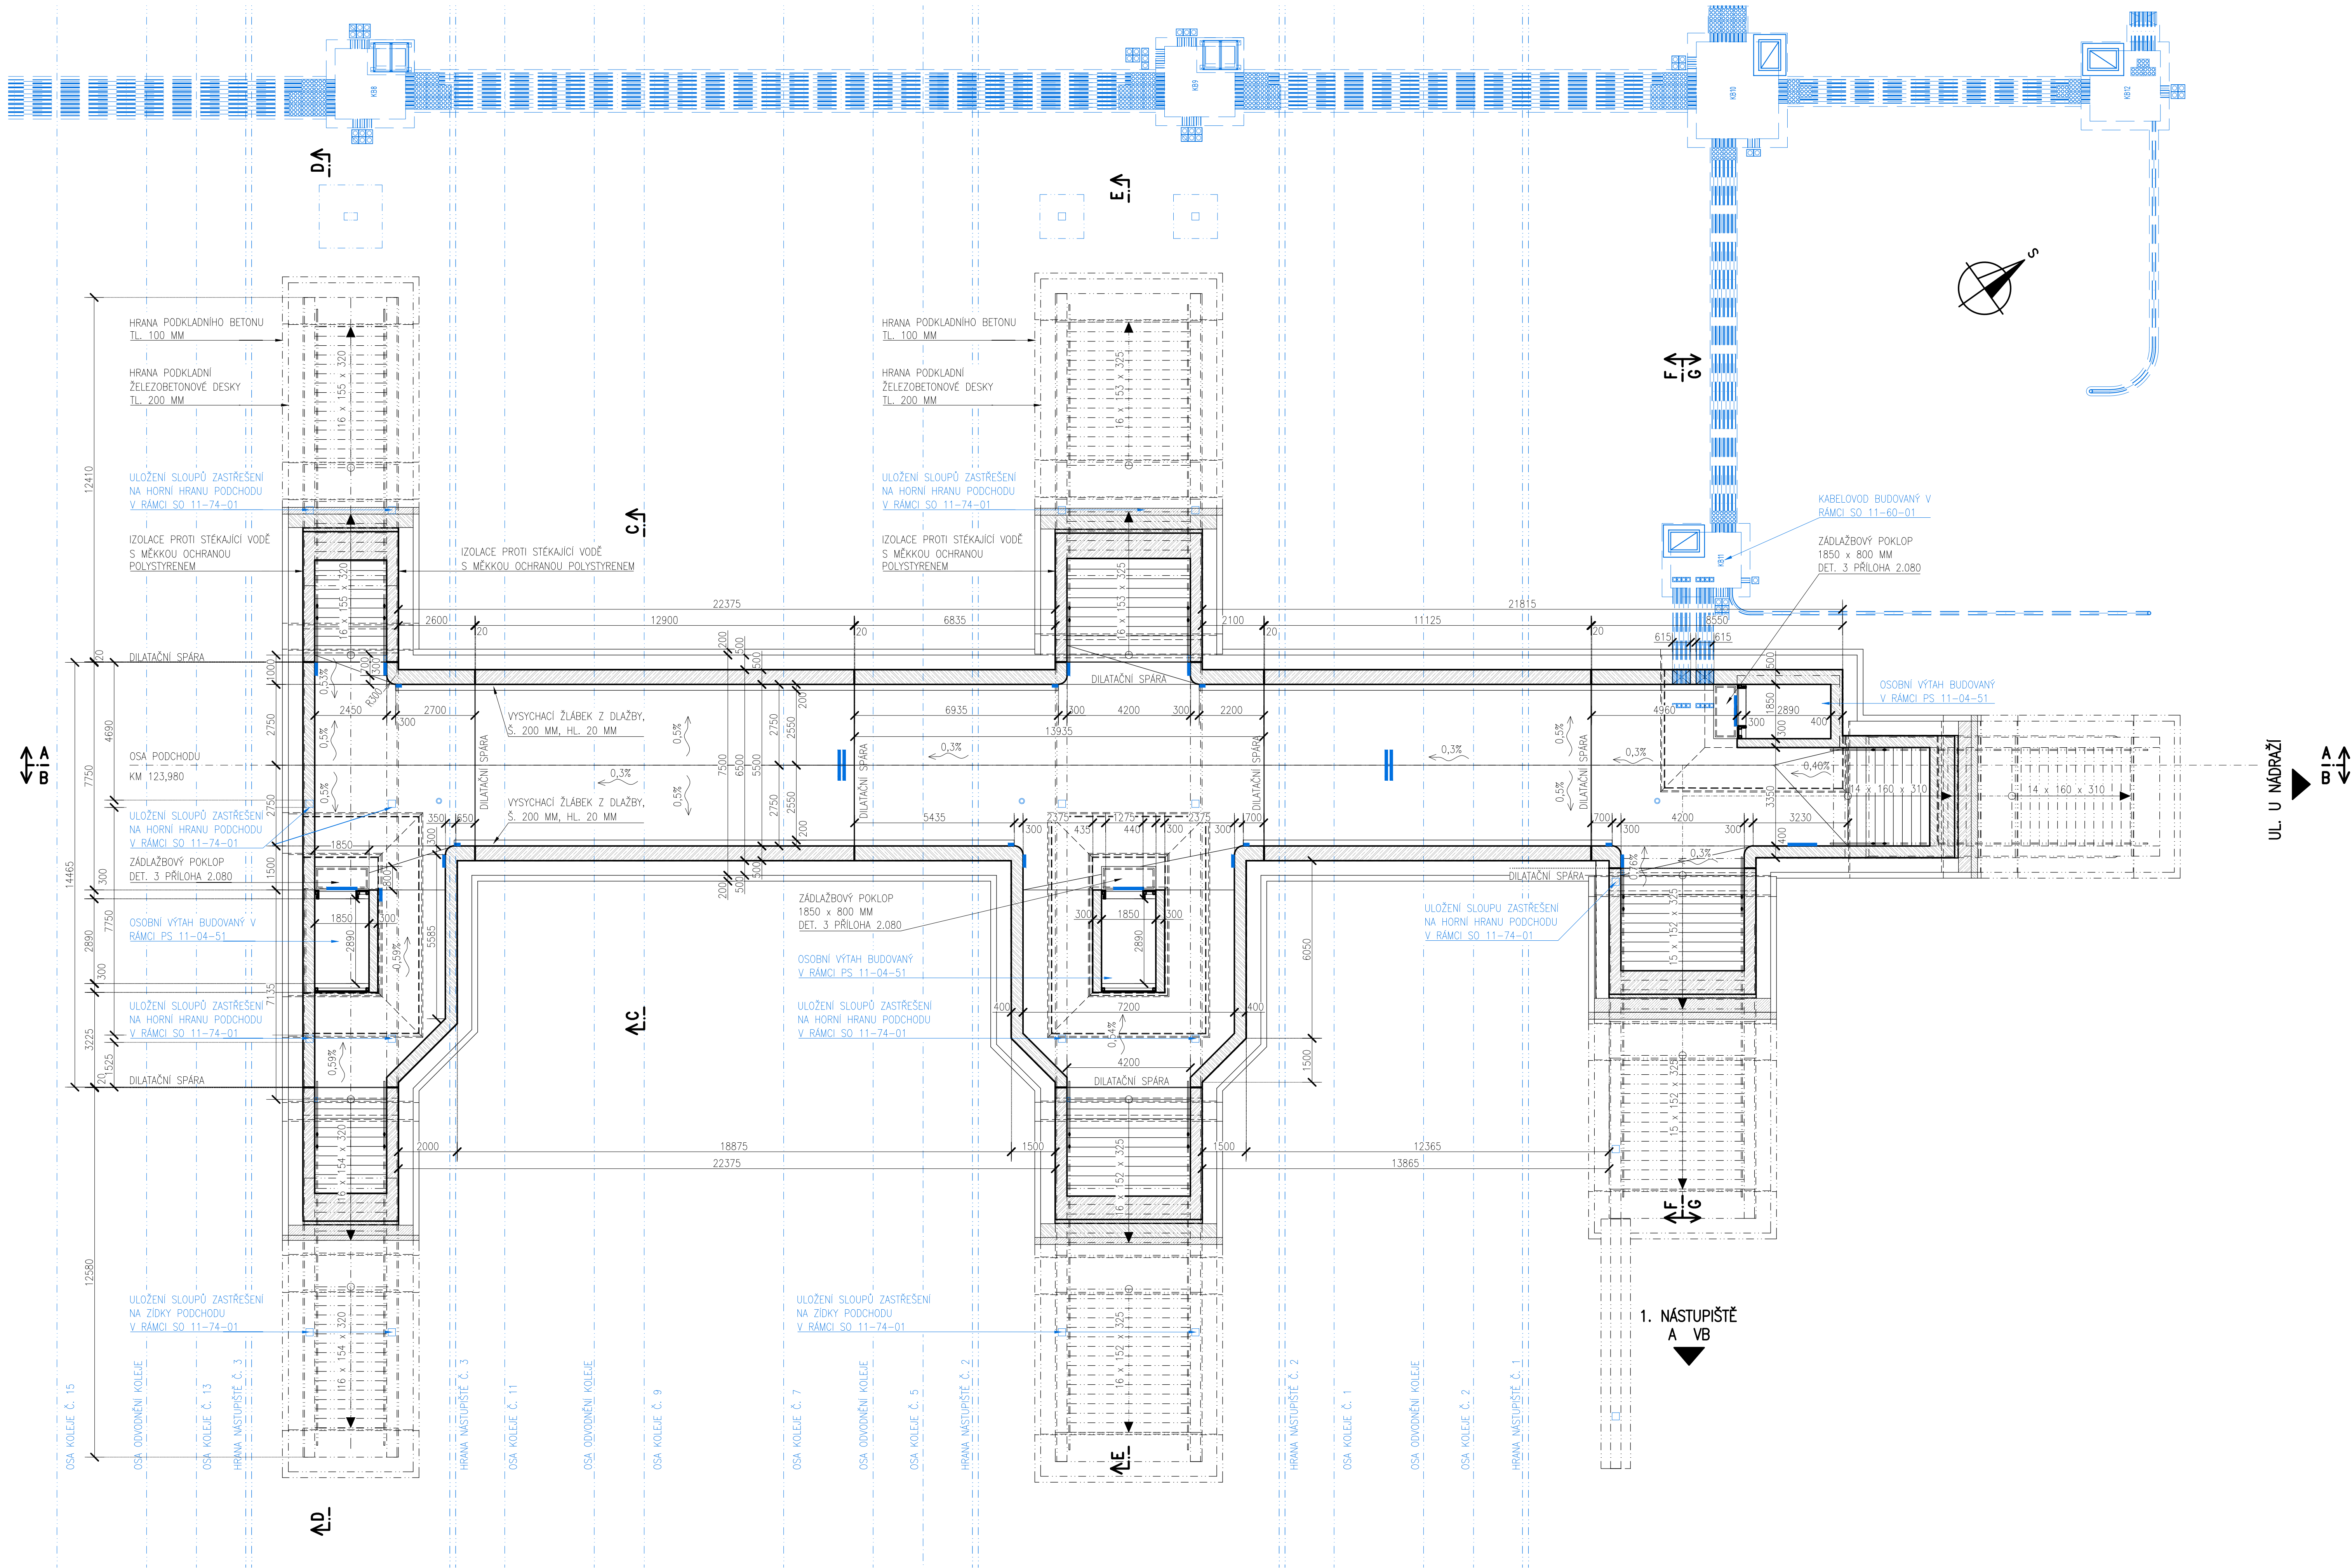

MATERIÁL:		
BETON:		C30/37 XC4, XD1, XF2, XA1
PODCHOD		CL 0,4, D _{MAX} 22MM, S3, MAX. PRŮSAK 35MM
PODKLADNÍ DESKA		C25/30 XC2, XF1
PODKLADNÍ BETON		CL 0,4, D _{MAX} 16 MM
SPÁDOVÝ BETON		C16/20 X0
VIROVNÁVACÍ MAZANINA		C20/25 XF2
PŘEBETONOVÁNÍ ZPĚTNÉHO SPOJE		C20/25 XF2
OCEL:		
VÝZTUŽ		B500B

- ZNAČKY SOUVISEJÍCÍCH OBJEKTŮ:
- ORIENTAČNÍ SYSTÉM V PODCHODU SO 11-77-01
 - KAMEROVÝ SYSTÉM V PODCHODU PS 11-02-42

POZNÁMKY:

v PŮDORYSE POD ÚROVNÍ NÁSTUPÍŠTĚ NEJSOU ZOBRAZENY NIKY PRO MONITORY, KABELOVÉ SKŘÍNĚ APOD.

TYTO JSOU ZOBRAZENY POUZE NA VÝKRESECH TVARU S OHLEDEM NA PŘEHLEDNOST DOKUMENTACE.

Ministerstvo dopravy Státní fond dopravní infrastruktury		Paré:	
Jiné ověření:		Razítko oprávněné osoby:	
Orientační schéma:		Podpis: Datum:	
Revize:	Datum:	Popis:	Kontroloval:
-	-	-	-
-	-	-	-
-	-	-	-
-	-	-	-
PO2	28.02.2025	Dokumentace pro vydání stavebního povolení k příloham	Ing. Anna Popoví
Stavebník/Investor:		SPRÁVA ŽELEZNIC	
Adresa:		Dlážděná 1003/7, 110 00 Praha 1	
Zástupce investora:		Stavební správa západ	
Adresa:		Ke Štvanici 656/3, 186 00 Praha 8 - Karlín	
Zhotovitel díla:		Ps + SB + A4 - ŽST Turnov DSP, PDPS	
Adresa:		U Elektrý 830/2b, 198 00 Praha 9	
Kontakt:		T: +420 281 090 860 E: firma@projekt-servis.cz	
Zhotovitel objektu:		PROJEKT servis spol. s r.o.	
Adresa:		U Elektrý 830/2b, 198 00 Praha 9	
Kontakt:		T: +420 281 090 860 E: firma@projekt-servis.cz	
Hlavní projektant (HIP):		Ing. Martin Koudelka	
Specialista:		Ing. Radomír Hanák	
Název stavby/akce:		Rekonstrukce žst. Turnov	
Označení investora:		S631700077	
Název části:		Mosty, propustky a zdi	
Označení části:		D.2.1.4	
Název objektu/dílo části:		Železniční most v km 123,980 (Podchod)	
Označení objektu/komplektu:		SO 11-20-04	
Název přílohy:		Půdorys v úrovni podchodu (řez 2-2)	
Označení přílohy (typ/pojedl):		2. 022	
Název dílčí části přílohy:		-	
Odpovědný projektant:		Ing. Aleš Menšík	
Zpracovatel přílohy:		Ing. Marie Peterková	
Měřítko:		1:100	
Katastrální území:		TUDU:	
Kraj:		Liberecký	
viz textová část		viz textová část	
Smluvní datum zpracování:		28.02.2025	
Stupeň dokumentace:		DSP	
Revize:		-	