



PODÉLNÝ ŘEZ V OSE LEVÉHO MOSTU 1:250

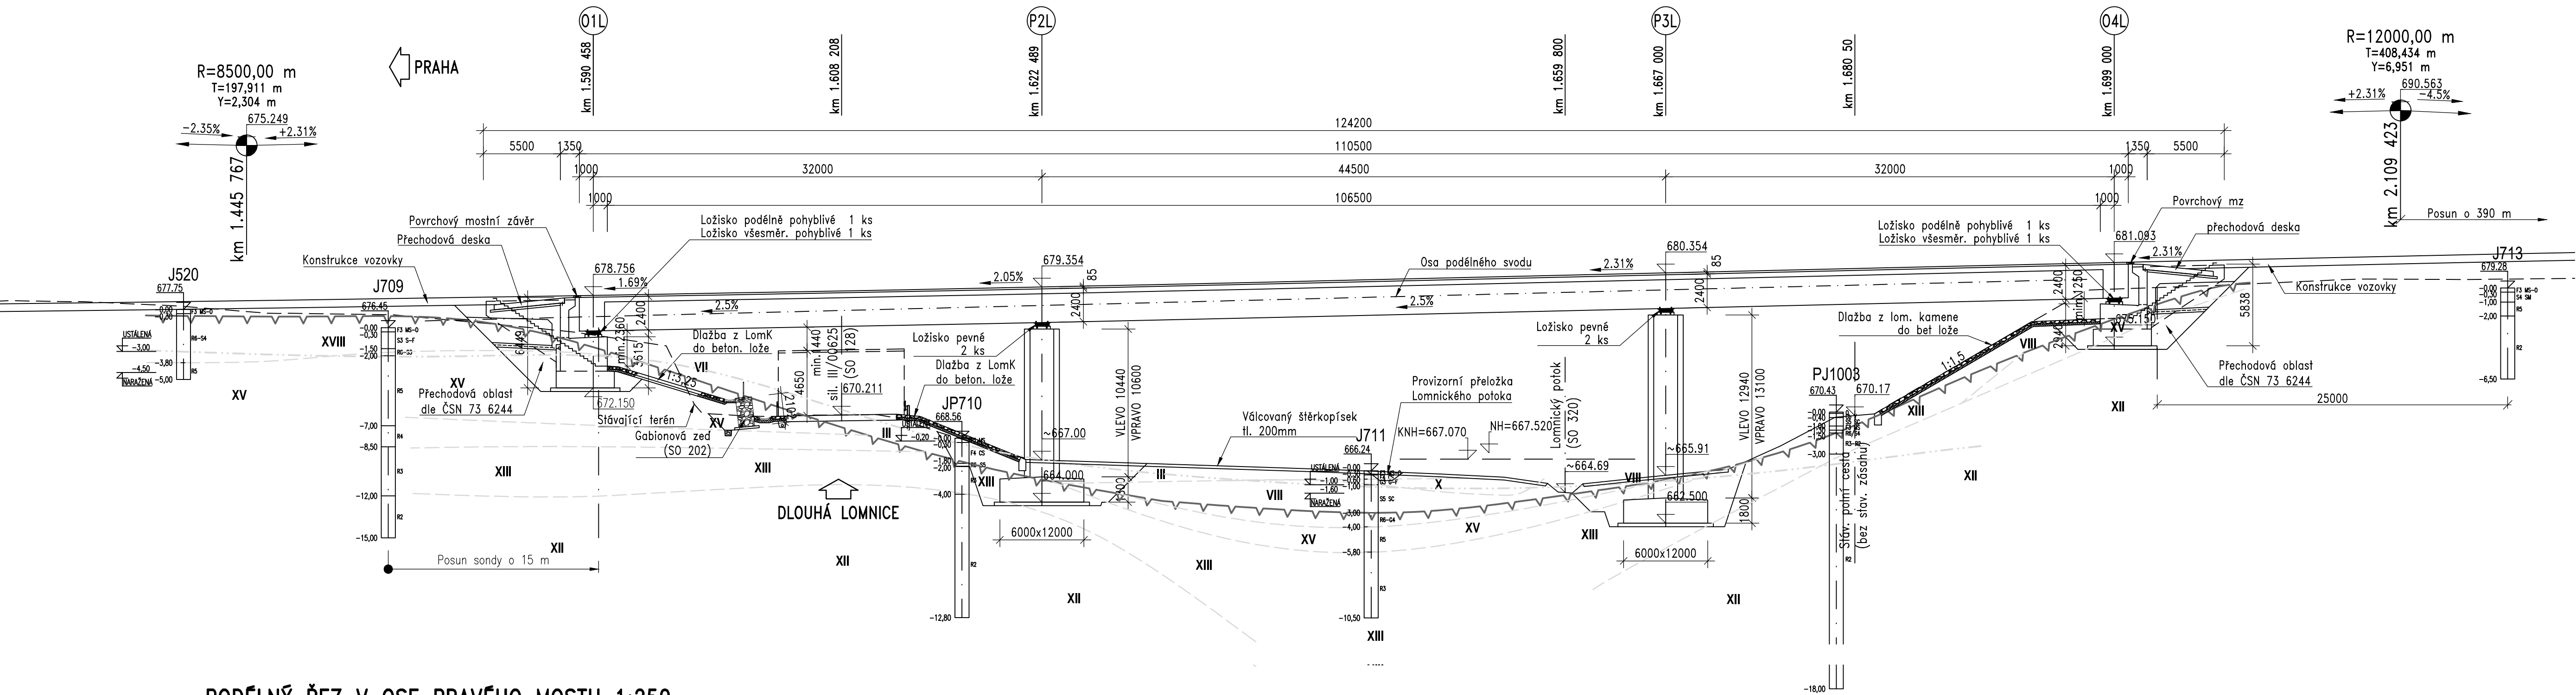

PODÉLNÝ ŘEZ V OSE PRAVÉHO MOSTU 1:250

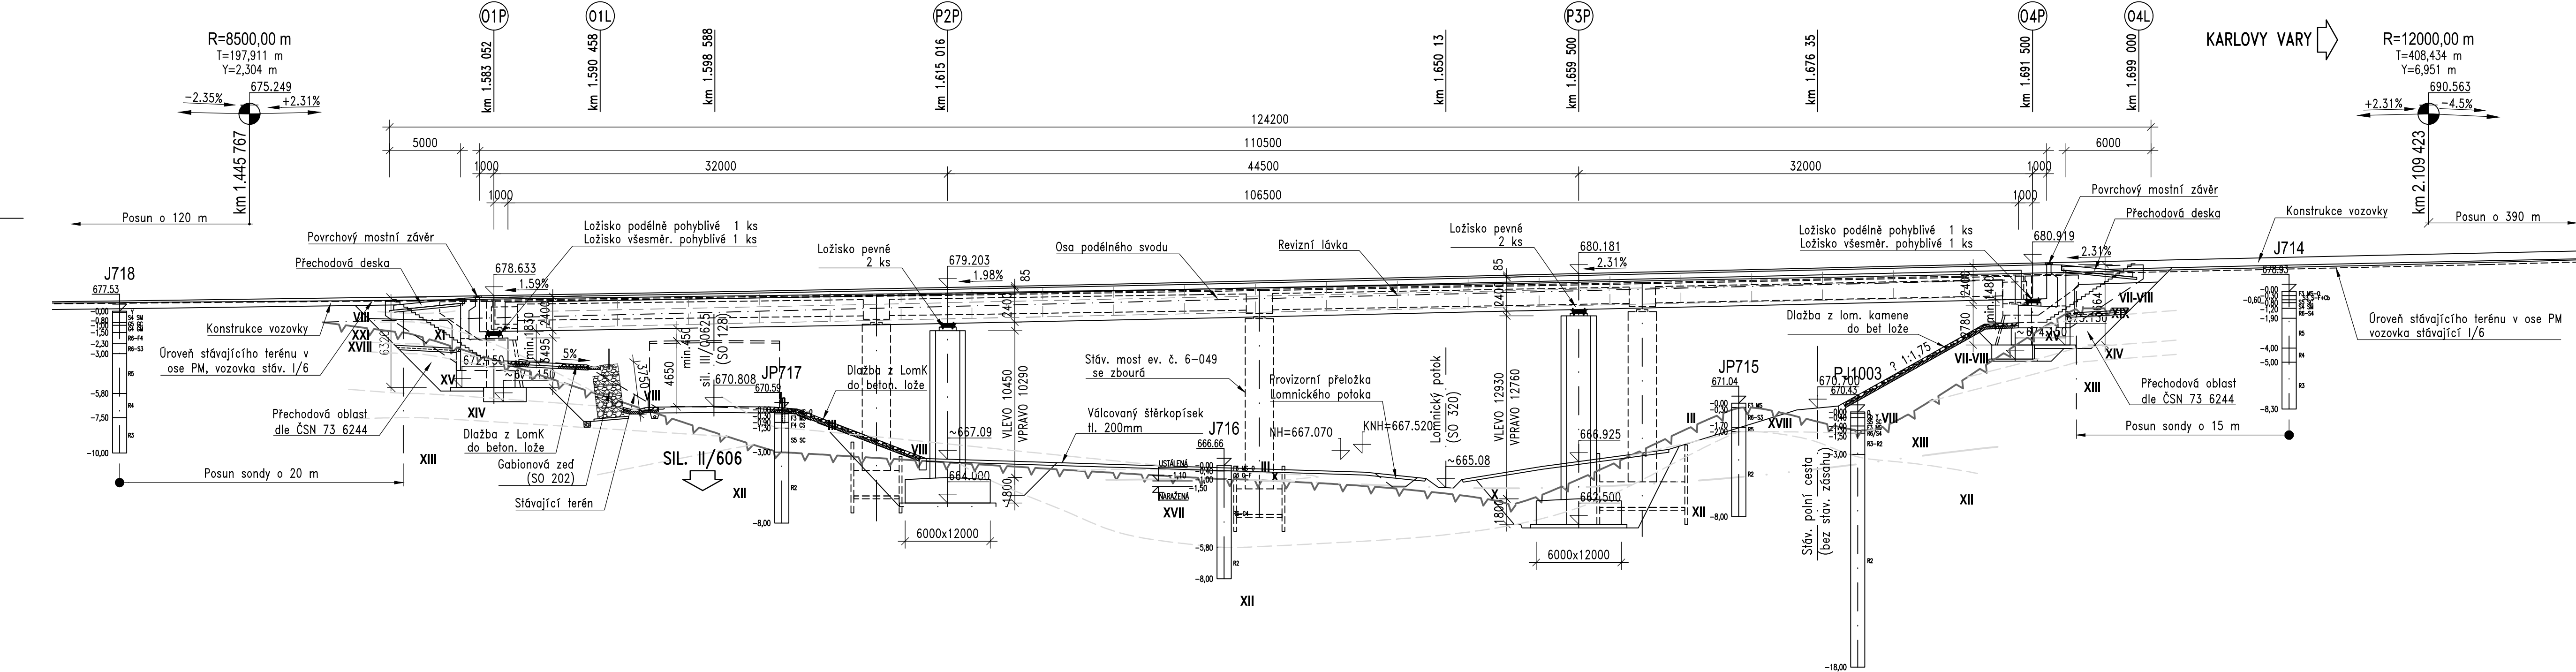

GEOTYPY:

G typ	Charakteristika vrstvy	Mocnost
Kvadrant		
III	Jíl písloj (F4 CS) tuhé konsistence	až 1,8 m
VII	Písek s příměsí jemnozrné zeminy (S3 B-F), středně ulehý	1,2 m
VIII	Písek hrubý (S4 SM) až písek jilovitý (S5 SC), středně zrnitý s příměsí drobného štěrku	1,7 m
X	Štěr s příměsí jemnozrné zeminy (G3 G-F), středně ulehý	0,8 m
Kvadrant		
XII	Granit navětralý až zdravý (R2)	
XIII	Granit mírně zvětralý (R3)	
XIV	Granit silně až mírně zvětralý (R4)	
XV	Granit silně zvětralý (R5)	
XVII	Granit zcela zvětralý (R6), charakteru štěrku hlinitého (S4 GM)	1,0-1,8 m
XVIII	Granit zcela zvětralý (R6), charakteru písku s příměsí jemnozrné zeminy (S3 B-F)	0,5-1,4 m
XIX	Granit zcela zvětralý (R6), charakteru písku hlinitého až jílovitého (S4 SM, S5 SC)	0,2-0,7 m

MATERIÁLY:

ZÁKLADY
DŘÍKY PILÍŘŮ
ŮLOŽNÉ PRAHY, ZÁV. ZDI, KRÍDLA
NOSNÁ KONSTRUKCE

C30/37 - XF1+XA2+XC2
C35/45 - XF1+XD1+XC4
C30/37 - XF4+XD3+XC4
C30/37 - XF4+XD3+XC4

TKP KAP 18 - BETONOVÉ KONSTRUKCE A MOSTY
ČSN EN 206+A2 - BETON - SPECIFIKACE, VLASTNOSTI, VÝROBA A SHODA

ČÁST D.2
SO 202



ČISTOPIS
Souřadnicový systém S-JTSK, Výškový systém Bpv
Objednatel:
ŘEDITELSTVÍ SILNIC A DÁLNIC s. p.
Čerčanská 2023/12
140 00 Praha 4 - Krč

Zhotovitel PD: PRAGOPROJEKT, o.s., K Rybáře 1668/16, 147 54 Praha 4, IČO: 45272387, www.pragoprojekt.cz, datová schránka: 4kfr54	
Navrhl/vypracoval: Ing. Karolína HEDVÁŽ podpis: <i>K. Hedváž</i>	Zodpovědný projektant: Ing. Martin BLÁTSKÝ podpis: <i>M. Blátský</i>
Technická kontrola: Ing. Kamil PEJCHAL podpis: <i>K. Pechal</i>	Navrhl inženýr projektu: Ing. Pavel ŠIAPA podpis: <i>P. Šíapa</i>
	Zástupce zodpovědného projektanta: Ing. Jan BAZIL podpis: <i>J. Bazil</i>
	Zástupce hlavního inženýra projektu: Ing. Radovan STANKOVEN podpis: <i>R. Stankoven</i>

Kraj: KARLOVARSKÝ KRAJ	Číslo zakázky: 25-150-2
Místo stavby: OLŠOVÁ VRATA, ANEŠKÁ HORA, ŽALMANOV, HORNÍ TAŠOVICE, BOCHOV	Číslo okna: 05-219
Objednatel: ŘSD s. p., Čerčanská 2023/12, 140 00 Praha 4, IČO: 65993390	Datum: 03/2026
Název stavby: D6 OLŠOVÁ VRATA-ŽALMANOV, VD-ZDS	Formát: <i>PDF</i>
Objekt: MOST NA D6 PŘES LOMNICKÝ POTOK V km 1,600 SO101	Stupeň: PDPS
Příloha: PODÉLNÉ ŘEZY	Číslo přílohy: 04