


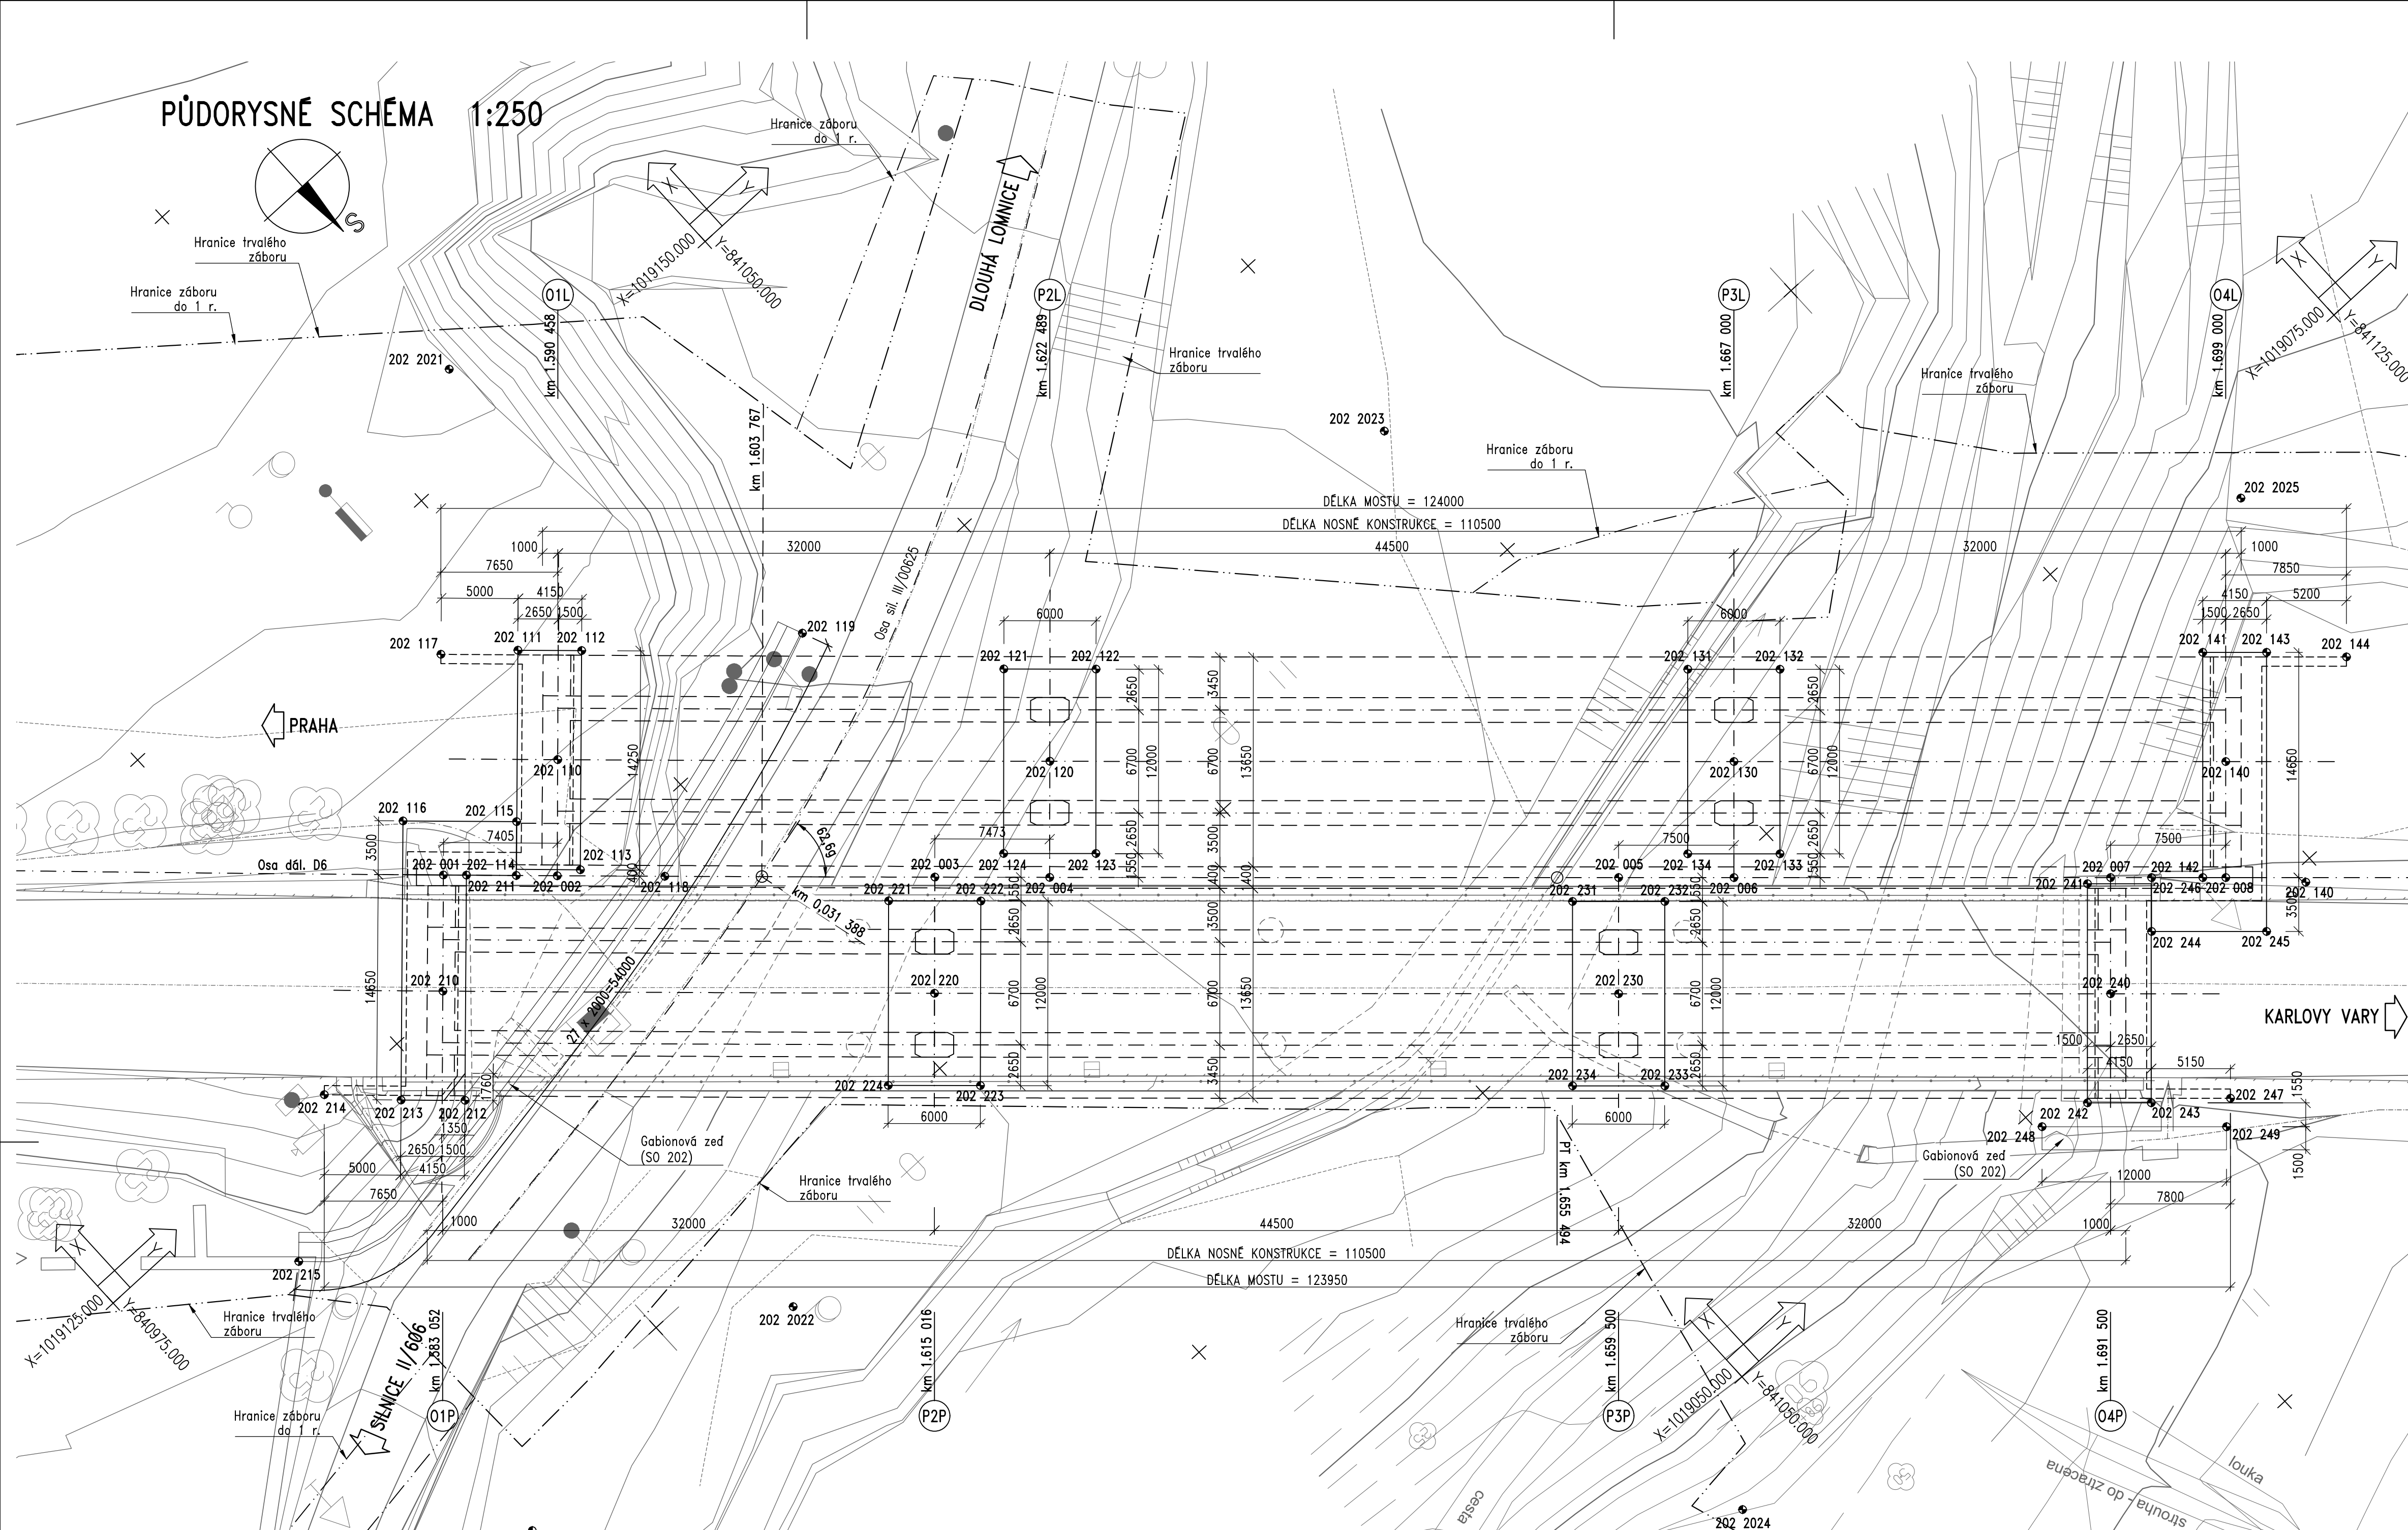


| Levý most |             |               |         |  |                       |
|-----------|-------------|---------------|---------|--|-----------------------|
| Bod       | Y (m)       | X (m)         | Z (m)   |  | Pozn.                 |
| 202 110   | 841 020.190 | 1 019 131.589 |         |  | prūs. os LM D6 a O1L  |
| 111       | 841 023.071 | 1 019 138.593 | 672.150 |  | základ O1L            |
| 112       | 841 026.119 | 1 019 135.777 | 672.150 |  | základ O1L            |
| 113       | 841 016.448 | 1 019 125.311 | 672.150 |  | základ O1L            |
| 114       | 841 013.114 | 1 019 127.847 | 672.150 |  | základ křídla u O1L   |
| 115       | 841 015.489 | 1 019 130.418 | 672.150 |  | základ křídla u O1L   |
| 116       | 841 010.073 | 1 019 135.434 | 672.150 |  | základ křídla u O1L   |
| 117       | 841 019.199 | 1 019 141.770 | 672.150 |  | křídlo opěry O1L      |
| 118       | 841 020.217 | 1 019 121.290 | 669.736 |  | prūs. LM D6 a gabionu |
| 119       | 841 037.488 | 1 019 126.923 | 669.100 |  | gabion vlevo          |
| 120       | 841 043.756 | 1 019 109.916 |         |  | prūs. os D6 a P2L     |
| 121       | 841 045.594 | 1 019 116.370 | 664.000 |  | základ pilíře P2L     |
| 122       | 841 050.018 | 1 019 112.317 | 664.000 |  | základ pilíře P2L     |
| 123       | 841 041.911 | 1 019 103.469 | 664.000 |  | základ pilíře P2L     |
| 124       | 841 037.487 | 1 019 107.522 | 664.000 |  | základ pilíře P2L     |
| 130       | 841 076.596 | 1 019 079.894 |         |  | prūs. os LM D6 a P3L  |
| 131       | 841 078.428 | 1 019 086.348 | 662.500 |  | základ pilíře P3L     |
| 132       | 841 082.858 | 1 019 082.301 | 662.500 |  | základ pilíře P3L     |
| 133       | 841 074.765 | 1 019 073.441 | 662.500 |  | základ pilíře P3L     |
| 134       | 841 070.335 | 1 019 077.488 | 662.500 |  | základ pilíře P3L     |
| 140       | 841 100.222 | 1 019 058.311 |         |  | prūs. os LM D6 a O4L  |
| 141       | 841 103.904 | 1 019 064.565 | 675.150 |  | základ opěry O4L      |
| 142       | 841 094.023 | 1 019 053.749 | 675.150 |  | základ opěry O4L      |
| 143       | 841 106.967 | 1 019 061.766 | 675.150 |  | základ opěry O4L      |
| 144       | 841 110.604 | 1 019 058.037 | 675.150 |  | křídlo opěry O4L      |

| Pravý most |             |               |         |  |                      |
|------------|-------------|---------------|---------|--|----------------------|
| Bod        | Y (m)       | X (m)         | Z (m)   |  | Pozn.                |
| 202 210    | 841 004.519 | 1 019 125.516 |         |  | prūs. os PM D6 a O1P |
| 211        | 841 010.739 | 1 019 130.045 | 672.150 |  | základ opěry O1P     |
| 212        | 841 000.783 | 1 019 119.298 | 672.150 |  | základ opěry O1P     |
| 213        | 840 997.739 | 1 019 122.118 | 672.150 |  | základ opěry O1P     |
| 214        | 840 994.279 | 1 019 125.741 | 672.150 |  | křídlo opěry O1P     |
| 215        | 840 985.735 | 1 019 118.855 | 670.990 |  | Gabion vpravo        |
| 220        | 841 028.040 | 1 019 103.840 |         |  | prūs. os PM D6 a P2P |
| 221        | 841 029.885 | 1 019 110.289 | 664.000 |  | základ pilíře P2P    |
| 222        | 841 034.307 | 1 019 106.233 | 664.000 |  | základ pilíře P2P    |
| 223        | 841 026.194 | 1 019 097.390 | 664.000 |  | základ pilíře P2P    |
| 224        | 841 021.773 | 1 019 101.447 | 664.000 |  | základ pilíře P2P    |
| 230        | 841 060.875 | 1 019 073.804 |         |  | prūs. os PM D6 a P3P |
| 231        | 841 062.707 | 1 019 080.258 | 662.500 |  | základ pilíře P3P    |
| 232        | 841 067.136 | 1 019 076.211 | 662.500 |  | základ pilíře P3P    |
| 233        | 841 059.043 | 1 019 067.351 | 662.500 |  | základ pilíře P3P    |
| 234        | 841 054.613 | 1 019 071.398 | 662.500 |  | základ pilíře P3P    |
| 240        | 841 084.501 | 1 019 052.221 |         |  | prūs. os PM D6 a O4P |
| 241        | 841 088.216 | 1 019 058.512 | 675.150 |  | základ opěry O4P     |
| 242        | 841 078.805 | 1 019 047.991 | 675.150 |  | základ opěry O4P     |
| 243        | 841 081.669 | 1 019 045.192 | 675.150 |  | základ opěry O4P     |
| 244        | 841 089.204 | 1 019 053.411 | 675.150 |  | základ křídla u O4P  |
| 245        | 841 094.726 | 1 019 048.366 | 675.150 |  | základ křídla u O4P  |
| 246        | 841 091.564 | 1 019 055.995 | 675.150 |  | základ opěry O4P     |
| 247        | 841 085.673 | 1 019 041.940 | 675.150 |  | křídlo opěry O4P     |
| 248        | 841 075.381 | 1 019 048.836 | 676.400 |  | Gabion vpravo        |
| 249        | 841 084.241 | 1 019 040.743 | 678.650 |  | Gabion vpravo        |

| průsečky osy dálnice D6 s osami uložení jednotlivých opěr/pilířů |         |            |             |  |
|------------------------------------------------------------------|---------|------------|-------------|--|
| O1P                                                              | 202 001 | 841009.639 | 1019131.064 |  |
| O1L                                                              | 202 002 | 841015.075 | 1019126.035 |  |
| P2P                                                              | 202 003 | 841033.144 | 1019109.403 |  |
| P2L                                                              | 202 005 | 841038.652 | 1019104.353 |  |
| P3P                                                              | 202 006 | 841065.967 | 1019079.379 |  |
| P3L                                                              | 202 007 | 841071.504 | 1019074.320 |  |
| O4P                                                              | 202 008 | 841089.593 | 1019057.796 |  |
| O4L                                                              | 202 009 | 841095.130 | 1019052.737 |  |

| průsečky osy LM s úložnými osami jednotlivých opěr/pilířů |         |            |             |
|-----------------------------------------------------------|---------|------------|-------------|
| O1L                                                       | 202 110 | 841020.190 | 1019131.589 |
| P2L                                                       | 202 120 | 841043.756 | 1019109.916 |
| P3L                                                       | 202 130 | 841076.596 | 1019079.894 |
| O4L                                                       | 202 140 | 841100.222 | 1019058.311 |

| průsečky osy PM s úložnými osami jednotlivých opěr/pilířů |         |            |             |
|-----------------------------------------------------------|---------|------------|-------------|
| O1P                                                       | 204 210 | 841004.519 | 1019125.516 |
| P2P                                                       | 204 220 | 841028.040 | 1019103.840 |
| P3P                                                       | 204 230 | 841060.875 | 1019073.804 |
| O4P                                                       | 204 240 | 841084.501 | 1019052.221 |

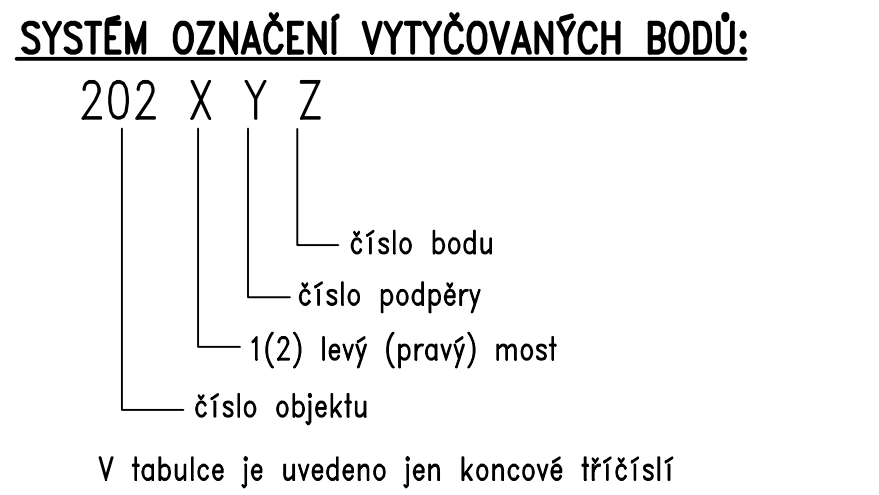

SOUŘADNÝ SYSTÉM:  
JTSK  
VÝŠKOVÝ SYSTÉM:  
B.p.v.

POZNÁMKY :

- PRŮSEČKY OSY MOSTU S ÚLOŽNÝMI PŘÍMKAMI JEDNOTLIVÝCH PODPOR JSOU POVAŽOVÁNY ZA CHARAKTERISTICKÉ BODY (CHB), RESP. HLAVNÍ VÝŠKOVÉ BODY (HVB). OSTATNÍ VYTÝČOVANÉ BODY JSOU POVAŽOVÁNY ZA PODROBNÉ BODY (PB).
- PARAMETRY SMĚROVÉHO A VÝŠKOVÉHO VEDENÍ DÁLNIČE D6 A KOMUNIKACÍ POD MOSTEM VIZ TECHNICKÁ ZPRÁVA.

PŘESNOST VYTÝČENÍ :

(DLE TKP PK, kap.1, příl. 9)

PRO CHARAKTERISTICKÉ BODY (CHB):  
DLE TAB. 24 A 25 V ČSN 730420-2

PRO HLAVNÍ VÝŠKOVÉ BODY (HVB):  
DLE TAB. 24 A 25 V ČSN 730420-2

PRO PODROBNÉ BODY (PB):  
DLE TAB. 27 V ČSN 730420-2

GEOMETRICKÁ PŘESNOST:

(DLE TKP PK kap.1, příl. 9 A TKP PK, kap. 18)

TOLERANCE ROVINATOSTI:  
DLE TAB. 4 V TKP PK, kap. 1, příl. 9

ODCHYLKY SVISLOSTI:  
DLE TAB. 5 V TKP PK, kap. 1, příl. 9

| body mikrosítě |      |           |            |
|----------------|------|-----------|------------|
| 202            | 2021 | 841032.10 | 1019155.10 |
|                | 2022 | 841007.50 | 1019095.00 |
|                | 2023 | 841074.30 | 1019111.10 |
|                | 2024 | 841044.20 | 1019043.60 |
|                | 2025 | 841112.50 | 1019070.30 |

ČÁST D.2  
SO 202

ČISTOPIS

Souřadnicový systém S-JTSK, Výškový systém Bpv

Objednatel:

ŘEDITELSTVÍ SILNIC A DÁLNIC

ŘEDITELSTVÍ SILNIC A DÁLNIC s. p.  
Čerčanská 2023/12  
140 00 Praha 4 – Krč

|   |                                                                     |                                                                                     |   |
|---|---------------------------------------------------------------------|-------------------------------------------------------------------------------------|---|
| Zhotovitel PD: PRAGOPROJEKT, s.r.o., K Rybářce 1688/16, 147 54 Praha 4, IČO: 45272387, www.pragoprojekt.cz, datová schránka: 4k4r54 |                                                                     |                                                                                     |   |
| Hlavní/vypracoval:<br>Ing. Karolína HEDVÁ<br>podpis: <i>K.H.</i>                                                                    | Zodpovědný projektant:<br>Ing. Martin BLAŽEK<br>podpis: <i>M.B.</i> | Zástupce zodpovědného projektanta:<br>Ing. Jan BAZIL<br>podpis: <i>J.B.</i>         | <br><b>PRAGOPROJEKT</b> |
| Technická kontrola:<br>Ing. Kamil PEČKA<br>podpis: <i>K.P.</i>                                                                      | Hlavní inženýr projektu:<br>Ing. Pavel SLÁPA<br>podpis: <i>P.S.</i> | Zástupce hlavního inženýra projektu:<br>Ing. Radovan STANKOV<br>podpis: <i>R.S.</i> |   |
|   |                                                                     |                                                                                     |   |

|                   |                                                               |                |          |
|-------------------|---------------------------------------------------------------|----------------|----------|
| Kraj:             | KARLOVARSKÝ KRAJ                                              | Číslo zakázky: | 25-150-2 |
| Místo stavby:     | OLŠOVÁ VRATA, ANDELSKÁ HORA, ŽALMANOV, HORNÍ TAŠOVICE, BOCHOV | Číslo díla:    | 05-219   |
| Objednatel:       | ŘSD s. p., Čerčanská 2023/12, 140 00 Praha 4, IČO 65993390    | Datum:         | 03/2026  |
| Název stavby:     | D6 OLŠOVÁ VRATA-ŽALMANOV, VD-ZDS                              | Formát:        |          |
| Objekt:           | MOST NA D6 PŘES LOMNICKÝ POTOK V km 1,600 SO101               | Měřítko:       |          |
| Příloha:          |                                                               | Stupeň:        | PDPS     |
| VYTÝČOVACÍ SCHÉMA |                                                               |                | Suprava: |
|                   |                                                               |                | 07       |