



PŮDORYSNÉ SCHÉMA 1:250
LEVÝ MOST

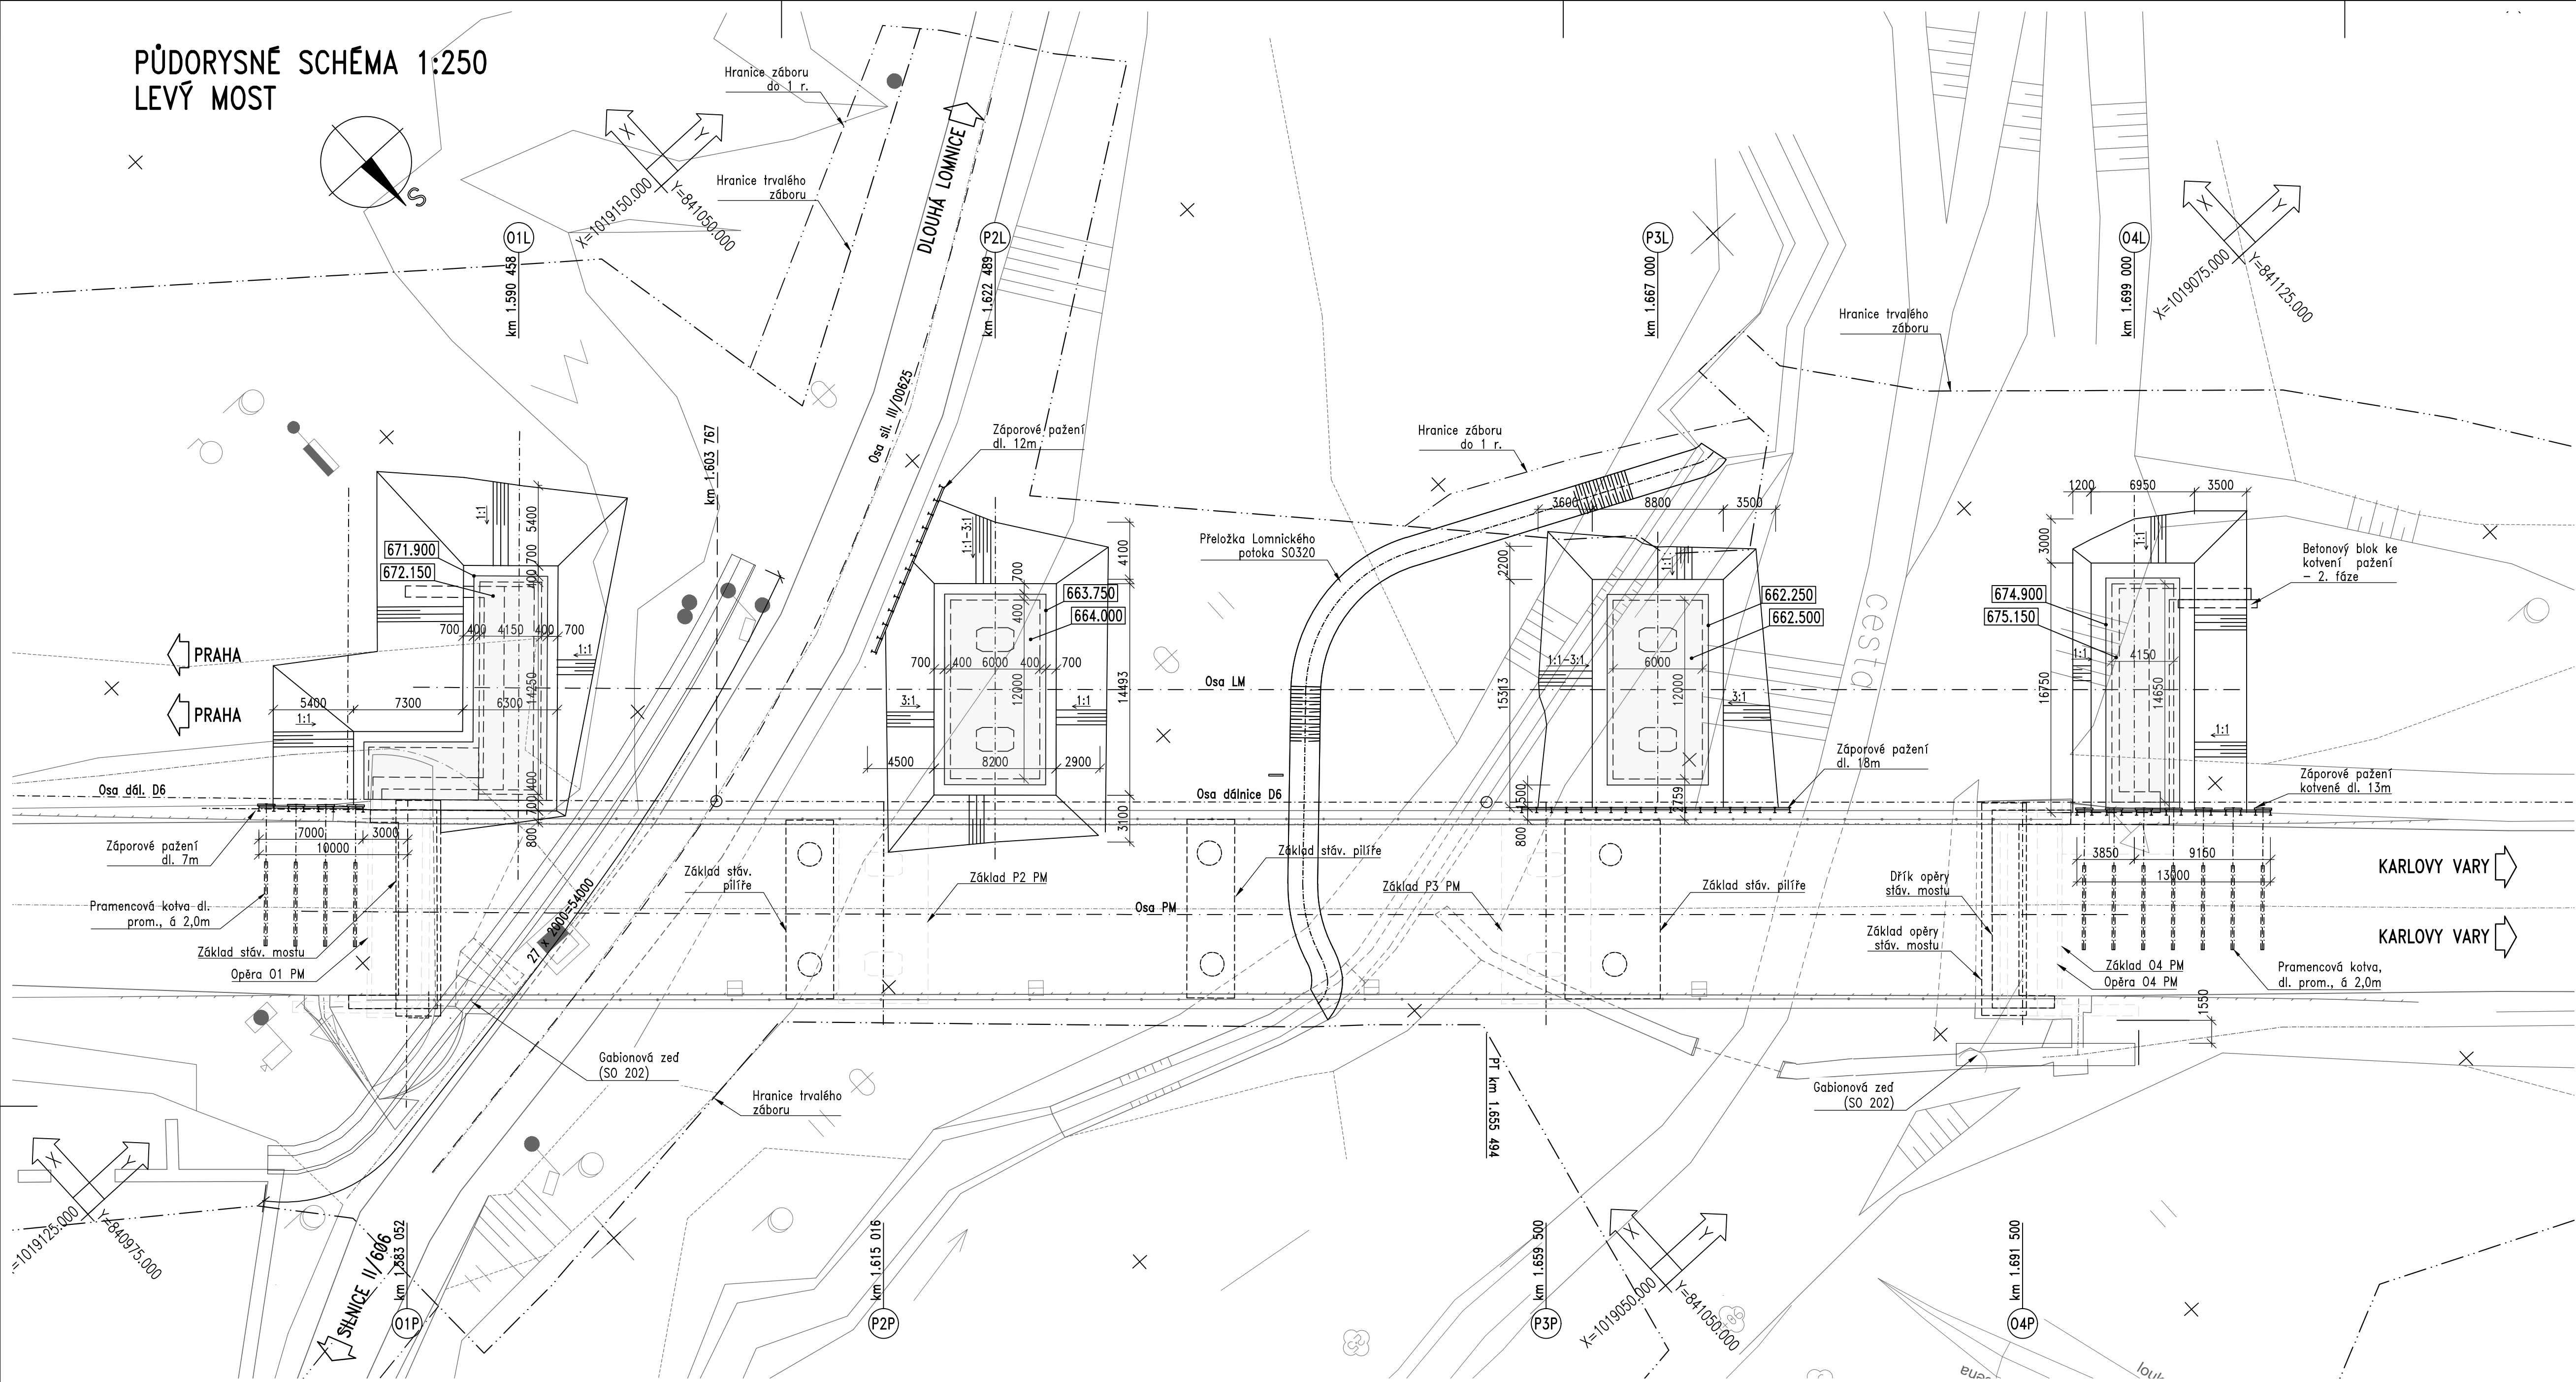


MATERIÁLY:
BETON:
PODKLADNÍ BETON
(TKP, KAP. 18)
C12/15-X0


PŮDORYS OPĚRY 01L A STÁVAJÍCÍ OPĚRY MOSTU EV.Č. 6-049 1:250

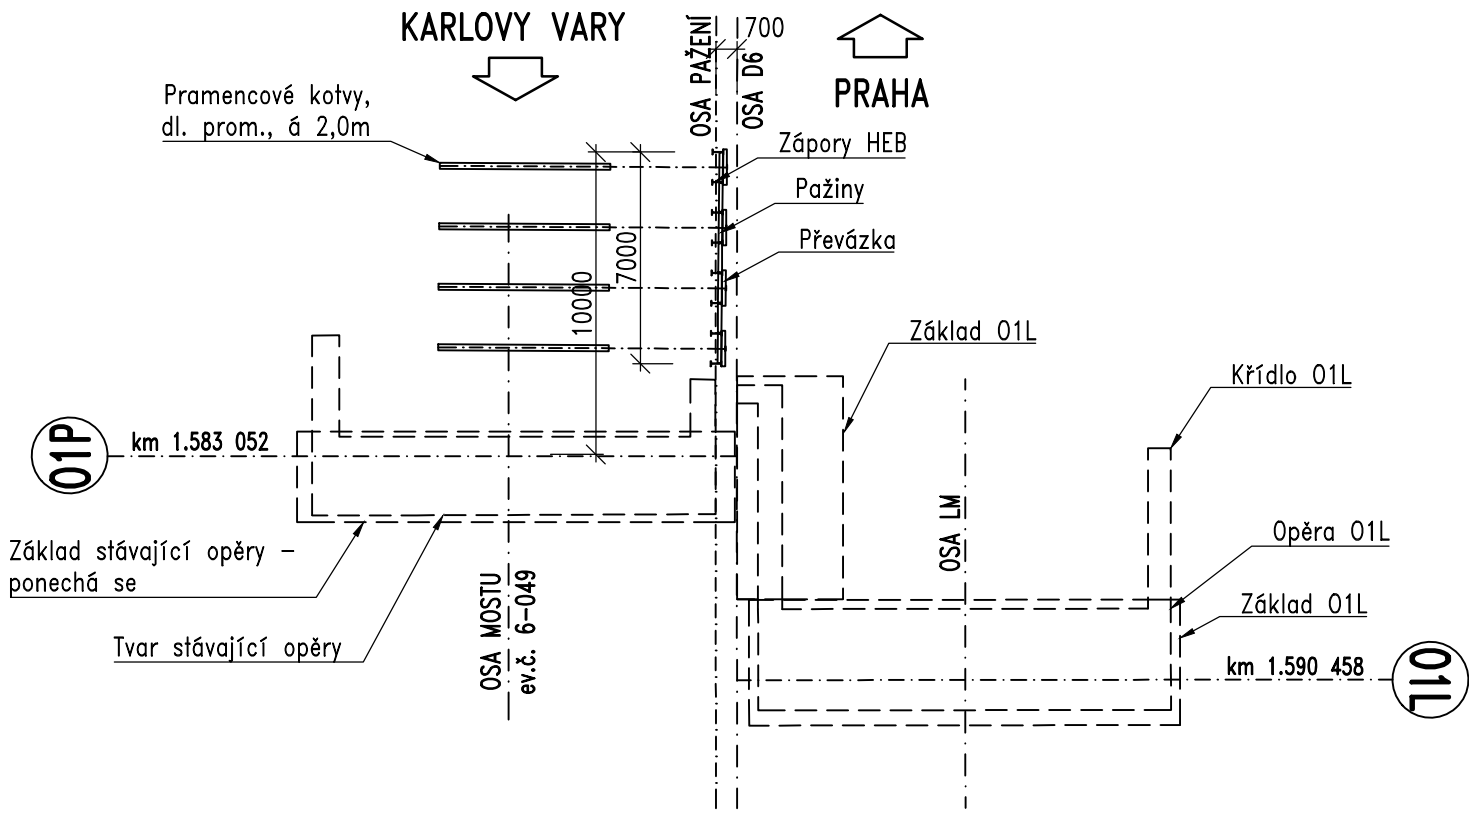


PŘÍČNÝ ŘEZ V OSE ULOŽENÍ 01L 1:250

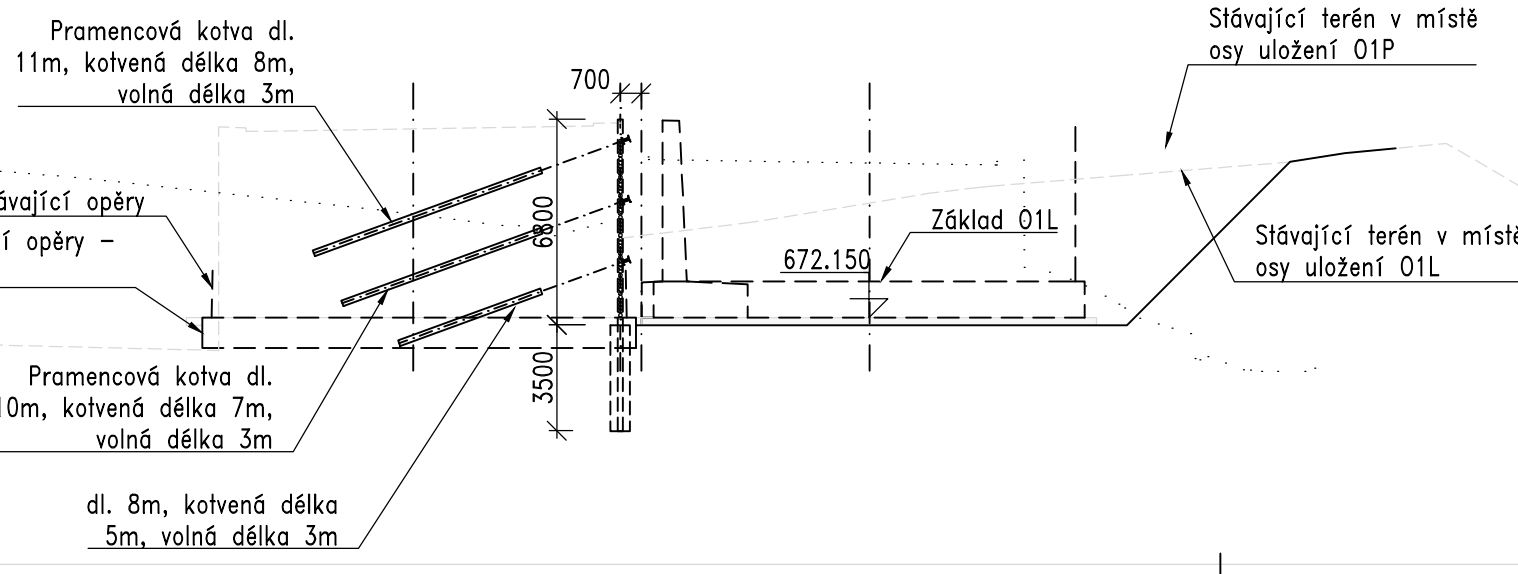

PŮDORYS OPĚRY 04L A STÁVAJÍCÍ OPĚRY MOSTU EV.Č. 6-049 1:100

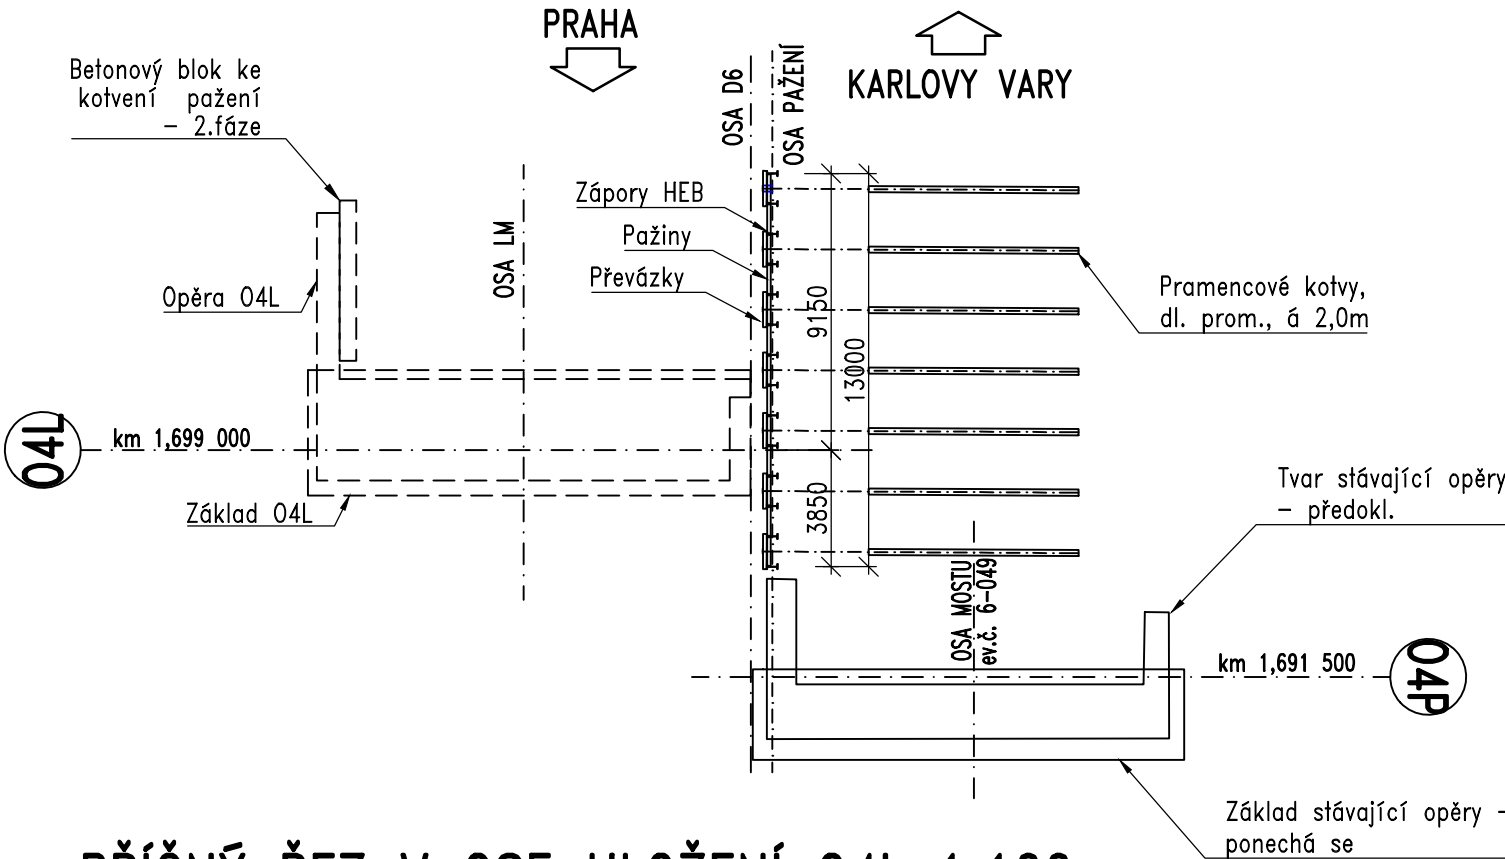

PŘÍČNÝ ŘEZ V OSE ULOŽENÍ 04L 1:100

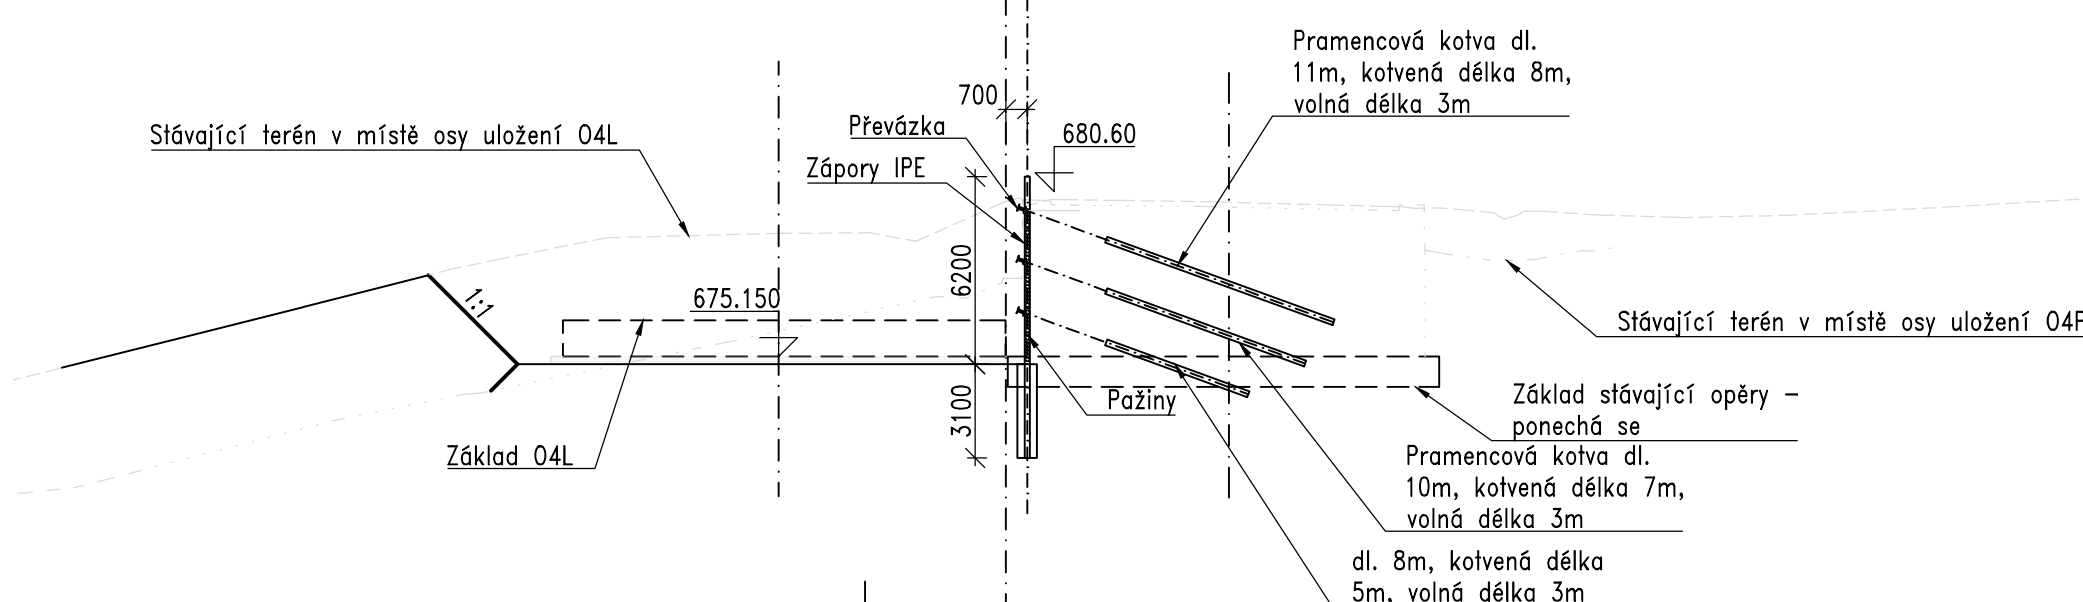

ČÁST D.2
SO 202


ČISTOPIS

Souřadnicový systém S-JTSK, Výškový systém Bpv

Objednatel:

**ŘEDITELSTVÍ
SILNIC
A DÁLNIC**

ŘEDITELSTVÍ SILNIC A DÁLNIC s. p.
Čerčanská 2023/12
140 00 Praha 4 – Krč

 Zhotovitel PD: PRAGOPROJEKT, a.s., K Rybáře 168/16, 147 54 Praha 4, IČO: 45272387, www.pragoprojekt.cz, datová schránka: 4klr54			
Navrhl/vypracoval: Ing. Karolína HEDGÁ podpis: <i>K. Hedgá</i>	Zodpovědný projektant: Ing. Martin BLATSKÝ podpis: <i>M. Blatský</i>	Zástupce zodpovědného projektanta: Ing. Jan BAZIL podpis: <i>J. Bazil</i>	 PRAGOPROJEKT
Technická kontrola: Ing. Kamil PEJCHAL podpis: <i>K. Pechal</i>	Hlavní inženýr projektu: Ing. Pavel SLÁPA podpis: <i>P. Slápa</i>	Zástupce hlavního inženýra projektu: Ing. Radovan STANKOVEN podpis: <i>R. Stankoven</i>	

Kraj:	KARLOVARSKÝ KRAJ	Číslo zakázky:	25-150-2
Místo stavby:	OLŠOVÁ VRATA, ANDELSKÁ HORA, ŽALMANOV, HORNÍ TAŠOVICE, BOCHOV	Číslo díla:	05-219
Objednatel:	ŘSD s. p., Čerčanská 2023/12, 140 00 Praha 4, IČO 65993390	Datum:	03/2026
Název stavby:	D6 OLŠOVÁ VRATA-ŽALMANOV, VD-ZDS	Formát:	
Objekt:	MOST NA D6 PŘES LOMNICKÝ POTOK V km 1,600 SO101	Měřítko:	
Příloha:		Stupeň:	
VÝKOPY A ZALOŽENÍ LEVÉHO MOSTU		PDPs	
		08.1	