




PŮDORYSNÉ SCHÉMA 1:250
PRAVÝ MOST

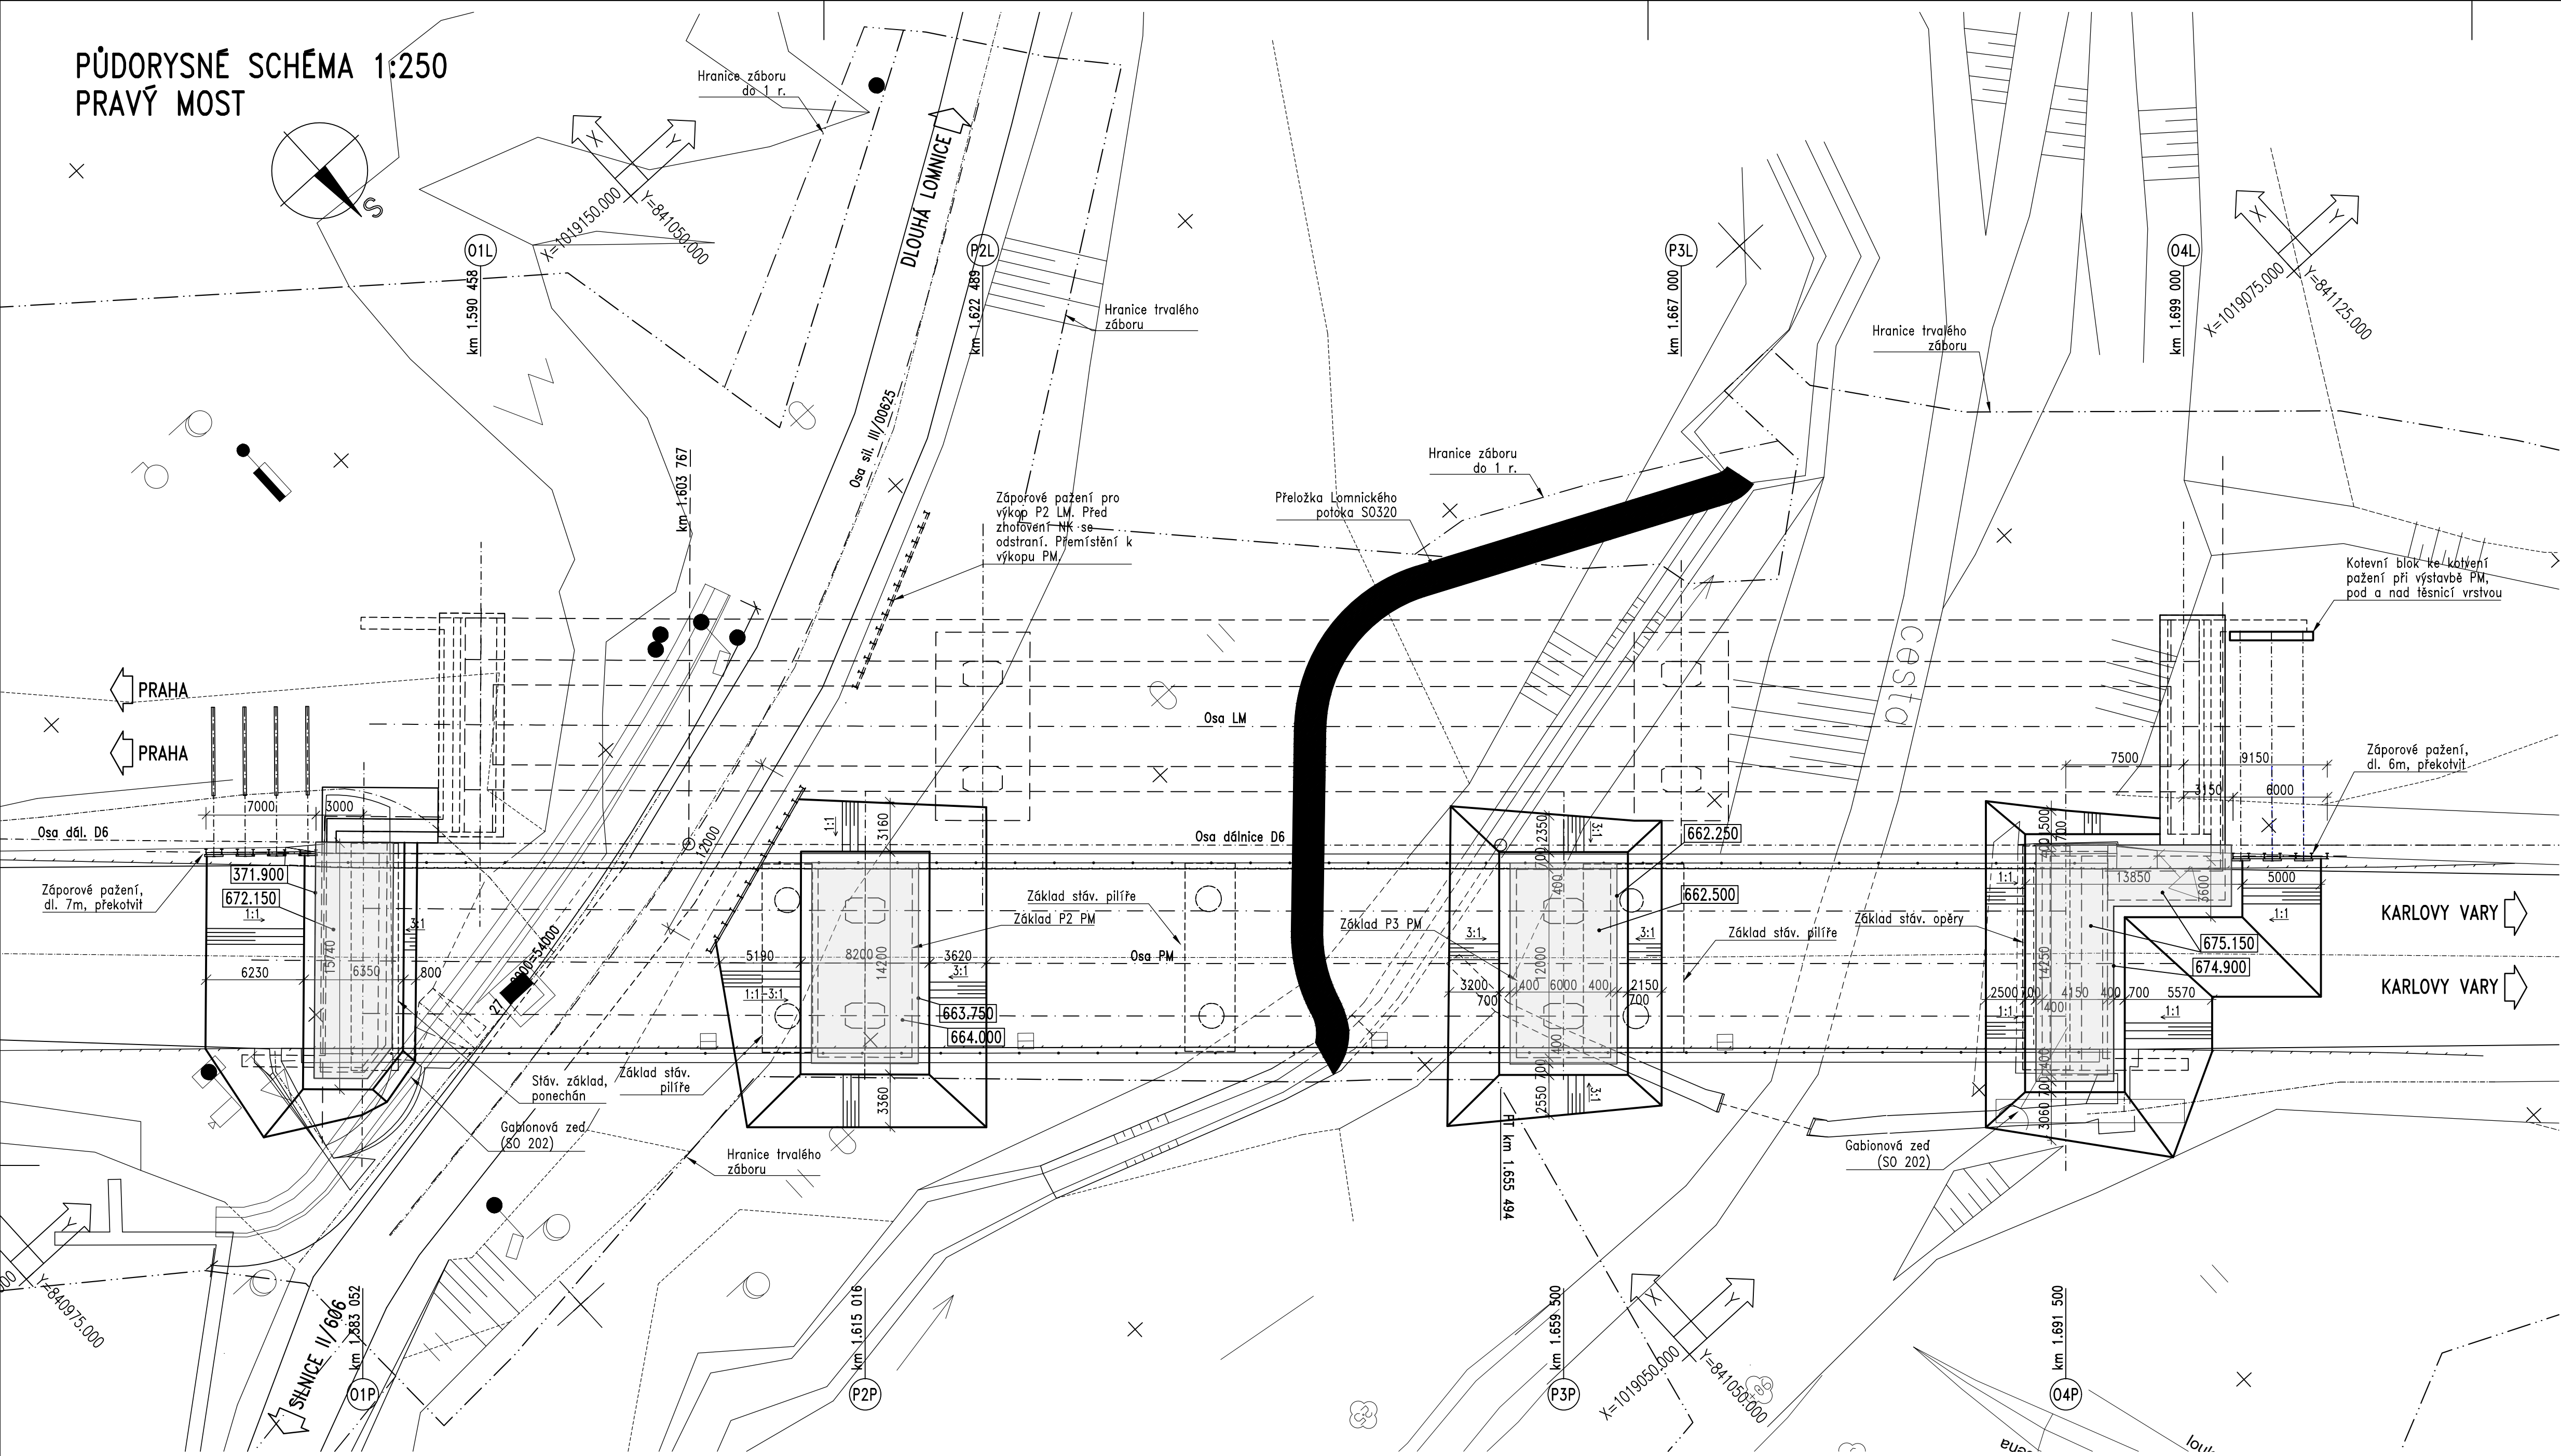


PŮDORYS OPĚRY O1P A O1L 1:250

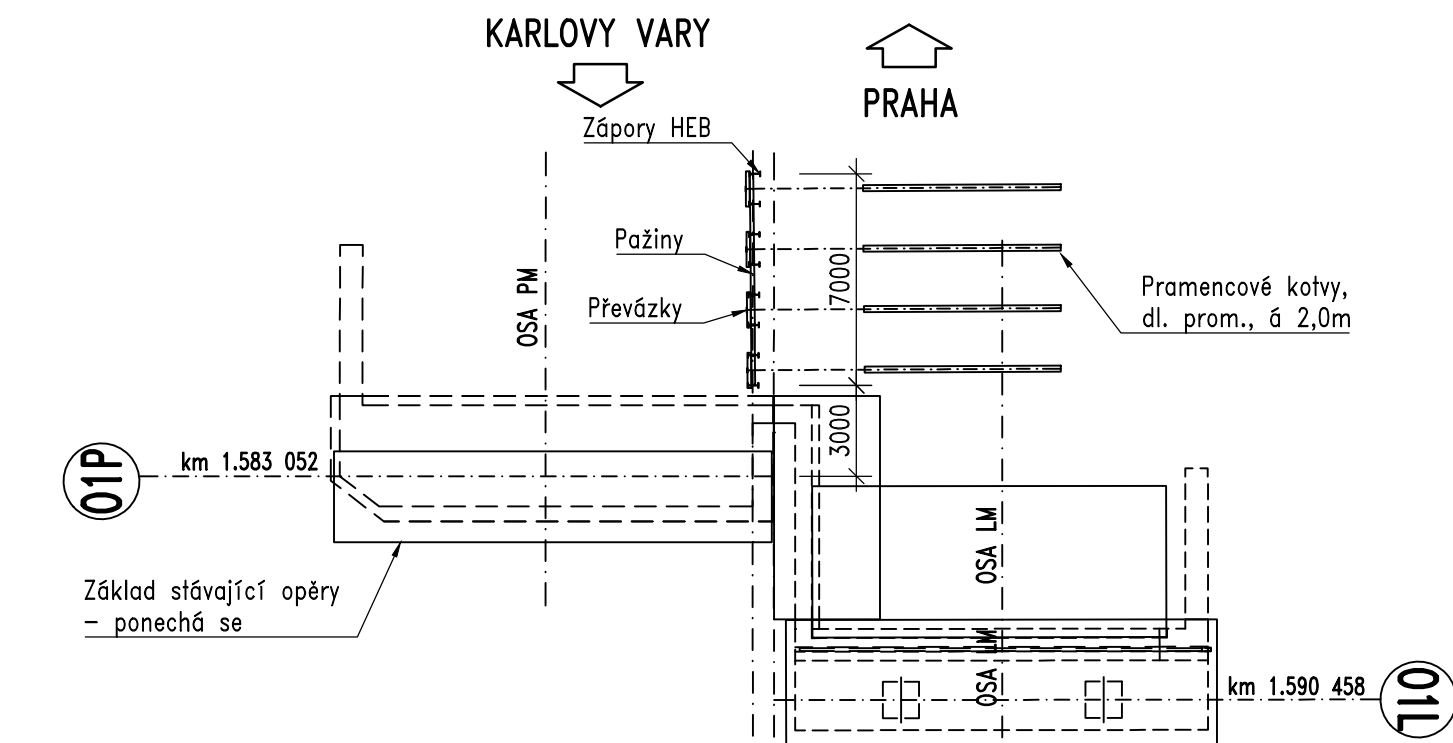


ŘEZ V OSE ULOŽENÍ O1P 1:250

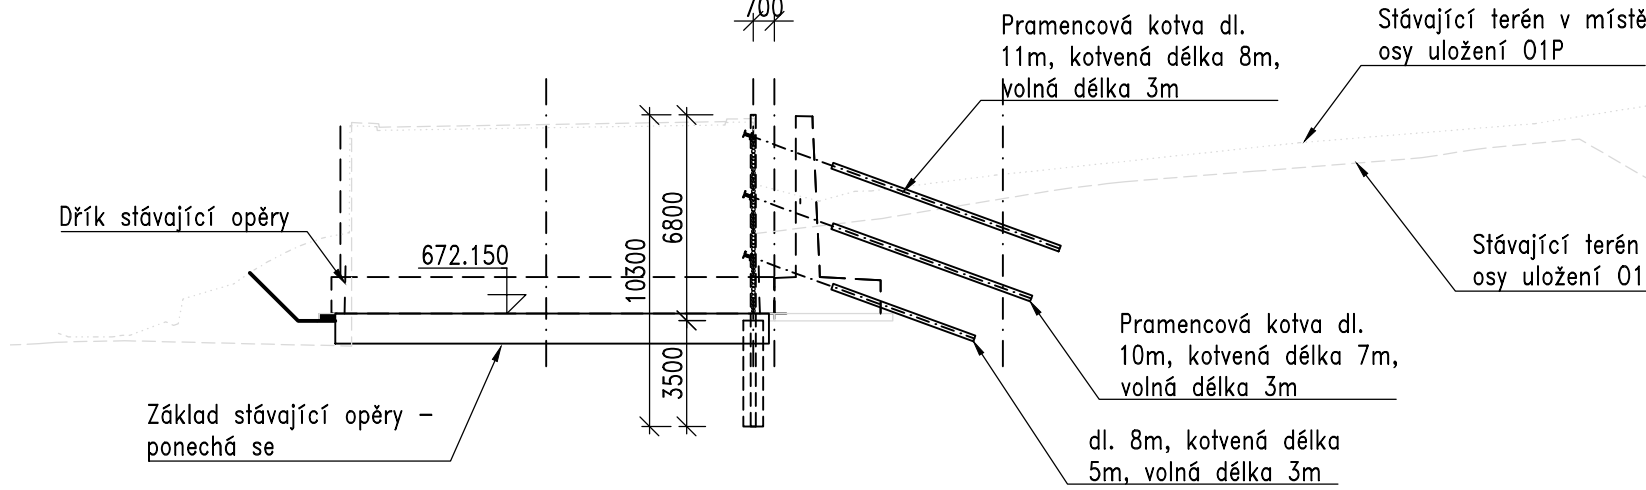

PŮDORYS OPĚRY O4P a O4L 1:250

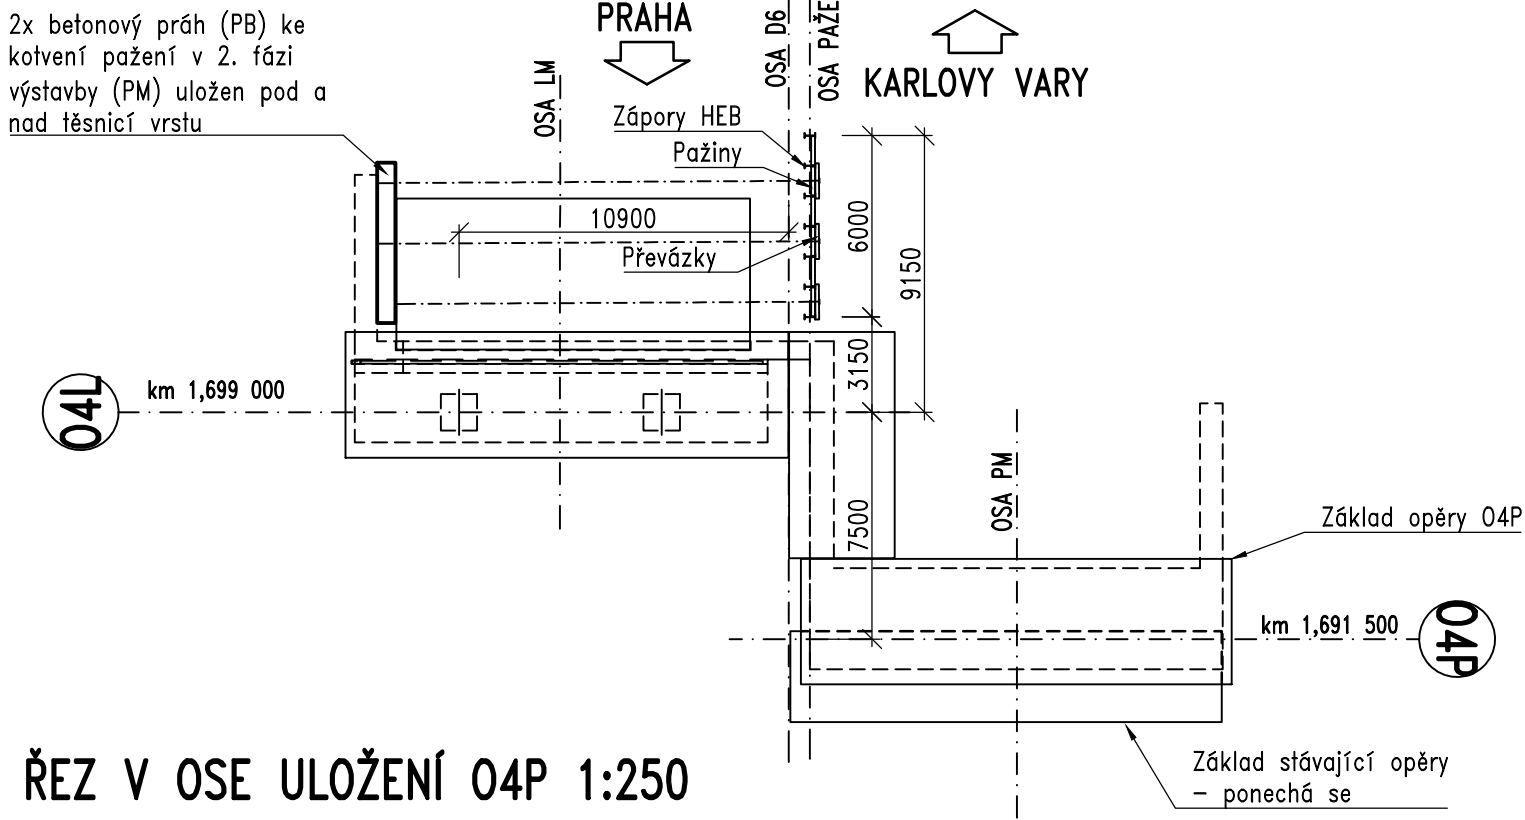

ŘEZ V OSE ULOŽENÍ O4P 1:250

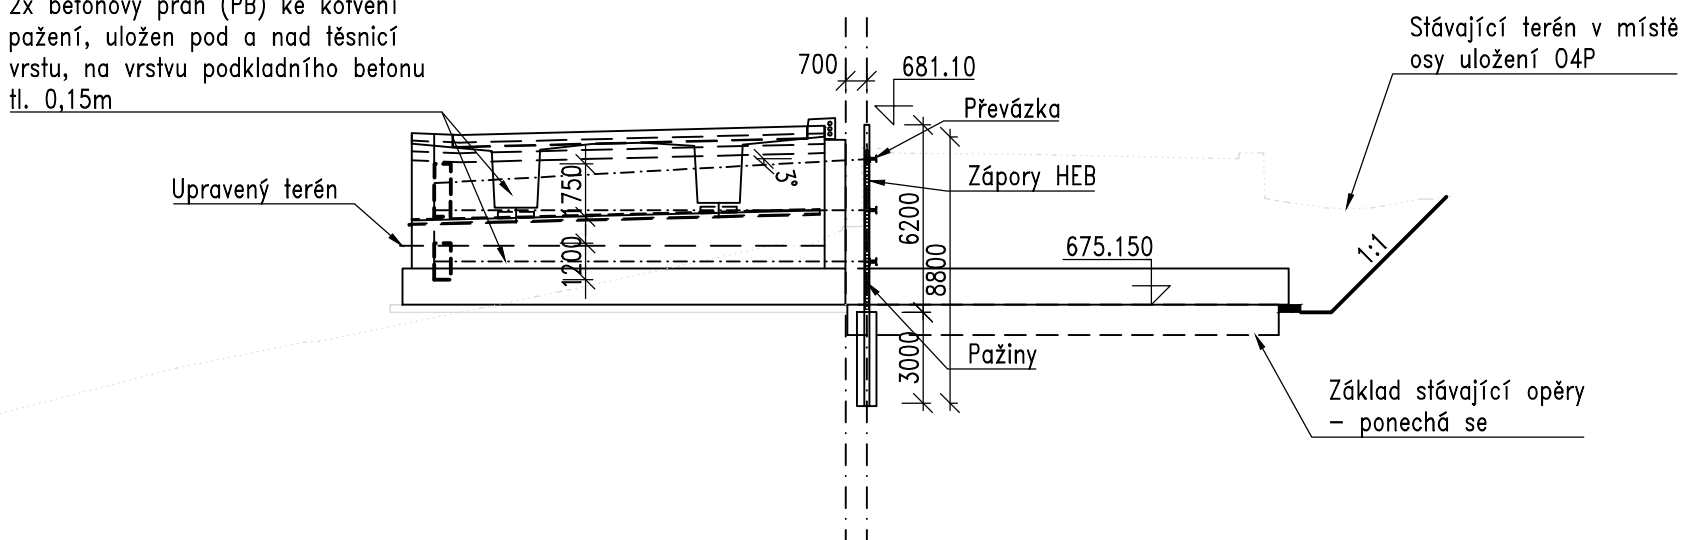

ČÁST D.2
SO 202

ČISTOPIS

Souřadnicový systém S-JTSK, Výškový systém Bpv

Ředitelství silnic a dálnic

Objednatel:

Ředitelství silnic a dálnic s. p.
Čerčanská 2023/12
140 00 Praha 4 – Krč

Zhotovitel PD: PRAGOPROJEKT, a.s., K Ryšánce 1668/16, 147 54 Praha 4, IČO: 45272387, www.pragoprojekt.cz, datová schránka: 4klfr54		
Návrh/vypracoval: Ing. Karolína HEDGÁ podpis: <i>K. Hedgá</i>	Zodpovědný projektant: Ing. Martin BLATSKÝ podpis: <i>M. Blatský</i>	Zástupce zodpovědného projektanta: Ing. Jan BAZIL podpis: <i>J. Bazil</i>
Technická kontrola: Ing. Kamil PEJCHAL podpis: <i>K. Pechal</i>	Hlavní inženýr projektu: Ing. Pavel SLÁPA podpis: <i>P. Slápa</i>	Zástupce hlavního inženýra projektu: Ing. Radovan STANKOVEN podpis: <i>R. Stankoven</i>



Kraj:	KARLOVARSKÝ KRAJ	Číslo zakázky:	25-150-2
Místo stavby:	OLŠOVÁ VRATA, ANDELSKÁ HORA, ŽALMANOV, HORNÍ TAŠOVICE, BOCHOV	Číslo díla:	05-219
Objednatel:	ŘSD s. p., Čerčanská 2023/12, 140 00 Praha 4, IČO 65993390	Datum:	03/2026
Název stavby:	D6 OLŠOVÁ VRATA-ŽALMANOV, VD-ZDS	Formát:	
Objekt:	MOST NA D6 PŘES LOMNICKÝ POTOK V km 1,600 S0101	Stupeň:	PDPS
Příloha:	VÝKOPY A ZALOŽENÍ PRAVÉHO MOSTU	Suprava:	08