




PODÉLNÝ ŘEZ OPĚROU O1 1:50

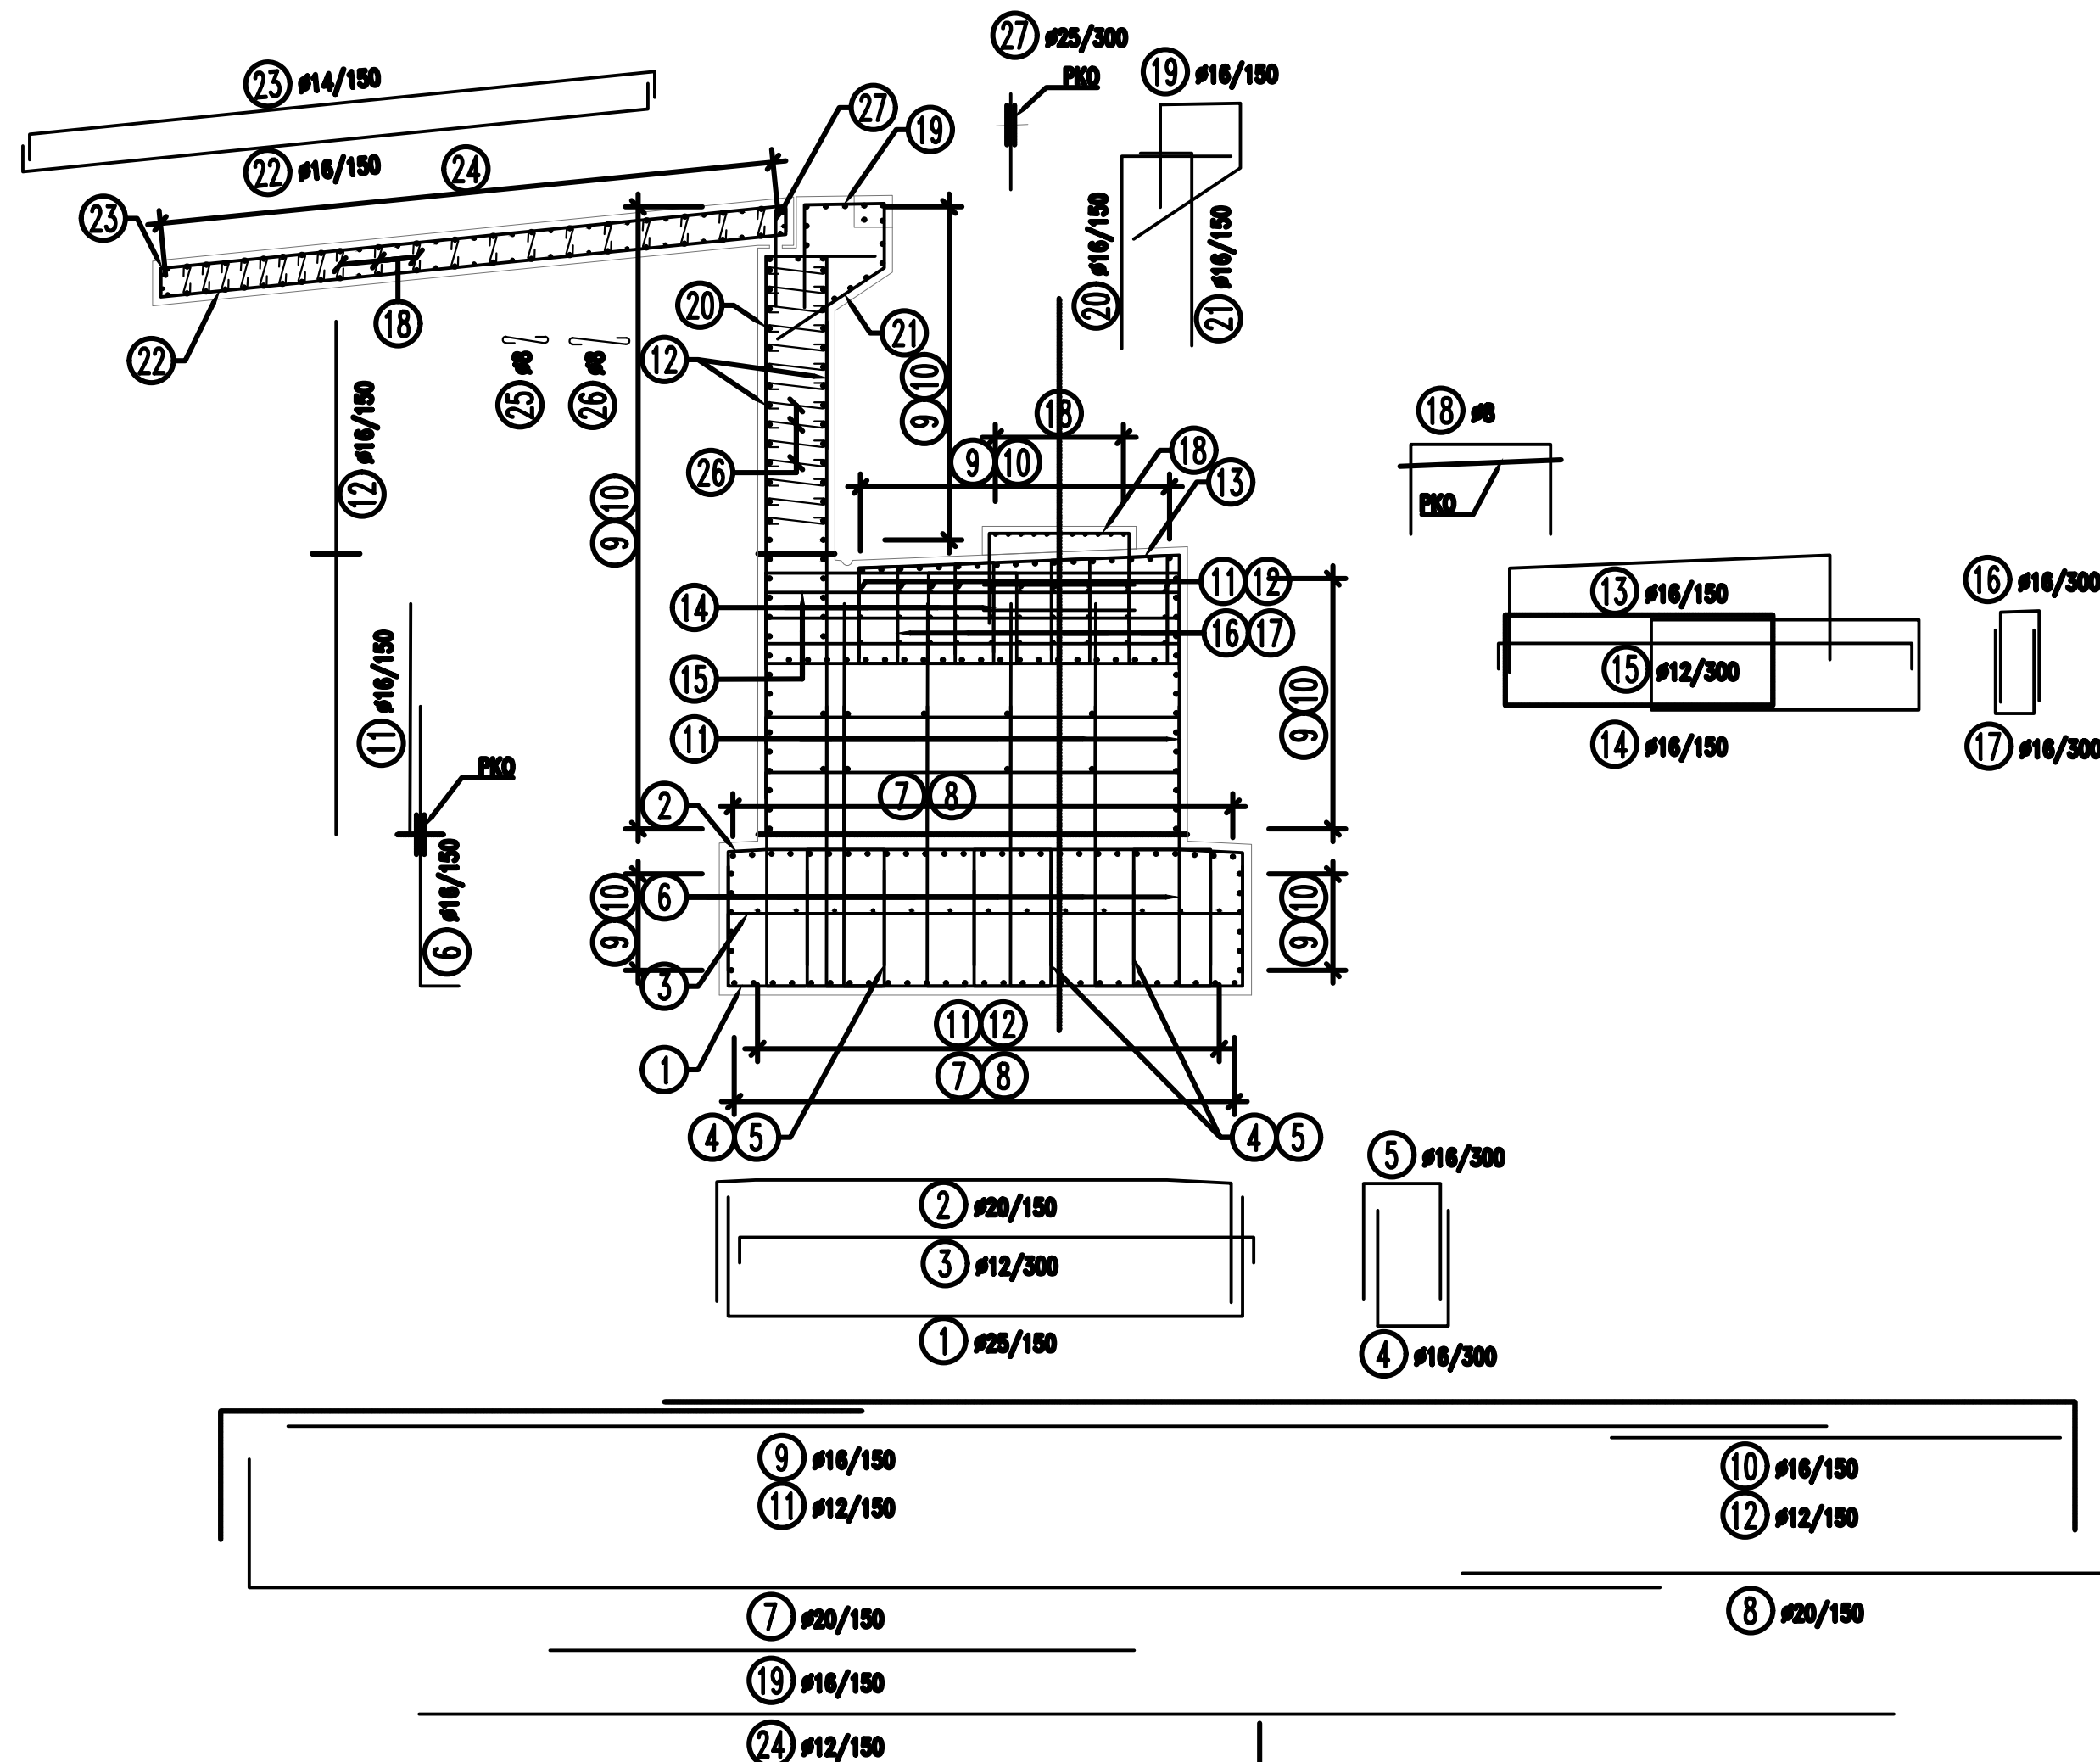

ŘEZ KŘÍDLEM PM 1:50

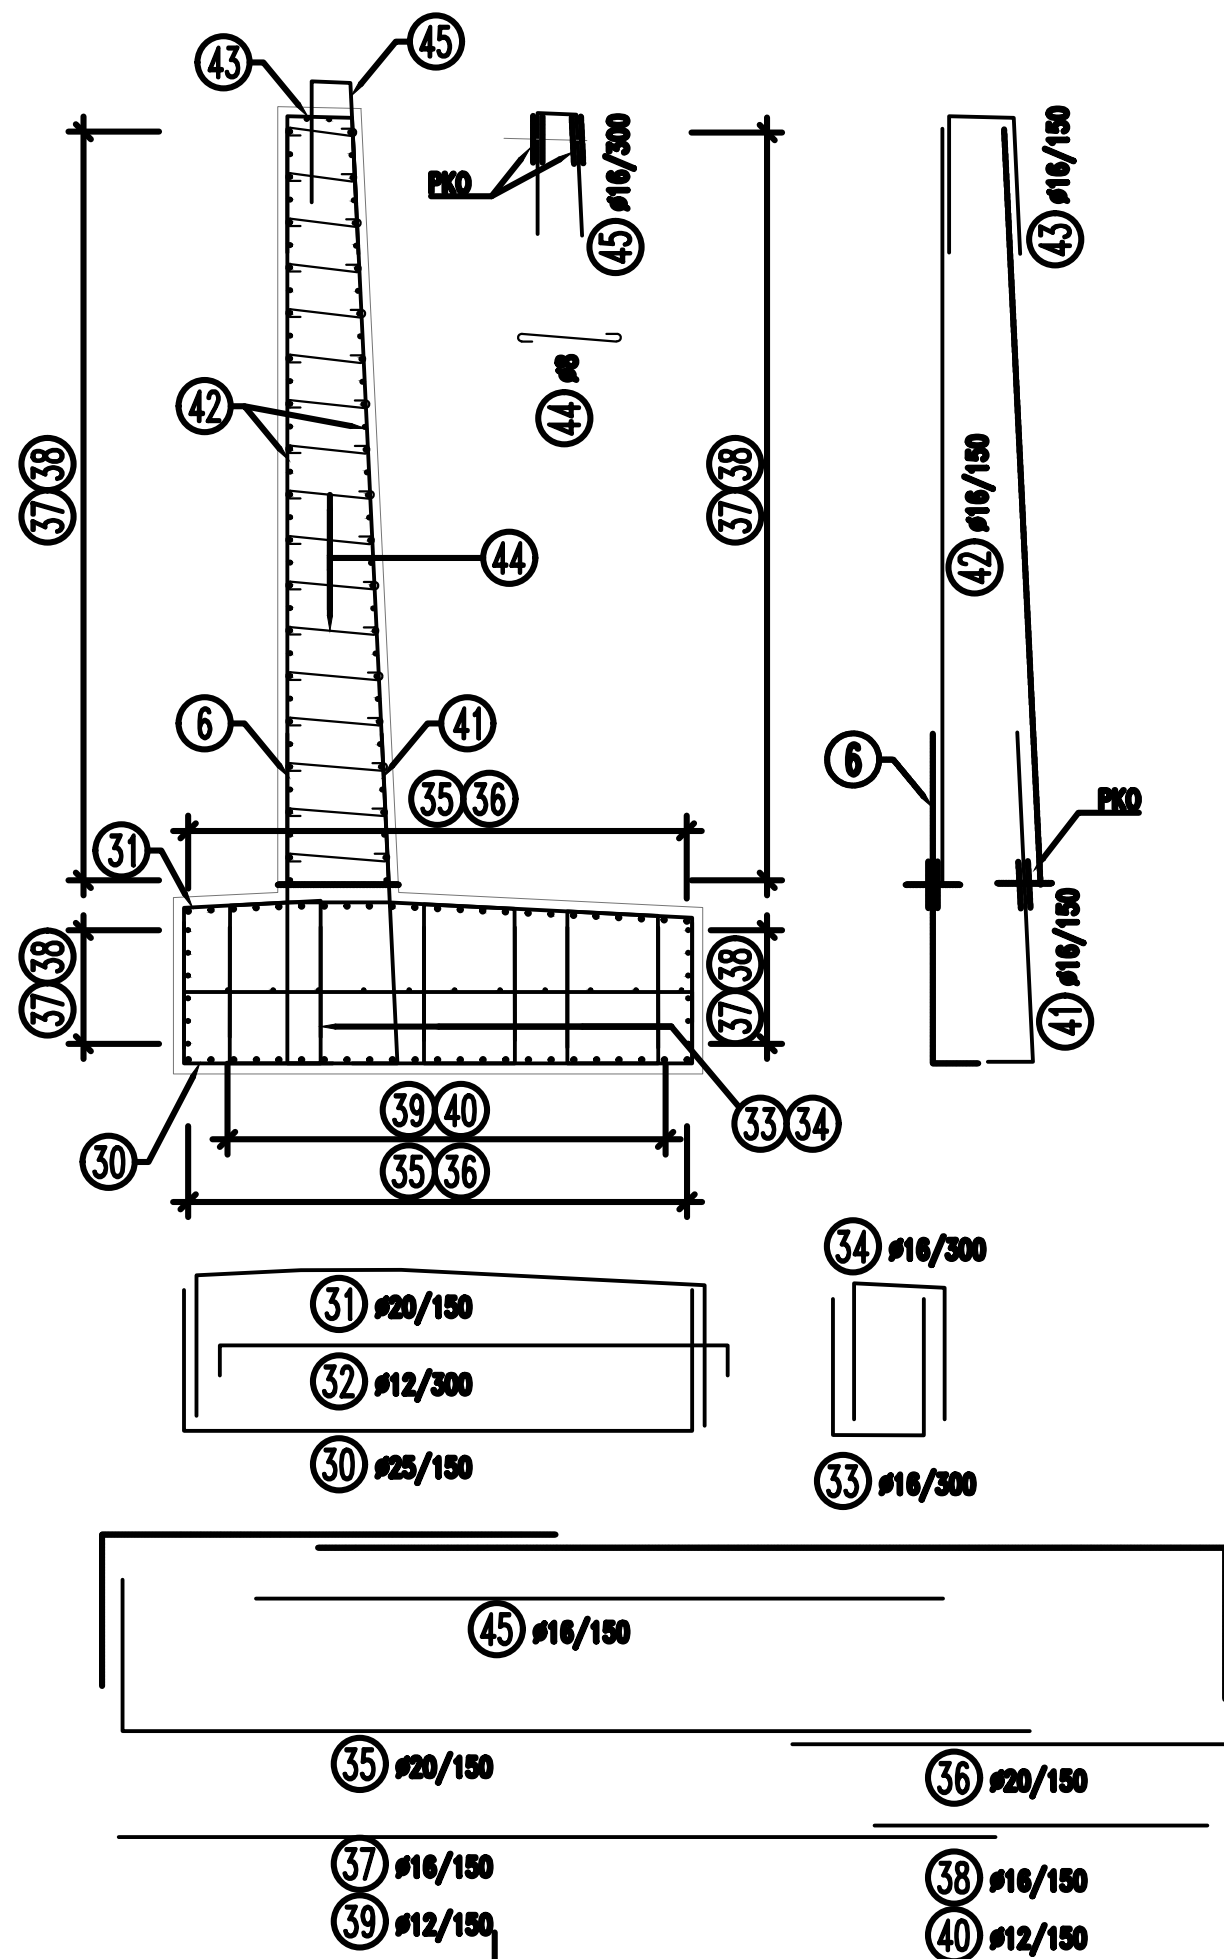

ŘEZ KŘÍDLEM 1:50

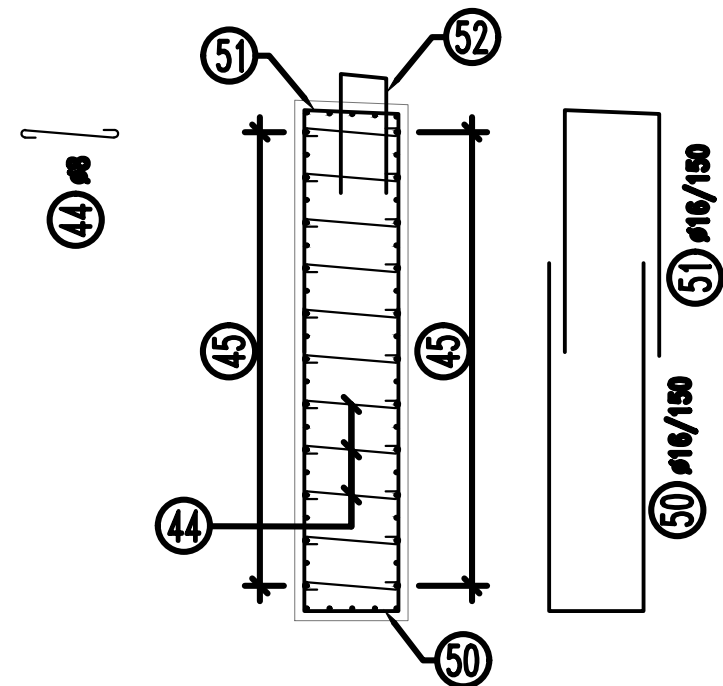

POZNÁMKY:

- VEŠKERÁ VÝZTUŽ PROCHÁZející PRACOVNÍ SPÁROU BUDE OPATŘENA OCHRANNÝM EPOX. NÁTĚREM VE VZDÁLENOSTI  $\pm 100\text{mm}$  NA KAŽDOU STRANU OD PRACOVNÍ SPÁRY.
- VEŠKERÁ VÝZTUŽ JE VÁZANÁ. PROVAŘENÍ VÝZTUŽE KVŮLI BLUDNÝM PROUDŮM BUDE PROVEDENO DLE TP 124
- KRYTÍ VÝZTUŽE JE UVAŽOVÁNO NA SPONY.

PŘEDPISY PRO PROVEDENÍ JEDNOTLIVÝCH KONSTRUKČNÍ ČÁSTÍ:

- TKP KAP 18 - BETONOVÉ KONSTRUKCE A MOSTY
- ČSN EN 206+A2 - BETON - SPECIFIKACE, VLASTNOSTI, VÝROBA A SHODA
- TP 124 - ZÁKLADNÍ OCHRANNÁ OPATŘENÍ PRO OMEZENÍ VLIVU BLUDNÝCH PROUDŮ NA MOSTNÍ OBJEKTY A OSTATNÍ BETONOVÉ KONSTRUKCE POZEMNÍCH KOMUNIKACÍ
- TP 193 - SVAŘOVÁNÍ BETONÁŘSKÉ VÝZTUŽE A JINÉ DRUHY SPOJŮ ČSN EN ISO 17660-2  
SVAŘOVÁNÍ - SVAŘOVÁNÍ BETONÁŘSKÉ OCELI ČÁST 2: NENOSNÉ SVAŘOVÉ SPOJE

KRYTÍ VÝZTUŽE

ZÁKLADY: MINIMÁLNÍ 50 mm, JMENOVITĚ 60 mm  
DRŽKY, KŘÍDLA: MINIMÁLNÍ 45 mm, JMENOVITĚ 55 mm

= ROZMĚRY OHÝBANÝCH VLOŽEK JSOU ROZMĚRY NA VNĚJŠÍ POVRCH  
= ZAKŘIVENÍ VLOŽEK JSOU UDÁVÁNA POLOMĚREM OHÝBACÍHO TRNU  
= POKUD NENÍ NA VÝKRESE UVEDENO JINAK, JE UVAŽOVÁN

VÝKAZ VÝZTUŽE - OPĚRY O1 + O4 VČETNĚ ZÁKLADŮ

| průměr<br>mm         | průměr<br>mm | délka<br>m | počet<br>ks | DĚLKA DLE PROFILU |             |             |             |             |             |             |             |             |             |             |          |
|----------------------|--------------|------------|-------------|-------------------|-------------|-------------|-------------|-------------|-------------|-------------|-------------|-------------|-------------|-------------|----------|
|                      |              |            |             | 8<br>B500B        | 10<br>B500B | 12<br>B500B | 14<br>B500B | 16<br>B500B | 18<br>B500B | 20<br>B500B | 22<br>B500B | 25<br>B500B | 28<br>B500B | 32<br>B500B |          |
| 8                    | 8            | 2392,55    | 1           | 2392,6            |             |             |             |             |             |             |             |             |             |             |          |
| 10                   | 10           | 0,00       | 1           |                   | 0,0         |             |             |             |             |             |             |             |             |             |          |
| 12                   | 12           | 9570,20    | 1           |                   |             | 9570,2      |             |             |             |             |             |             |             |             |          |
| 14                   | 14           | 0,00       | 1           |                   |             |             | 0,0         |             |             |             |             |             |             |             |          |
| 16                   | 16           | 16747,85   | 1           |                   |             |             |             | 16747,9     |             |             |             |             |             |             |          |
| 18                   | 18           | 0,00       | 1           |                   |             |             |             |             | 0,0         |             |             |             |             |             |          |
| 20                   | 20           | 10527,22   | 1           |                   |             |             |             |             |             | 10527,2     |             |             |             |             |          |
| 22                   | 22           | 0,00       | 1           |                   |             |             |             |             |             |             | 0,0         |             |             |             |          |
| 25                   | 25           | 11005,73   | 1           |                   |             |             |             |             |             |             |             | 11005,7     |             |             |          |
| 28                   | 28           | 0,00       | 1           |                   |             |             |             |             |             |             |             |             | 0,0         |             |          |
| 32                   | 32           | 0,00       | 1           |                   |             |             |             |             |             |             |             |             |             |             | 0,0      |
| Hm. 1 bm             |              |            | [kg/m]      | 0,395             | 0,617       | 0,888       | 1,209       | 1,579       | 1,998       | 2,467       | 2,985       | 3,854       | 4,834       | 6,314       |          |
| Hm. prof.            |              |            | [kg]        | 945,1             | 0,0         | 8498,3      | 0,0         | 26444,9     | 0,0         | 25970,7     | 0,0         | 42416,1     | 0,0         | 0,0         |          |
| HMOTNOST CELKEM (kg) |              |            |             |                   |             |             |             |             |             |             |             |             |             |             | 104275,0 |

VÝKAZ VÝZTUŽE - PŘECHODOVÉ DESKY O1 + O4

| průměr<br>mm         | průměr<br>mm | délka<br>m | počet<br>ks | DĚLKA DLE PROFILU |             |             |             |             |             |             |             |             |             |             |         |
|----------------------|--------------|------------|-------------|-------------------|-------------|-------------|-------------|-------------|-------------|-------------|-------------|-------------|-------------|-------------|---------|
|                      |              |            |             | 8<br>B500B        | 10<br>B500B | 12<br>B500B | 14<br>B500B | 16<br>B500B | 18<br>B500B | 20<br>B500B | 22<br>B500B | 25<br>B500B | 28<br>B500B | 32<br>B500B |         |
| 8                    | 8            | 912,08     | 1           | 912,1             | 0,0         | 4788,4      | 3420,3      | 2280,2      | 0,0         | 0,0         | 0,0         | 0,0         | 0,0         | 0,0         | 0,0     |
| 10                   | 10           | 0,00       | 1           |                   |             |             |             |             |             |             |             |             |             |             |         |
| 12                   | 12           | 4788,42    | 1           |                   |             |             |             |             |             |             |             |             |             |             |         |
| 14                   | 14           | 3420,30    | 1           |                   |             |             |             |             |             |             |             |             |             |             |         |
| 16                   | 16           | 2280,20    | 1           |                   |             |             |             |             |             |             |             |             |             |             |         |
| 18                   | 18           | 0,00       | 1           |                   |             |             |             |             |             |             |             |             |             |             |         |
| 20                   | 20           | 0,00       | 1           |                   |             |             |             |             |             |             |             |             |             |             |         |
|                      |              |            | [m]         | 912,1             | 0,0         | 4788,4      | 3420,3      | 2280,2      | 0,0         | 0,0         | 0,0         | 0,0         | 0,0         | 0,0         | 0,0     |
| Hm. 1 bm             |              |            | [kg/m]      | 0,395             | 0,617       | 0,888       | 1,209       | 1,579       | 1,998       | 2,467       | 2,985       | 3,854       | 4,834       | 6,314       | 0,0     |
| Hm. prof.            |              |            | [kg]        | 360,3             | 0,0         | 4252,1      | 4135,1      | 3600,4      | 0,0         | 0,0         | 0,0         | 0,0         | 0,0         | 0,0         | 0,0     |
| HMOTNOST CELKEM (kg) |              |            |             |                   |             |             |             |             |             |             |             |             |             |             | 12348,0 |

ZAKRESLENA OPĚRA O1, OPĚRA O4 ANALOGICKY

ČÁST D.2  
SO 202

Souřadnicový systém S-JTSK, Výškový systém Bpv



ŘEDITELSTVÍ  
SILNIC  
A DÁLNIC

ČISTOPIS

ŘEDITELSTVÍ SILNIC A DÁLNIC s. p.  
Čerčanská 2023/12  
140 00 Praha 4 – Krč

|   |                                                                            |                                                                                               |  |                                                                                     |
|---|----------------------------------------------------------------------------|-----------------------------------------------------------------------------------------------|--|-------------------------------------------------------------------------------------|
| Zhotovitel PD: PRAGOPROJEKT, a.s., K Rysánci 1668/16, 147 54 Praha 4, IČO: 45272387, www.pragoprojekt.cz, datová schránka: 4kif54 |                                                                            |                                                                                               |  |  |
| Návrh/ vypracoval:<br>Ing. Karolína Hédová<br>podpis: <i>K. Hédová</i>                                                            | Zodpovědný projektant:<br>Ing. Martin BLATSKÝ<br>podpis: <i>M. Blatský</i> | Zástupce zodpovědného projektanta:<br>Ing. Jan BAZIL<br>podpis: <i>J. Bazil</i>               |  |                                                                                     |
| Technická kontrola:<br>Ing. Kamil PEJCHAL<br>podpis: <i>K. Pejchal</i>                                                            | Hlavní inženýr projektu:<br>Ing. Pavel ŠLAPA<br>podpis: <i>P. Šlapa</i>    | Zástupce hlavního inženýra projektu:<br>Ing. Radovan STANKOVEN<br>podpis: <i>R. Stankoven</i> |  |                                                                                     |
|   |                                                                            |                                                                                               |  |                                                                                     |

|                                                                             |                         |
|-----------------------------------------------------------------------------|-------------------------|
| Kraj: KARLOVARSKÝ KRAJ                                                      | Číslo zakázky: 25-150-2 |
| Místo stavby: OLŠOVÁ VRATA, ANDĚLSKÁ HORA, ŽALMANOV, HORNÍ TAŠOVICE, BOCHOV | Číslo akce: 05-219      |
| Objednatel: ŘSD s. p., Čerčanská 2023/12, 140 00 Praha 4, IČO 65993390      | Datum: 03/2026          |
| Název stavby: D6 OLŠOVÁ VRATA-ŽALMANOV, VD-ZDS                              | Formát: PDPS            |
| Objekt: Most na D6 přes Lomnický potok v km 1,600                           | Stupeň: Souprava:       |
| Příloha: SCHÉMA VÝZTUŽE OPĚRY O1, O2                                        | Číslo přílohy: 10       |