ŘEZ A–A 1:50

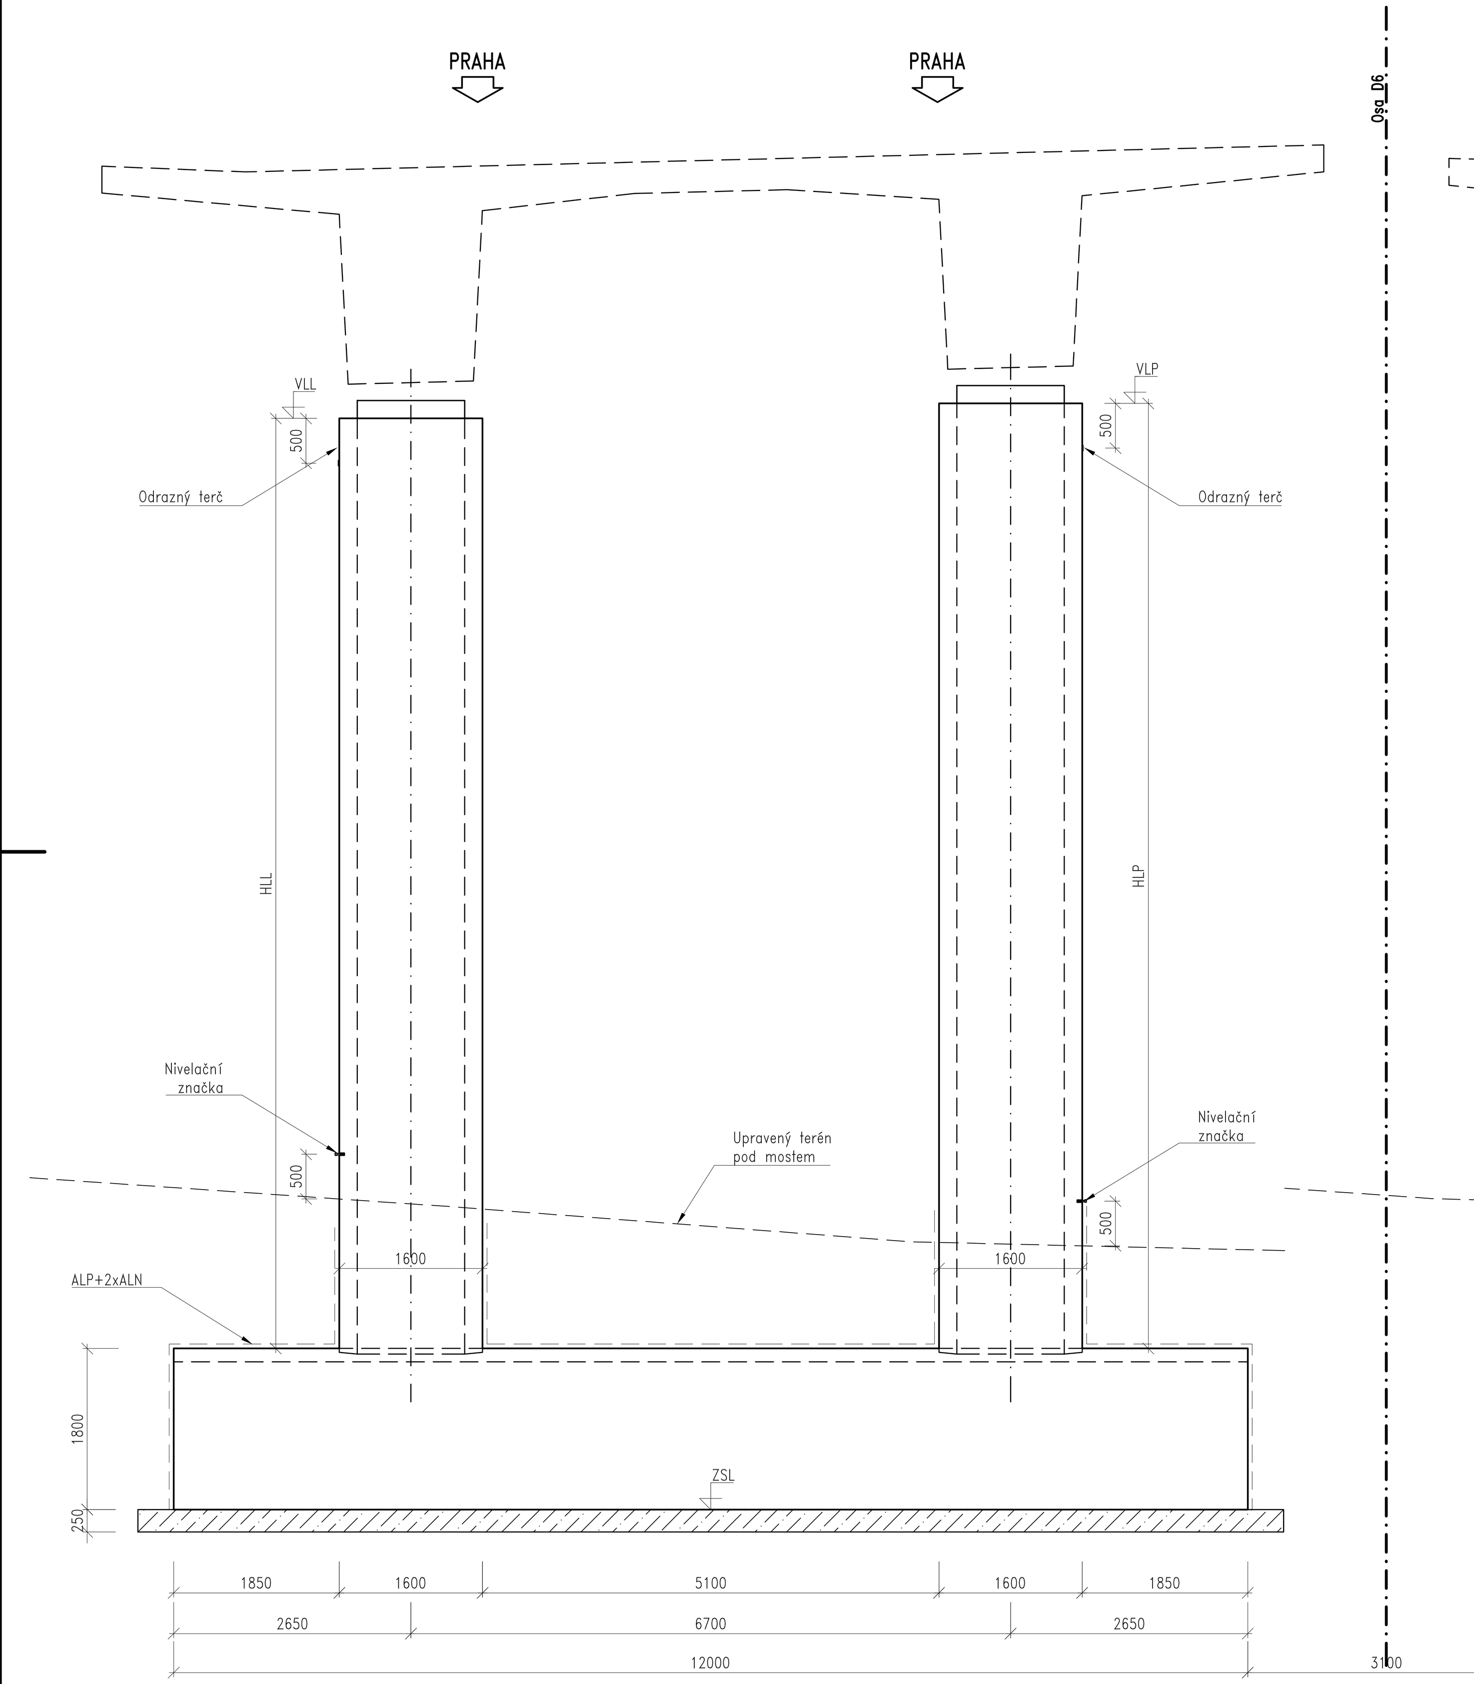

ŘEZ B–B 1:50

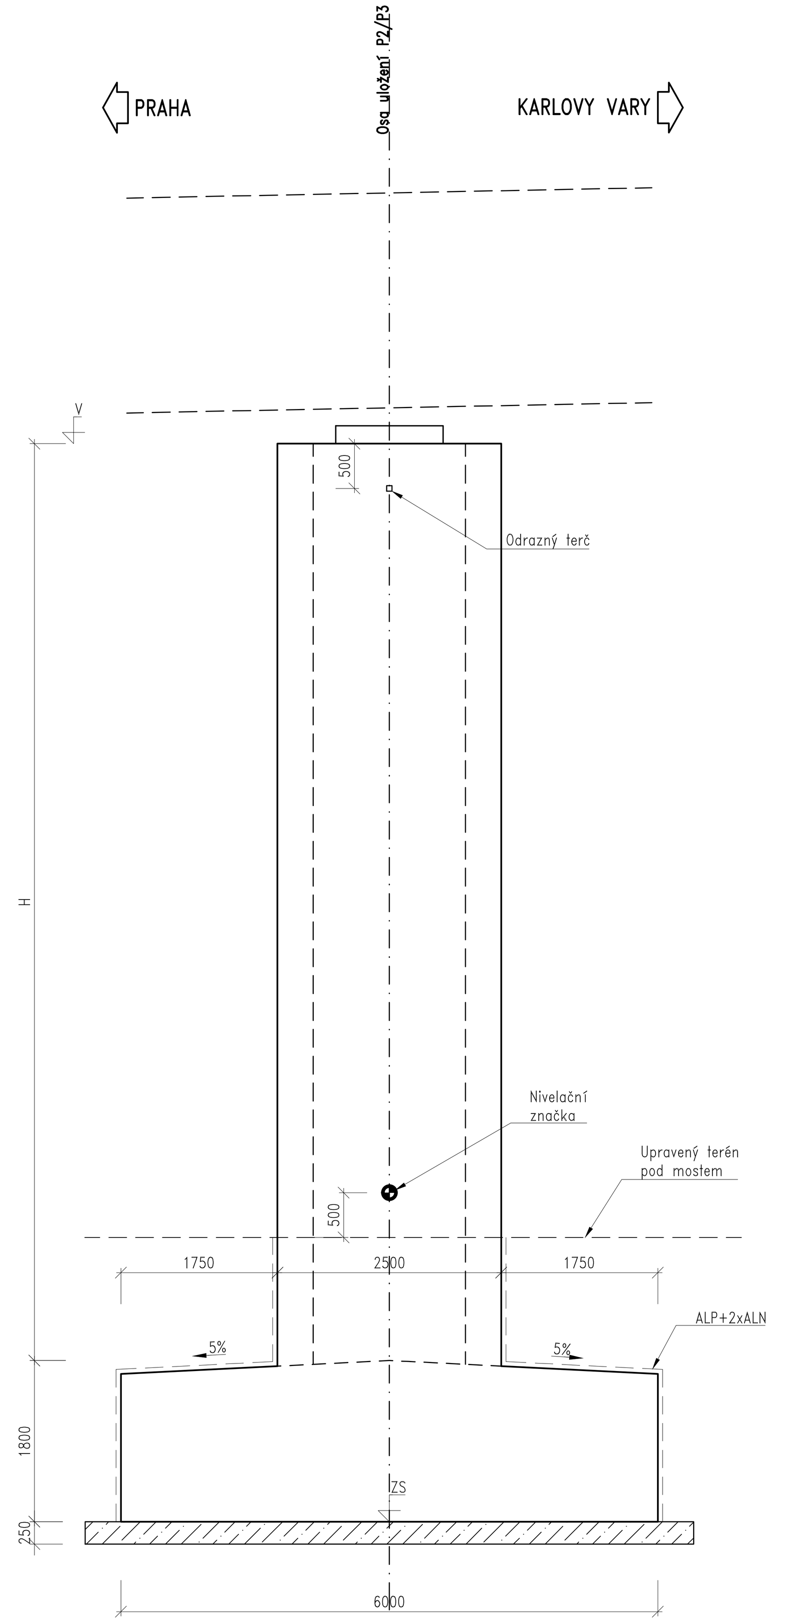

PŮDORYS 1:50

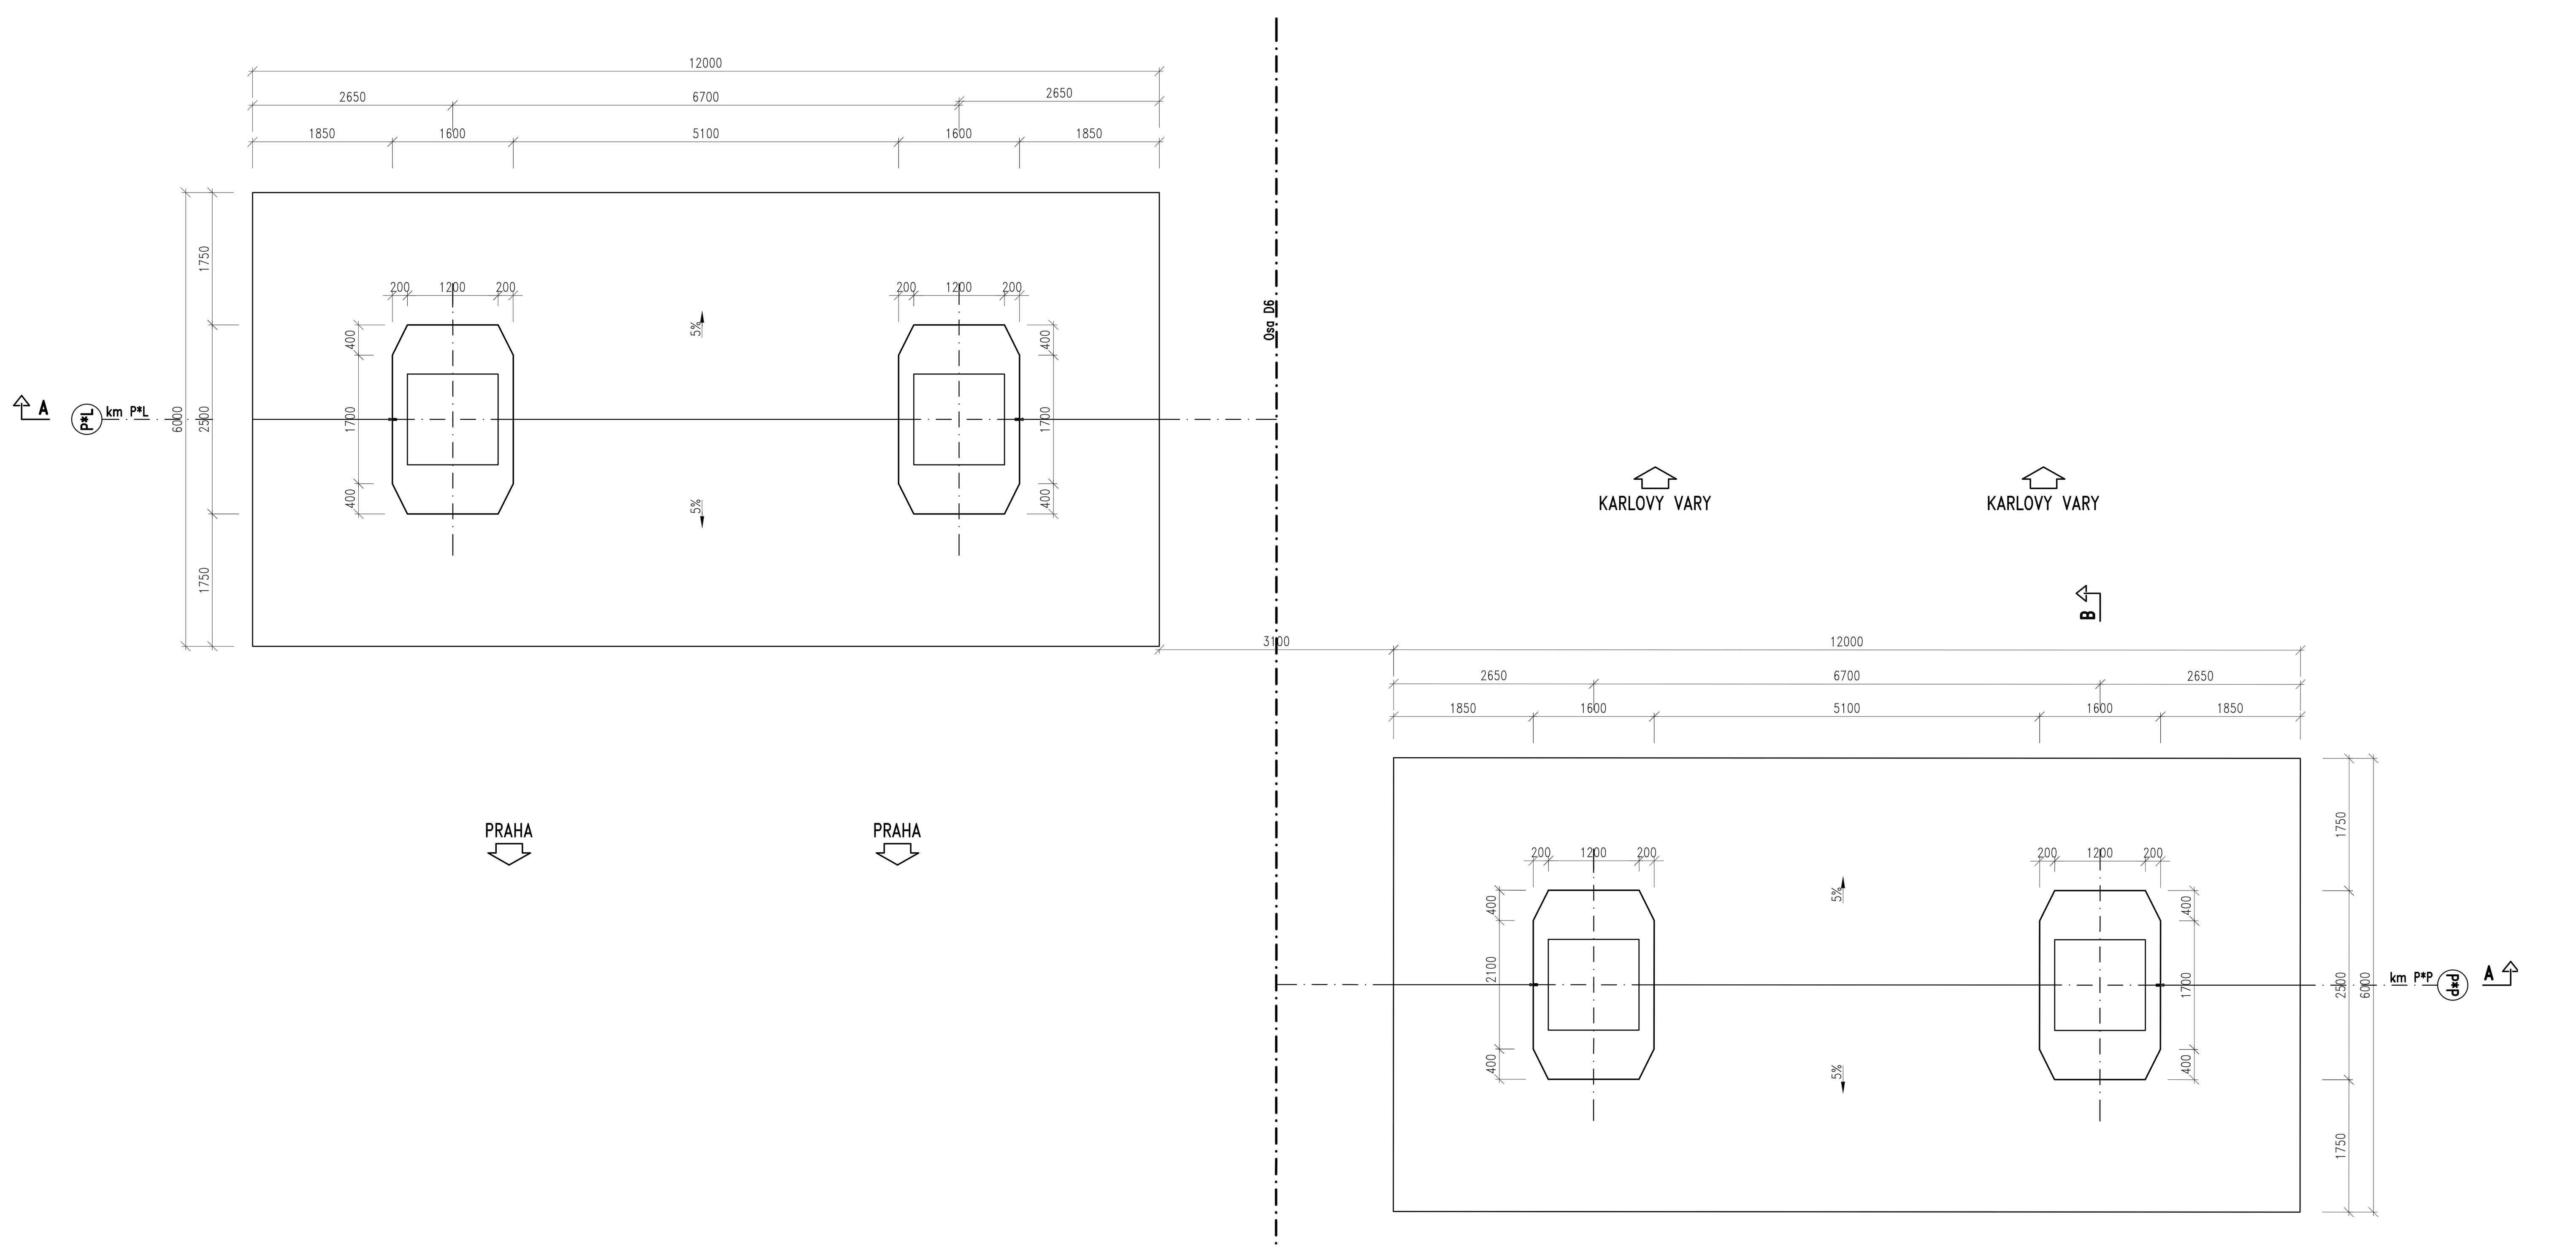

POZNÁMKA:

P2L	Staničení	HZSL	VLL	VLP	HLL	HLP
	1,622489	664,000	676,240	676,400	10440	10600
P2P	Staničení	HZSP	VPL	VPP	HPL	HPP
	1,615016	664,000	676,250	676,090	10450	10290
P3L	Staničení	HZSL	VLL	VLP	HLL	HLP
	1,667000	662,500	677,240	677,400	12940	13100
P3P	Staničení	HZSP	VPL	VPP	HPL	HPP
	1,659500	662,500	677,230	677,060	12930	12760

MATERIÁLY :

BETON (TKP 18, ČSN EN 206+A2):
PODKLADNÍ BETON C25–30–XA2
ZÁKLADY C30/37–XC2+XF1+XA2
PILÍŘE C35/45–XC4+XF1+XD1

KATEGORIE POVRCH. ÚPRAVY:

POHLEDOVÉ PLOCHY C2d
ostatní plochy C1a

Všechny plochy v trvalém kontaktu se zeminou budou opatřeny nátěry proti zemní vlhkosti ALP+2xALN

ČÁST D.2
SO 202

ČISTOPIS
Souřadnicový systém S–JTSK, Výškový systém Bpv

Objednatel:
ŘEDITELSTVÍ SILNIC A DÁLNIC
ŘEDITELSTVÍ SILNIC A DÁLNIC s. p.
Čerčanská 2023/12
140 00 Praha 4 – Krč

Zhotovitel PD: PRAGOPROJEKT, a.s., K Ryšánce 1668/16, 147 54 Praha 4, IČO: 45272387, www.pragoprojekt.cz, datová schránka: 4kifr54

Navrhl/vypracoval: Ing. Karolína Hédová, podpis:	Zodpovědný projektant: Ing. Martin BLATSKÝ, podpis:	Zástupce zodpovědného projektanta: Ing. Jan BAŽIL, podpis:
Technická kontrola: Ing. Kamil PEJCHAL, podpis:	Hlavní inženýr projektu: Ing. Pavel ŠLAPA, podpis:	Zástupce hlavního inženýra projektu: Ing. Radovan STANKOVEN, podpis:

PRAGOPROJEKT

Kraj:	KARLOVARSKÝ KRAJ	Číslo zakázky:	25–150–2
Místo stavby:	OLŠOVÁ VRATA, ANDĚLSKÁ HORA, ŽALMANOV, HORNÍ TAŠOVICE, BOCHOV	Číslo akce:	05–219
Objednatel:	ŘSD s. p., Čerčanská 2023/12, 140 00 Praha 4, IČO 65993390	Datum:	03/2026
Název stavby:	D6 OLŠOVÁ VRATA-ŽALMANOV, VD-ZDS	Formát:	
		Měřítko:	
Objekt:	MOST NA D6 PŘES LOMNICKÝ POTOK V km 1,600 S0101	Stupeň:	PDPS
		Souprava:	
Příloha:	TVAR PILÍŘŮ	Číslo přílohy:	11