



PŮDORYS 1:50

K. VARY

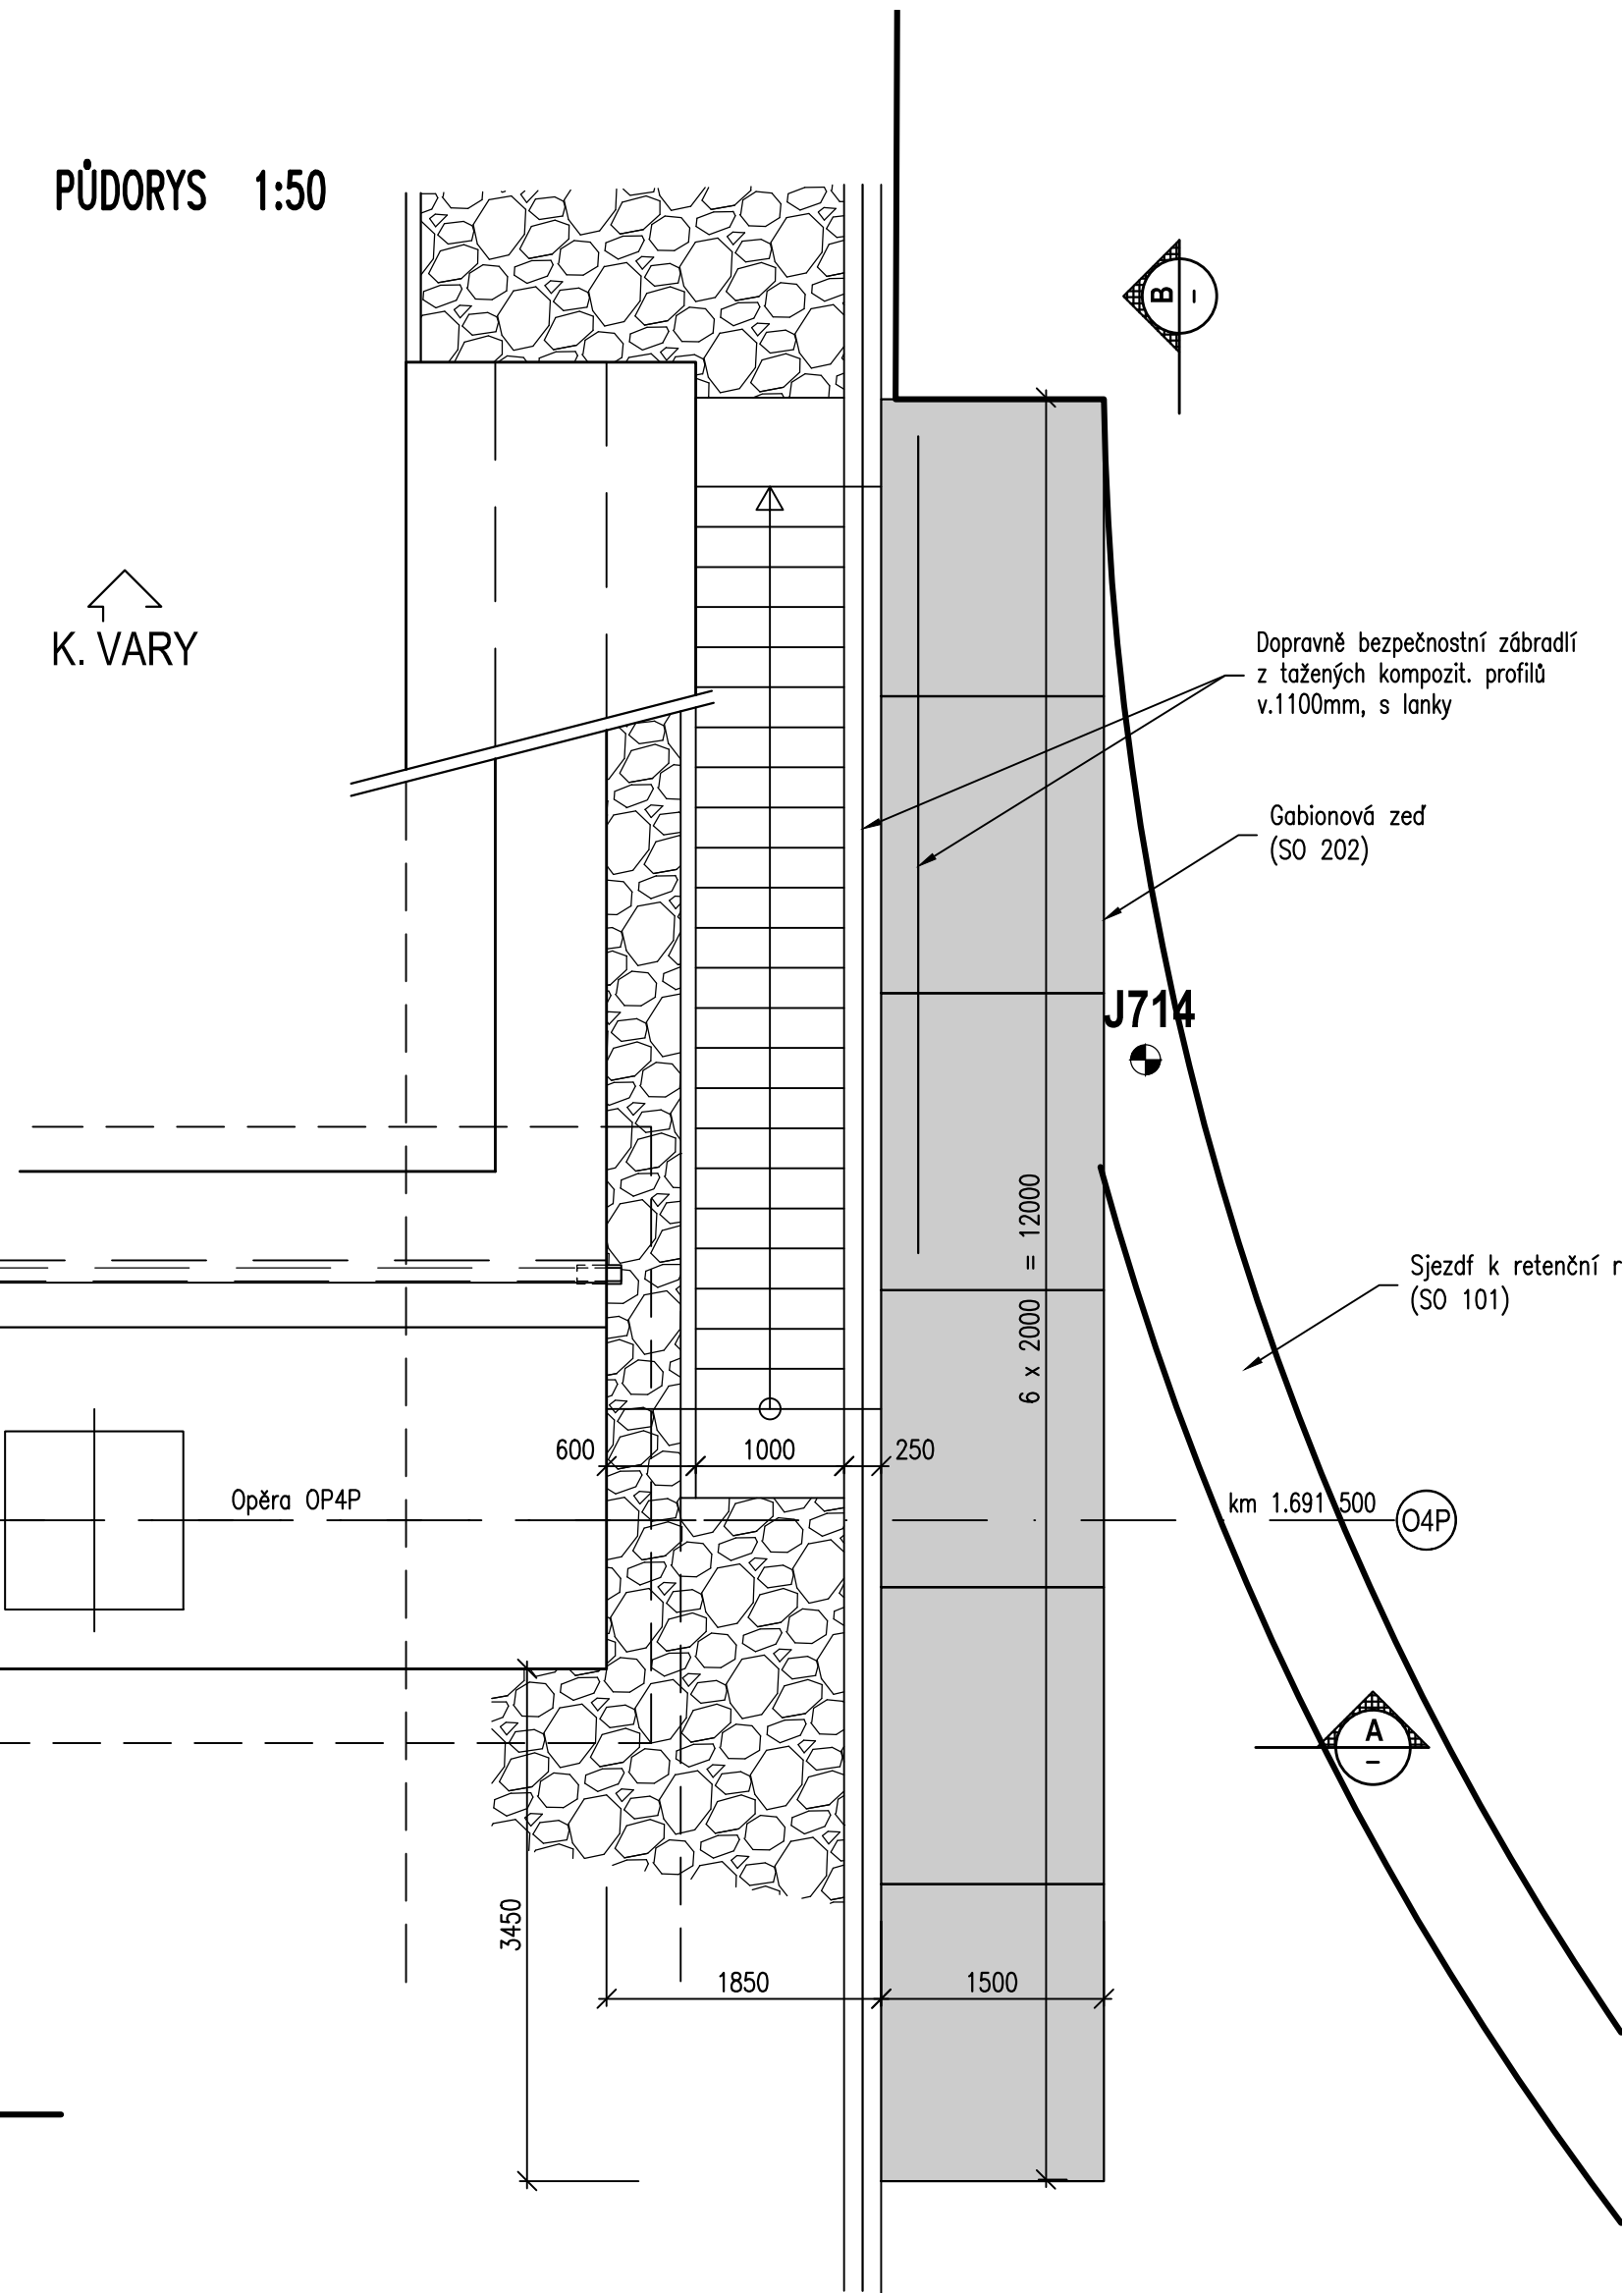


ŘEZ A 1:50

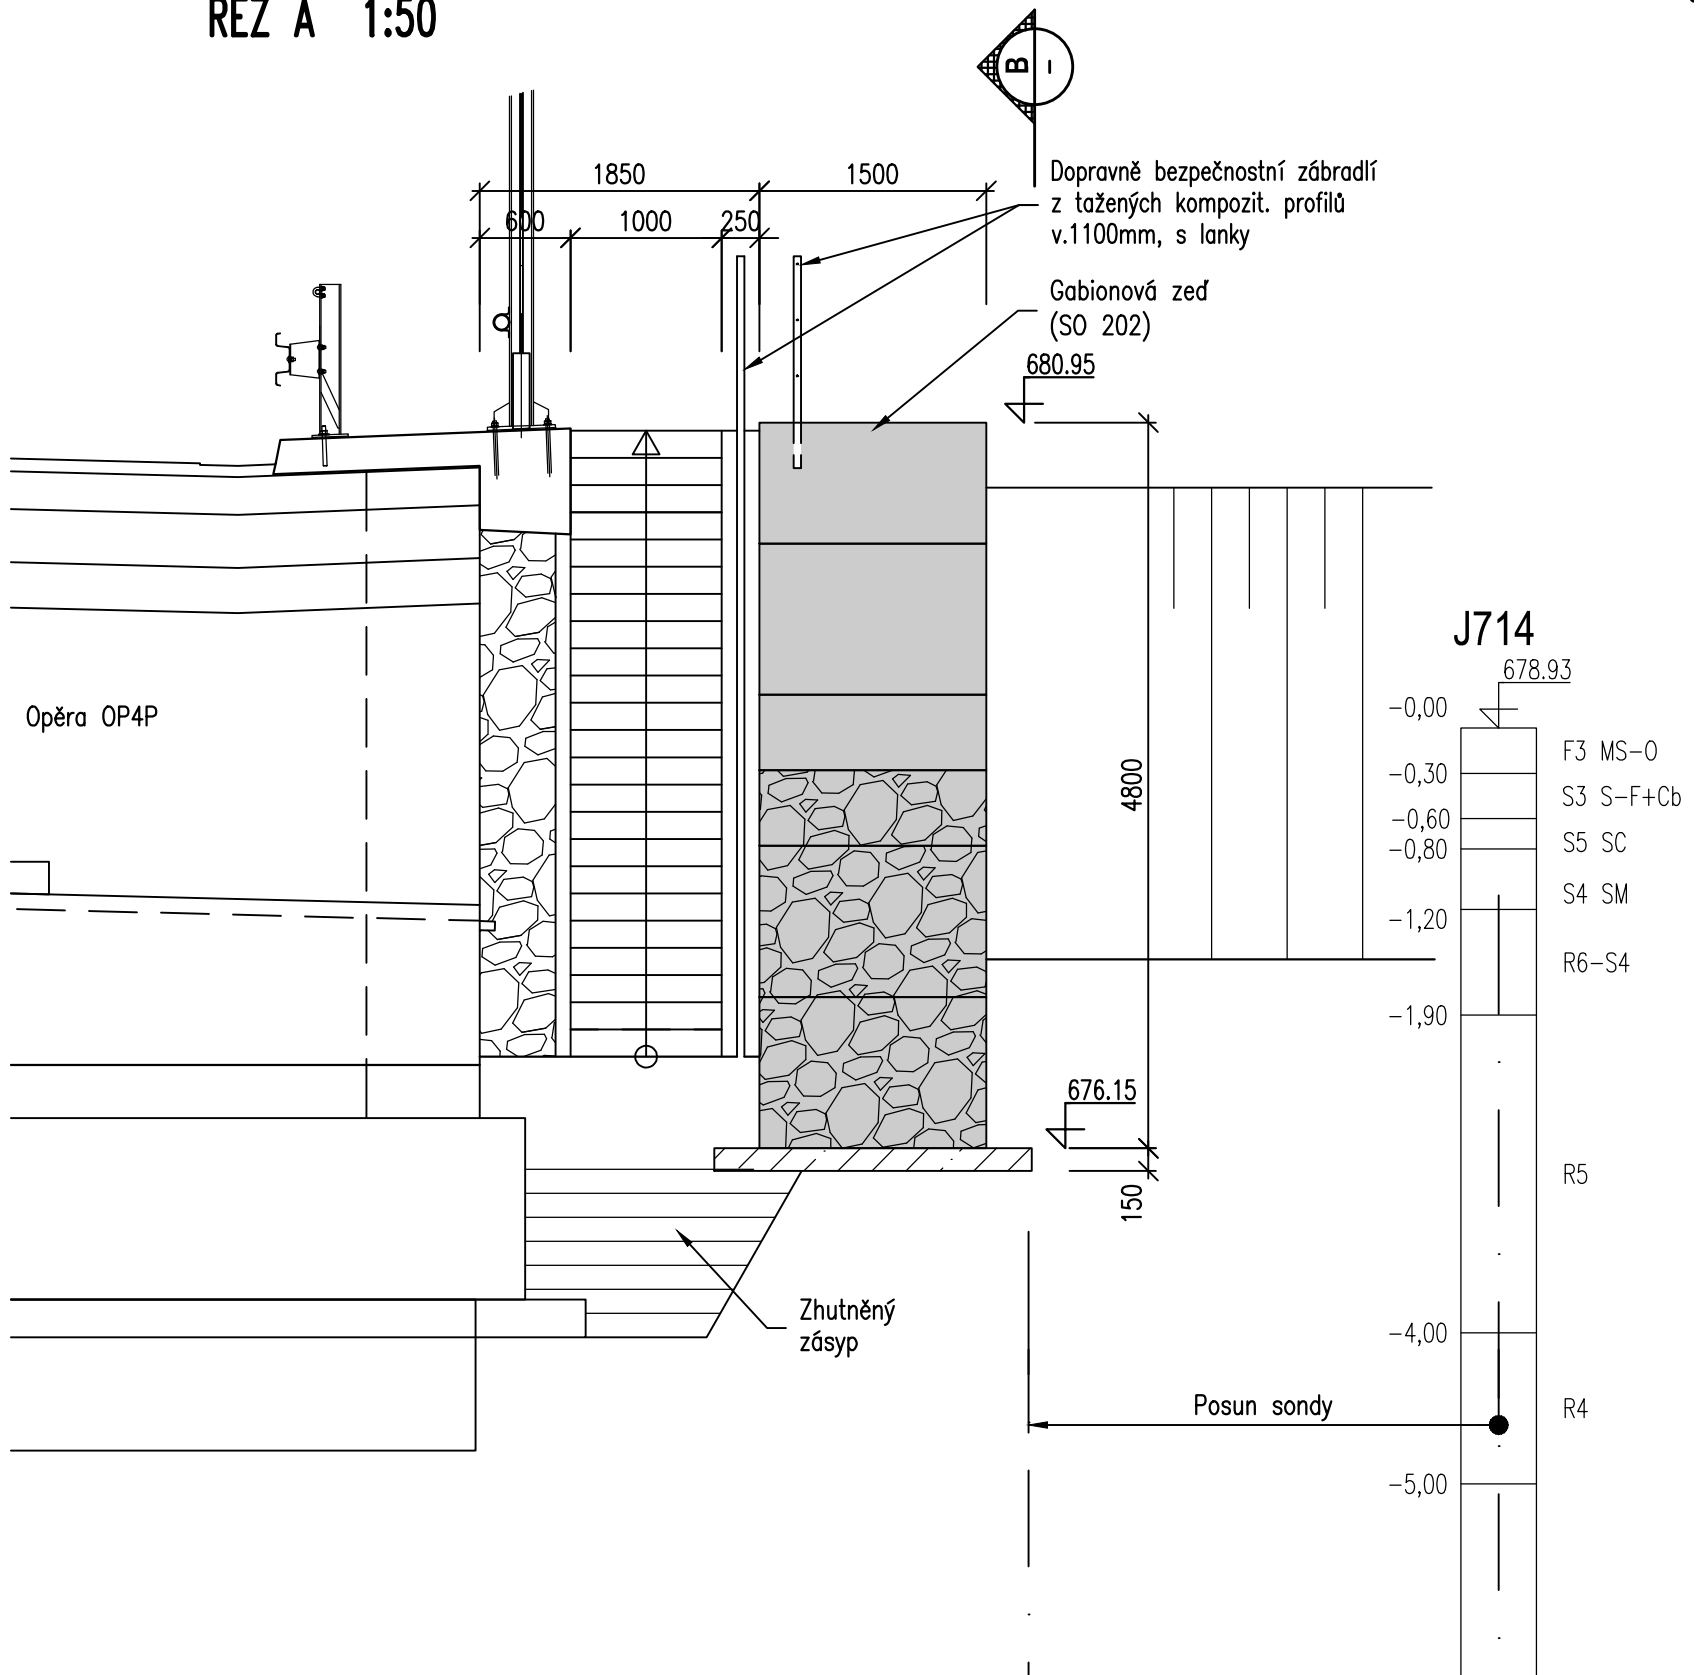


PŘÍČNÝ ŘEZ ÚNIKOVÝM SCHODIŠTĚM 1:25

U 04


V MÍSTĚ NEJNIŽŠÍHO GABIONU, STANIČENÍ 1,687050

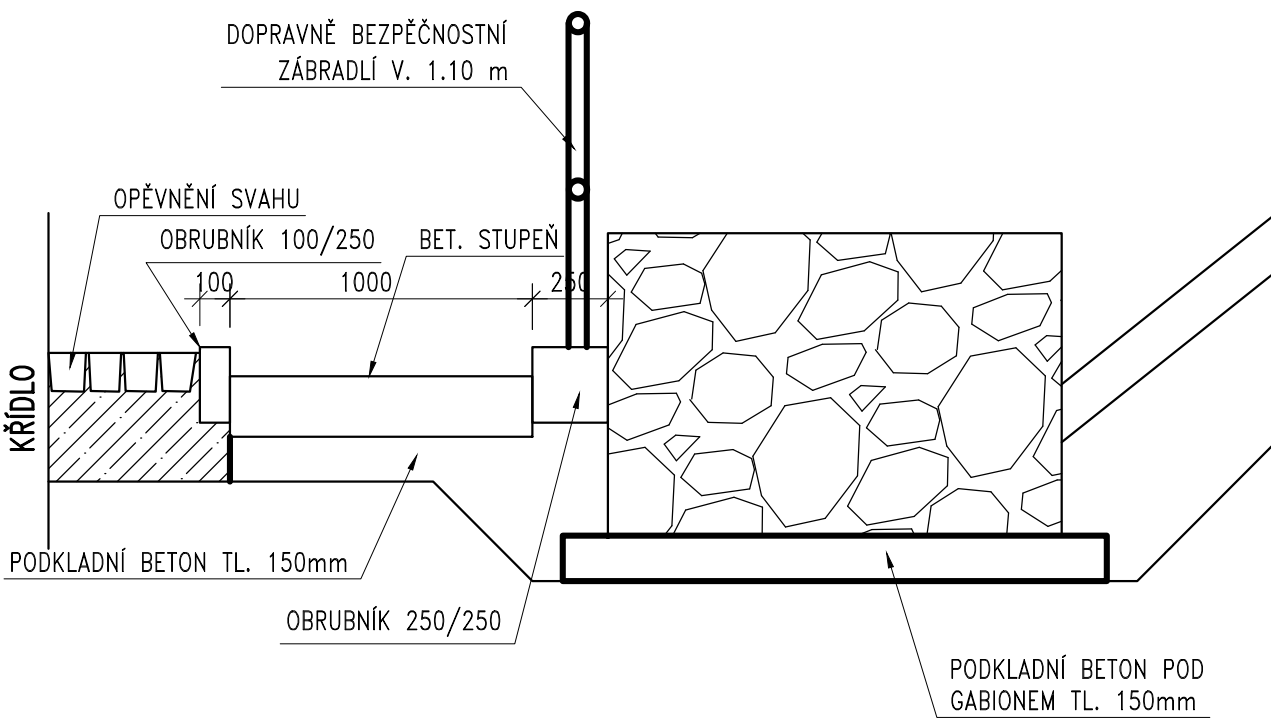

ŘEZ C 1:50

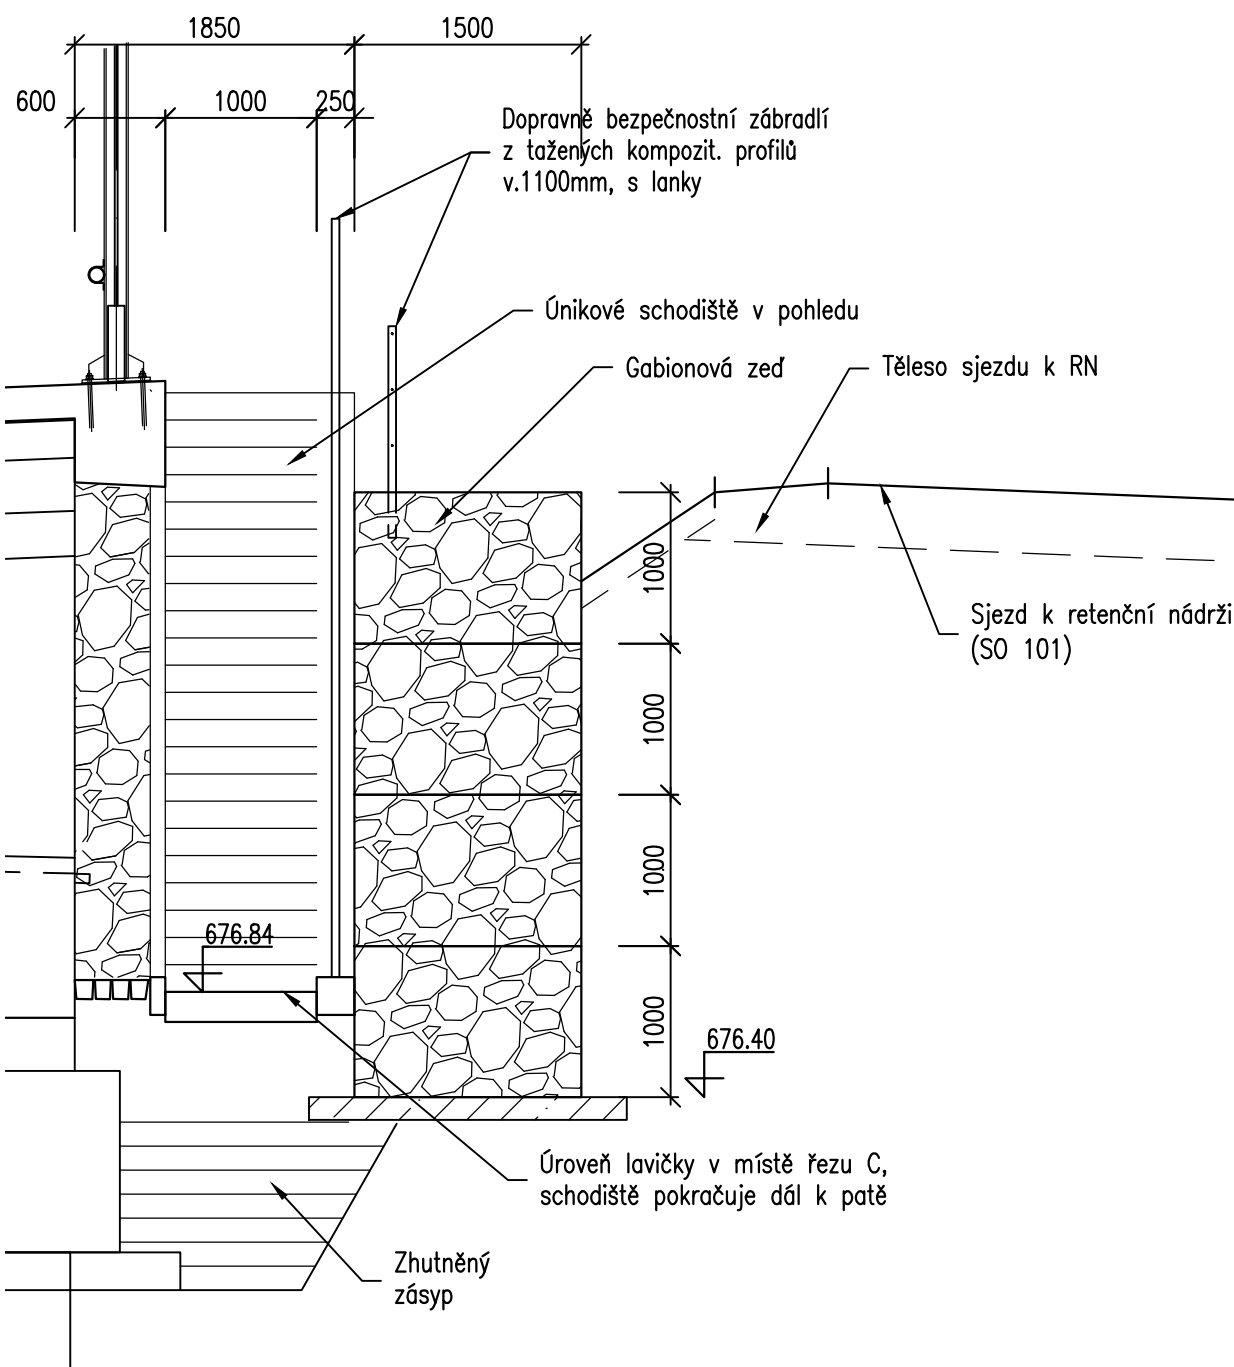

POHLED B 1:50

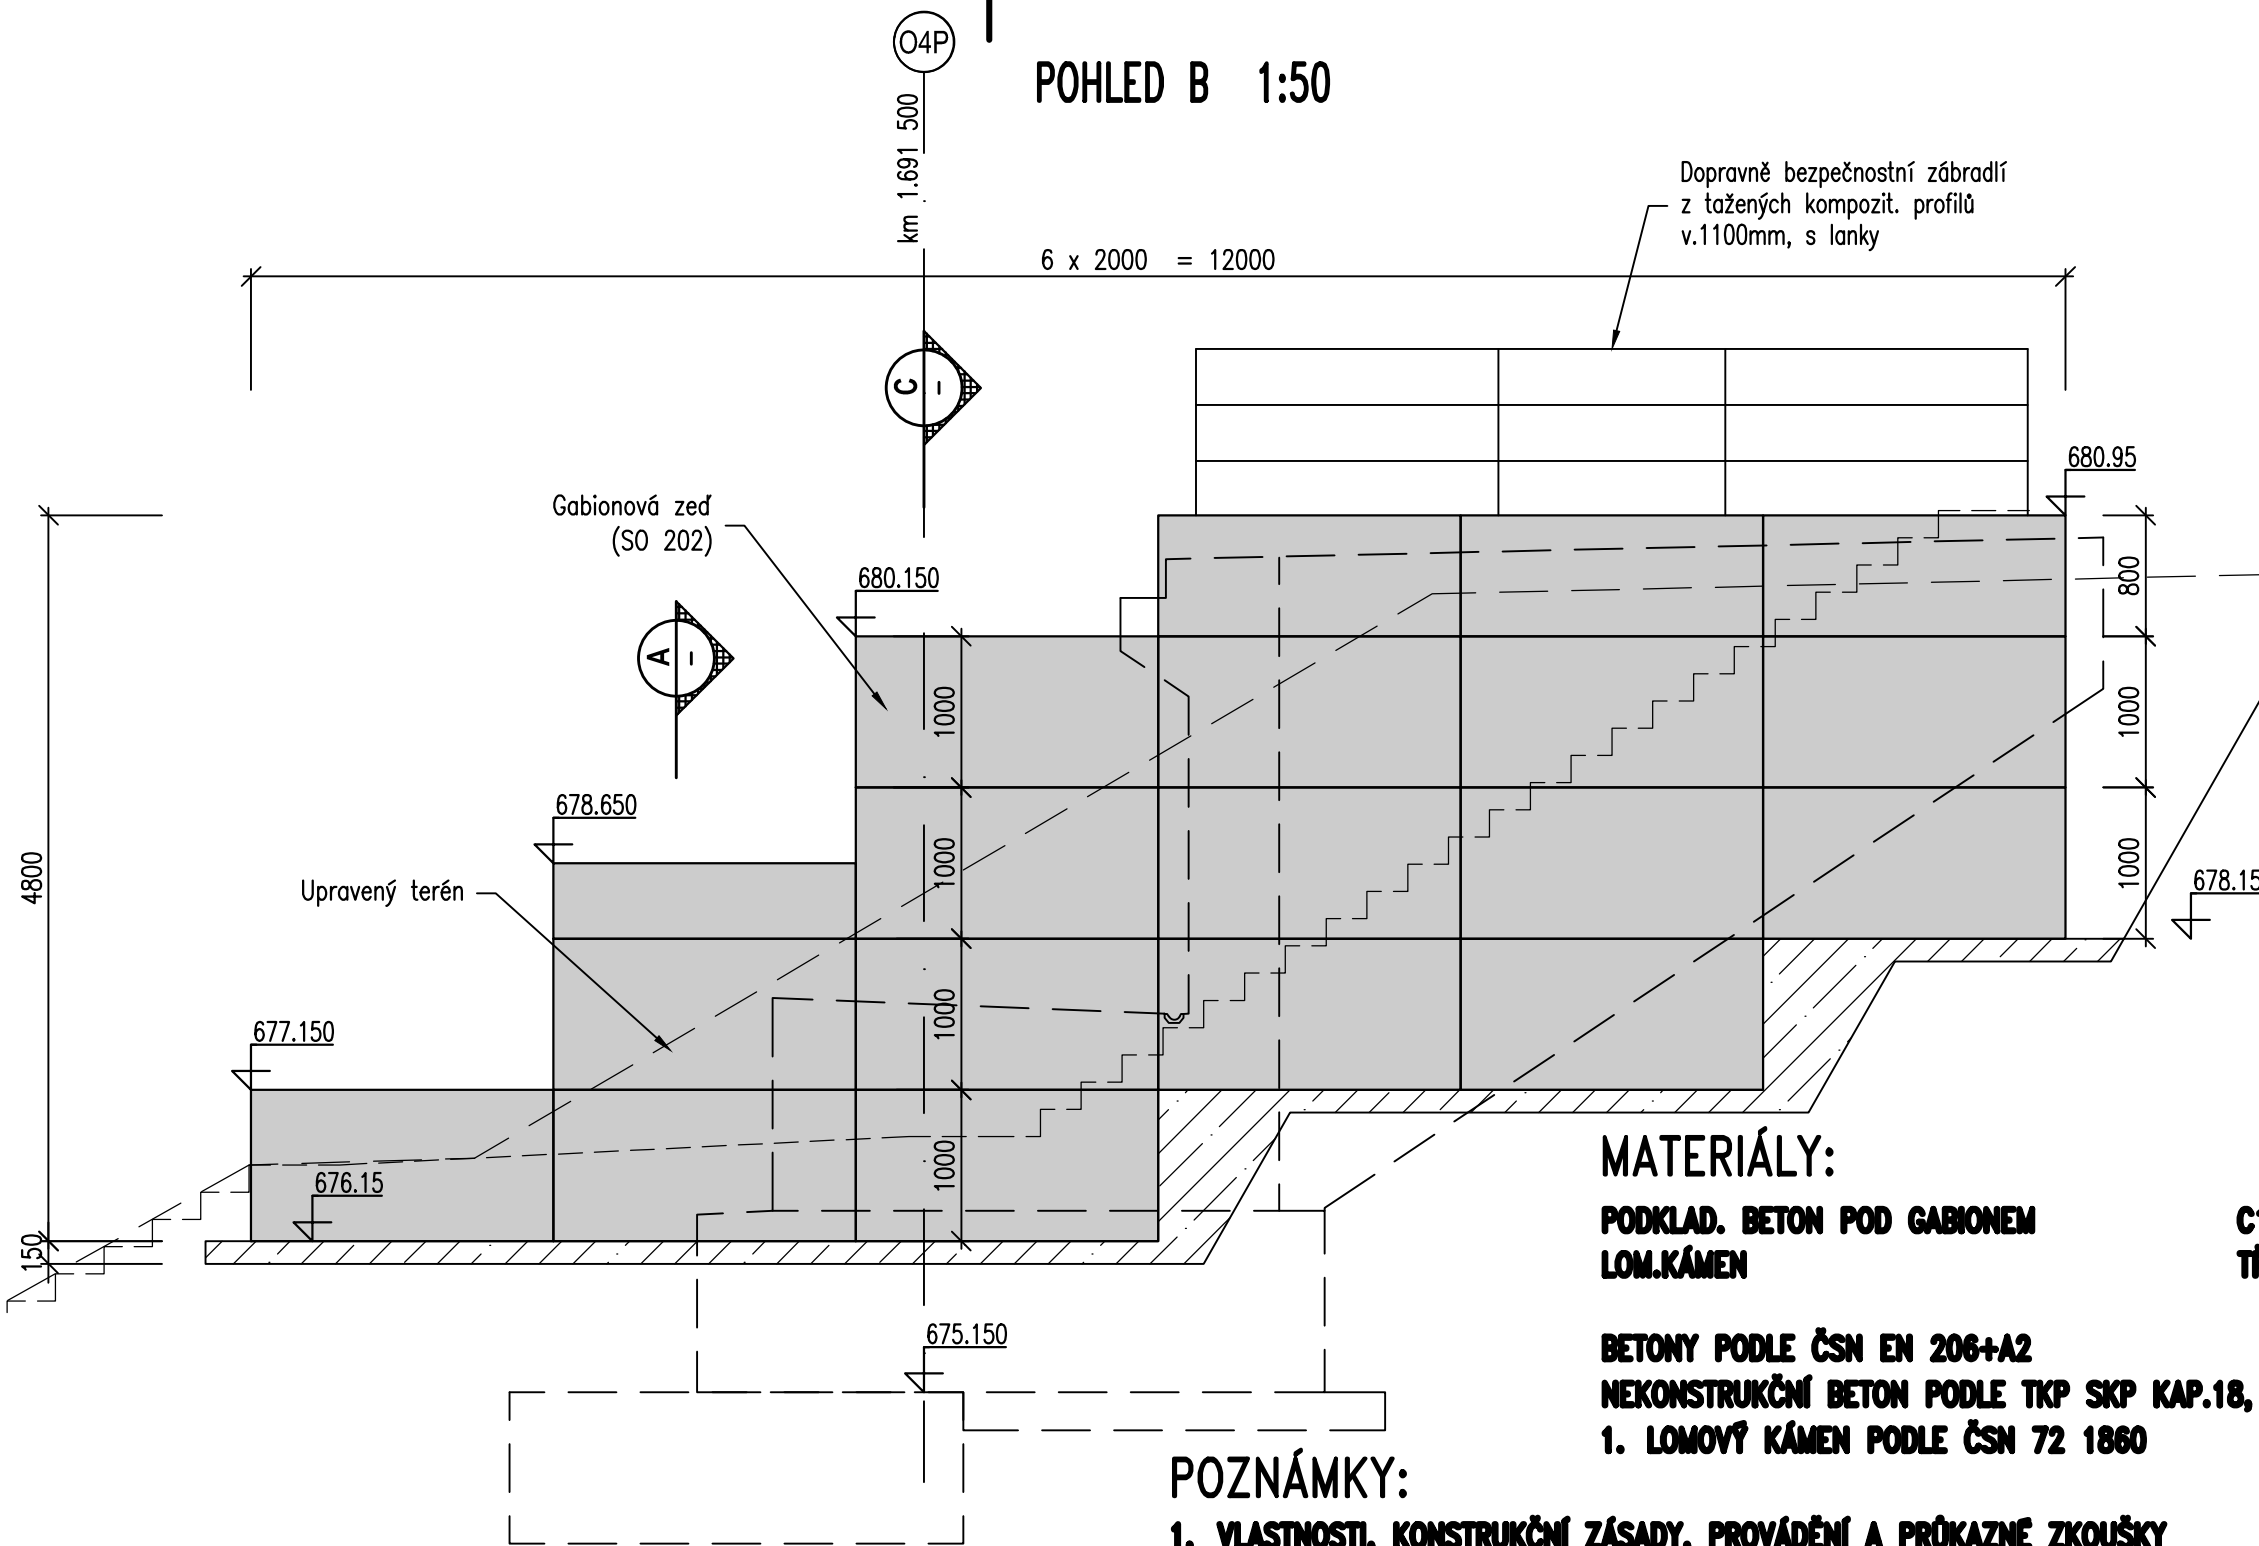

MATERIÁLY:

PODKLAD. BETON POD GABIONEM
LOM.KÁMEN

C12/15-X0
TRÍDA JAKOSTI "I"

BETONY PODLE ČSN EN 206+A2
NEKONSTRUKČNÍ BETON PODLE TKP SKP KAP.18, TAB. 18-2N
1. LOMOVÝ KÁMEN PODLE ČSN 72 1860

POZNÁMKY:

- VLASTNOSTI, KONSTRUKČNÍ ZÁSADY, PROVÁDĚNÍ A PRŮKAZNÉ ZKOUŠKY MATERIÁLŮ MUSÍ BÝT V SOULADU S TKP 30.
- GABIONY BUDOU ZE SVAŘOVANÉ SÍTĚ S OKY 100x100mm. TL. DRÁTU 4mm, POVRCHOVÁ ÚPRAVA ZnAL. PEVNOST SÍTĚ MIN. 40kN/m.
- VÝPLŇOVÝ KÁMEN BUDE ODOLNÝ VŮČI POVĚTRNOSTNÍM VLIVŮM, NEŠTĚPIVÝ A DOSTATEČNĚ TVRÝ. NA RUBU GABIONU BUDE POUŽITO KAMENIVO FRAKCE 32-63, PŘÍP. 63-125. DO POHLEDOVÉ STRANY BUDE POUŽIT LOMOVÝ KÁMEN VELIKOSTI 1.5-2 NÁSOBKU OKATOSTI SÍTĚ.
- POSLEDNÍ ŘADA KOŠŮ BUDE PO ZAVÍKOVÁNÍ DOSYPÁNA DROBNĚJŠÍM KAMENIVEM.
- RUB GABIONŮ BUDE OPATŘEN NETKANOU SEPARAČNĚ FILTRAČNÍ GEOTEXTILIÍ. ODOLNOST PROTI PROTRŽENÍ (CBR) MIN. 2,5kN, PLOŠNÁ HMOTNOST MIN. 400g/m².
- ZÁSYP OPĚRNÉ ZDI SE PROVEDE ZE ZEMIN VHODNÝCH NEBO PODMÍNEČNĚ VHODNÝCH DO NÁSYPU DLE ČSN 73 6133 S HUTNĚNÍM PO VRSTVÁCH TL. MAX. 300 mm NA ID=0.85 AŽ 0.90, RESP. D=100%PS

ČÁST D.2 SO 202

Souřadnicový systém S-JTSK, Výškový systém Bpv

ČISTOPIS

Objednatel:



ŘEDITELSTVÍ
SILNIC
A DÁLNIC

ŘEDITELSTVÍ SILNIC A DÁLNIC s. p.
Čerčanská 2023/12
140 00 Praha 4 – Krč

Zhotovitel PD: PRAGOPROJEKT, a.s., K Ryšánci 1668/16, 147 54 Praha 4, IČO: 45272387, www.pragoprojekt.cz, datová schránka: 4kfr54		
Navrh/vypracoval: Ing. Karolína HEDGÁVÁ podpis: <i>K. Hedgá</i>	Zodpovědný projektant: Ing. Martin BLATSKÝ podpis: <i>M. Blatský</i>	Zástupce zodpovědného projektanta: Ing. Jan BAZIL podpis: <i>J. Bazil</i>
Technická kontrola: Ing. Kamil PEJCHAL podpis: <i>K. Pejchal</i>	Hlavní inženýr projektu: Ing. Pavel SLAPÁ podpis: <i>P. Slapá</i>	Zástupce hlavního inženýra projektu: Ing. Radovan STANKOVEN podpis: <i>R. Stankoven</i>



PRAGOPROJEKT

Kraj:	KARLOVARSKÝ KRAJ	Číslo zakázky:	25-150-2
Místo stavby:	OLŠOVÁ VRATA, ANDELSKÁ HORA, ŽALMANOV, HORNÍ TAŠOVICE, BOCHOV	Číslo akce:	05-219
Objednatel:	RSD s. p., Čerčanská 2023/12, 140 00 Praha 4, IČO 65993390	Datum:	03/2026
Název stavby:	D6 OLŠOVÁ VRATA-ŽALMANOV, VD-ZDS		
Objekt:	Most na D6 přes Lomnický potok v km 1,600 SO 101	Formát:	
Příloha:	GABIONOVÁ ZEĎ U OP4	Stupeň:	PDPS
		Číslo přílohy:	23