


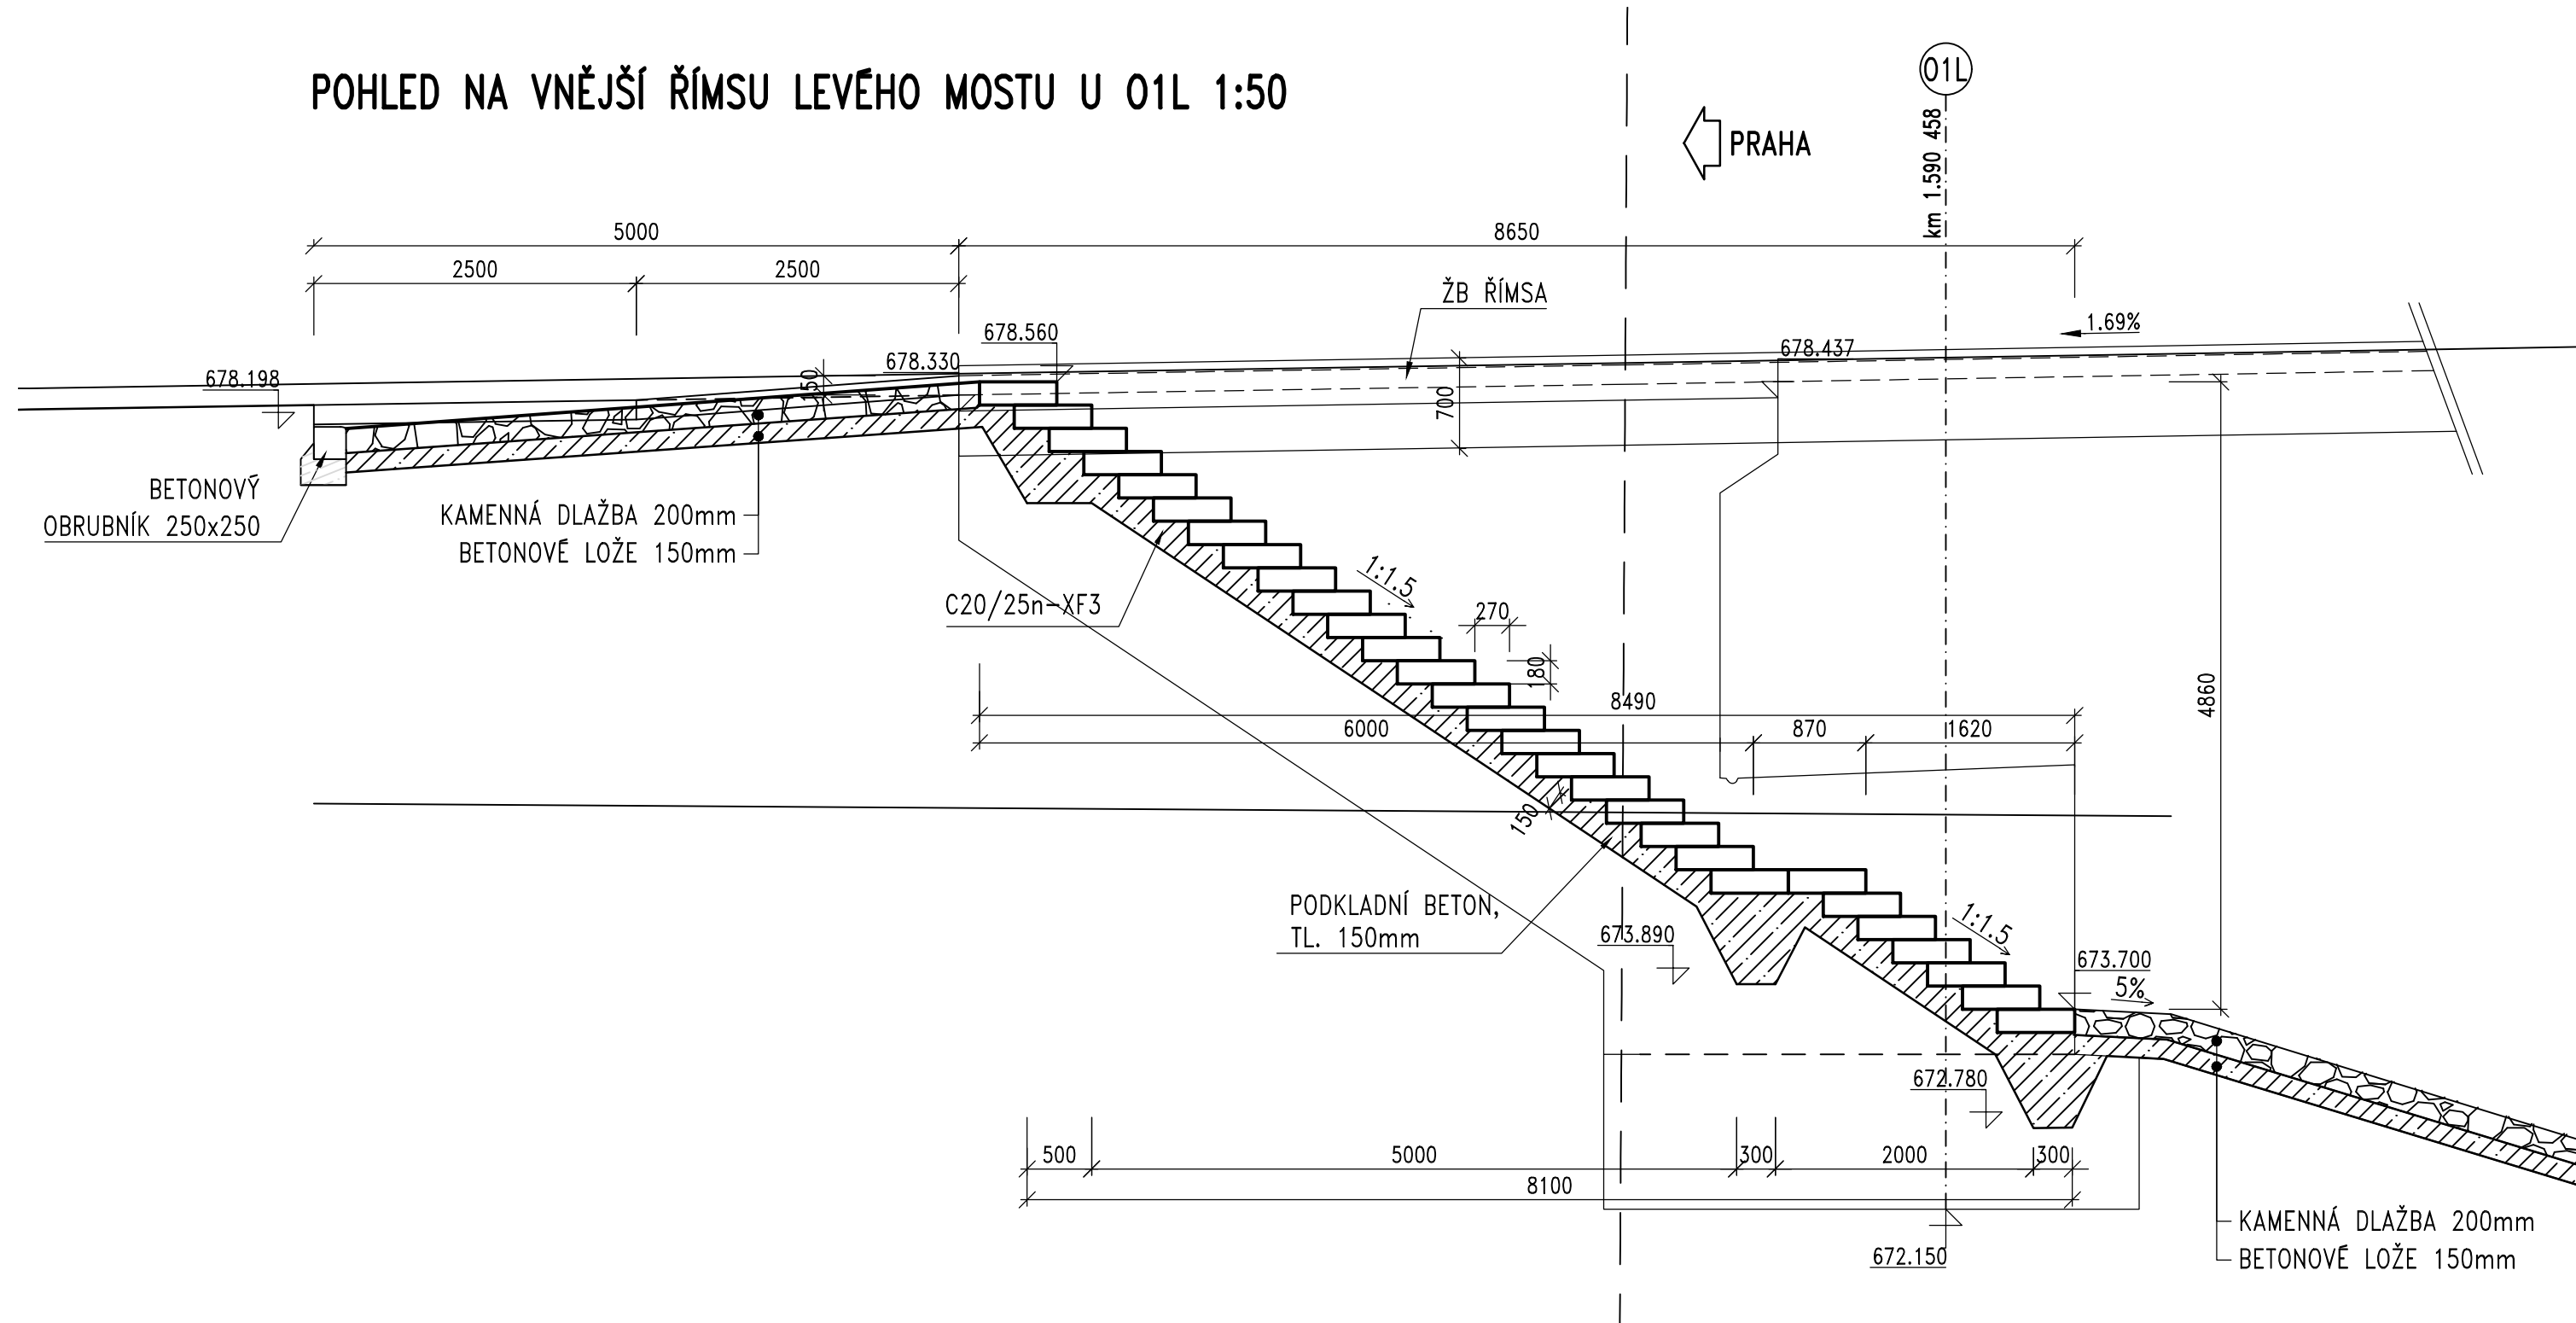


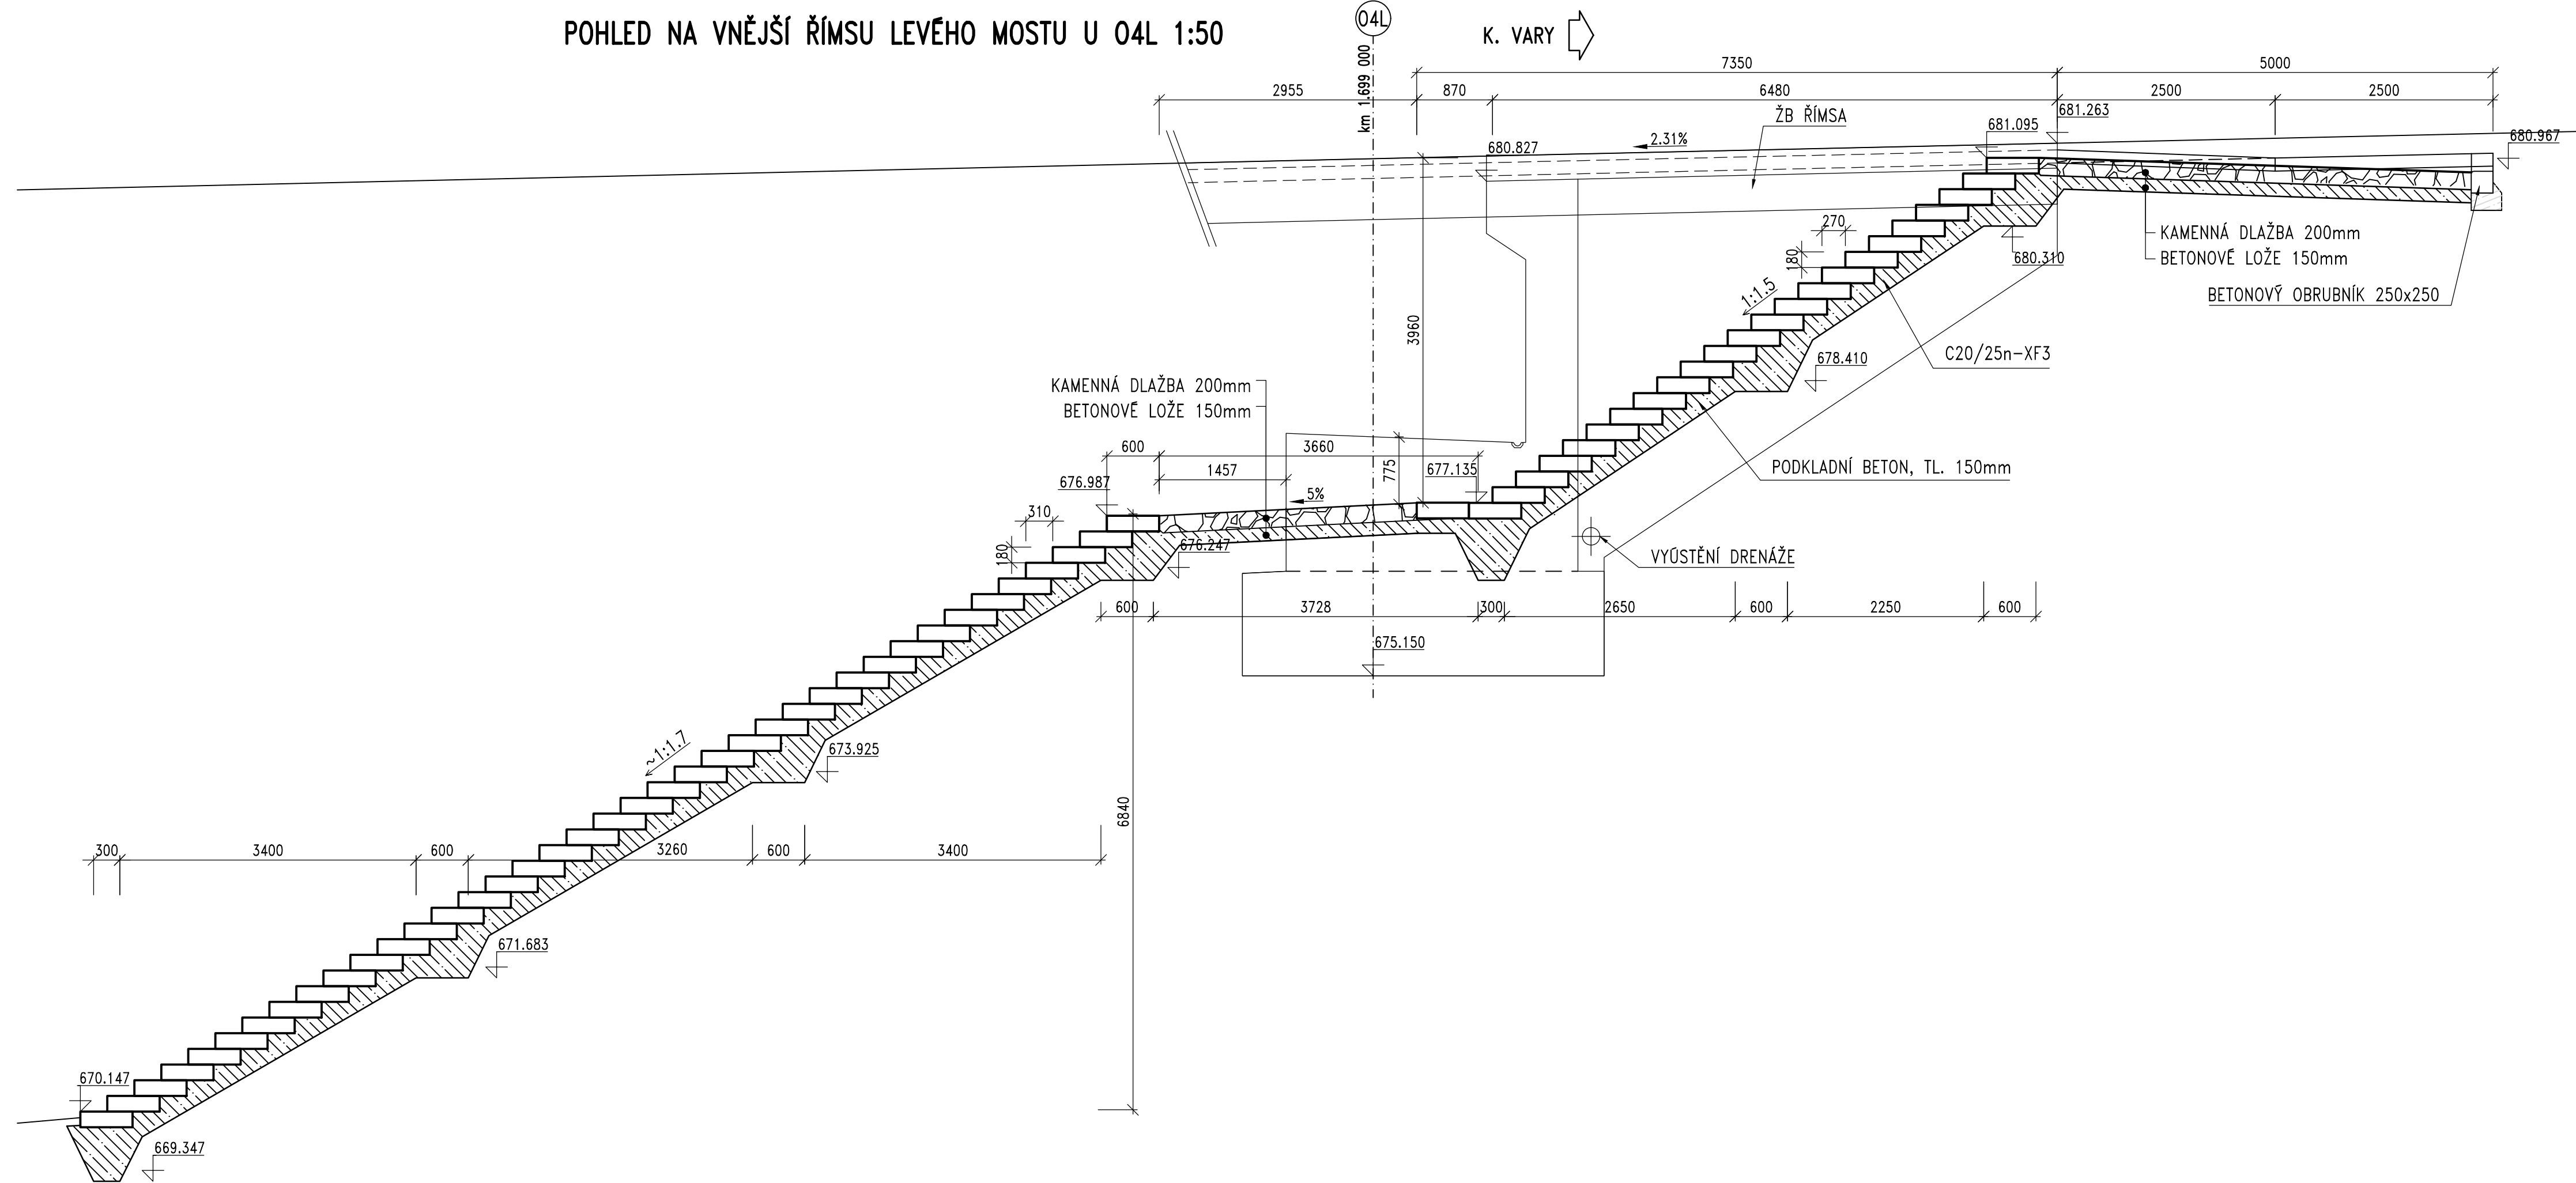

ŘEZ ÚNIKOVÝM SCHODIŠTĚM U 01P 1:50

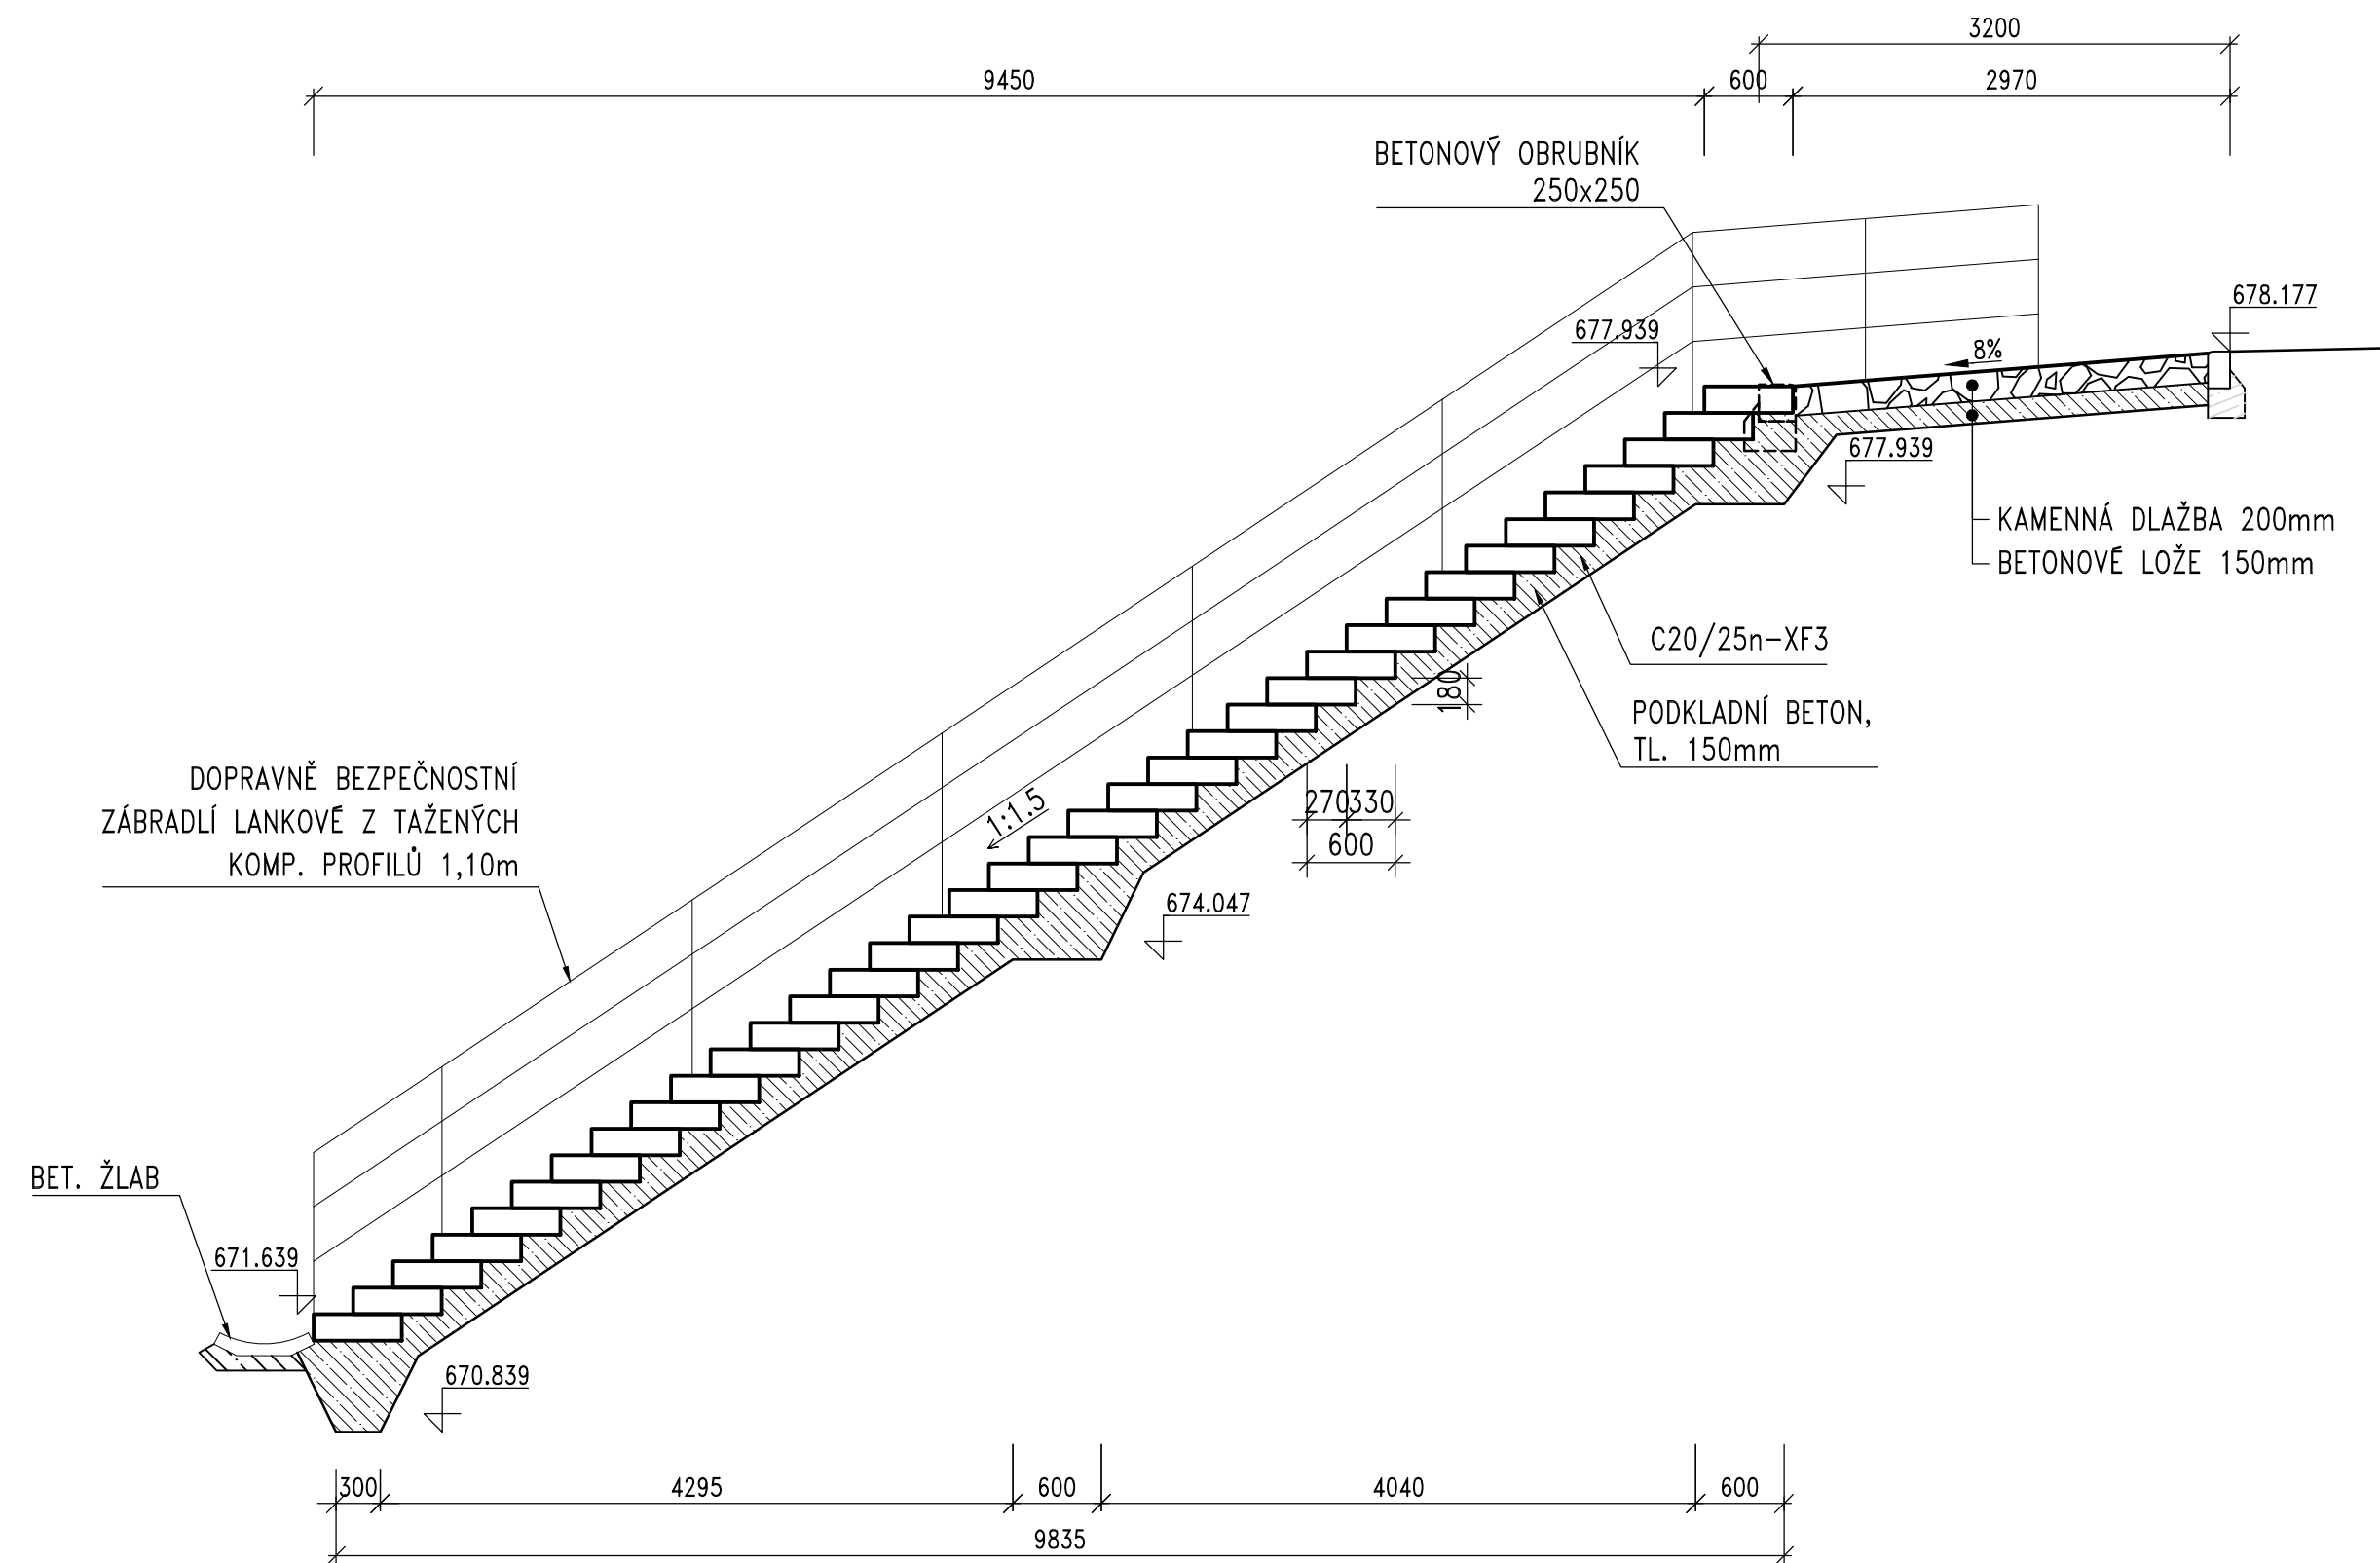

POHLED NA VNĚJŠÍ ŘÍMSU PRAVÉHO MOSTU U 04P 1:50

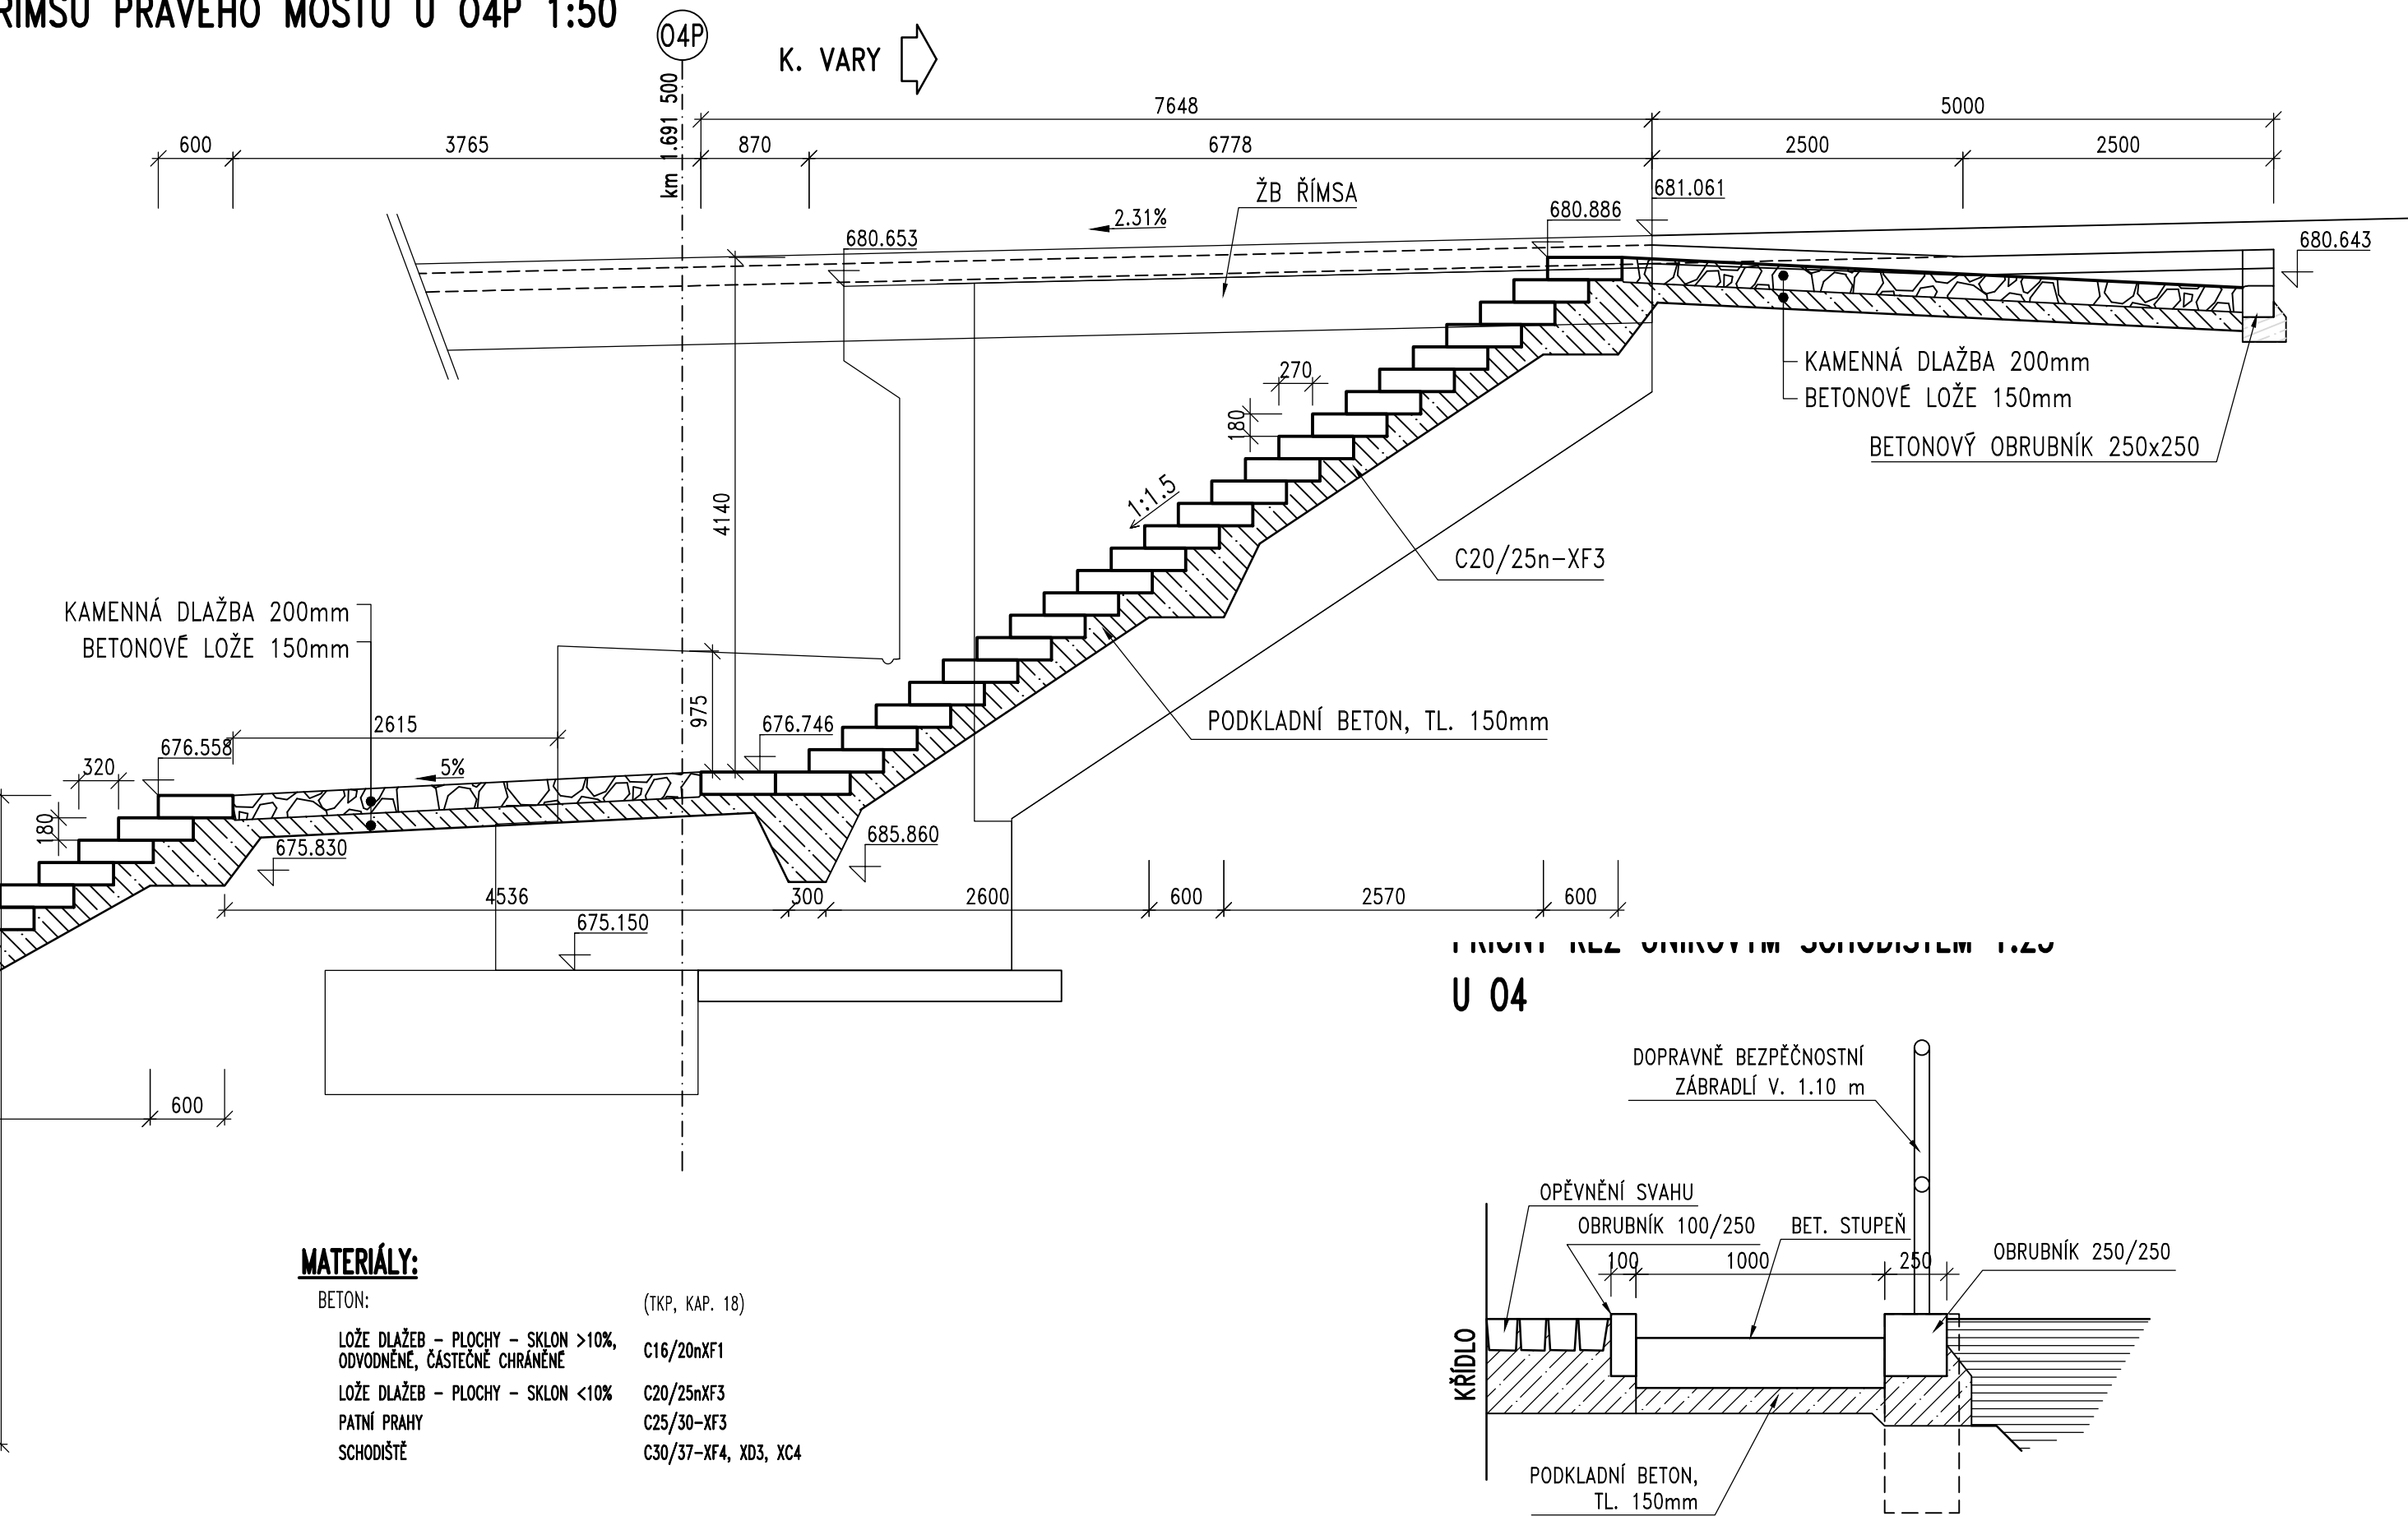

MATERIÁLY:

BETON: (TKP, KAP. 18)
LOŽE DLAŽEB - PLOCHY - SKLON >10%,
ODVOVNĚNÉ, ČÁSTEČNĚ CHRÁNĚNÉ C16/20wXF1
LOŽE DLAŽEB - PLOCHY - SKLON <10% C20/25wXF3
PATNÍ PRÁHY C25/30-XF3
SCHODIŠTĚ C30/37-XF4, XD3, XC4

ČÁST D.2
SO 202

ČISTOPIS

Souřadnicový systém S-JTSK, Výškový systém Bpv

Objednatel:

ŘEDITELSTVÍ SILNIC A DÁLNIC

ŘEDITELSTVÍ SILNIC A DÁLNIC s. p.
Čertánská 2023/12
140 00 Praha 4 - Krč

Zhotovitel PD: PRAGOPROJEKT, a.s., K Rybáře 1688/16, 147 54 Praha 4, IČO: 45272387, www.pragoprojekt.cz, datová schránka: 4kfr54

Namířil/ovracoval: Ing. Karolína HEDVÁ
podpis: *K. Hedvá*

Zodpovědný projektant: Ing. Martin BLATSKÝ
podpis: *M. Blatský*

Zástupce zodpovědného projektanta: Ing. Jan BAŽIL
podpis: *J. Bažil*

Technická kontrola: Ing. Kamel PEJCHAL
podpis: *K. Pejchal*

Hlavní inženýr projektu: Ing. Pavel SLÁPA
podpis: *P. Slápa*

Zástupce hlavního inženýra projektu: Ing. Radovan STANKOVEN
podpis: *R. Stankoven*

PRAGOPROJEKT

Kraj: KARLOVARSKÝ KRAJ Číslo zakázky: 25-150-2

Místo stavby: OLŠOVÁ VRATA, ANĚLSKÁ HORA, ŽALMANOV, HORNÍ TÁSOVICE, BOCHOV Číslo akce: 05-219

Objednatel: RSD s. p., Čertánská 2023/12, 140 00 Praha 4, IČO 65993390 Datum: 03/2026

Název stavby: D6 OLŠOVÁ VRATA-ŽALMANOV, VD-ZDS Formát: Měřítko: Stupeň: Souprava: 25

Objekt: MOST NA D6 PŘES LOMNICKÝ POTOK V km 1,600 SO101 PDPS

Příloha: TERÉNNÍ ÚPRAVY Číslo přílohy: 25