
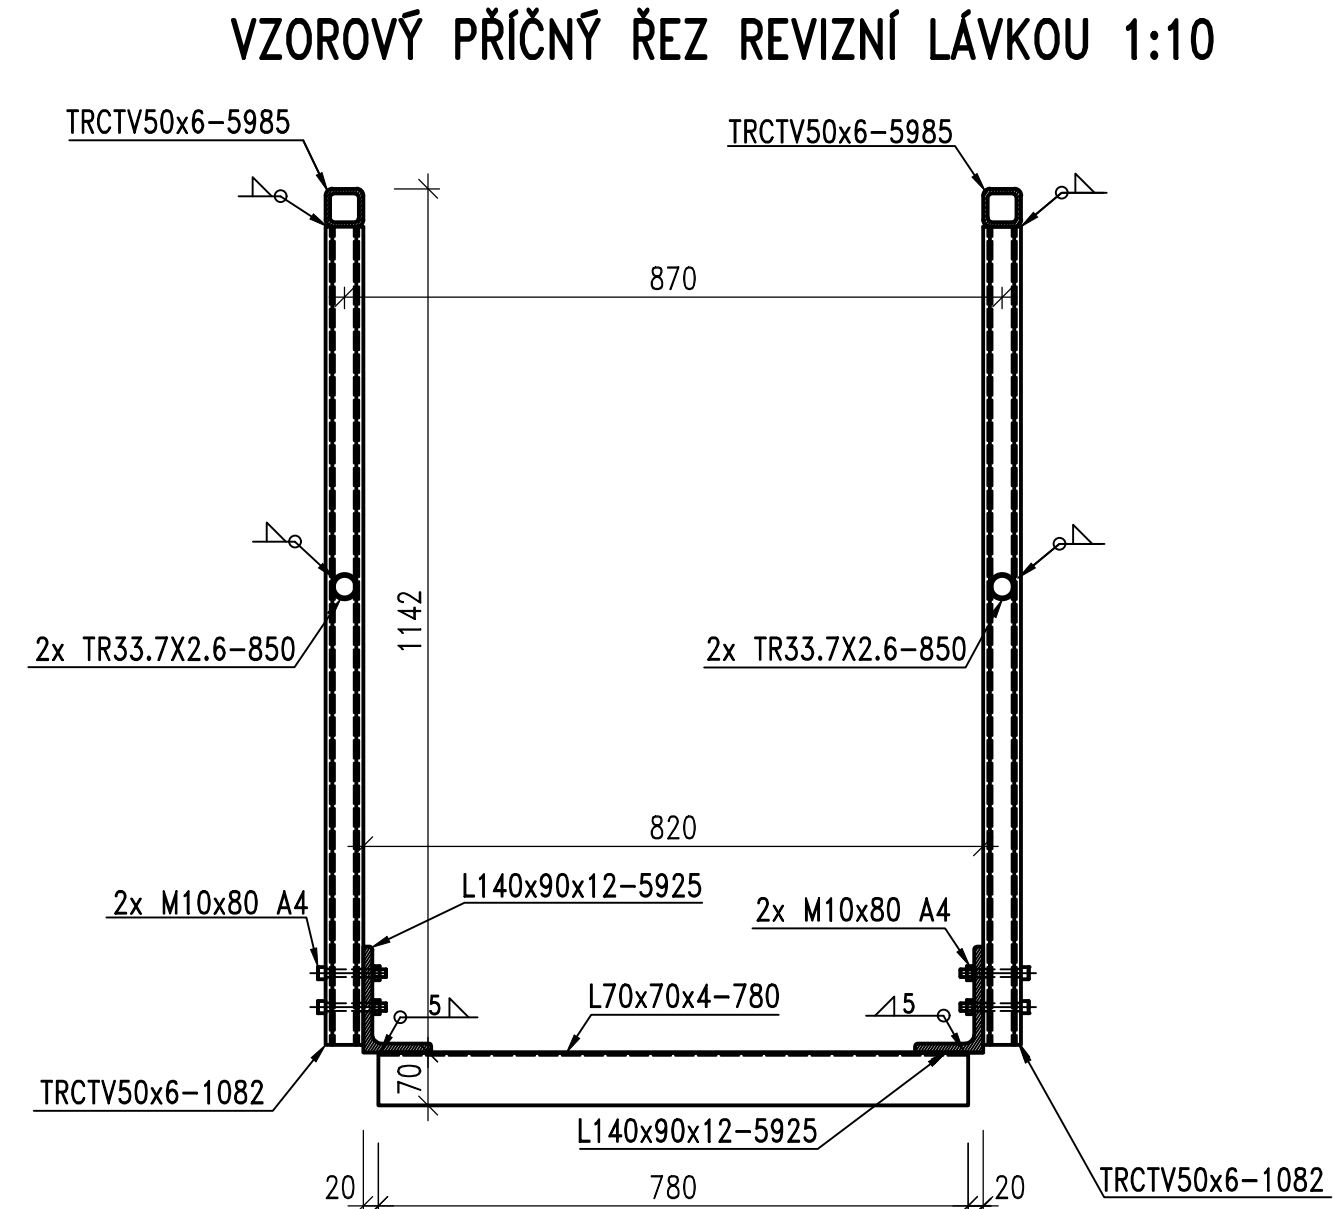
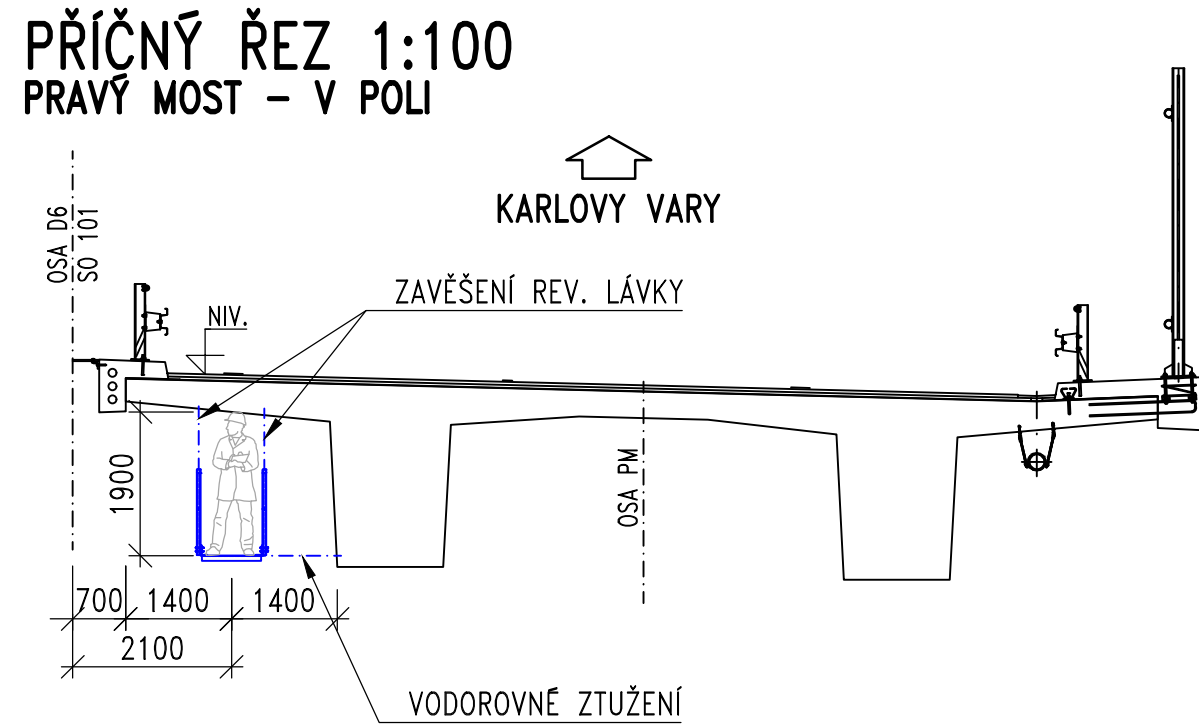


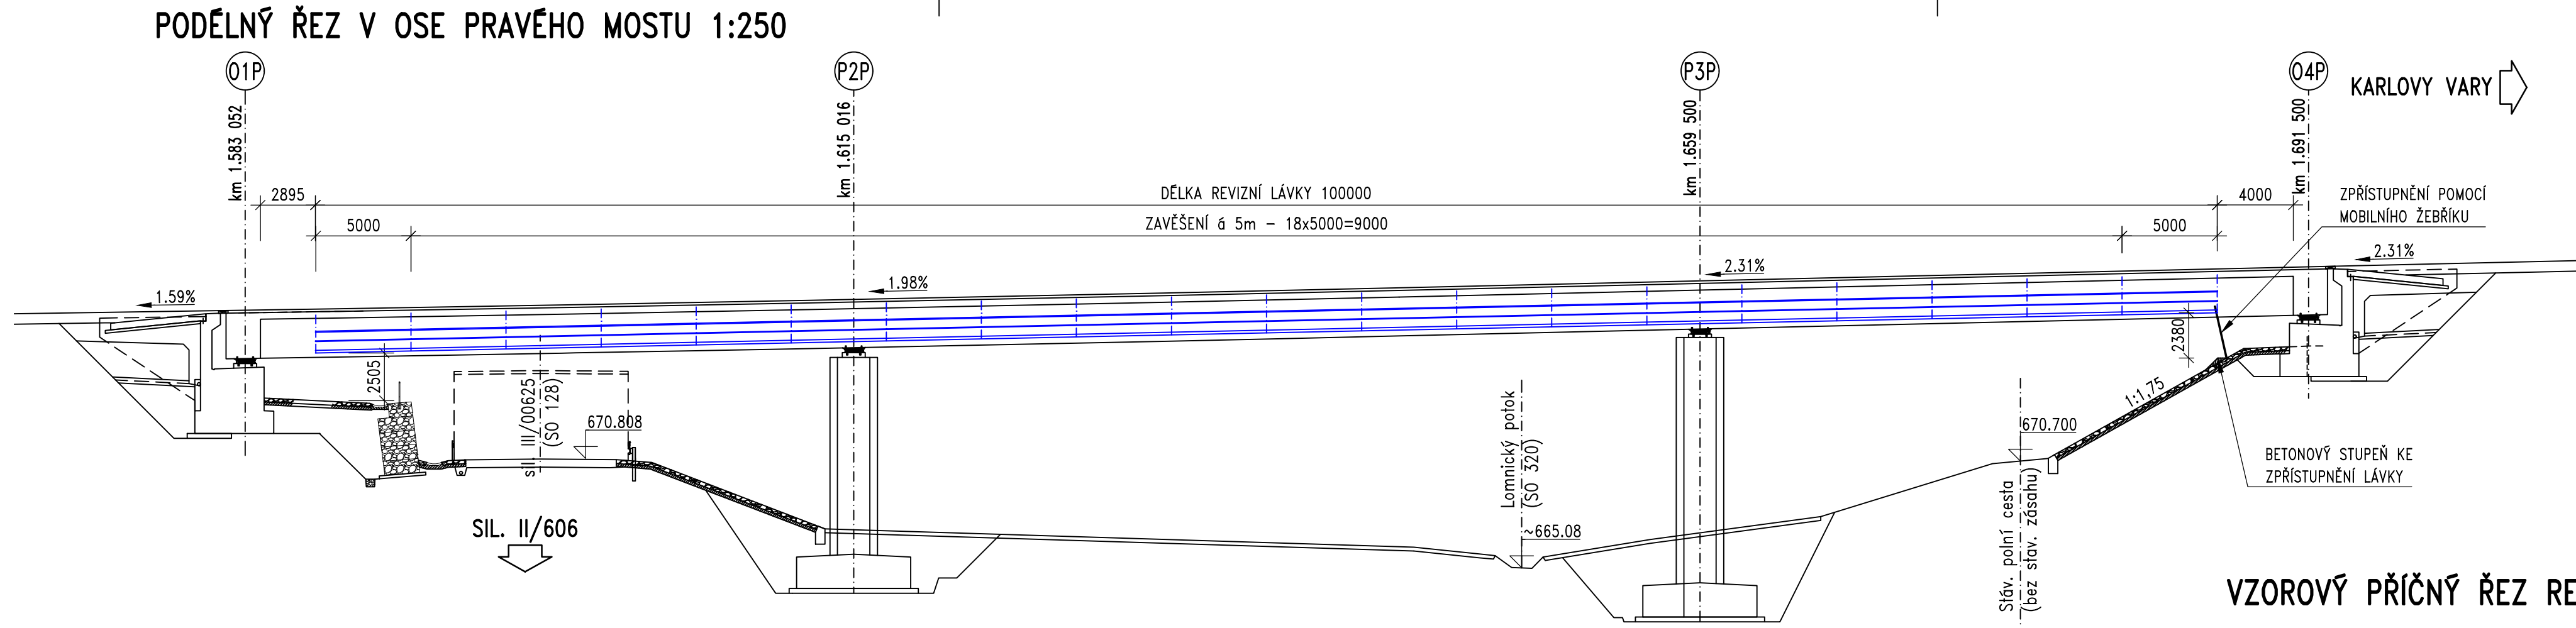

KONSTRUKČNÍ OCEL:

DLE EN 10025+A1:
ROŠT LÁVKY S235 J2
ZÁBRADLÍ LÁVKY KOMPOZIT
POCHOZÍ ROŠT KOMPOZIT

TŘÍDA PROVEDENÍ: EXC2 (dle ČSN EN 1090-2+A1)

POVRCHOVÁ OCHRANA:

OKRAJOVÉ PODMÍNKY PRO NÁVRH PKO:
-KOROZNÍ ZATÍŽENÍ C4 (DLE ISO 12944)
-ČISTOTA POVRCHU Sa 3 DLE EN ISO 8501-1, ZAOBLENÍ HRAN R=2mm
-PRO NÁVRH SKLADBY A ROZSAHU PKO PLATÍ TKP 19b
TYP III A
-ODSTÍN PKO RAL 7043 DOPRAVNÍ ŠEDÍ B

POZNÁMKA:

-PŘEDPOKLÁDÁ SE KOTVENÍ NA DODATEČNĚ VLEPENÉ CHEMICKÉ KOTVY
-SPODNÍ RÁM LÁVKY JE PROVEDEN Z OCELOVÉHO ROŠTU
-ZÁBRADLÍ LÁVKY TVOŘÍ KONSTRUKCE Z KOMPOZITNÍHO MATERIÁLU
-VÝKRES SLOUŽÍ JAKO PODKLAD PRO VYPRACOVÁNÍ VTD
-PŘÍSTUP NA LÁVKY BUDE POMOCÍ PŘENOSNÉHO ŽEBŘÍKU
-KONCE LÁVKY BUDOU OPATŘENY ŘETĚZOVOU ZÁVLAČÍ

ČÁST D.2

SO 202


Souřadnicový systém S-JTSK, Výškový systém Bpv



ŘEDITELSTVÍ
SILNIC
A DÁLNIC

ČISTOPIS

ŘEDITELSTVÍ SILNIC A DÁLNIC s. p.
Čerčanská 2023/12
140 00 Praha 4 – Krč

 Zhotovitel PD: PRAGOPROJEKT, a.s., K Ryšánci 1668/16, 147 54 Praha 4, IČO: 45272387, www.pragoprojekt.cz, datová schránka: 4kif54				
Návrh/vypracoval: Ing. Karolína HEDOVÁ podpis: 	Zodpovědný projektant: Ing. Martin BLATSKÝ podpis: 	Zástupce zodpovědného projektanta: Ing. Jan BAZIL podpis: 		
Technická kontrola: Ing. Kamil PEJCHAL podpis: 	Hlavní inženýr projektu: Ing. Pavel ŠLAPA podpis: 	Zástupce hlavního inženýra projektu: Ing. Radovan STANKOVEN podpis: 		

Kraj: KARLOVARSKÝ KRAJ	Číslo zakázky: 25-150-2
Místo stavby: OLŠOVÁ VRATA, ANDELSKÁ HORA, ŽALMANOV, HORNÍ TAŠOVICE, BOCHOV	Číslo akce: 05-219
Objednatel: RSD s. p., Čerčanská 2023/12, 140 00 Praha 4, IČO 65993390	Datum: 03/2026
Název stavby: D6 OLŠOVÁ VRATA-ŽALMANOV, VD-ZDS	Formát: PDPS
Objekt: MOST NA D6 PŘES LOMNICKÝ POTOK V km 1,600 SO101	Stupeň: 26
Příloha: REVIZNÍ LÁVKA	Číslo přílohy: 26