




 

ŘEZ VNĚJŠÍ ŘÍMSOU, LEVÝ MOST 1:25

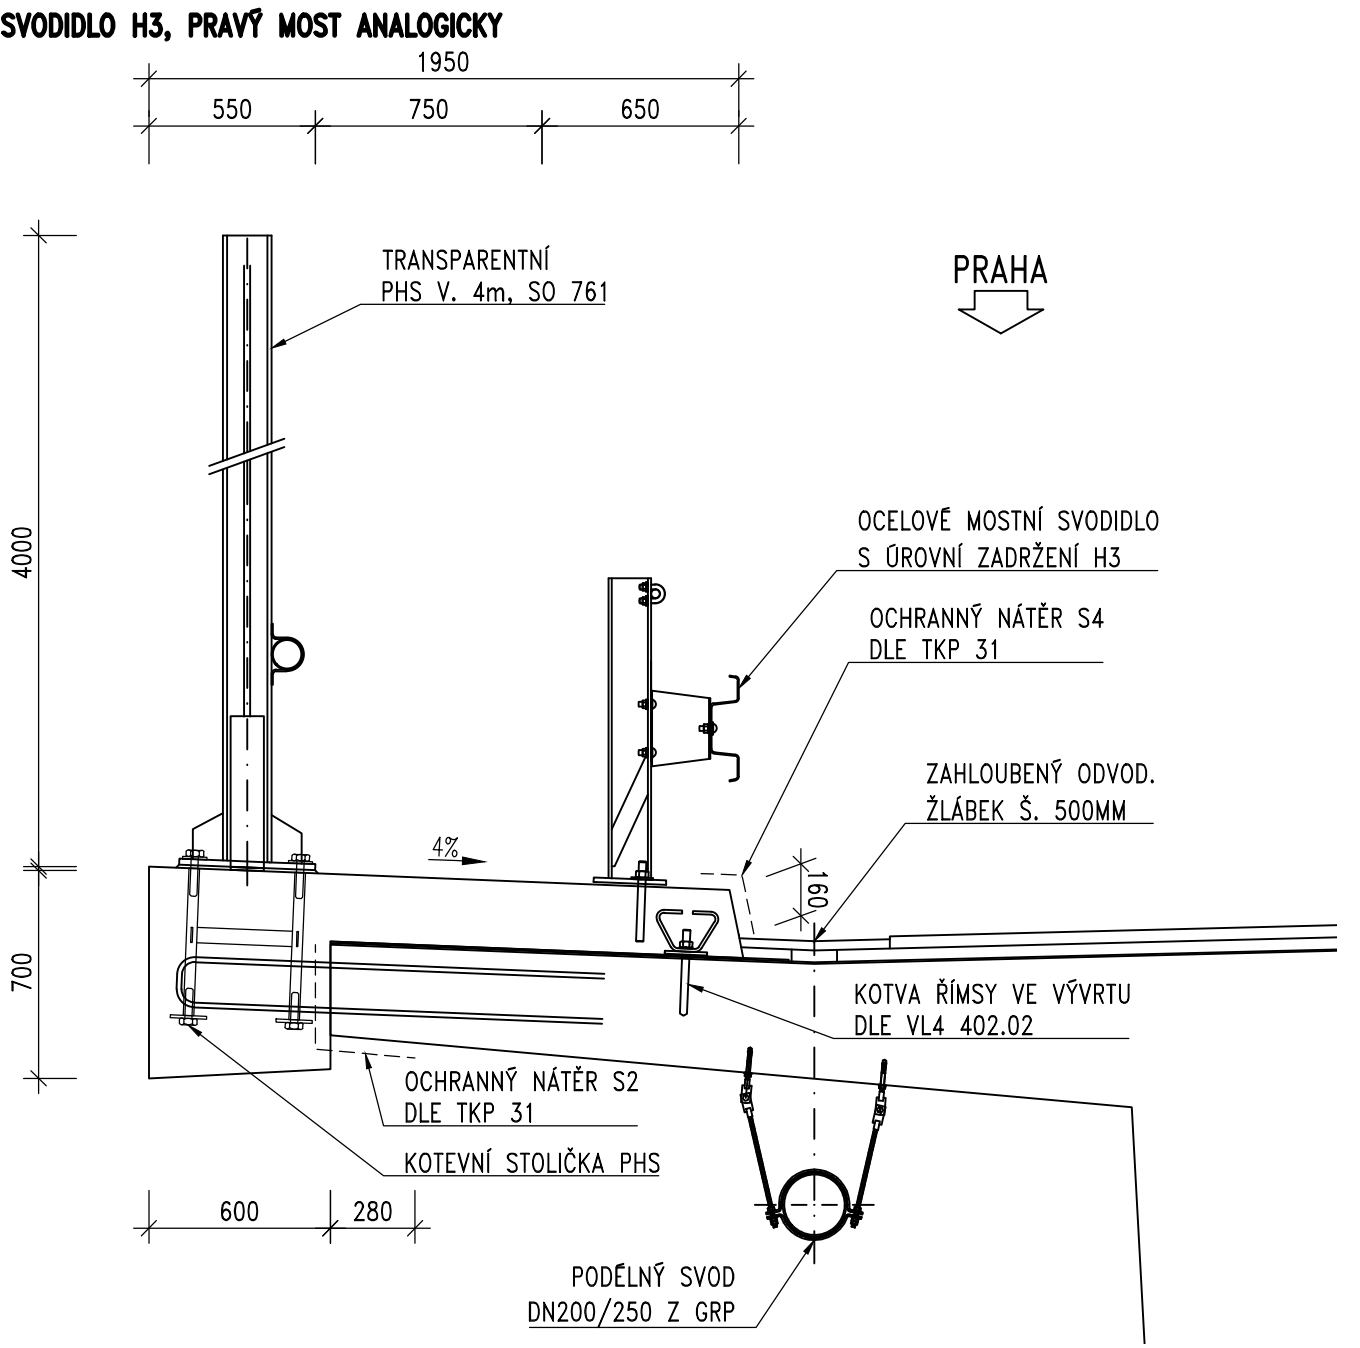

ŘEZ VNITŘNÍMI ŘÍMSAMI 1:25

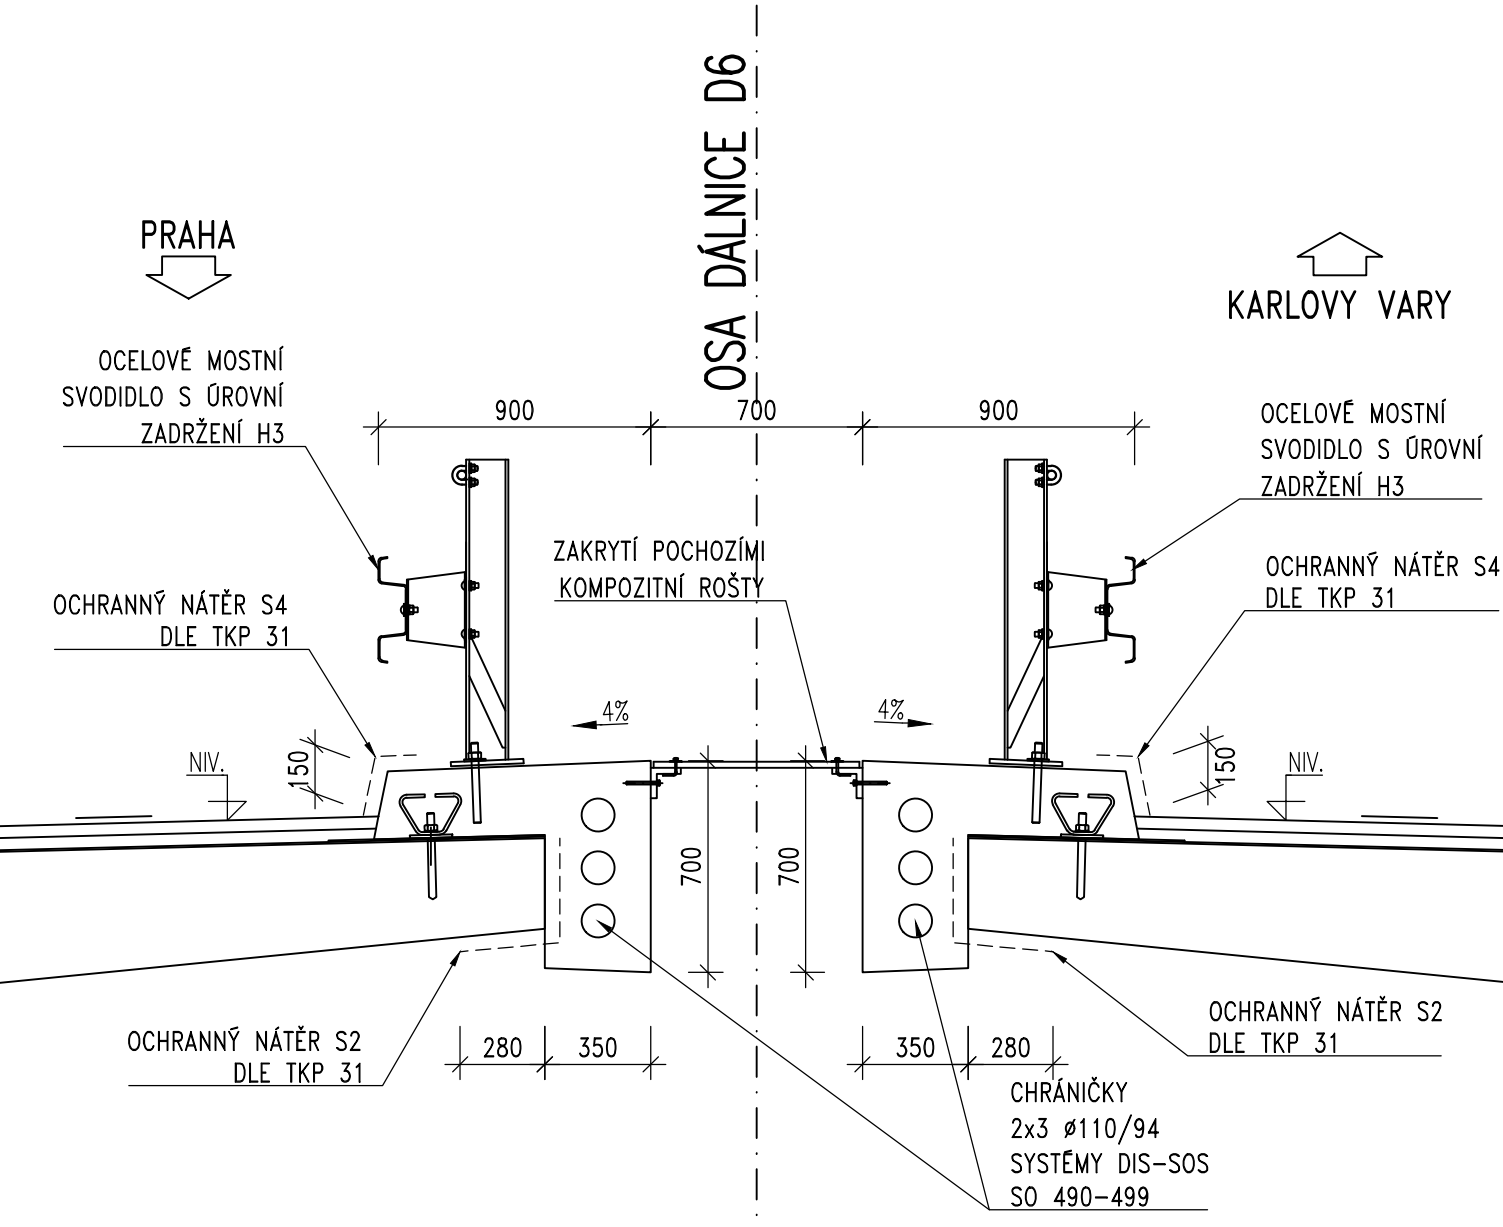

MATERIÁLY

BETON DLE TKP18
NOSNÁ KONSTRUKCE
DOBETONÁVKA KOTEV A MZ
ŘÍMSY
BETONÁŘSKÁ VÝZTUŽ
B500 B V BÉŽNÝCH PROFILECH

PROTİKOROZNÍ OCHRANA SVODIDEL:

- PKO JE NAVRŽENA V SOULADU S TKP. 19B
- POUŽITÝ SYSTÉM MUSÍ BÝT SCHVÁLEN NA www.pjpk.cz
NAVRŽENÁ SKLADBA PKO: IIIA, SVODNICE IIIA
ŽÁROVÝ Zn 85µm
2x EPOXID DVOUKOMPONENTNÍ 160µm
ALIFATICKÝ POLYURETAN 60µm
CELKEM 305µm
SVODNICE - ŽÁROVÝ Zn 70 µm
STUPĚŇ KOROZNÍ AGRESIVITY: C4
POŽADOVÁNÁ ŽIVOTNOST KONSTRUKCE: 30 LET
POŽADOVÁNÁ ŽIVOTNOST PKO: 15 LET

PŘEDPISY PRO PROVEDENÍ JEDNOTLIVÝCH KONSTRUKČNÍCH ČÁSTÍ:

- TKP KAP 18 - BETONOVÉ KONSTRUKCE A MOSTY
- ČSN EN 206+A2 - BETON - SPECIFIKACE, VLASTNOSTI, VÝROBA A SHODA
- TKP KAP 21 - IZOLACE PROTI VODĚ
- ČSN EN 14188 - ŽALUZIE A VLOŽKY DO SPÁR
- ČSN EN ISO 11600 - STAVEBNÍ KONSTRUKCE - TĚSNÍCÍ HMOTY - KLASIFIKACE A POŽADAVKY PRO TMĚLY
- TP 124 - ZÁKLADNÍ OCHRANNÁ OPATŘENÍ PRO OMEZENÍ VLIVU BLUDNÝCH PRŮDŮ NA MOSTNÍ OBJEKTY A OSTATNÍ BETONOVÉ KONSTRUKCE POZEMNÍCH KOMUNIKACÍ
- TP 193 - SVAŘOVÁNÍ BETONÁŘSKÉ VÝZTUŽE A JINÉ DRUHY SPOJŮ ČSN EN ISO 17660-2 SVAŘOVÁNÍ - SVAŘOVÁNÍ BETONÁŘSKÉ OCELI ČÁST 2: NENOSNÉ SVAŘOVÉ SPOJE

ČÁST D.2
SO 202

ČISTOPIS

Logo of Ředitelství silnic a dálnic (RSD) and project information.

Table with project details, including names of responsible parties and their roles.

Table with project details, including dates, locations, and other administrative information.