
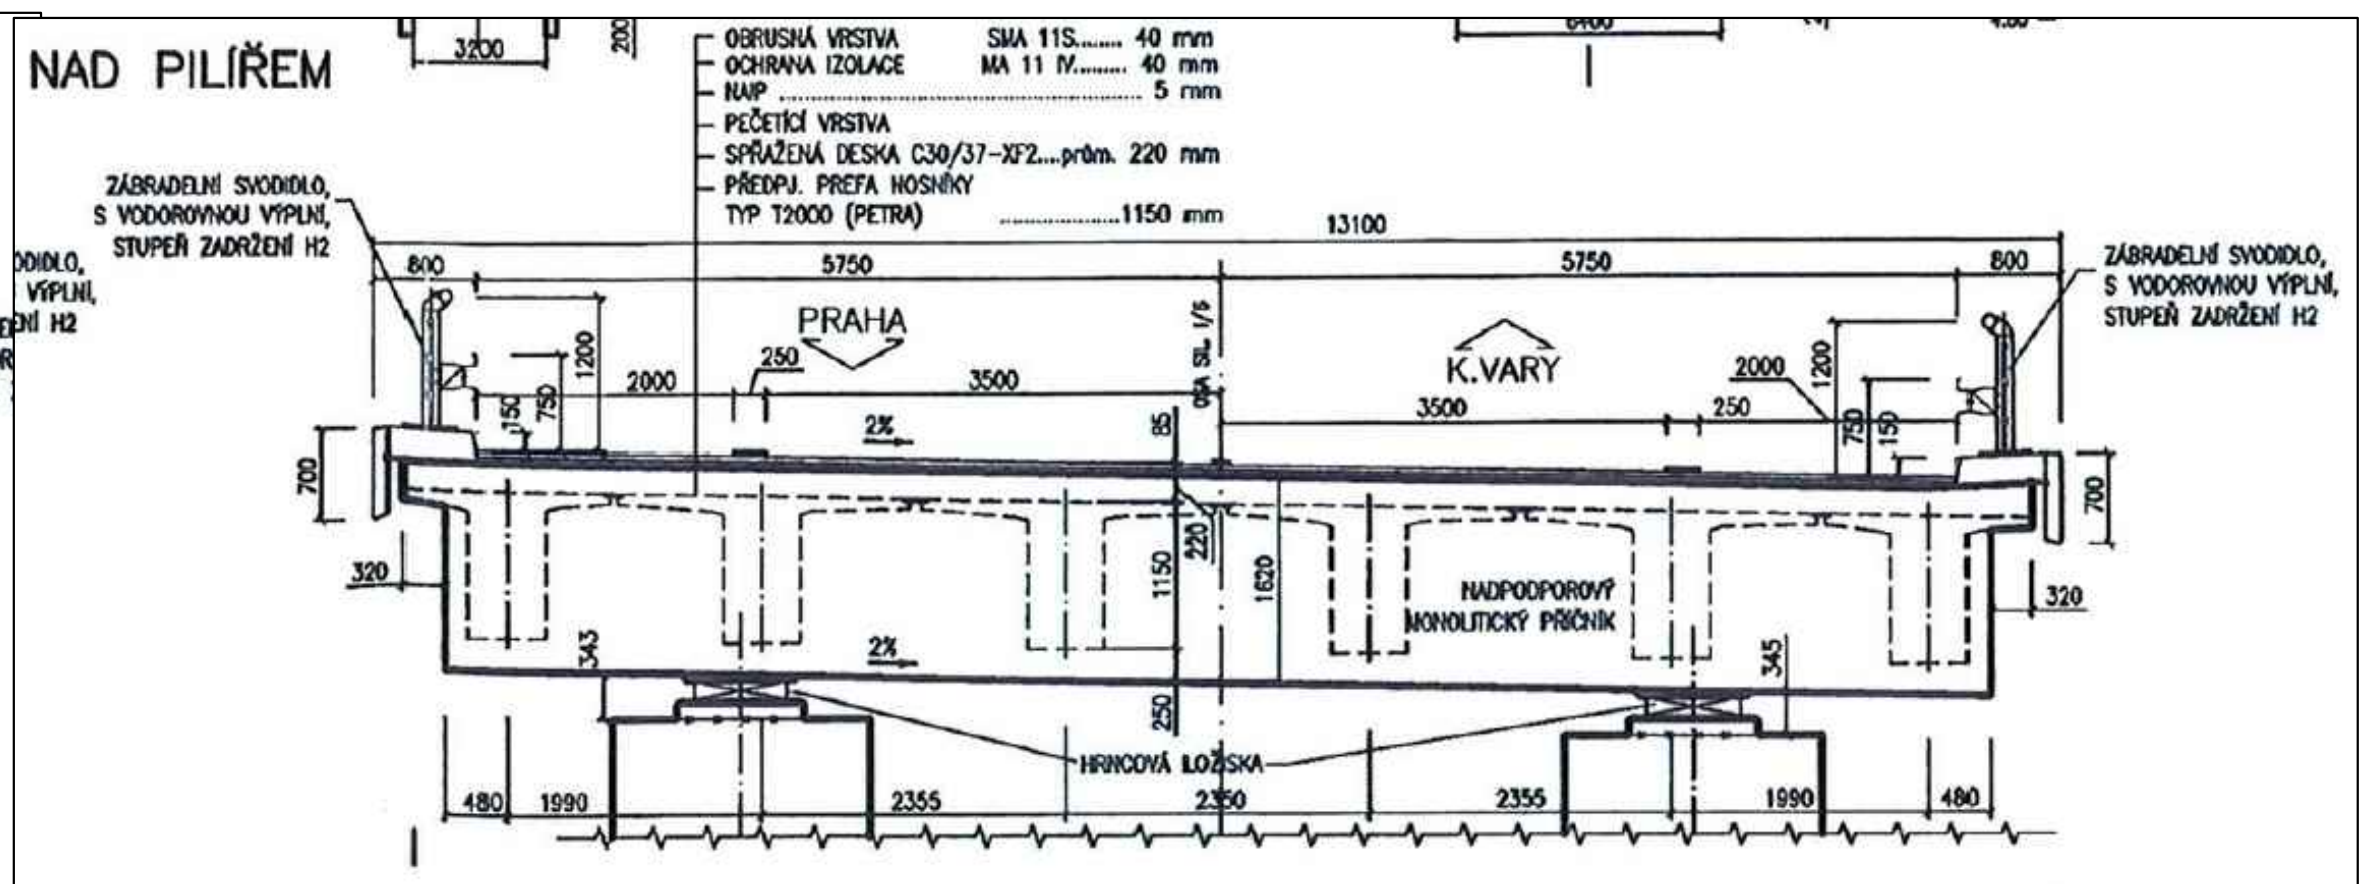
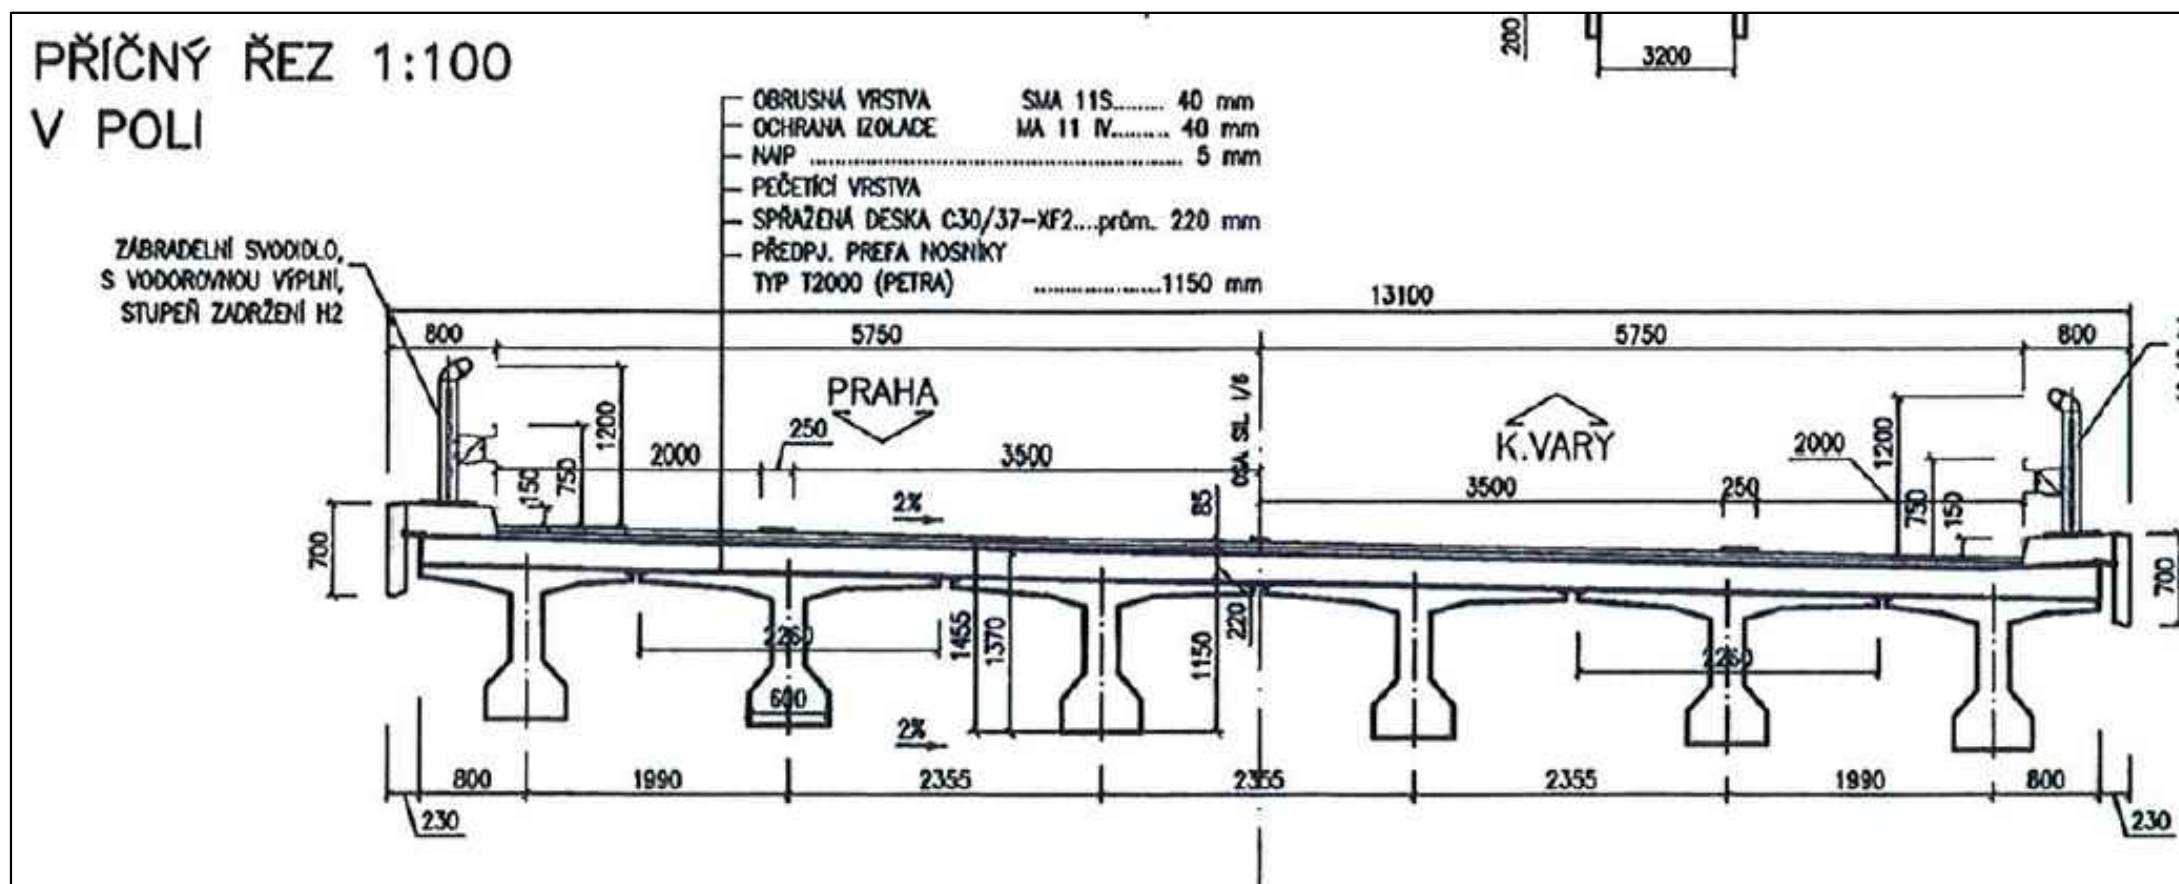
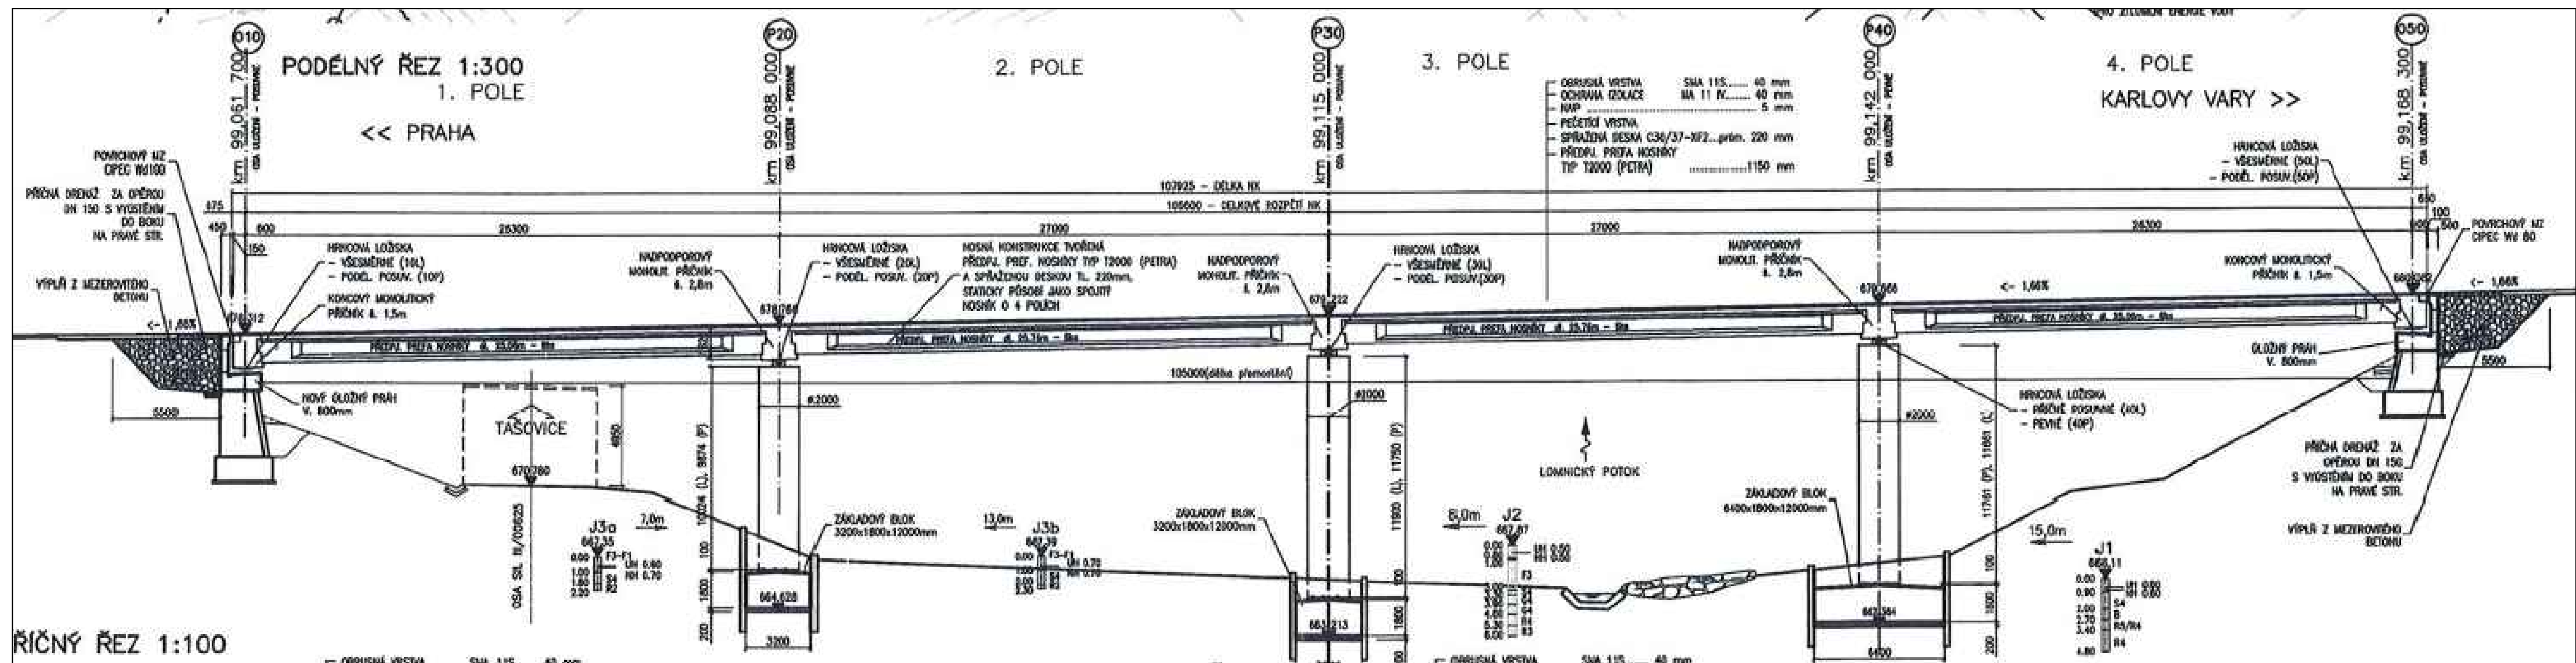


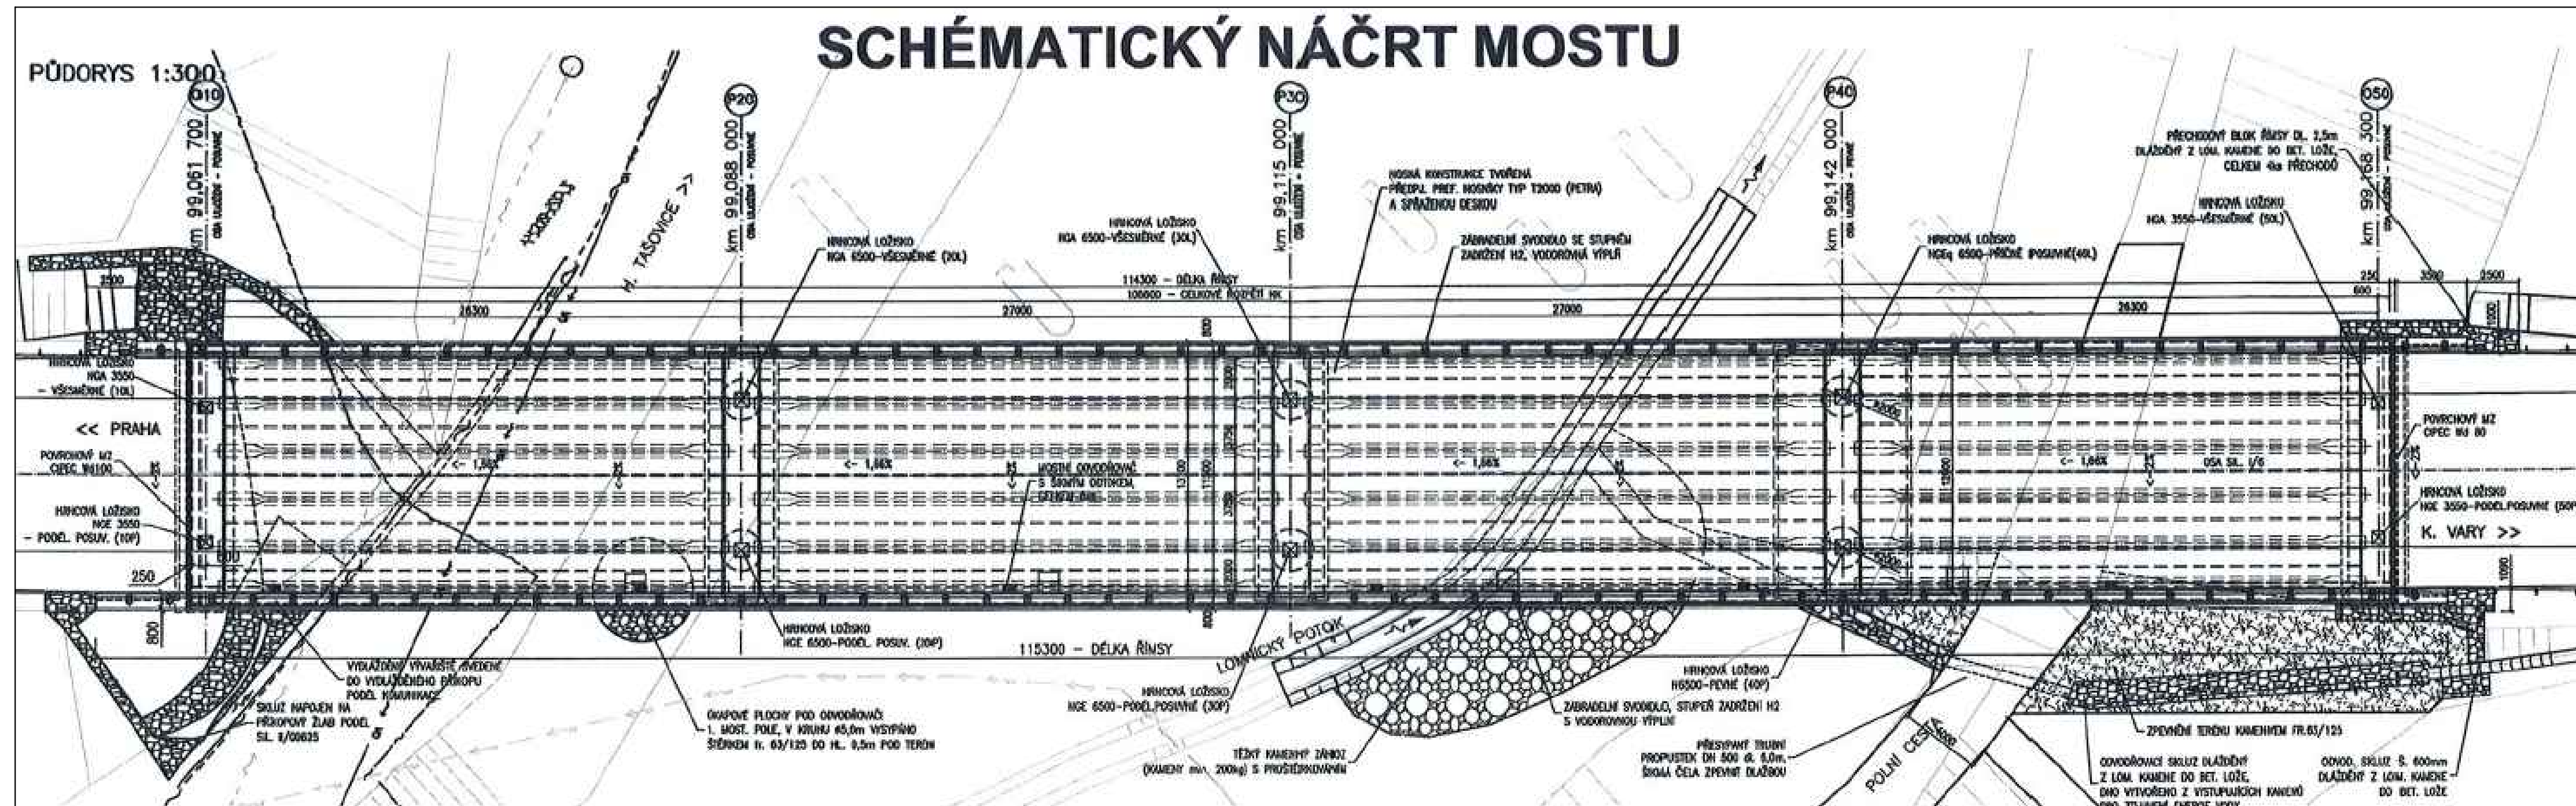

ČÁST D.2
SO 202

ČISTOPIS

Souřadnicový systém S-JTSK, Výškový systém Bpv

Objednatel: Ředitelství silnic a dálnic

Ředitelství silnic a dálnic s. p.
Čerčanská 2023/12
140 00 Praha 4 - Krč

Zhotovitel PD: PRAGOPROJEKT, a.s., K Rybáře 1668/16, 147 54 Praha 4, IČO: 45272387, www.pragoprojekt.cz, datová schránka: 4klrf54

Namí/vypracoval: Ing. Karolína HEDGÁ
Zodpovědný projektant: Ing. Martin BLATSKÝ
Zástupce zodpovědného projektanta: Ing. Jan BAZIL
Podpis: *K. Hedgá* *M. Blatský* *J. Bazil*

Technická kontrola: Ing. Kamil PEČIHAL
Hlavní inženýr projektu: Ing. Pavel SLÁPA
Zástupce hlavního inženýra projektu: Ing. Radovan STANKOVEN
Podpis: *K. Pečihal* *P. Slápa* *R. Stankoven*

PRAGOPROJEKT

Kraj: KARLOVARSKÝ KRAJ
Místo stavby: OLŠOVÁ VRATA, ANDELSKÁ HORA, ŽALMANOV, HORNÍ TAŠOVICE, BOCHOV
Objednatel: ŘSD s. p., Čerčanská 2023/12, 140 00 Praha 4, IČO 65993390
Název stavby: D6 OLŠOVÁ VRATA-ŽALMANOV, VD-ZDS
Objekt: MOST NA D6 PŘES LOMNICKÝ POTOK V km 1,600 SO101
Příloha: STÁVAJÍCÍ STAV A DEMOLICE

Číslo zakázky: 25-150-2
Číslo dílu: 05-219
Datum: 03/2026
Formát:
Měřítko:
Stupeň:
Souprava:
PDPS
Číslo přílohy: 30