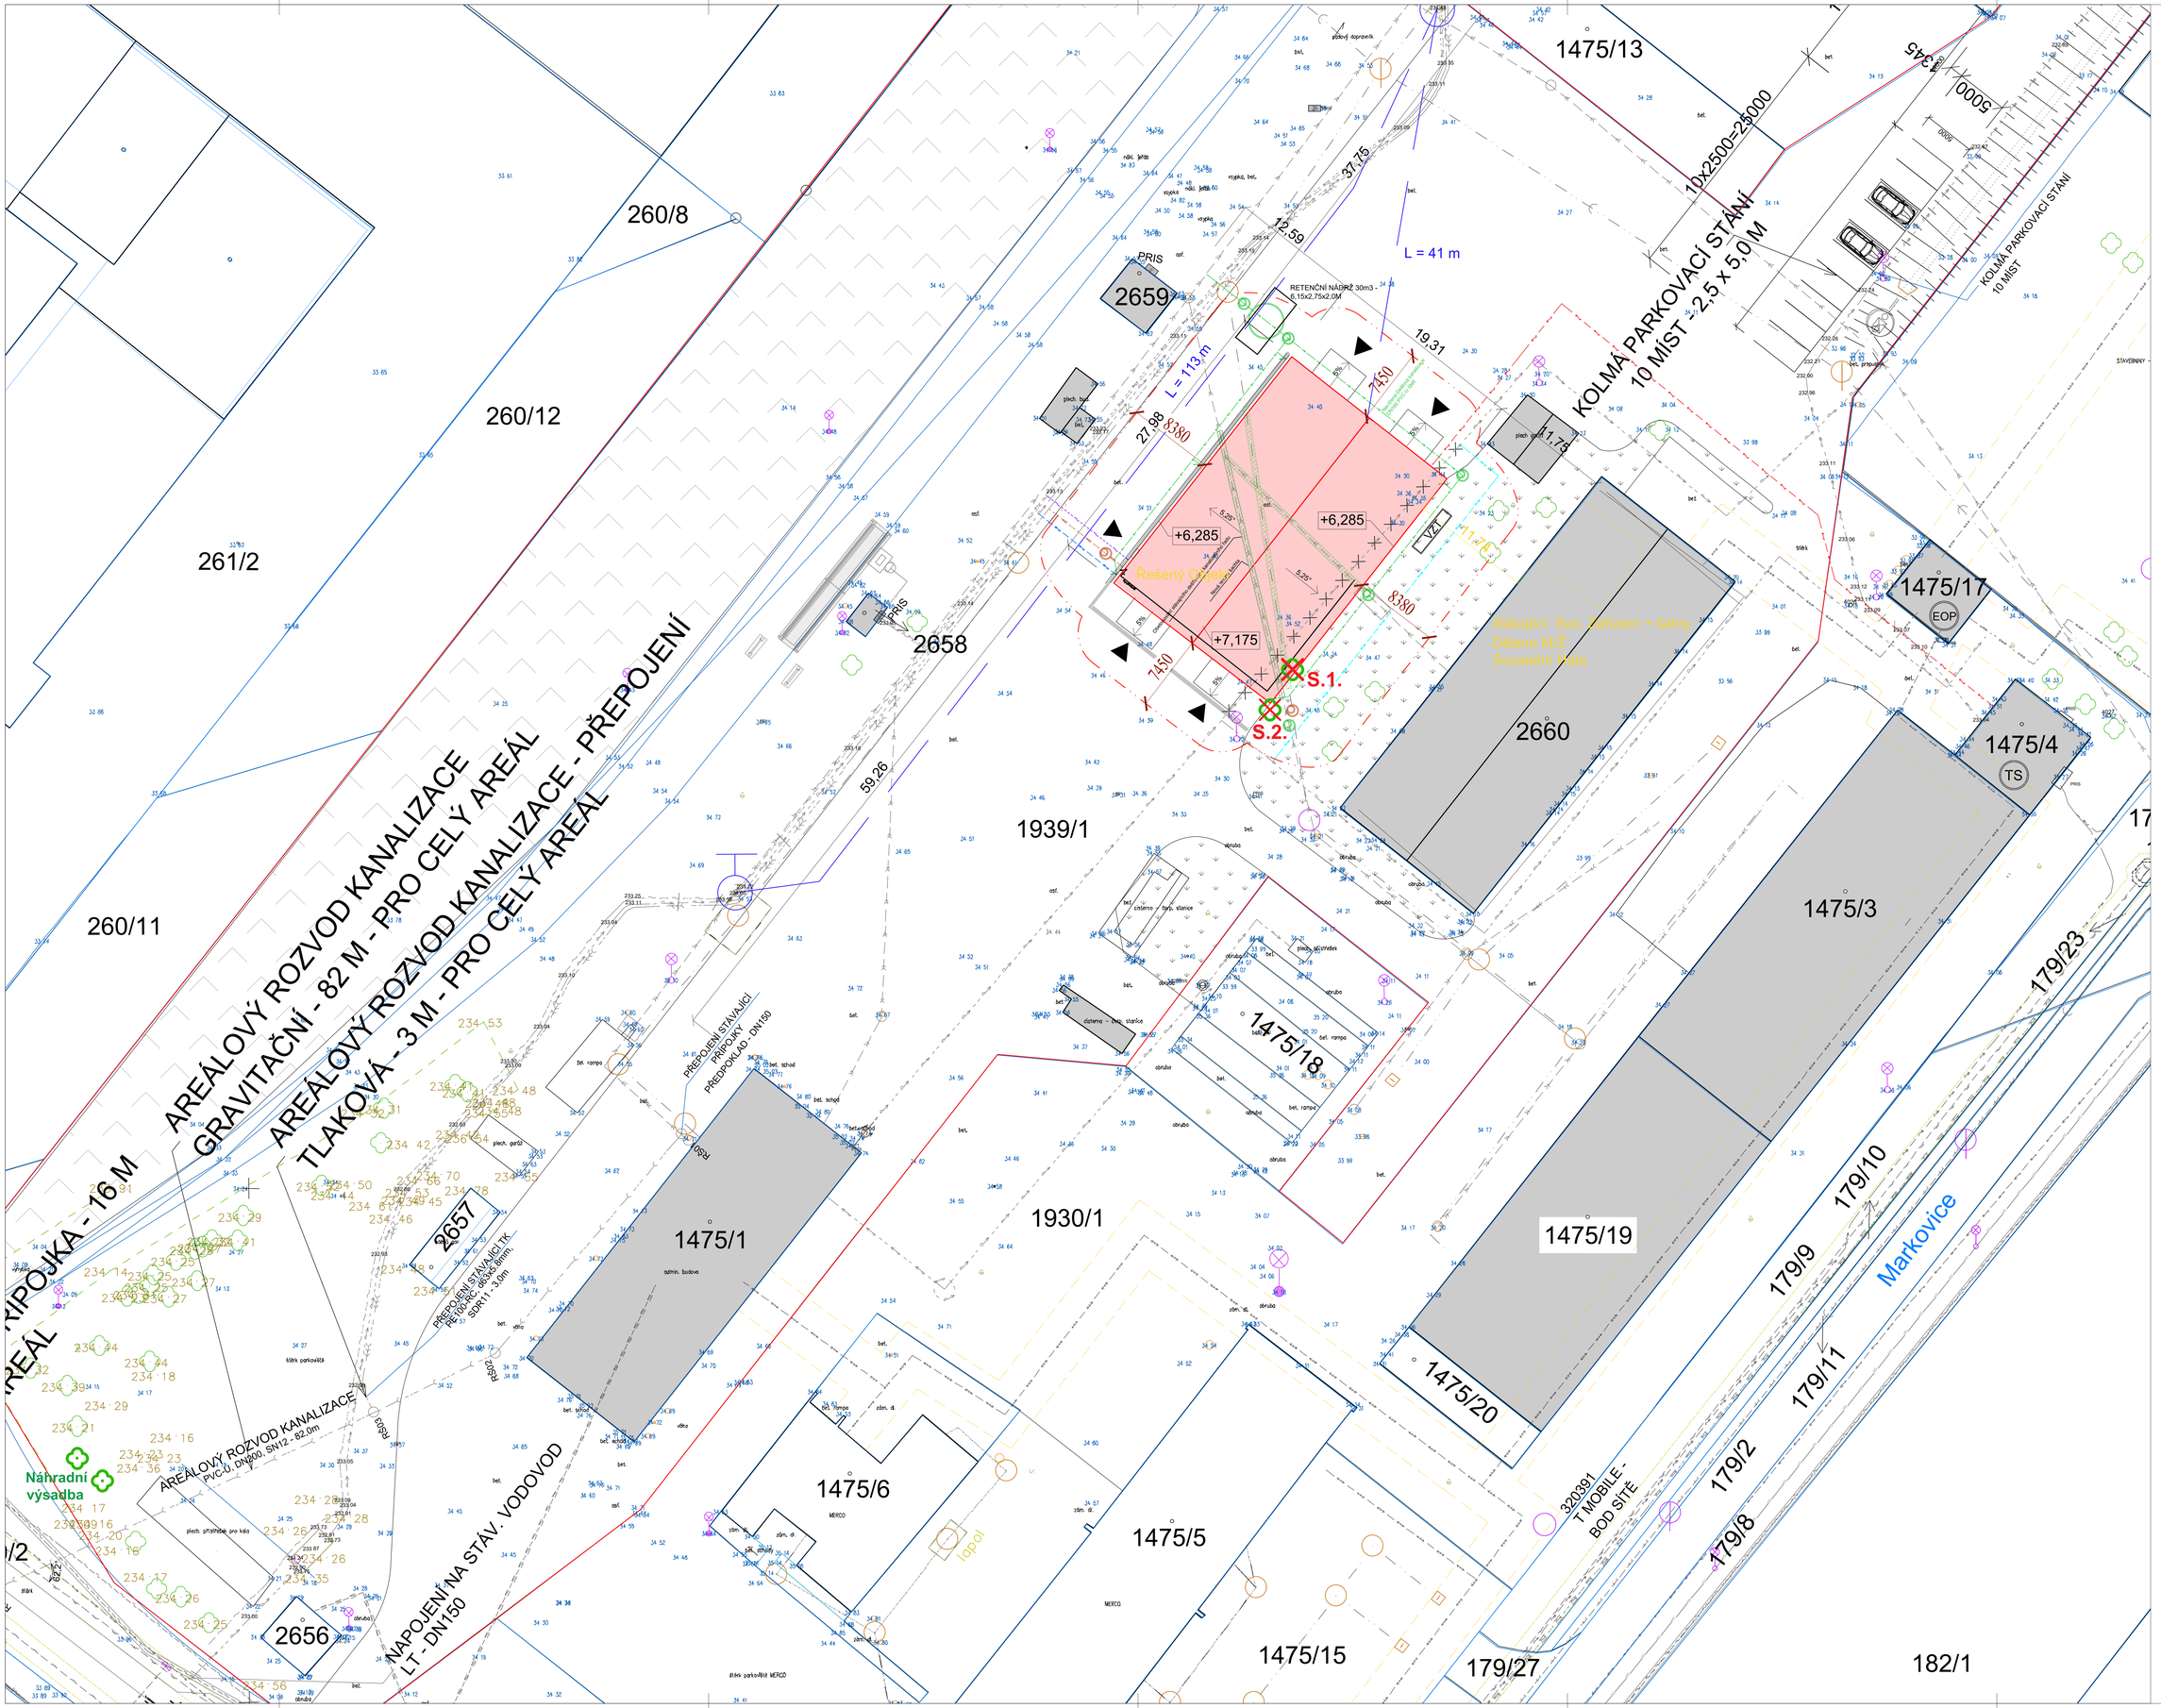

LEGENDA

- NAVRHOVANÝ OBJEKT
- STÁVAJÍCÍ OBJEKTY
- HRANICE ŘEŠENÉHO POZEMKU
- STÁVAJÍCÍ VYSOKÁ ZELEŇ
- KÁCENÍ, S.1. - S.2.
- STÁVAJÍCÍ POULIČNÍ OSVĚTLENÍ
- STÁVAJÍCÍ KOLEJE - VLEČKA
- PŘEDPOKLÁDANÝ POŽÁRNĚ NEBEZPEČNÝ PROSTOR ŘEŠENÉHO OBJEKTU
- HYDRANTY (Podz.)
- PBŘ ODSTUP
- TRÁVNÍK, NÍZKÁ ZELEŇ
- STÁVAJÍCÍ VYSOKÁ ZELEŇ
- STÁVAJÍCÍ VOZOVKA - ASFALT
- LINIOVÝ ŽLAB PRO ODVOD DEŠŤOVÉ VODY
- VSTUP

INŽENÝRSKÉ SÍTĚ_STÁVAJÍCÍ
- PŘEDPOKLÁDANÁ TRASA - NUTNO PROVĚŘIT

- STÁVAJÍCÍ VEDENÍ NN
- STÁVAJÍCÍ KANALIZACE DEŠŤOVÁ
- STÁVAJÍCÍ KANALIZACE SPLAŠKOVÁ
- STÁVAJÍCÍ VODOVODNÍ ŘAD
- STÁVAJÍCÍ VEDENÍ OPTICKÉHO KABELU
- STÁVAJÍCÍ TEPLOVOD + OCHRANNÉ PÁSMO
- STÁVAJÍCÍ HORKOVOD + OCHRANNÉ PÁSMO
- STÁVAJÍCÍ NADZEMNÍ VEDENÍ CETIN
- STÁVAJÍCÍ VEDENÍ POULIČNÍHO OSVĚTLENÍ
- STÁVAJÍCÍ PROVOZNÍ SPLAŠKOVÁ KANALIZACE
- STÁVAJÍCÍ VEDENÍ PLYNU STL + OCHRANNÉ PÁSMO
- TS — STÁVAJÍCÍ TRAFOSTANICE
- EOP — CENTRÁLNÍ ROZVODNA TEPLA

INŽENÝRSKÉ SÍTĚ_NAVRŽENÉ

- PRIS — STÁVAJÍCÍ ELEKTRO PŘÍPOJKOVÁ SKŘÍŇ
- PŘÍPOJKA NN
- PŘÍPOJKA KANALIZACE DEŠŤOVÁ
- PŘÍPOJKA KANALIZACE SPLAŠKOVÁ
- PŘÍPOJKA VODOVODNÍ ŘAD
- PŘÍPOJKA VEDENÍ OPTICKÉHO KABELU
- PŘELOŽKA VODOVODNÍHO ŘADU
- PŘELOŽKA VODOVODNÍHO ŘADU
- REVIZNÍ ŠACHTA
- RETENČNÍ NÁDRŽ 30 m3
- VZT — VENKOVNÍ VZT JEDNOTKA S REKUPERACÍ
- OBETONOVÁNÍ STÁVAJÍCÍCH SÍTÍ

AUTORIZOVANÝ ARCHITEKT ČKA ČESKÁ REPUBLIKA

Digitálně podepsal
Ing. arch. Jakub Volka
Datum: 2025.10.30
14:14:23 +01'00'

SKLADOVÁ HALA HRADEC KRÁLOVÉ

Hradec Králové
k.ú. Slezské Předměstí (664597E)

STUPEŇ PROJEKTU: +235,000 mnm Bpv

DOKUMENTACE PRO STAVEBNÍ POVOLENÍ (DSP)

ODPOVĚDNÝ PROJEKTANT
Ing.arch. Jakub Volka, ČKA 03967
733 575 363, jakub.volka@baseapoint.cz

VYPRACOVAL
Ing.arch. Jakub Volka
Bc. Ivan Sýkora

INVESTOR
SOLAR DEPOREC s.r.o.
Malostranské náměstí 5/28, Malá Strana
118 00 Praha 1

DÍL: C
ČÁST DOKUMENTACE: C.3
OBSAH VÝKRESU: SITUACE KÁCENÍ

MĚŘÍTKO	FORMÁT
1:200	2 X A4
DATUM	1 V VYDÁNÍ
10/2025	01/2024

STUPEŇ	DÍL	ČÁST	ČÍSLO	PŘÍLOHA	REVIZE
DSP	D-S001	ARS	A101	1NP	R00

ZPRACOVATEL ČÁSTI
Baseport s.r.o
V Beránkách 2350/6
143 00 Praha 11
www.baseport.cz

GENERÁLNÍ PROJEKTANT
Baseport s.r.o
V Beránkách 2350/6
143 00 Praha 11
www.baseport.cz