PŮDORYS ODVODNĚNÍ TERAS M 1:250

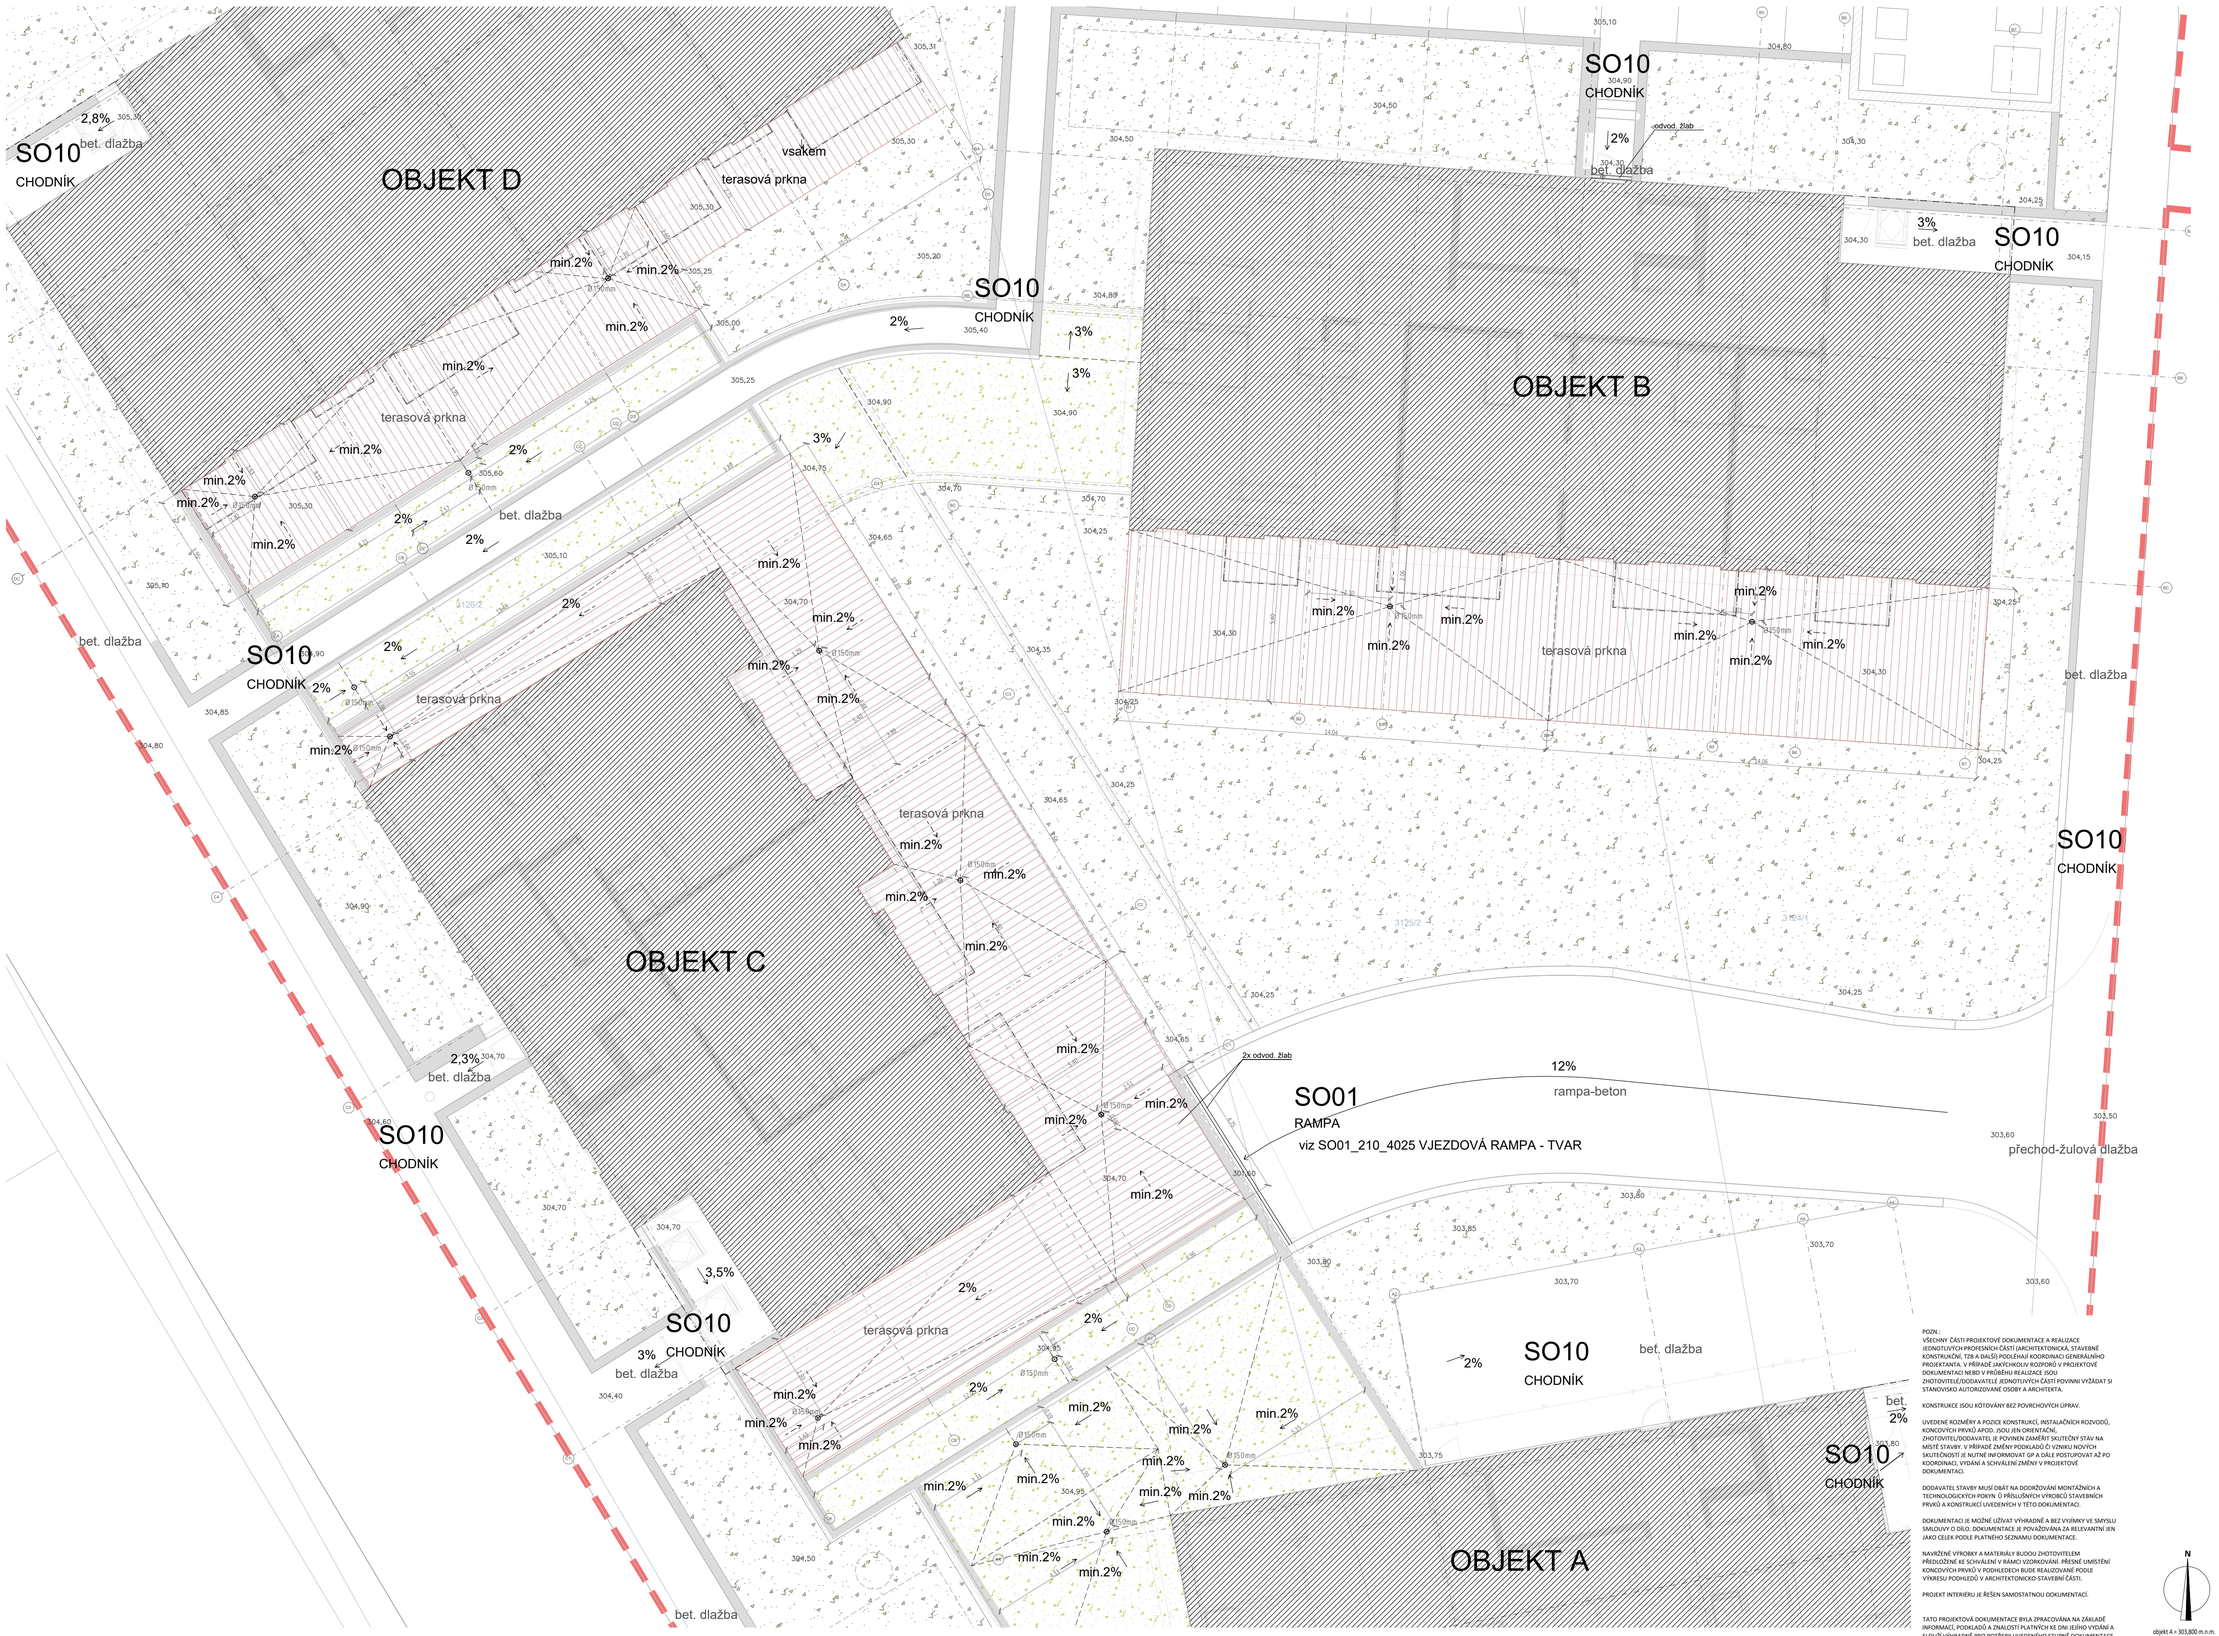

LEGENDA

- HRANICE ŘEŠENÉHO ÚZEMÍ
- KATASTRÁLNÍ HRANICE
- 1818/76 — KATASTRÁLNÍ ČÍSLO
- NAVRHOVANÉ NADZEMNÍ OBJEKTY
- NAVRHOVANÉ PODZEMNÍ OBJEKTY
- HRANICE STAVEBNÍHO OBJEKTU V ÚROVNI ZEMĚ
- 303,62 — VÝŠKOVÁ ÚROVEŇ (m.n.m.) NAVRHOVANÁ
- TRAVNÍ POROST
- ZELENÁ STŘECHA - TRAVNÍ POROST
- TERASA - TERASOVÁ PRKNA (POVRCH F 09)
- ZPEVNĚNÉ PLOCHY, KOMUNIKACE (VIZ SO10)
- NADZEMNÍ OBJEKTY (A, B, C, D) V ÚROVNI 1NP
- min.2% 2% — SKLON ODVODNĚNÍ/POVRCHU

ODVODNĚNÍ POVRCHOVÝCH VOD NA TERASÁCH ŘEŠENO PODKLADNÍ VRSTVOU SE SPÁDOVÝMI KLÍNY DLE VYZNAČENÉHO SKLONU. ROVINU TERAS ZAJIŠŤUJE REKTIFIKACE.

ODVODNĚNÍ POVRCHŮ KOMUNIKACÍ A ZPEVNĚNÝCH PLOCH DLE ČÁSTI KOMUNIKACE, PODÉLNÉ PROFILY, VIZ D_SO10
PLOCHY CHODNÍKŮ NAD SUTERÉNEM JSOU SE SPÁDOVÝMI KLÍNY

ODVODNĚNÍ BALKONŮ A STŘECH VIZ PŘÍSLUŠNÉ PODLAŽÍ D_SO01_...

POZN.:
VŠECHNY ČÁSTI PROJEKTOVÉ DOKUMENTACE A REALIZACE JEDNOTLIVÝCH PROFESNÍCH ČÁSTÍ (ARCHITEKTONICKÁ, STAVEBNĚ KONSTRUKČNÍ, TZB A DALŠÍ) PODLÉHAJÍ KOORDINACI GENERÁLNÍHO PROJEKTANTA. V PŘÍPADĚ JAKÝCHKOLIV ROZPORŮ V PROJEKTOVÉ DOKUMENTACI NEBO V PRŮBĚHU REALIZACE JSOU ZHOTOVITELÉ/DODAVATELÉ JEDNOTLIVÝCH ČÁSTÍ POVINNI VYŽÁDAT SI STANOVISKO AUTORIZOVANÉ OSOBY A ARCHITEKTA.

KONSTRUKCE JSOU KÓTOVÁNY BEZ POVRCHOVÝCH ÚPRAV.

UVEDENÉ ROZMĚRY A POZICE KONSTRUKCÍ, INSTALAČNÍCH ROZVODŮ, KONCOVÝCH PRVKŮ APOD. JSOU JEN ORIENTAČNÍ.
ZHOTOVITEL/DODAVATEL JE POVINEN ZAMĚŘIT SKUTEČNÝ STAV NA MÍSTĚ STAVBY. V PŘÍPADĚ ZMĚNY PODKLADŮ Č VZNIKU NOVÝCH SKUTEČNOSTÍ JE NUTNÉ INFORMOVAT GP A DÁLE POSTUPOVAT AŽ PO KOORDINACI, VYDÁNÍ A SCHVÁLENÍ ZMĚNY V PROJEKTOVÉ DOKUMENTACI.

DODAVATEL STAVBY MUSÍ OBÁT NA DODRŽOVÁNÍ MONTÁŽNÍCH A TECHNOLOGICKÝCH POKYN. Č PŘÍSLUŠÝCH VÝROBCŮ STAVEBNÍCH PRVKŮ A KONSTRUKCÍ UVEDENÝCH V TÉTO DOKUMENTACI.

DOKUMENTACI JE MOŽNÉ UŽÍVAT VÝHRADNĚ A BEZ VYJÍMKY VE SMYSLU SMLOUVY O DÍLO. DOKUMENTACE JE POVAŽOVÁNA ZA RELEVANTNÍ JEN JAKO CELEK PODLE PLATNÉHO SEZNAMU DOKUMENTACE.

NAVRŽENÉ VÝROBKY A MATERIÁLY BUDOU ZHOTOVITELEM PŘEDLOŽENÉ KE SCHVÁLENÍ V RÁMCI VZORKOVÁNÍ. PŘESNÉ UMÍSTĚNÍ KONCOVÝCH PRVKŮ V PODHLEDECH BUDE REALIZOVÁNÉ PODLE VÝKRESU PODHLEDŮ V ARCHITEKTONICKO-STAVEBNÍ ČÁSTI.

PROJEKT INTERIÉRU JE ŘEŠEN SAMOSTATNOU DOKUMENTACÍ.

TATO PROJEKTOVÁ DOKUMENTACE BYLA ZPRACOVÁNA NA ZÁKLADĚ INFORMACÍ, PODKLADŮ A ZNALOSTÍ PLATNÝCH KE DNI JEJÍHO VYDÁNÍ A SLOUŽÍ VÝHRADNĚ PRO POTŘEBY UVEDENÉHO STUPNĚ DOKUMENTACE (NENAHRAZUJE PŘEDCHOZÍ NEBO NÁSLEDUJÍCÍ STUPNĚ). V PŘÍPADĚ ROZPORU MEZI JEDNOTLIVÝMI PŘÍLOHAMI NEBO PROFESNÍMI DÍLY JE POTŘEBNÉ NA TENTO ROZPOR UPOZORNIT A VYŽÁDAT SI OFICIÁLNÍ STANOVISKO GENERÁLNÍHO PROJEKTANTA.

objekt A = 303,800 m.n.m.
objekt B = 304,300 m.n.m.
objekt C = 304,700 m.n.m.
objekt D = 305,300 m.n.m.
výškový systém: Bpv
souřadný systém: JTSK

projekt / project — Číslo zakázky / project number: 185-01

BYTOVÝ SOUBOR LIBUŠE

stupeň dokumentace / design stage

DOKUMENTACE PRO PROVEDENÍ STAVBY — DPS
DETAIL DESIGN DOCUMENTATION — DDD

klient / client
VELTON REAL ESTATE
Na Strži 2102/61a
140 00 Praha 4 - Krč

architekt / architect
adns architekti
A.D.N.S. architekti s.r.o.
Na Příkopě 853/12
110 00 Praha 1 - Nové Město

generální projektant / general designer
ABMV WORLD
ABMV worlď s.r.o.
Prosecká 527/24, 180 00 Praha 8
tel.: +420 731 441 125

projektant / designer
ABMV WORLD
ABMV worlď s.r.o.
Prosecká 527/24, 180 00 Praha 8
tel.: +420 731 441 125

odpovědný projektant / designer: Ing. arch. Zdeněk Vávra
vypracoval / drawn by: Ing. arch. Tomáš Blažek
kontroloval / checked by: Ing. Marek Veselý

revize / revision	popis / description	datum / date

část dokumentace / documentation part: D | DOKUMENTACE OBJEKTŮ A TECHNICKÝCH A TECHNOLOGICKÝCH ZAŘÍZENÍ
stavební objekt / building object: SO01 | BYTOVÝ DŮM
profesní díl / specialist part: 100 | ARCHITEKTONICKO STAVEBNÍ ŘEŠENÍ

název výkresu / drawing title
ODVODNĚNÍ TERAS

datum revize 00 / revision date 00	měřítko / scale	počet A4 / A4 count
15.09.2021	1:100	8 x A4

číslo výkresu / sheet number: 4040
kód výkresu / sheet code: 185-01_DPS_D_SO01_100_4040_R00

paré