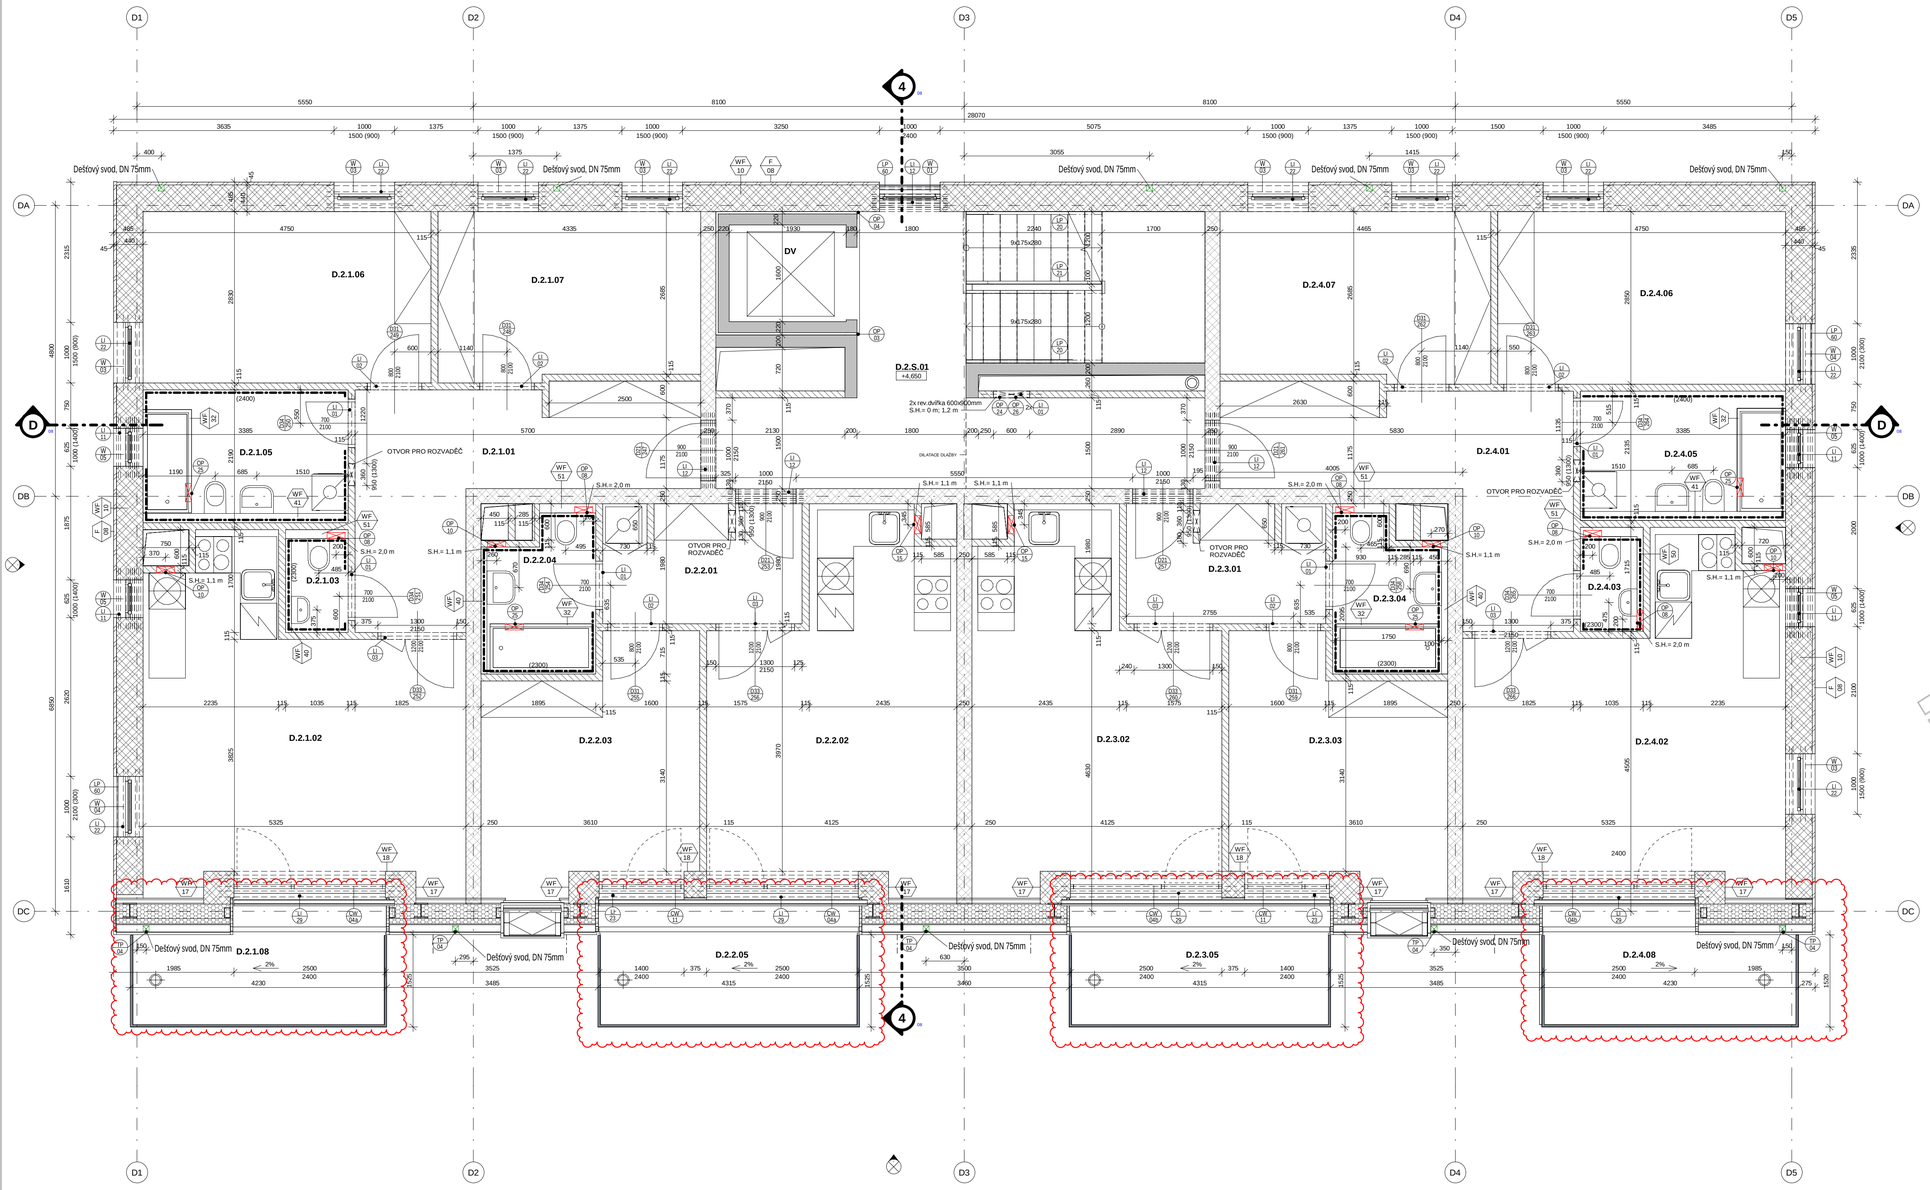

LEGENDA MATERIÁLŮ

- ŽELEZOBETON (WF 21)
- NOSNÉ ZDIVO - KERAMICKÁ TVÁRNICE (WF 10)
- NOSNÉ ZDIVO - AKUSTICKÉ KERAM. TVÁRNICE (WF20)
- PŘÍČKY - KERAMICKÁ TVÁRNICE (WF 3a)
- SDK PŘEDSTĚNY (WF 4a)
- TEPELNÁ IZOLACE - MINERÁLNÍ VATA
- CEMENTOVÉ PÁSKY TERICA (F08)

LEGENDA TAGŮ

XF 01	Označení specifikace skladby a povrchu; značení CF, WF, FF, RF Viz D_01_100_030 - Tabulka specifikace skladeb a povrchů
D01 001	Označení dveří Viz D_01_100_041 - Tabulka dveří
LP 01	Označení zámečnických prvků Viz D_01_100_050 - Tabulka zámečnických prvků
TP 01	Označení klempířských prvků Viz D_01_100_060 - Tabulka klempířských prvků
OP 001	Označení ostatních prvků Viz D_01_100_080 - Tabulka ostatních prvků
W 01	Označení oken Viz D_01_100_040 - Tabulka výplně otvorů
CW 001	Označení prosklených příček Viz D_01_100_040 - Tabulka výplně otvorů

Tabulka místností 2.NP

Č. místnosti	Název	Plocha
D.2.1		
D.2.1.01	CHODBA	13,9 m²
D.2.1.02	OBÝVACÍ POKOJ + KK	24,9 m²
D.2.1.03	WC	1,4 m²
D.2.1.05	KOUPELNA	6,9 m²
D.2.1.06	POKOJ	13,4 m²
D.2.1.07	POKOJ	11,9 m²
D.2.1.08	BALKON	7,9 m²
D.2.1: 7		80,4 m²
D.2.2		
D.2.2.01	CHODBA	6,4 m²
D.2.2.02	OBÝVACÍ POKOJ + KK	21,6 m²
D.2.2.03	POKOJ	13,5 m²
D.2.2.04	KOUPELNA	4,3 m²
D.2.2.05	BALKON	9,2 m²
D.2.2: 5		55,0 m²
D.2.3		
D.2.3.01	CHODBA	6,4 m²
D.2.3.02	OBÝVACÍ POKOJ + KK	21,6 m²
D.2.3.03	POKOJ	13,5 m²
D.2.3.04	KOUPELNA	4,3 m²
D.2.3.05	BALKON	9,2 m²
D.2.3: 5		54,9 m²
D.2.4		
D.2.4.01	CHODBA	14,1 m²
D.2.4.02	OBÝVACÍ POKOJ + KK	25,0 m²
D.2.4.03	WC	1,5 m²
D.2.4.05	KOUPELNA	6,7 m²
D.2.4.06	POKOJ	13,5 m²
D.2.4.07	POKOJ	12,3 m²
D.2.4.08	BALKON	8,0 m²
D.2.4: 7		81,1 m²
Společné prostory		
D.2.S.01	SPOLEČNÁ CHODBA	17,9 m²
Společné prostory: 1		17,9 m²

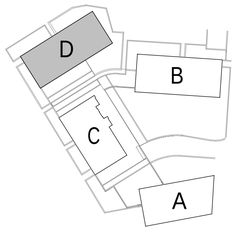

POZN.:
VŠECHNY ČÁSTI PROJEKTOVÉ DOKUMENTACE A REALIZACE JEDNOTLIVÝCH PROFESNÍCH ČÁSTÍ (ARCHITEKTONICKÁ, STAVEBNĚ KONSTRUKČNÍ, TZB A DALŠÍ) PODLÉHAJÍ KOORDINACI GENERÁLNÍHO PROJEKTANTA, V PŘÍPADĚ JAKÝCHKOLIV ROZPORŮ V PROJEKTOVÉ DOKUMENTACI NEBO V PRŮBĚHU REALIZACE JSOU ZHOTOVITELÉ/DODAVATELÉ JEDNOTLIVÝCH ČÁSTÍ POVINNI VYŽÁDAT SI STANOVISKO AUTORIZOVANÉ OSOBY A ARCHITEKTA.

KONSTRUKCE JSOU KÓTOVÁNY BEZ POVRCHOVÝCH ÚPRAV.

UVEDENÉ ROZMĚRY A POZICE KONSTRUKCÍ, INSTALAČNÍCH ROZVODŮ, KONCOVÝCH PRVKŮ APOD. JSOU JEN ORIENTAČNÍ.
ZHOTOVITEL/DODAVATEL JE POVINEN ZAMĚŘIT SKUTEČNÝ STAV NA MÍSTĚ STAVBY. V PŘÍPADĚ ZMĚNY PODKLADŮ ČI VZNIKU NOVÝCH SKUTEČNOSTÍ JE NUTNÉ INFORMOVAT GP A DÁLE POSTUPOVAT AŽ PO KOORDINACI, VYDÁNÍ A SCHVÁLENÍ ZMĚNY V PROJEKTOVÉ DOKUMENTACI.

DODAVATEL STAVBY MUSÍ DBÁT NA DODRŽOVÁNÍ MONTÁŽNÍCH A TECHNOLOGICKÝCH POKYNŮ PŘÍSLUŠNÝCH VÝROBCŮ STAVEBNÍCH PRVKŮ A KONSTRUKCÍ UVEDENÝCH V TÉTO DOKUMENTACI.

DOKUMENTACI JE MOŽNÉ UŽÍVAT VÝHRADNĚ A BEZ VÝJIMKY VE SMYSLU SMLOUVY O DÍLO. DOKUMENTACE JE POVAŽOVÁNA ZA RELEVANTNÍ JEN JAKO CELEK PODLE PLATNÉHO SEZNAMU DOKUMENTACE.

NAVRŽENÉ VÝROBKY A MATERIÁLY BUDOU ZHOTOVITELEM PŘEDLOŽENÉ KE SCHVÁLENÍ V RÁMCI VZORKOVÁNÍ. PŘESNÉ UMÍSTĚNÍ KONCOVÝCH PRVKŮ V PODHLEDECH BUDE REALIZOVANÉ PODLE VÝKRESŮ PODHLEDŮ V ARCHITEKTONICKO-STAVEBNÍ ČÁSTI.

PROJEKT INTERIÉRU JE ŘEŠEN SAMOSTATNOU DOKUMENTACÍ.

TATO PROJEKTOVÁ DOKUMENTACE BYLA ZPRACOVÁNA NA ZÁKLADĚ INFORMACÍ, PODKLADŮ A ZNALOSTÍ PLATNÝCH KE DNI JEJÍHO VYDÁNÍ A SLOUŽÍ VÝHRADNĚ PRO POTŘEBY UVEDENÉHO STUPNĚ DOKUMENTACE (NEBO NAZLEDUJÍCÍ STUPNĚ). V PŘÍPADĚ ROZPORU MEZI JEDNOTLIVÝMI PŘÍLOHAMI NEBO PROFESNÍMI DÍLY JE POTŘEBNÉ NA TENTO ROZPOR UPOZORNIT A VYŽÁDAT SI OFICIÁLNÍ STANOVISKO GENERÁLNÍHO PROJEKTANTA.

N

±0,000 = 303,800 m n. m. Bpv
výškový systém: Bpv
souřadný systém: JTSK

projekt / project — *číslo zakázky / project number:* 185-01

BYTOVÝ SOUBOR LIBUŠE

stupeň dokumentace / design stage

DOKUMENTACE PRO PROVEDENÍ STAVBY — DPS
DETAIL DESIGN DOCUMENTATION — DDD

klient / client

VELTON REAL ESTATE
Na Strži 2102/61a
140 00, Praha 4 - Krč

architekt / architect

adns architekti
A.D.N.S. architekti s.r.o.
Na Příkopě 853/12
110 00 Praha 1 - Nové Město

general projektant / general designer

ABMV WORLD
ABMV world s.r.o.
Prosecká 527/24,180 00 Praha 8
tel.: +420 731 441 125

projektant / designer

ABMV WORLD
ABMV world s.r.o.
Prosecká 527/24,180 00 Praha 8
tel.: +420 731 441 125

odpovědný projektant / designer
Ing. arch. Zdeněk Vávra

vypracoval / drawn by
Ing. Lukáš Vojta

kontroloval / checked by
Ing. Marek Veselý

revize / revision	*popis / description*	*datum / date*
01	Spádování balkónů	30.11.2021

část dokumentace / documentation part
D | DOKUMENTACE OBJEKTŮ A TECHNICKÝCH A TECHNOLOGICKÝCH ZAŘÍZENÍ

stavební objekt / building object
SO01 | BYTOVÝ DŮM

profesní díl / specialist part
140 | ARCHITEKTONICKO-STAVEBNÍ ŘEŠENÍ, OBJEKT D - NADZEMNÍ ČÁST

název výkresu / drawing title
OBJEKT D - Půdorys 2 .NP

datum revize 00 / revision date 00	*měřítko / scale*	*počet A4 / A4 count*
15/09/2021	1:50	8 x A4

číslo výkresu / sheet number 4420

kód výkresu / sheet code 185-01_DPS_D_SO01_140_4420_01

paré