


PŪDORYS 1:200

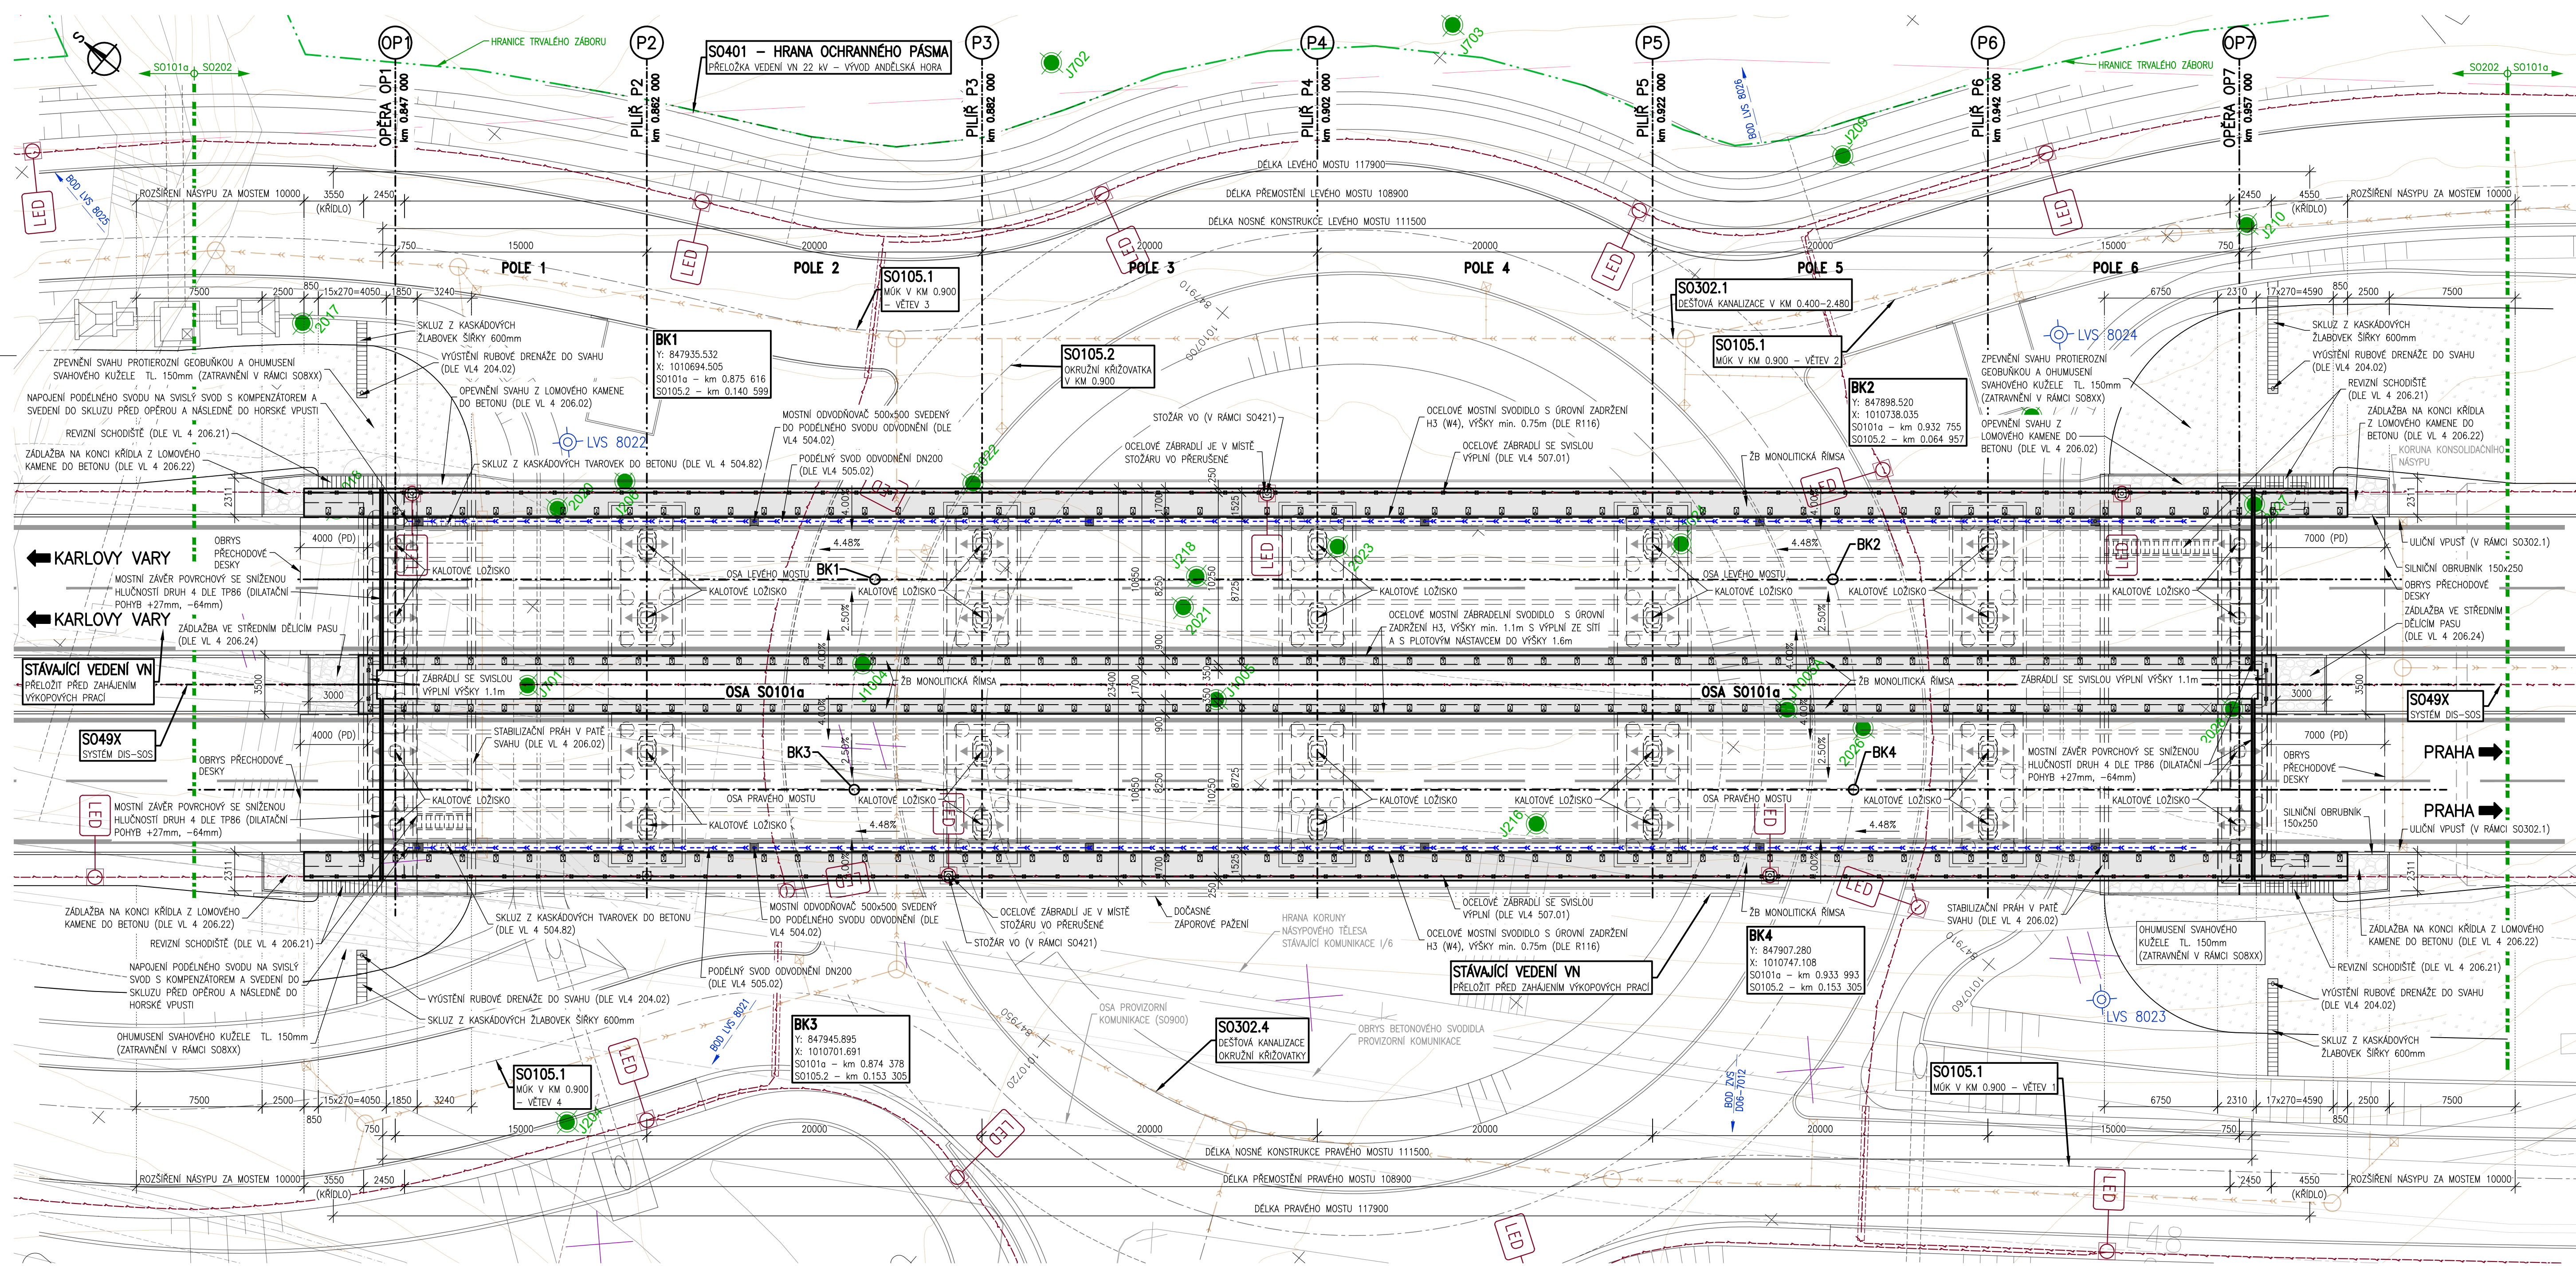

SOUVISEJÍCÍ OBJEKTY:

50	101a	SILNICE 1/6 KAPALÝ VÁRY – OLŠOVÁ VRATA
50	101b	MŮK V KM 0,900
50	105,2	KROUŽKOVÁNÍ V KM 0,900
50	102,1	SVLÉK A VODOVODNÉ DOPRAVNÍ ZNAČENÍ – SIL. I/6
50	302,1	DEŠŤOVÁ KANALIZACE KM 0,400 – 2,480
50	302,4	DEŠŤOVÁ KANALIZACE KROUŽKOVÁNÍ KŘÍŽOVATKY (STARÁ KYSELKÁ)
50	401	PŘELOŽKA VEDENÍ VN 22 KV – VÝVOD KYSELKÁ HORA
50	421	VEŘEČNÉ OSYĚLENÍ KM 0,0 – 1,000
50	491	VÝSTĚM DIS-SOS – KABLOVÉ VEDENÍ
50	494	SYSTÉM DIS-SOS – TRUBKY PRO OPTICKÉ KABELY
50	498	SYSTÉM DIS-SOS – OPTICKÉ KABELY RSD
50	801,1	VEGETAČNÍ ÚPRAVY – SIL. I/6
50	901,1	PŘECHODNÉ DOPRAVNÍ ZNAČENÍ – SIL. I. TŘÍDY

MATERIÁLÝ:

BETON:
(DLE ČSN EN 206+A2 A TKP 18)

PODKLADNÍ BETON
PÍLAŽNÍ ŠABLONA OPĚRY OP1
VRÁTNE OPĚRY
ZAKLAD OPĚRY
ZAKLADY PÍLŘŮ P2, P4, P5, P6
ZAKLAD PÍLŘŮ P3
MOŠTNÍ OPĚRY
PÍLŘE P2, P3 P5, P6
PÍLŘ P4
NOSNÁ KONSTRUKCE
DOBĚTAVNÁ KAPES MŮZ A PŘE
PŘECHODOVÁ DESKA
ŘÍMSA
SCHODIŠTĚVÉ STUPNĚ MONOLITICKÉ
SILNICNÍ OBRUBNÍKY POĐEL KOM.
KASKADOVĚ SKLIZOVÉ TVARVNICE
BETONOVÉ PRAHY V PATE SVAHU
PODKLADNÍ BETON POD DLAŽBU
LOŽE PRO OBRUBNÍKY
LOŽE PRO OSLUŽNÉ SCHODIŠTĚ
DRENÁŽNÍ BETON

C12/15 X0
C16/20 X0
C30/37 XA2
C25/30 XF1
C25/30 XF1
C25/30 XF3
C30/37 XF4
C35/45 XF4
C35/45 XF2
C30/37 XF4
C25/30 XF2
C30/37 XF4
C30/37 XF4
Min. C30/37 XF
Min. C30/37 XF
C25/30 XF3
C20/25n XF3
C20/25n XF3
C20/25n XF3
MCB

BETONÁŘSKÁ VÝZTU
(DLE ČSN EN 10080 A ČSN 42 0139)
VÁZANÁ BETONÁŘSKÁ VÝZTUŽ
SVAŘOVANÉ SÍTĚ

PŘEDPÍNACÍ VÝZTUŽ

DODATEČNĚ PŘEDPÍNANÉ KABELY (19 LAN) Y1860 S7-15.

4) Y1860 S7-15.
2 DLE ČSN EN

D

PDPS

OBJEDNATEL ŘEDITELSTVÍ SILNIC A DÁLNIC s. p. ČERČANSKÁ 12, 140 00 PRAHA 4 STAVBU ZAJIŠŤUJE: SPRÁVA KARLOVY VARY, ZÁVODNÍ 82, 360 06 KARLOVY VARY	 ŘEDITELSTVÍ SILNIC A DÁLNIC
ZHOTOVITEL Morava - RD velké zakázky FIDIC 2023 VEDOUČÍ SDRUŽENÍ: VIAPONT s.r.o., VODNÍ 13, 602 00 BRNO	ČLENOVÉ SDRUŽENÍ: Stráský, Husty a partneři s.r.o. SHB, akciová společnost DOPRAVOPROJEKT Ostrava a.s. PK OSSENDORF s.r.o. G-Consult, spol. s r.o. Mott MacDonald CZ, spol. s r.o. METROPROJEKT Praha a.s.
HLAVNÍ PROJEKTANT VIAPONT s.r.o. VODNÍ 13, 602 00 BRNO HLAVNÍ INŽENÝR PROJEKTU ING. IVO FISCHER	 PROJEKČNÍ A INŽENÝRSKÁ KANCELÁŘ VODNÍ 13, 602 00 BRNO ČÍSLO ZAKÁZKY 2550-01

D.1.2.1 SO202 Most na sil. I/6 v km 0,900

SOURADNICOVÝ SYSTÉM: S-JTSK		VÝŠKOVÝ SYSTÉM: Bpvs		
VEDOUcí PROJEKTANT	ING. IVAN KUŠÁK			
ZODPOVĚDNÝ PROJEKTANT	ING. JAN MACÁK			
VYPRACOVAL	ING. JAN MACÁK			
KONTROLOVAL	ING. IVAN KUŠÁK		PROJEKČNÍ A INŽENÝRSKÁ KANCELÁŘ VODNÍ 13, 602 00 BRNO	
KRAJ: KARLOVSKÝ		OBEC: KARLOVY VARY, ANDELSKÁ HORA	STUPEŇ	PDPŠ
NÁZEV STAVBY:			DÁTUM	ŘÍJEN 2025
D6 KARLOVY VARY - OLŠOVÁ VRATA			FORMÁT	10 A4
			MĚŘÍTKO	1 : 200
			Č. ZAKÁZKY	2550-01
			ARCHIVNÍ Č.	
NÁZEV PŘÍLOHY:			Č. SOUPRAVY:	Č. PŘÍLOHY:
PŮDORYS				03