PODÉLNÝ ŘEZ – PRAVÝ MOST 1:200

ŘEZ JE VEDEN OSOU LEVÉHO (VNITŘNÍHO) TRÁMU
(VÝŠKOVÉ KÓTY HORNÍHO POVRCHU VOZOVKY JSOU VZTAŽENY K NIVELETĚ MOSTU)

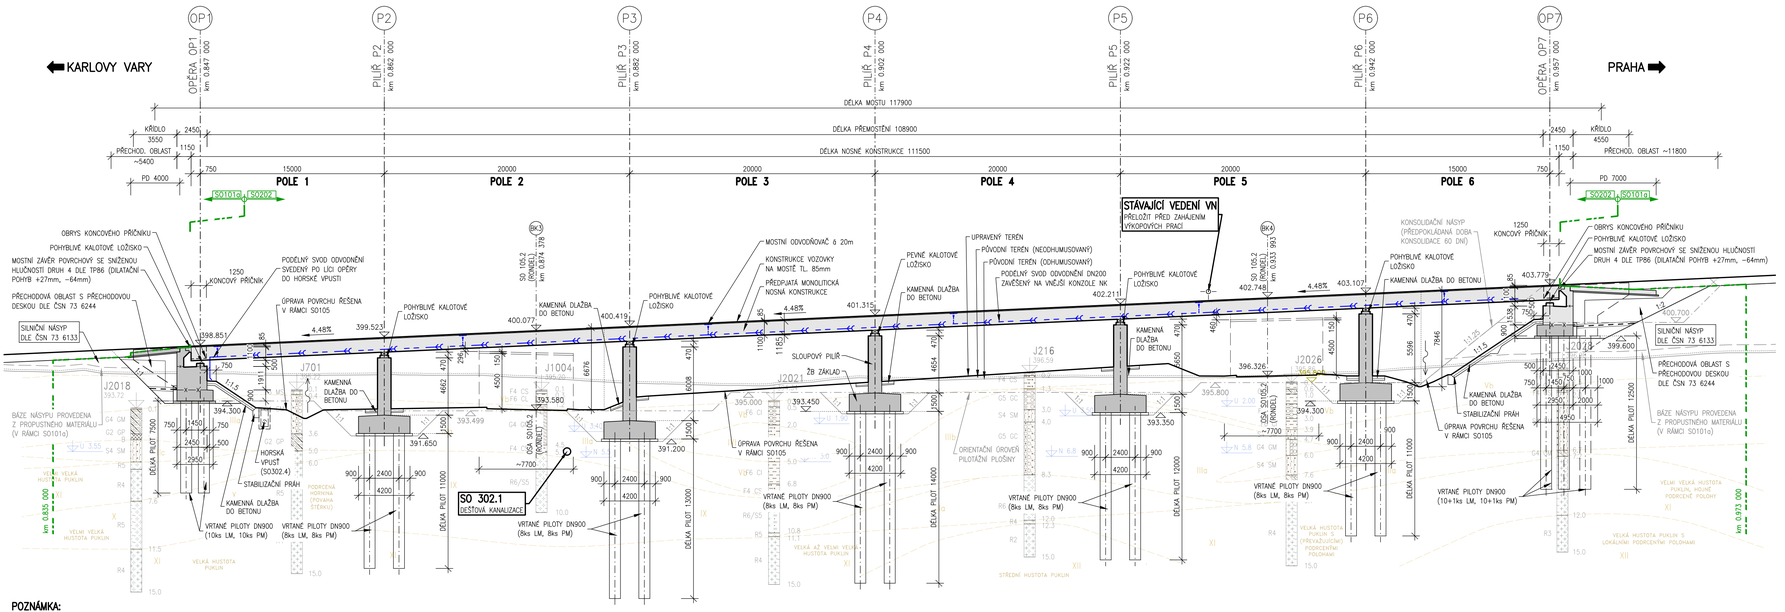

POZNÁMKA:
ÚPRAVY POVRCHU POD MOSTEM JSOU, MIMO ZPEVNĚNÍ SVAHU KOLEM OPĚRY A PILÍŘŮ ŘEŠENY V RÁMCI SO105.

MATERIÁLY:

BETON:

(DLE ČSN EN 206+A2 A TKP 18)

PODKLADNÍ BETON	C12/15 X0
PILOTÁŽNÍ ŠABLONA OPĚRY OP1	C16/20 X0
VRTANÉ PILOTY	C30/37 XA2
ZÁKLAD OPĚRY	C25/30 XF1
ZÁKLADY PILÍŘŮ P2, P4, P5, P6	C25/30 XF1
ZÁKLAD PILÍŘE P3	C25/30 XF3
MOSTNÍ OPĚRY	C30/37 XF4
PILÍŘE P2, P3 P5, P6	C35/45 XF4
PILÍŘ P4	C35/45 XF2
NOSNÁ KONSTRUKCE	C35/45 XF2
DOBETONÁVKA KAPES MOZ A PŘEDPĚTÍ	C30/37 XF4
PŘECHODOVÁ DESKA	C25/30 XF2
ŘÍMSA	C30/37 XF4
SCHODIŠŤOVÉ STUPNĚ MONOLITICKÉ	C30/37 XF4
SILNIČNÍ OBRUBNÍKY PODÉL KOM.	Min. C30/37 XF4
KASKÁDOVITÉ SKLUZOVÉ TVÁRNICE	Min. C30/37 XF4
BETONOVÉ PRAHY V PATĚ SVAHU	C25/30 XF3
PODKLADNÍ BETON POD DLAŽBU	C20/25n XF3
LOŽE PRO OBRUBNÍKY	C20/25n XF3
LOŽE PRO OBSLUŽNÉ SCHODIŠTĚ	C20/25n XF3
DRENÁŽNÍ BETON	MCB

BETONÁŘSKÁ VÝZTUŽ:

(DLE ČSN EN 10080 A ČSN 42 0139)

VÁZANÁ BETONÁŘSKÁ VÝZTUŽ	B500B
SVAŘOVANÉ SÍTĚ	B500A

PŘEDPÍNACÍ VÝZTUŽ:

(DLE ČSN EN 10138)

DODÁTEČNĚ PŘEDPÍNANÉ KABELY (19 LAN) Y1860 S7–15.7

- STUPEŇ PROTIKOROZNÍ OCHRANY PL2 DLE ČSN EN 1992–2, TABULKA NA.3.

SOUVISEJÍCÍ OBJEKTY:

SO 101a	SILNICE I/6 KARLOVY VARY – OLŠOVÁ VRATA
SO 105.1	MÍK V KM 0,900
SO 105.2	OKRUŽNÍ KŘIŽOVATKA V KM 0,900
SO 120a.1	SVISLÉ A VODOROVNÉ DOPRAVNÍ ZNAČENÍ – SIL. I/6
SO 302.1	DEŠŤOVÁ KANALIZACE KM 0,400 – 2,480
SO 302.4	DEŠŤOVÁ KANALIZACE OKRUŽNÍ KŘIŽOVATKY (STARÁ KYSIBELSKÁ)
SO 401	PŘELOŽKA VEDENÍ VN 22 KV – VÝVOD ANDĚLSKÁ HORA
SO 421	VEŘEJNÉ OSVĚTLENÍ KM 0,0 – 1,000
SO 491	SYSTÉM DIS–SOS – KABELOVÉ VEDENÍ
SO 494	SYSTÉM DIS–SOS – TRUBKY PRO OPTICKÉ KABELY
SO 498	SYSTÉM DIS–SOS – OPTICKÉ KABELY ŘSD
SO 801.1	VEGETAČNÍ ÚPRAVY – SIL. I/6
SO 901.1	PŘECHODNÉ DOPRAVNÍ ZNAČENÍ – SIL. I. TŘÍDY

SKLADBA KONSTRUKCE VOZOVKY

SKLADBA KONSTRUKCE VOZOVKY NA MOSTĚ:

ASFALTOVÝ KOBEREC MASTIXOVÝ	SMA 11S	40mm
SPOJOVACÍ POSTŘIK	PS–CP	0,35kg/m²
LITÝ ASFALT MODIFIKOVANÝ	MA 11IV	40mm
NAIP NA PEČETÍCÍ VRSTVU		5mm
CELKEM		**85mm**

SKLADBA KONSTRUKCE VOZOVKY NA PŘEDPOLÍ:

ASFALTOVÝ KOBEREC MASTIXOVÝ	SMA 11S	40mm
SPOJOVACÍ POSTŘIK	PS–CP	0,35kg/m²
ASFALTOVÝ BETON PRO LOŽNÉ VRSTVY	AC L 22S	80mm
SPOJOVACÍ POSTŘIK	PS–CP	0,35kg/m²
ASFALTOVÝ BETON S VYS. MOD. TUHOSTÍ	VMT 22	120mm
INFILTRAČNÍ POSTŘIK	Pi–C	0,60kg/m²
MECHANICKY ZPEVNĚNÉ KAMENIVO	MZK 0/32 G_A	150mm
ŠTĚRKODRŤ	$Š\check{D}_A$	250mm
CELKEM		**640mm**

D

PDPS

OBJEDNATEL
ŘEDITELSTVÍ SILNIC A DÁLNIC s. p.
ČERČANSKÁ 12, 140 00 PRAHA 4
STAVBU ZAJIŠŤUJE:
SPRÁVA KARLOVY VARY, ZÁVODNÍ 82, 360 06 KARLOVY VARY

ŘEDITELSTVÍ SILNIC A DÁLNIC

ZHOTOVITEL
Morava - RD velké zakázky FIDIC 2023
VEDOUCÍ SDRUŽENÍ:
VIAPONT s.r.o., VODNÍ 13, 602 00 BRNO

ČLENOVÉ SDRUŽENÍ:
Stráský, Husty a partneři s.r.o.
SHB, akciová společnost
DOPRAVOPROJEKT Ostrava a.s.
PK OSSENDORF s.r.o.
G-Consult, spol. s r.o.
Most MacDonald CZ, spol. s r.o.
METROPROJEKT Praha a.s.

HLAVNÍ PROJEKTANT
VIAPONT s.r.o.
VODNÍ 13, 602 00 BRNO
HLAVNÍ INŽENÝR PROJEKTU
ING. IVO FISCHER

VIAPONT PROJEKČNÍ A INŽENÝRSKÁ KANCELÁŘ VODNÍ 13, 602 00 BRNO
ČÍSLO ZAKÁZKY 2550-01

D.1.2.1 SO202 Most na sil. I/6 v km 0,900

SOUŘADNICOVÝ SYSTÉM: S-JTSK
VÝŠKOVÝ SYSTÉM: Bpv

VEDOUCÍ PROJEKTANT	ING. IVAN KUSÁK	
ZODPOVĚDNÝ PROJEKTANT	ING. JAN MAČÁK	
VYPRACOVAL	ING. JAN MAČÁK	
KONTROLOVAL	ING. IVAN KUSÁK	

VIAPONT PROJEKČNÍ A INŽENÝRSKÁ KANCELÁŘ VODNÍ 13, 602 00 BRNO

KRAJ: KARLOVARSKÝ | OBEC: KARLOVY VARY, ANDĚLSKÁ HORA

NÁZEV STAVBY:
D6 KARLOVY VARY - OLŠOVÁ VRATA

NÁZEV PŘÍLOHY:
PODÉLNÝ ŘEZ - PRAVÝ MOST

STUPEŇ	PDPS
DATUM	ŘÍJEN 2025
FORMÁT	5 A4
MĚŘÍTKO	1 : 200
Č. ZAKÁZKY	2550-01
ARCHIVNÍ Č.	
Č. SOUPRAVY:	Č. PŘÍLOHY: 04.2