


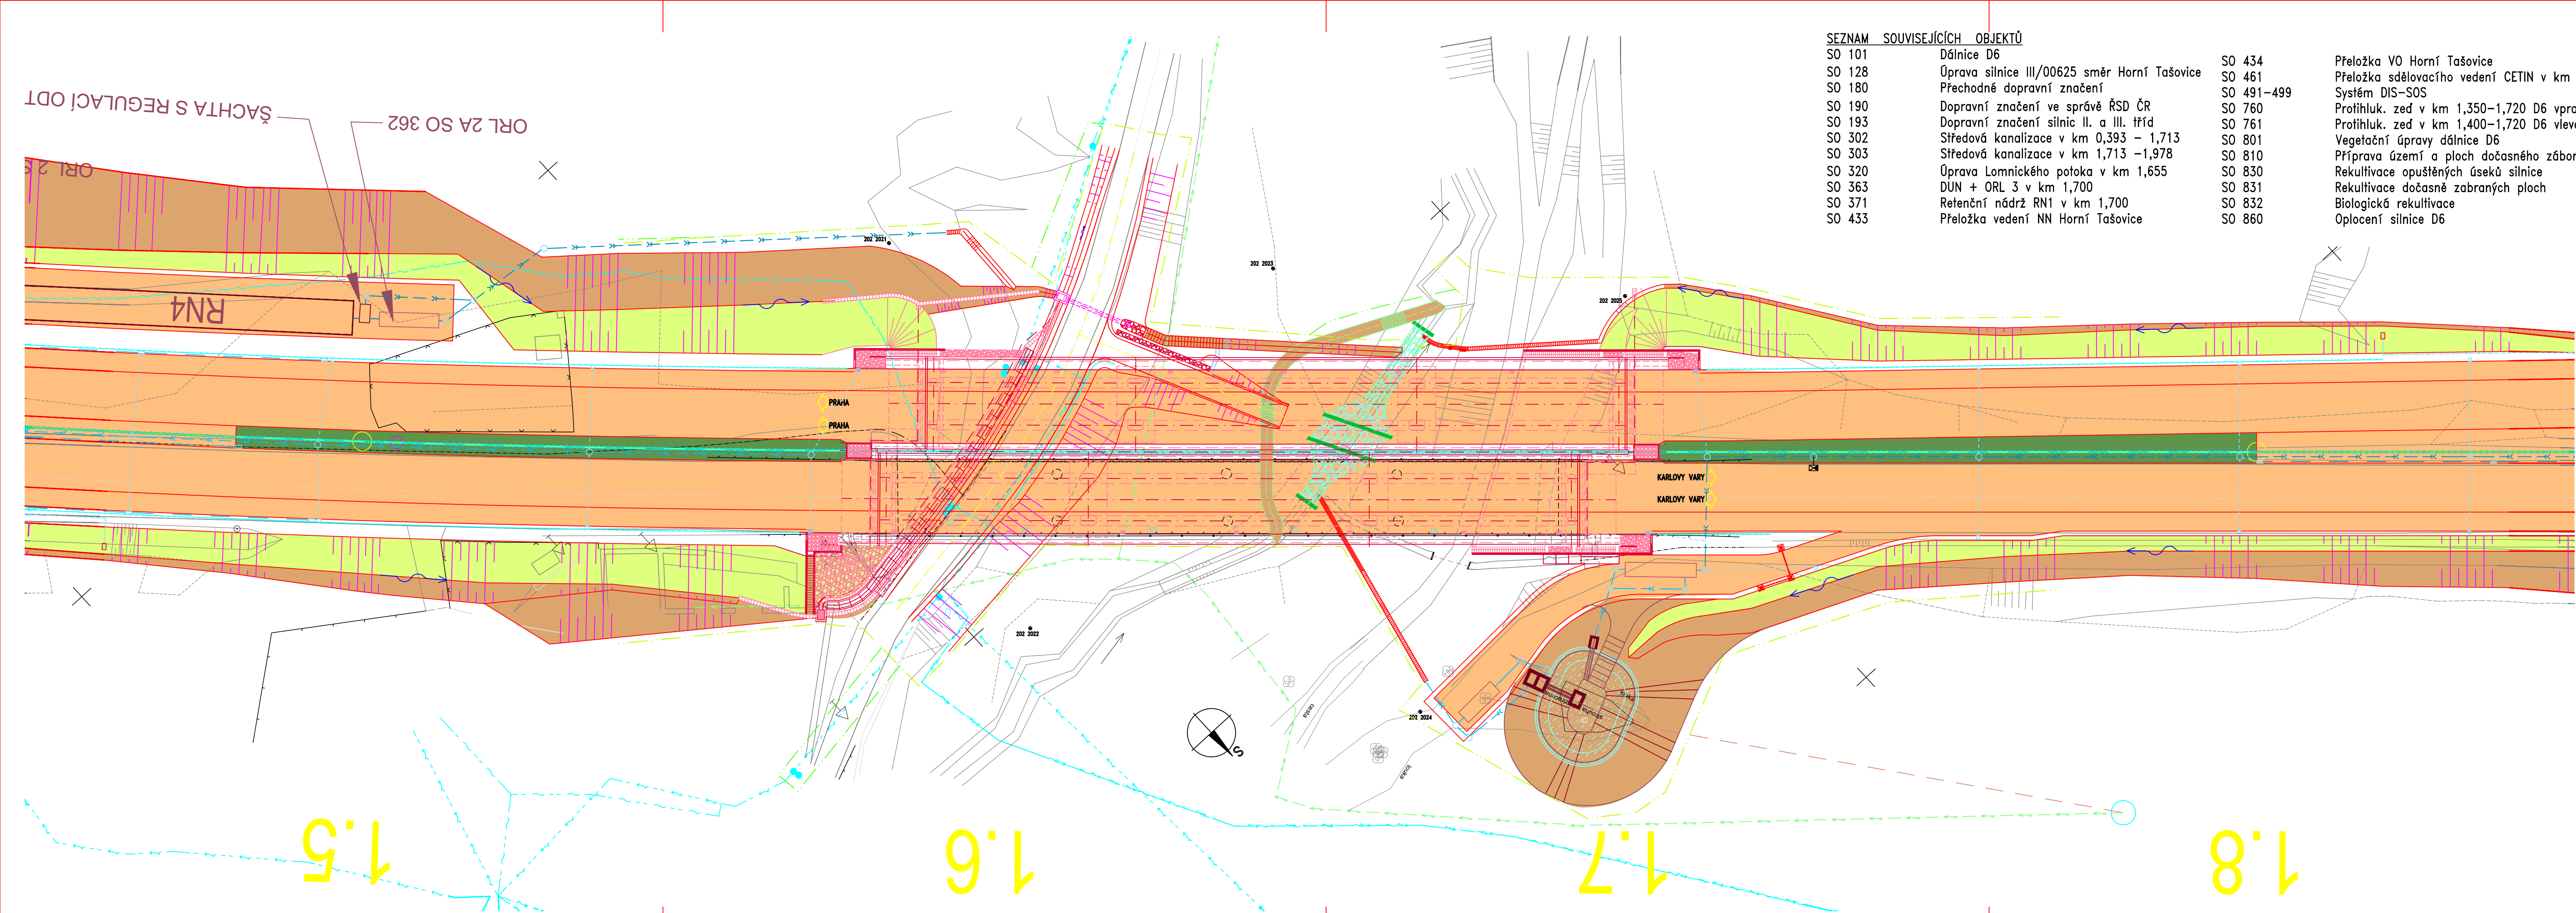

SEZNAM	SOUVISEJÍCÍCH	OBJEKTŮ
SO 101	Dálnice D6	
SO 128	Úprava silnice III/00625 směr Horní Tašovice	
SO 180	Přechodné dopravní značení	
SO 190	Dopravní značení ve správě ŘSD ČR	
SO 193	Dopravní značení silnic II. a III. tříd	
SO 302	Středová kanalizace v km 0,393 – 1,713	
SO 303	Středová kanalizace v km 1,713 – 1,978	
SO 320	Úprava Lomnického potoka v km 1,655	
SO 363	DUN + ORL 3 v km 1,700	
SO 371	Retenční nádrž RN1 v km 1,700	
SO 433	Přeložka vedení NN Horní Tašovice	

SO 434	Přeložka VO Horní Tašovice
SO 461	Přeložka sdělovacího vedení CETIN v km 0,000–1,600
SO 491–499	Systém DIS–SOS
SO 760	Protihluk. zeď v km 1,350–1,720 D6 vpravo
SO 761	Protihluk. zeď v km 1,400–1,720 D6 vlevo
SO 801	Vegetační úpravy dálnice D6
SO 810	Příprava území a ploch dočasného záboru
SO 830	Rekultivace opuštěných úseků silnice
SO 831	Rekultivace dočasně zabraných ploch
SO 832	Biologická rekultivace
SO 860	Oplocení silnice D6

ČÁST D.2

SO 202

Souřadnicový systém S–JTSK, Výškový systém Bpv



ŘEDITELSTVÍ
SILNIC
A DÁLNIC

ČISTOPIS

Objednatel:
ŘEDITELSTVÍ SILNIC A DÁLNIC s. p.
Čerčanská 2023/12
140 00 Praha 4 – Krč

Zhotovitel PD: PRAGOPROJEKT, a.s., K Rysánc 1668/16, 147 54 Praha 4, IČO: 45272387, www.pragoprojekt.cz, datová schránka: 4kif54

Navštívil/propracoval: Ing. Karolína Hédová podpis: <i>K. Hédová</i>	Zodpovědný projektant: Ing. Martin BLATSKÝ podpis: <i>M. Blatský</i>	Zástupce zodpovědného projektanta: Ing. Jan BAZIL podpis: <i>J. Bazil</i>
Technická kontrola: Ing. Kamil PEJCHAL podpis: <i>K. Pejchal</i>	Hlavní inženýr projektu: Ing. Pavel ŠLAPA podpis: <i>P. Šlapa</i>	Zástupce hlavního inženýra projektu: Ing. Radovan STANKOVEN podpis: <i>R. Stankoven</i>



Kraj:	KARLOVARSKÝ KRAJ	Číslo zakázky:	25–150–2
Místo stavby:	OLŠOVÁ VRATA, ANDELSKÁ HORA, ŽALMANOV, HORNÍ TAŠOVICE, BOCHOV	Číslo akce:	05–219
Objednatel:	ŘSD s. p., Čerčanská 2023/12, 140 00 Praha 4, IČO 65993390	Datum:	03/2026
Název stavby:	D6 OLŠOVÁ VRATA-ŽALMANOV, VD-ZDS	Formát:	
Objekt:	Most na D6 přes Lomnický potok v km 1,600 SO 101	Měřítko:	
Příloha:	SITUACE	Stupeň:	
		PDPs	
		Číslo přílohy:	02

Souprava:	
-----------	--