


PŮDORYS 1:250

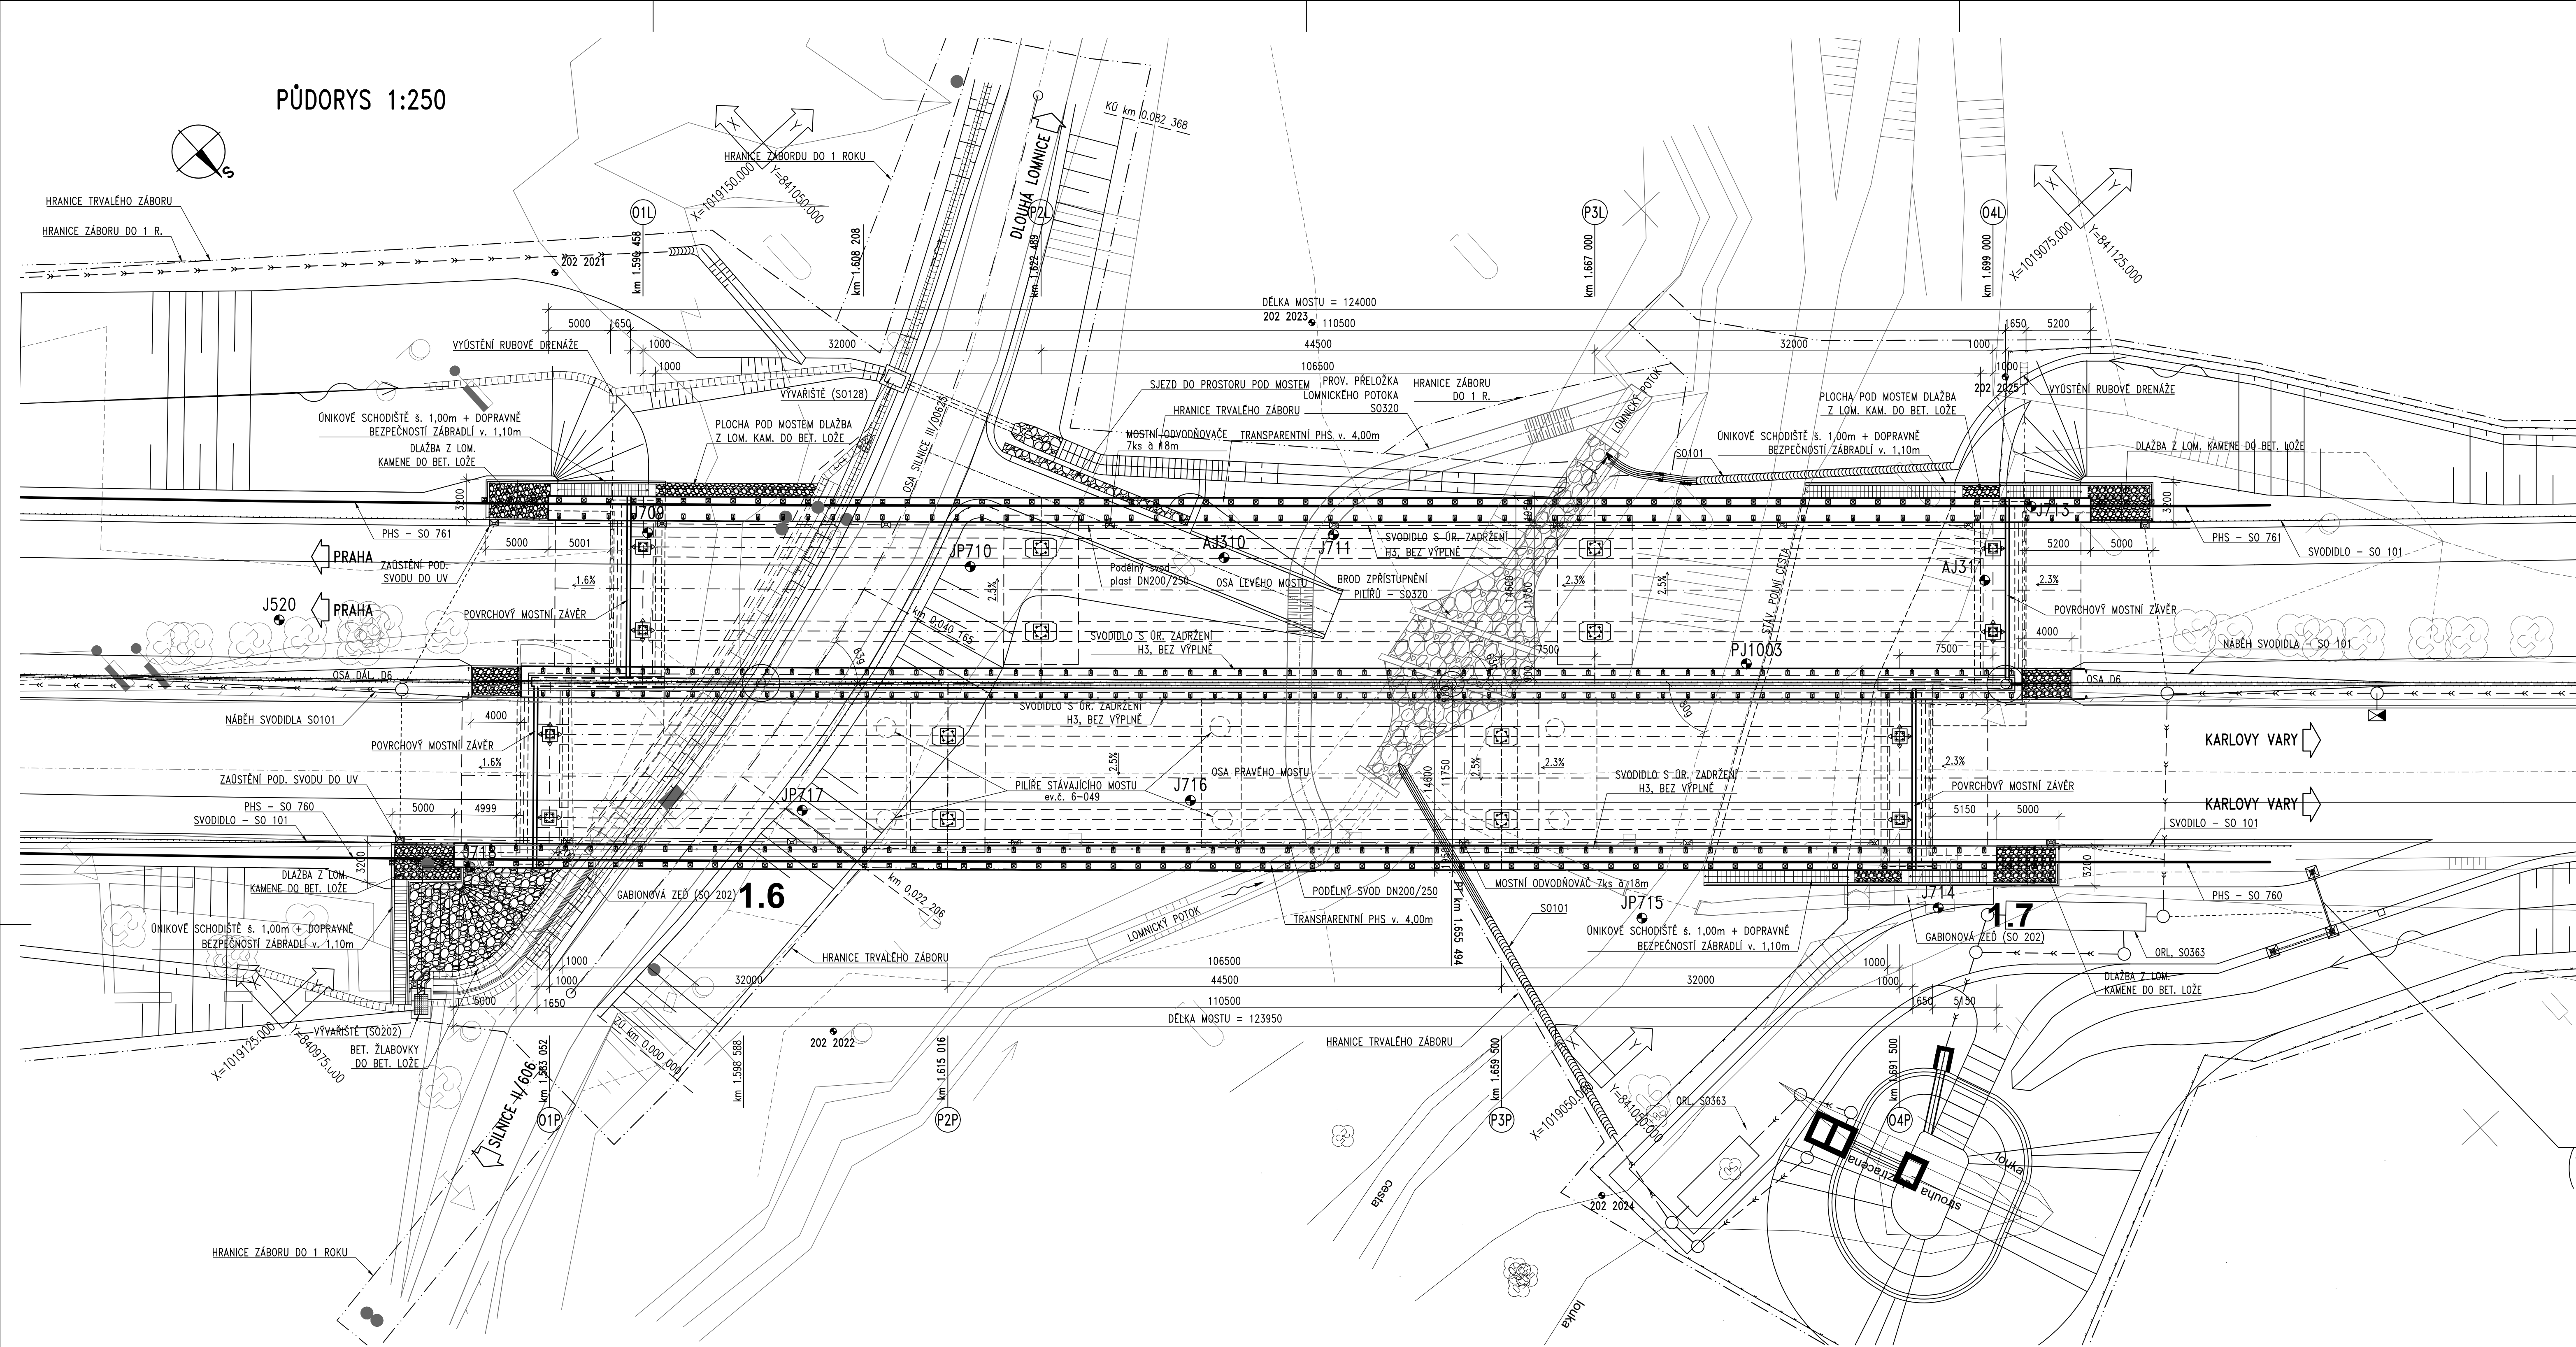

ČÁST D.2
SO 202

ČISTOPIS

Souřadnicový systém S-JTSK, Výškový systém Bpv



ŘEDITELSTVÍ
SILNIC
A DÁLNIC

ŘEDITELSTVÍ SILNIC A DÁLNIC s. p.
Čertanská 2023/12
140 00 Praha 4 – Krč

Zhotovitel PD: PRAGOPROJEKT, a.s., K Rybáře 1668/16, 147 54 Praha 4, IČO: 45272387, www.pragoprojekt.cz, datová schránka: 4klf54			
Naměřil/vypracoval: Ing. Karolína HEDVÁ podpis: <i>K. Hedvá</i>	Zodpovědný projektant: Ing. Martin BLATSKÝ podpis: <i>M. Blatský</i>	Zatvrdil zodpovědného projektanta: Ing. Jan BAZIL podpis: <i>J. Bazil</i>	
Technická kontrola: Ing. Kamel PEJCHAL podpis: <i>K. Pejchal</i>	Hlavní inženýr projektu: Ing. Pavel SLAPA podpis: <i>P. Slapa</i>	Zatvrdil hlavního inženýra projektu: Ing. Radovan STANKOVEN podpis: <i>R. Stankoven</i>	

Kraj: KRALOVSKÝ KRAJ	Číslo zakázky: 25-150-2
Místo stavby: OLŠOVÁ VRATA, ANEŠKÁ HORA, ŽALMANOV, HORNÍ TAŠOVICE, BOCHOV	Číslo akce: 05-219
Objednatel: RSD s. p., Čertanská 2023/12, 140 00 Praha 4, IČO 65993390	Datum: 03/2026
Název stavby: D6 OLŠOVÁ VRATA-ŽALMANOV, VD-ZDS	Formát: MAPA: Stupeň: PDPS
Objekt: MOST NA D6 PŘES LOMNICKÝ POTOK V KM 1,600 SO101	Číslo přílohy: 03
Příloha: PŮDORYS A TERÉNNÍ ÚPRAVY	