


VZOROVÝ PŘÍČNÝ ŘEZ 1:50

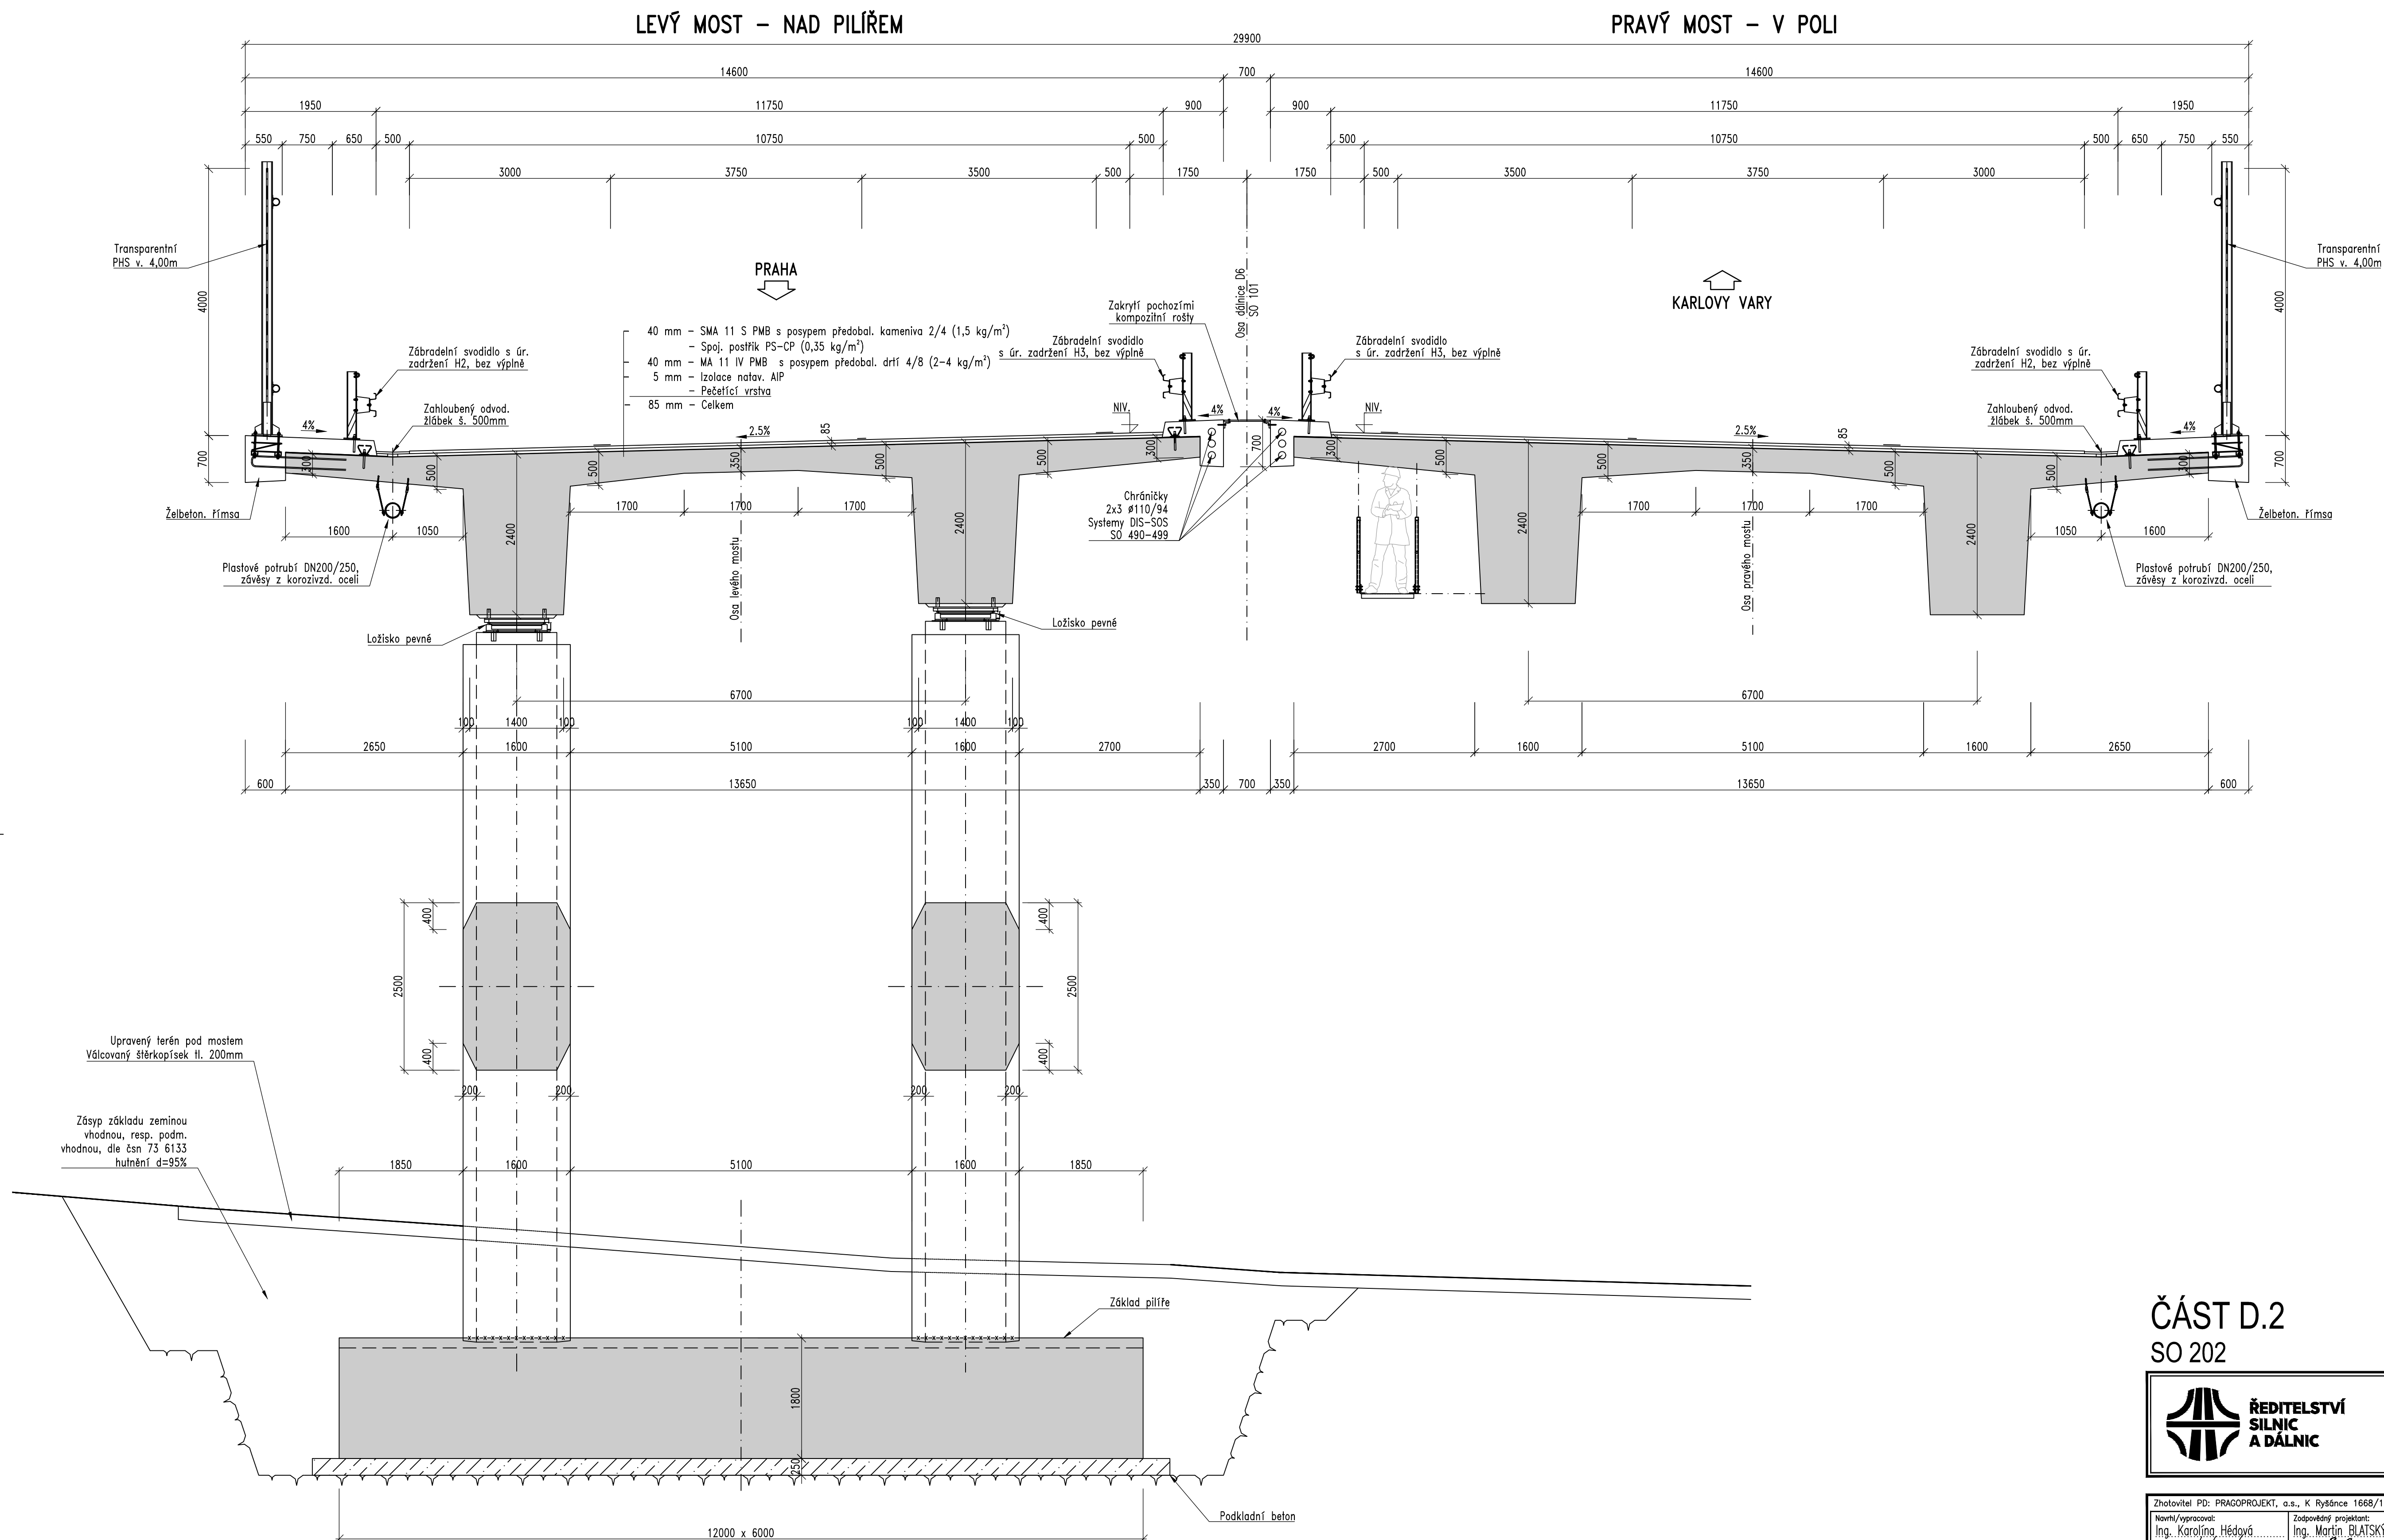

ČÁST D.2
SO 202

ČISTOPIS

Souřadnicový systém S-JTSK, Výškový systém Bp

Objednatel



ŘEDITELSTVÍ SILNIC A DÁLNIC

ŘEDITELSTVÍ SILNIC A DÁLNIC s.
Čerčanská 2023/12
140 00 Praha 4 – Krč

Zhotovitel: PD PRAGOPROJEKT, s.a., K Rybáře 1668/16, 147 54 Praha 4, IČO: 45272387, www.pragoprojekt.cz, datová schránka: 4kfrfz		Zastupitel zodpovědný projektanta:	
Nařízení/organizoval: Ing. Karolína Hédváb podpis: <i>Karolína Hédváb</i>	Zodpovědný projektant: Ing. Martin BLATSKÝ podpis: <i>M. Blatský</i>	Ing. Jan BAZIL podpis: <i>Jan Bazil</i>	
Technická kontrola: Ing. Kamil PEJCHAL podpis: <i>Kamil Pejchal</i>	Hlavní inženýr projektu: Ing. Pavel ŠLAPÁ podpis: <i>Pavel Šlapá</i>	Zástupce hlavního inženýra projektu: Ing. Radovan ŠTANKOVEN podpis: <i>Radovan Štankoven</i>	
			



PRAGOPROJE

Kraj:	KARLOVARSKÝ KRAJ	Číslo zakázky:	25-150-2
Místo stavby:	OLŠOVÁ VRATA, ANDĚLSKÁ HORA, ŽALMANOV, HORNÍ TÁBOŘICE, BOCHOV	Číslo díce:	05-219
Objednatel:	RSD s. p., Čerčanská 2023/12, 140 00 Praha 4, IČO 65993390	Datum:	03/2026
Název stavby:		Formát:	
		MAPInfo:	
		Stupeň:	
Objekt:	MOST NA D6 PŘES LOMNICKÝ POTOK V km 1,600 SO101	PDPS	
Příloha:		Číslo přílohy:	05
	VZOROVÝ PŘÍČNÝ ŘEZ		