



PILÍŘE P2L, P2P 1:100

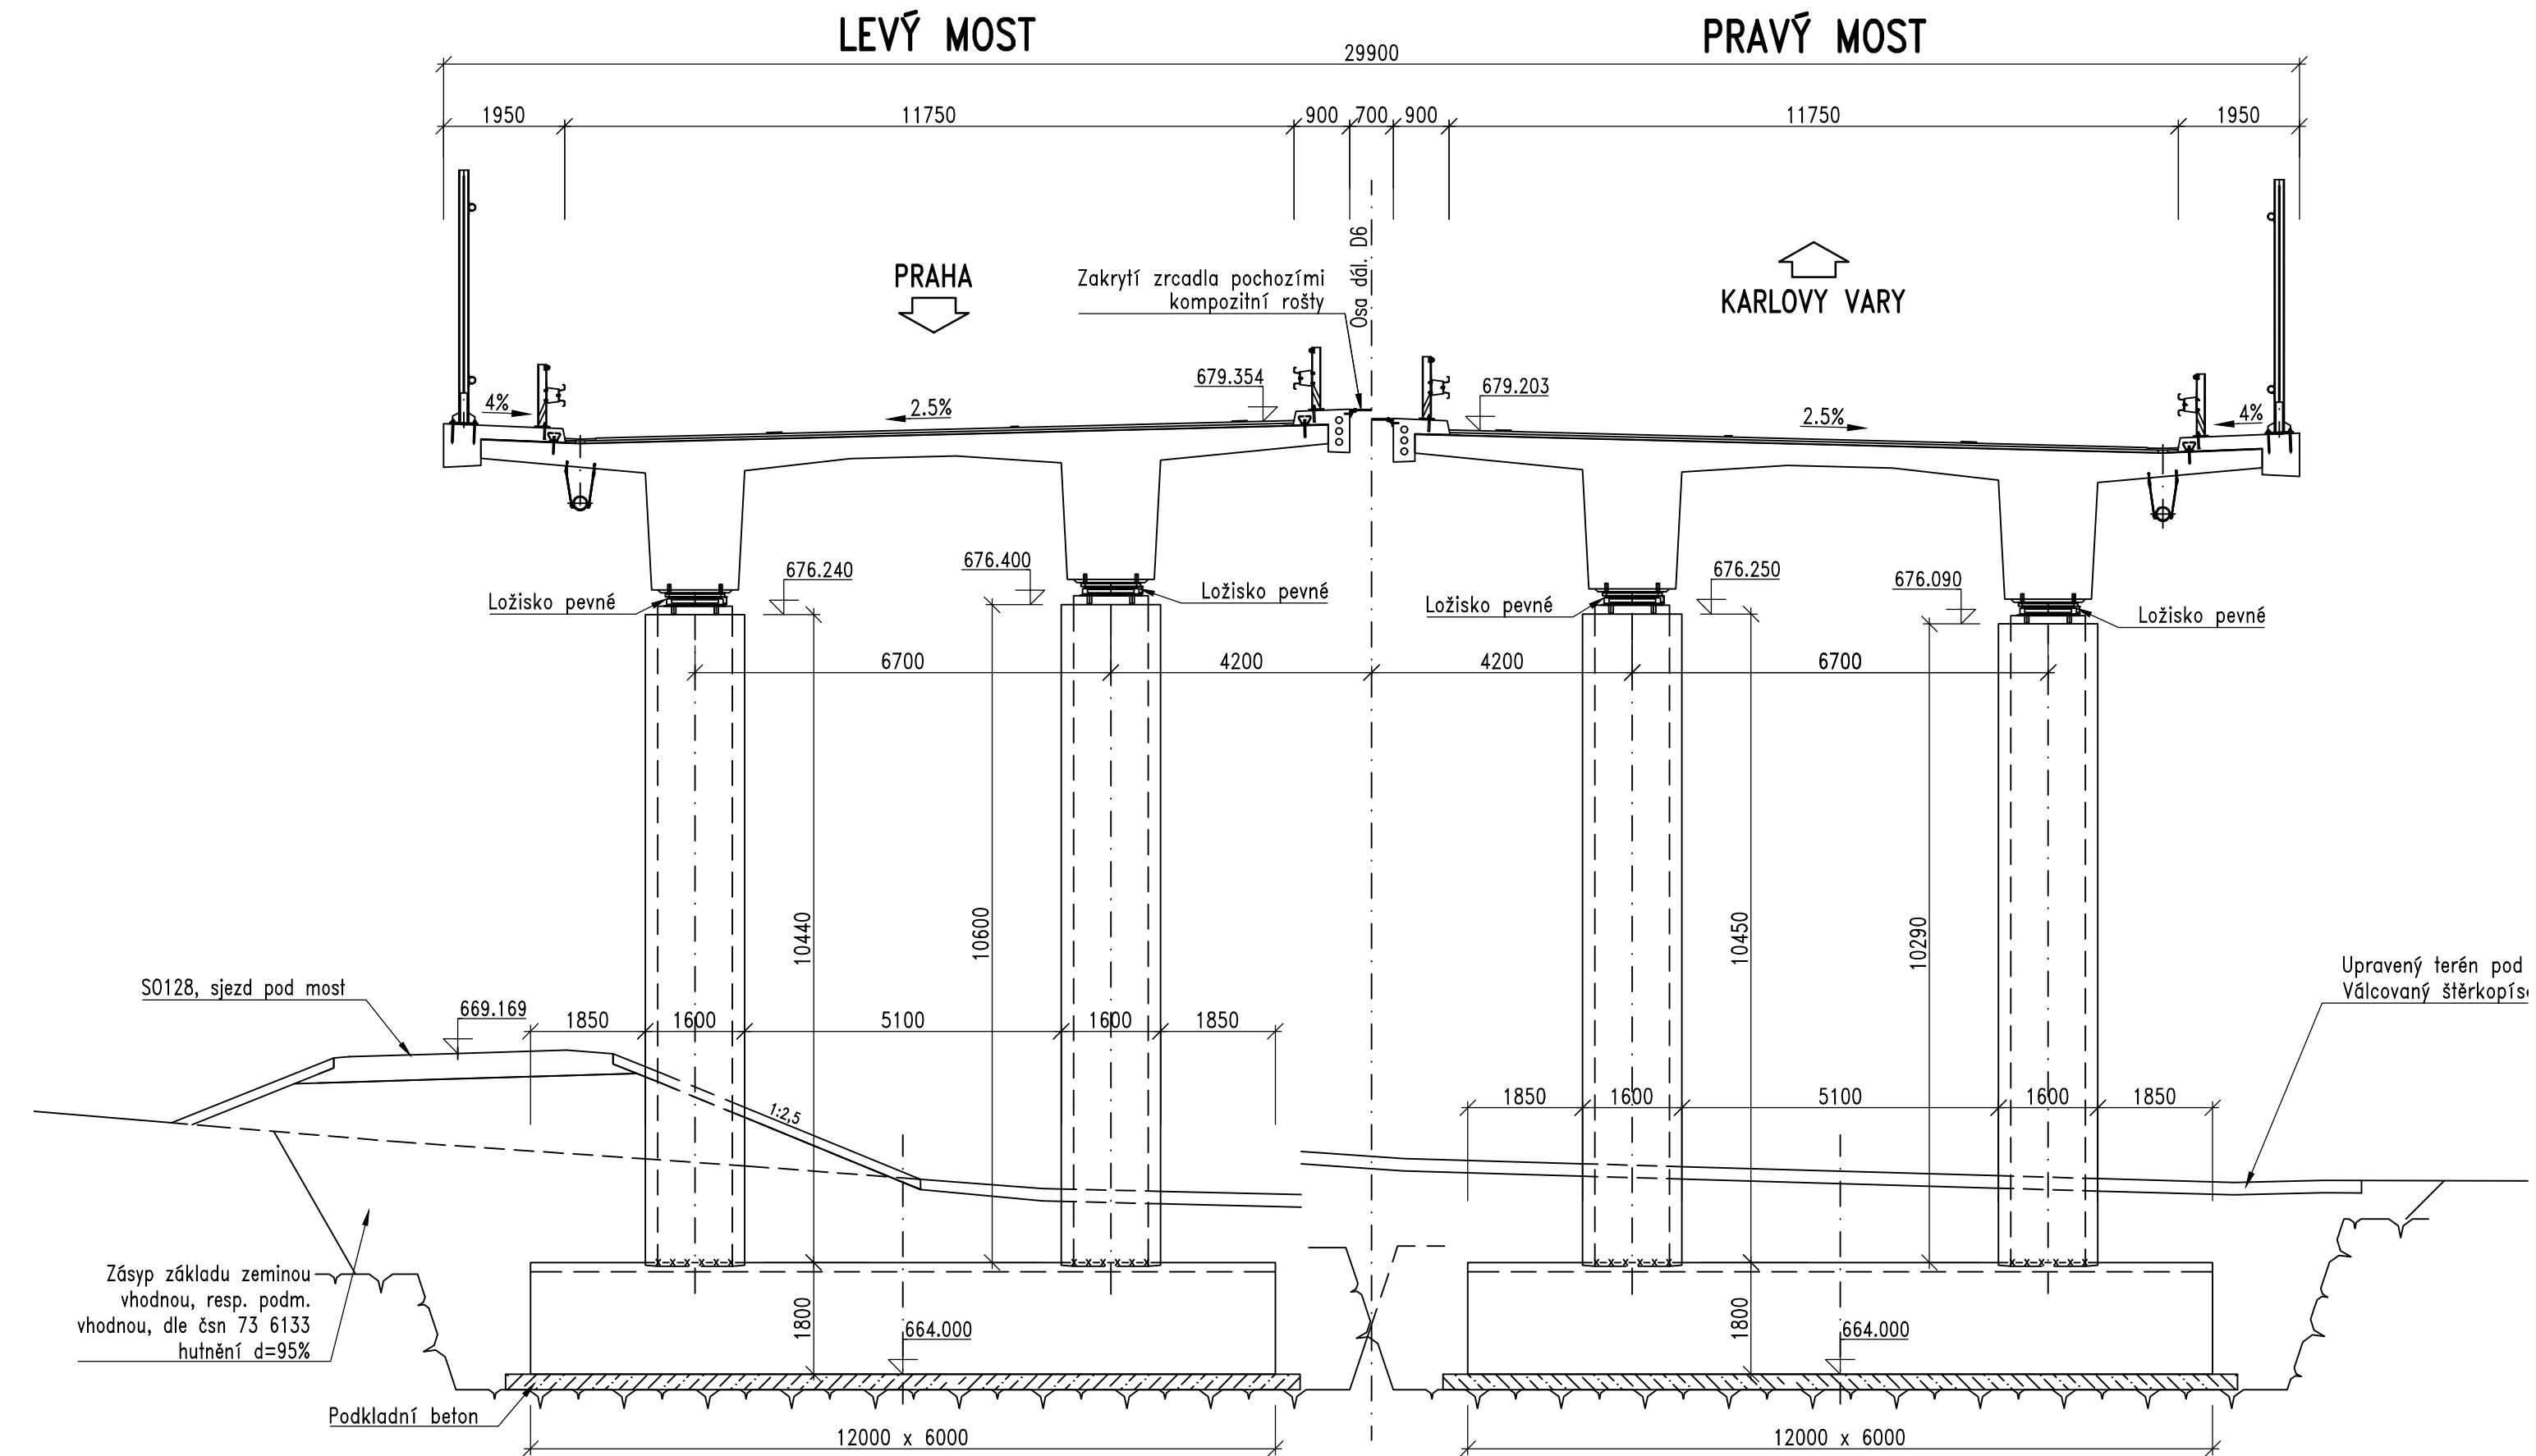


OPĚRA 04L, 04P 1:100

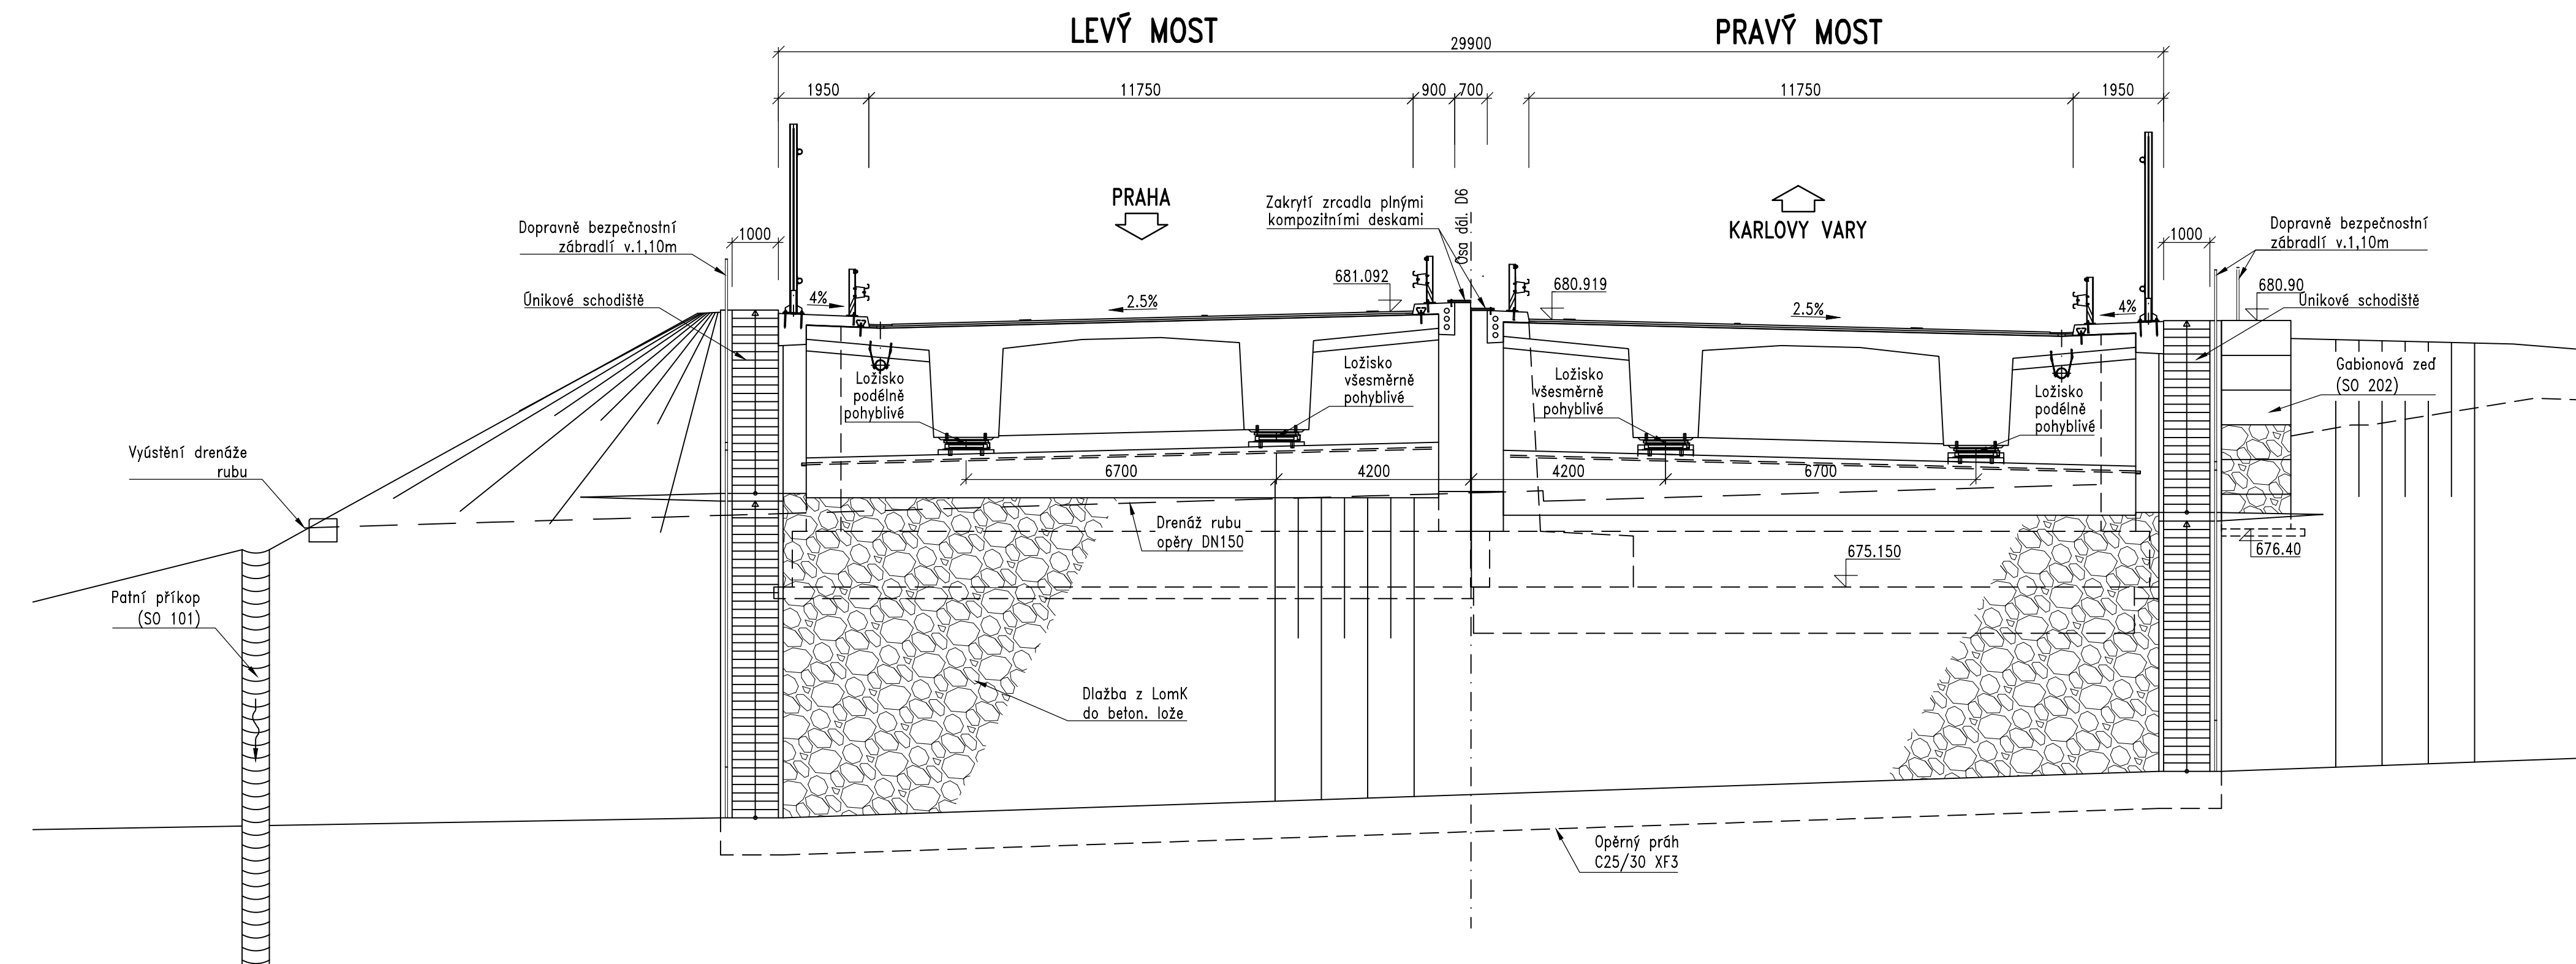

ČISTOPIS

Souřadnicový systém S-JTSK, Výškový systém Bpv

Objednatel:

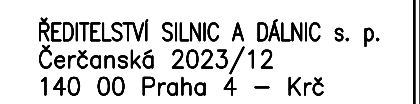

PRAGOPROJEKT

	PDPS
Číslo přílohy:	06