
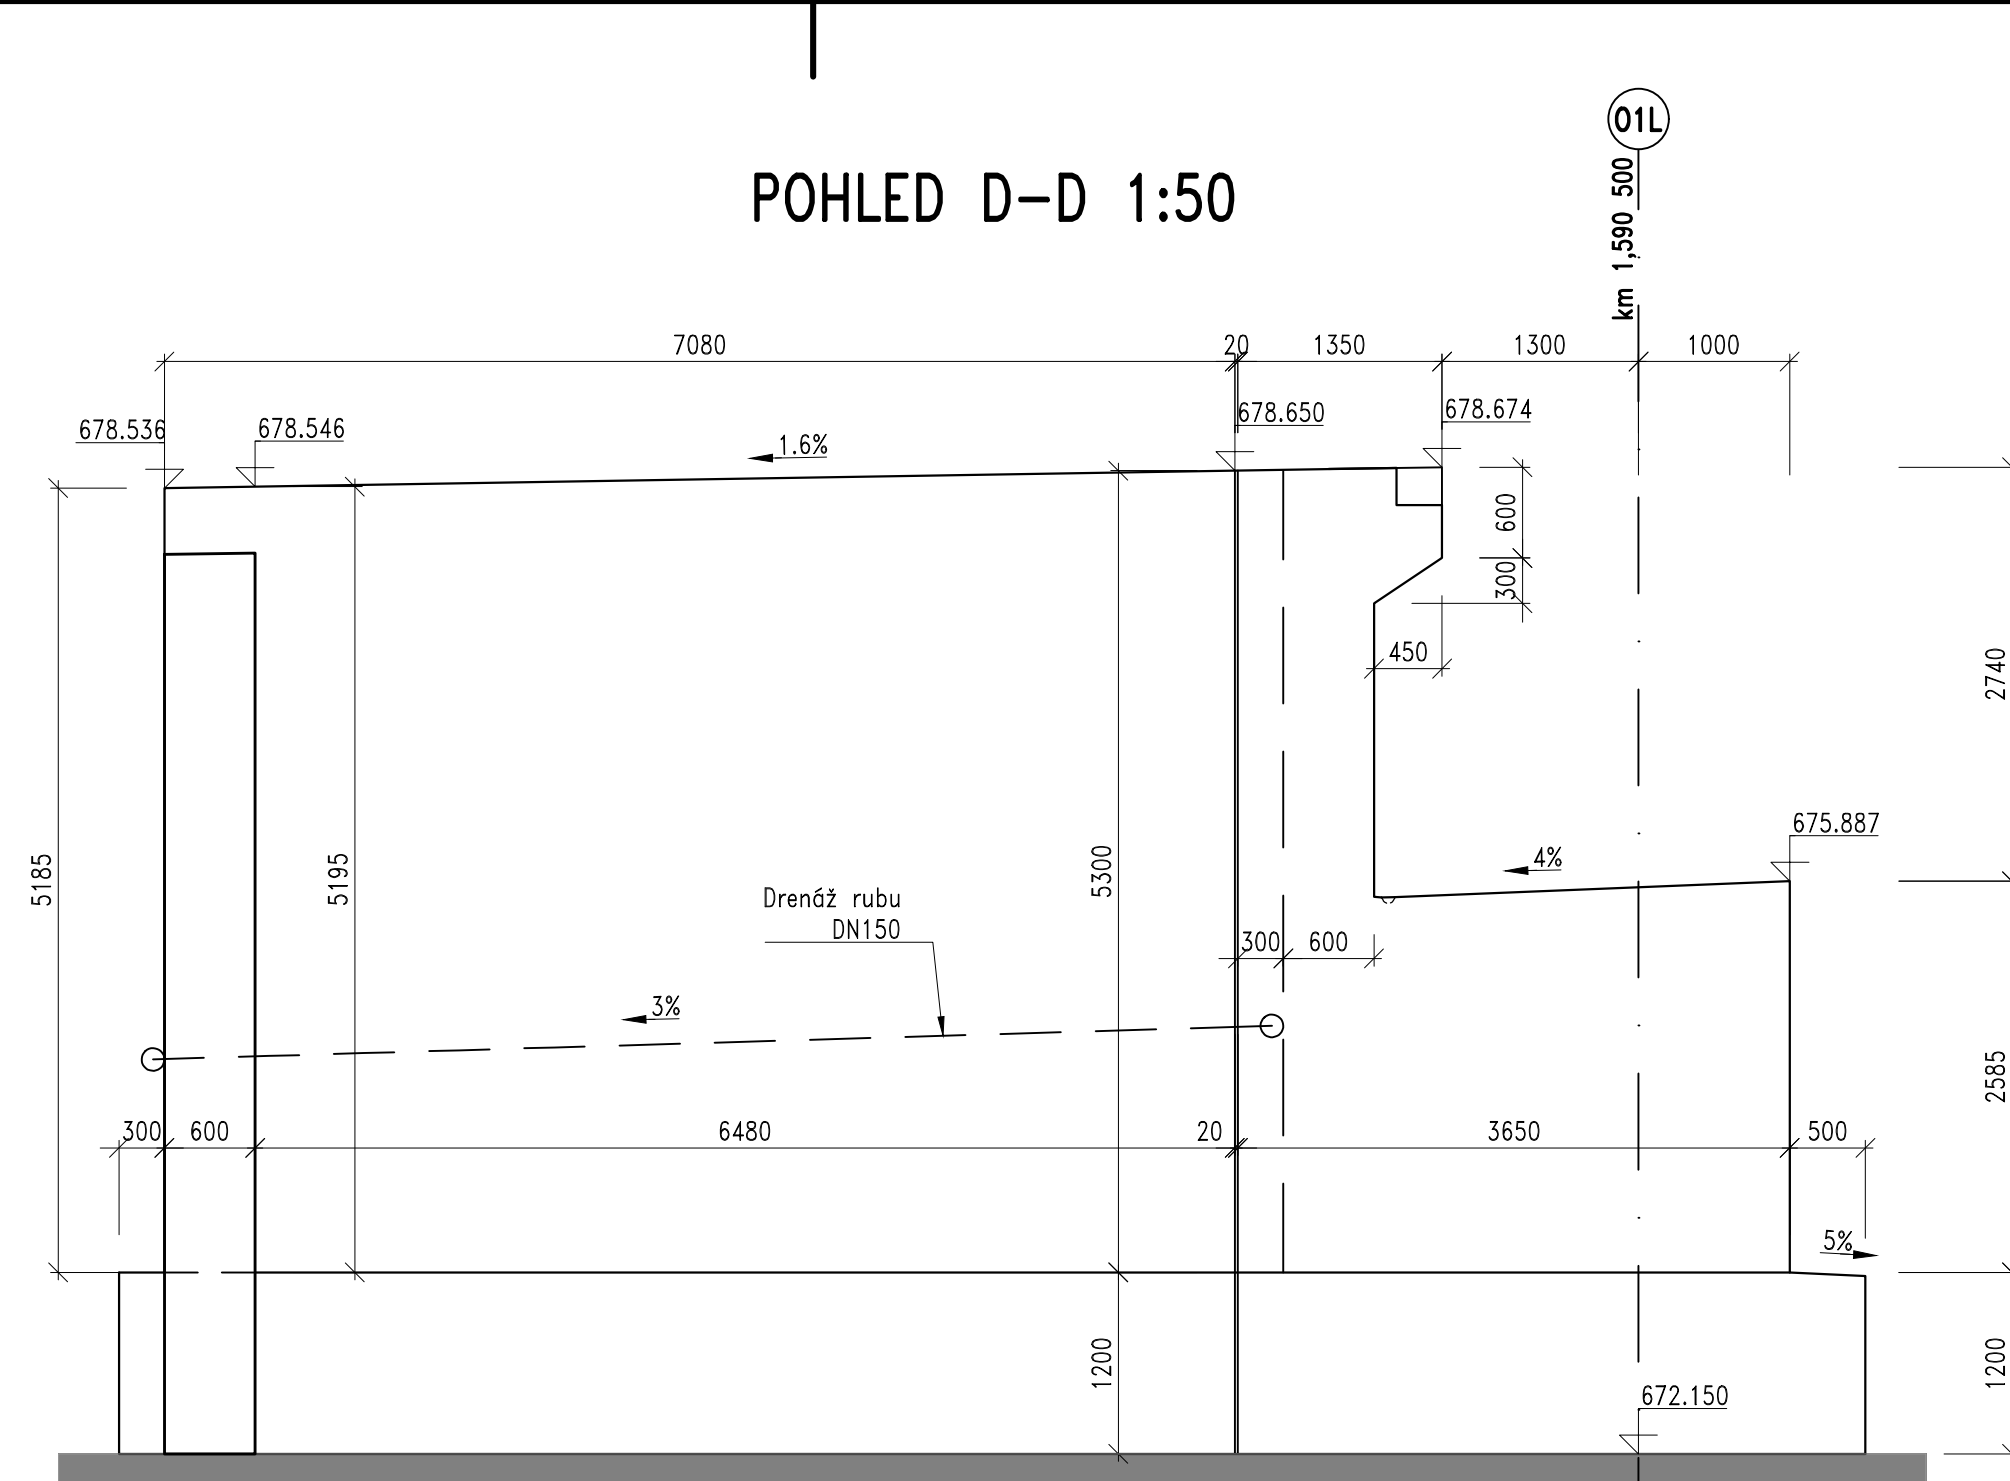
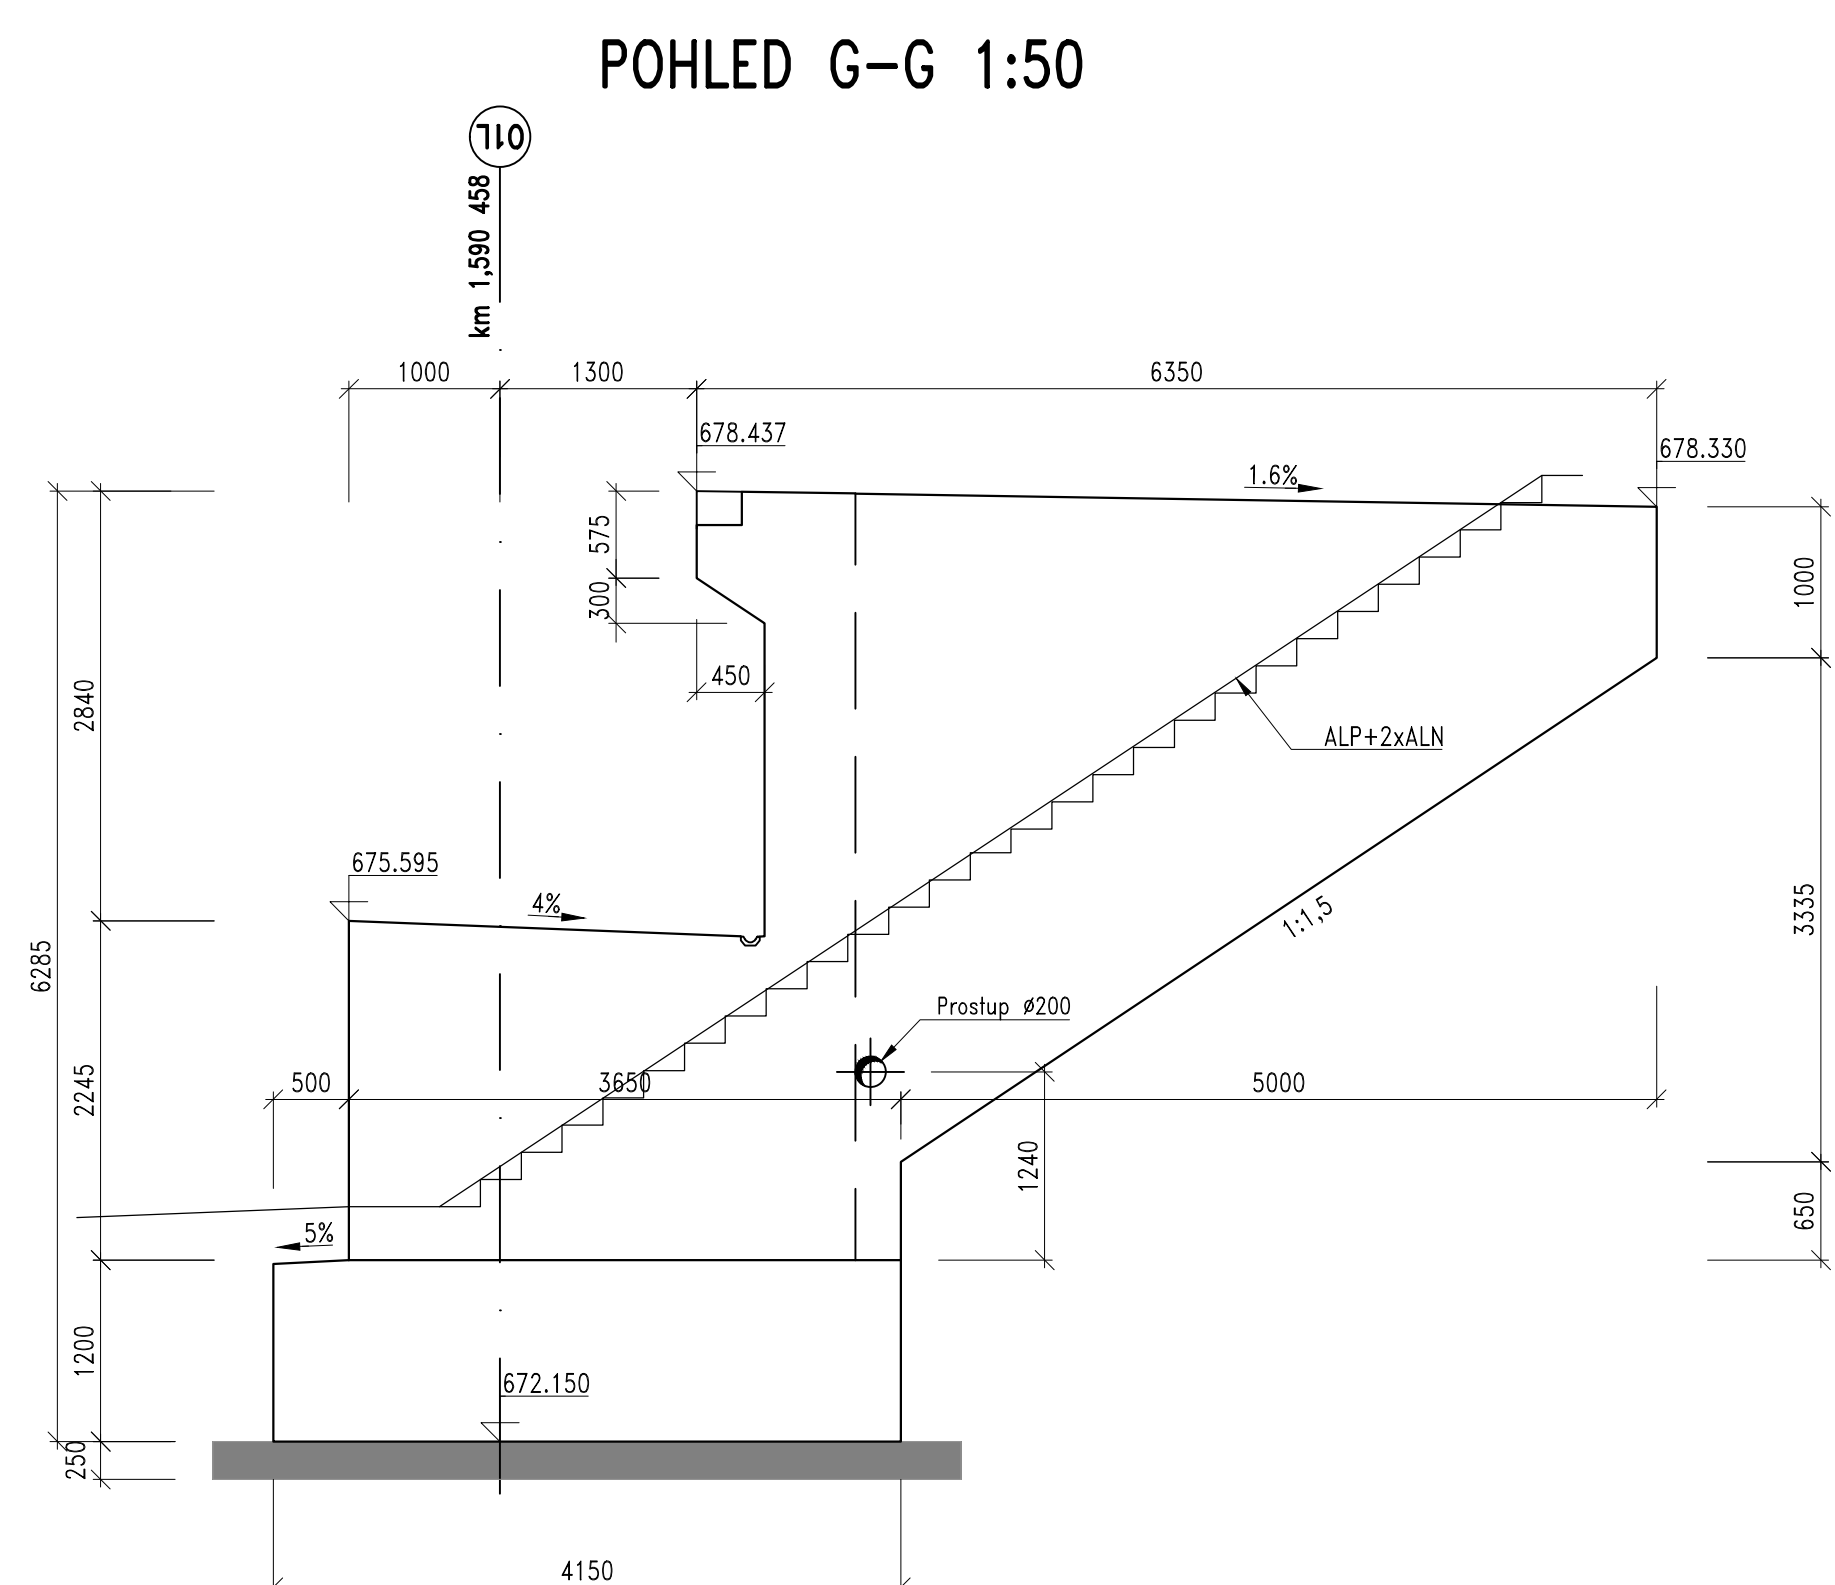
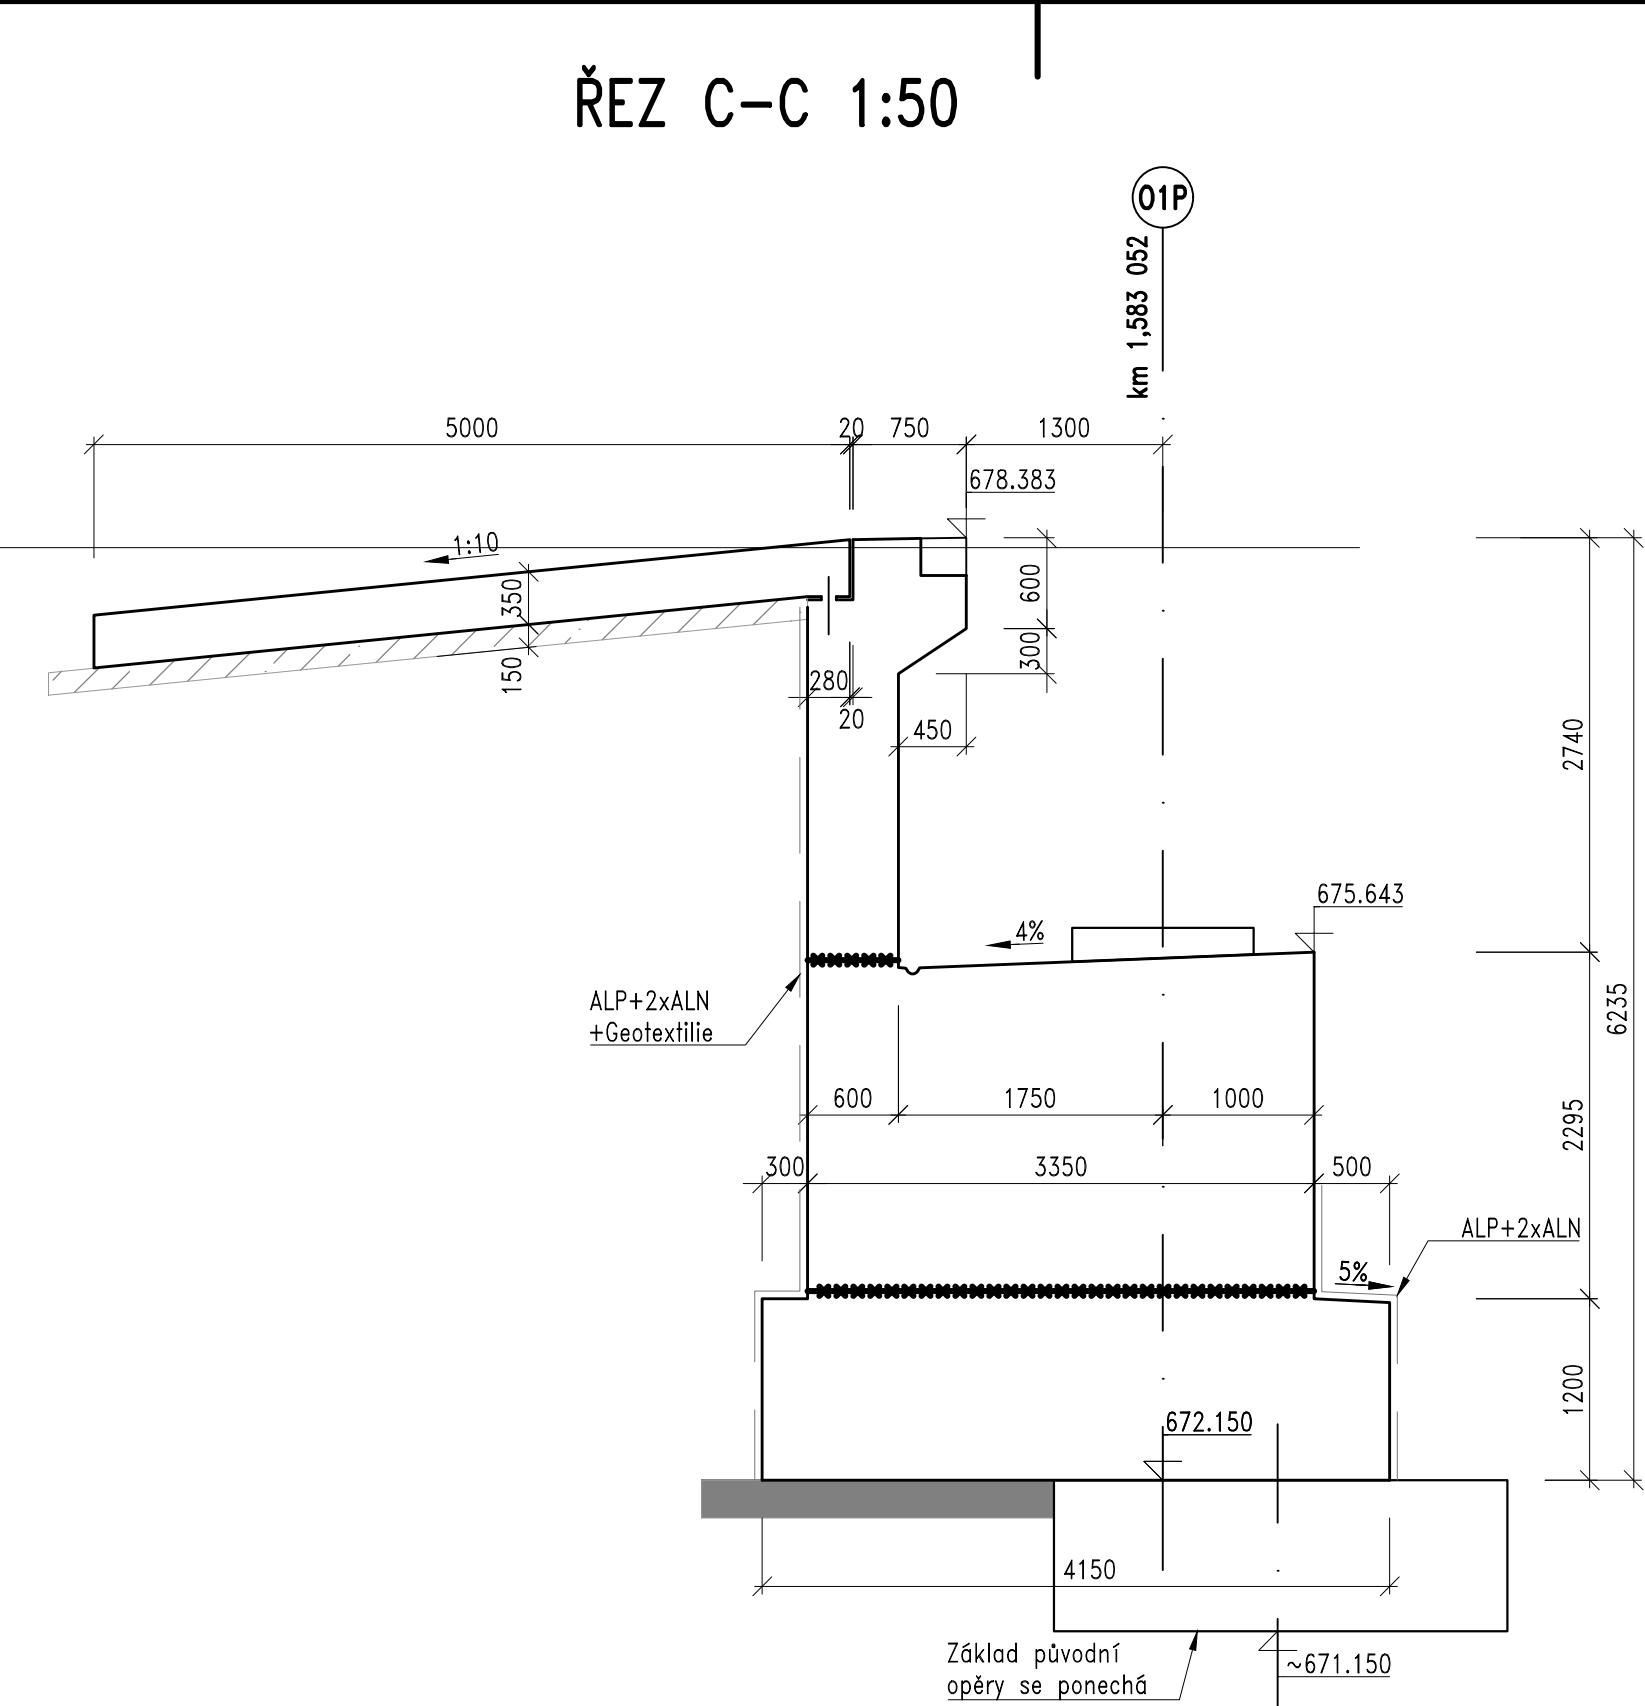
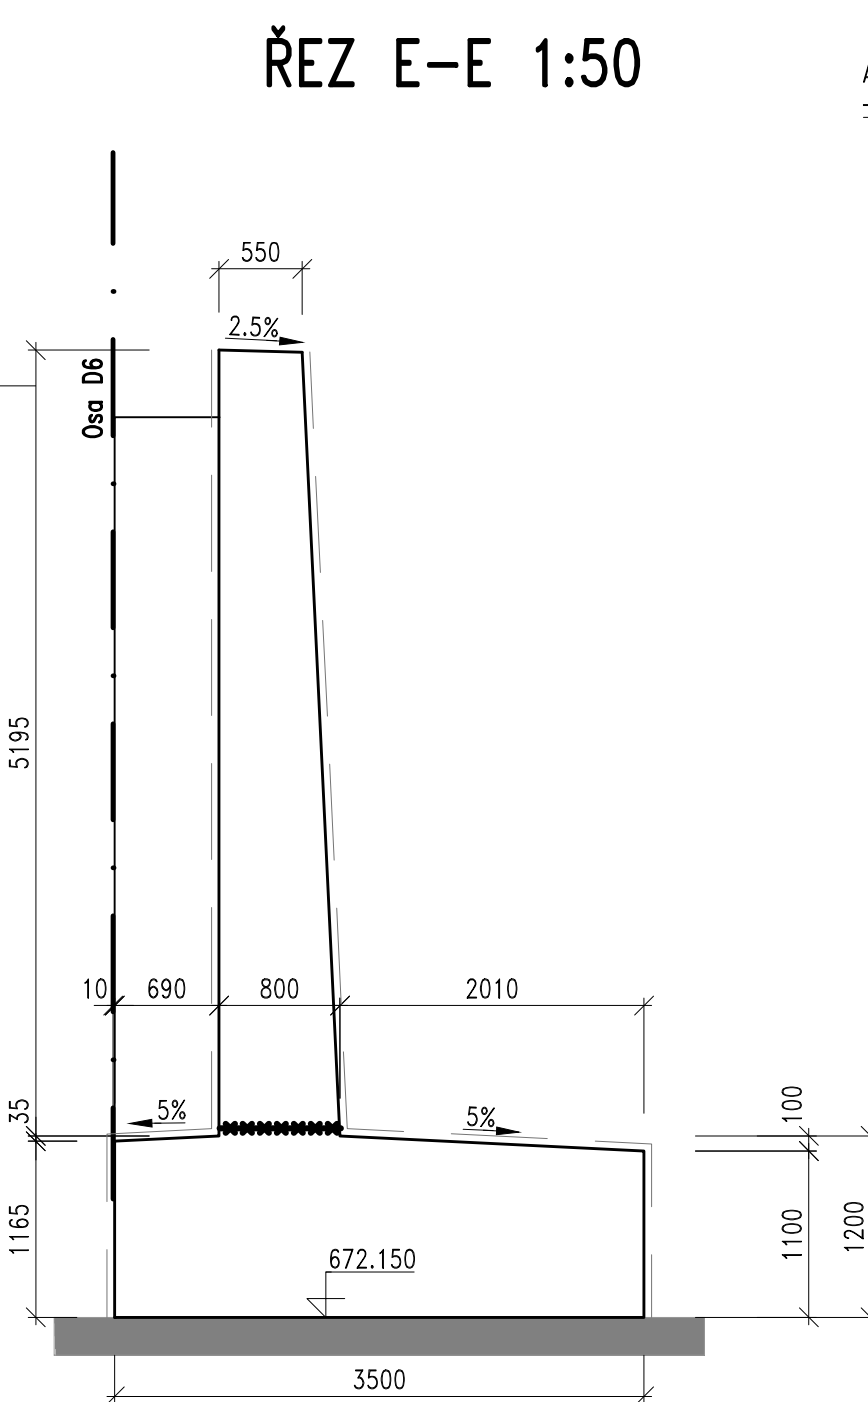
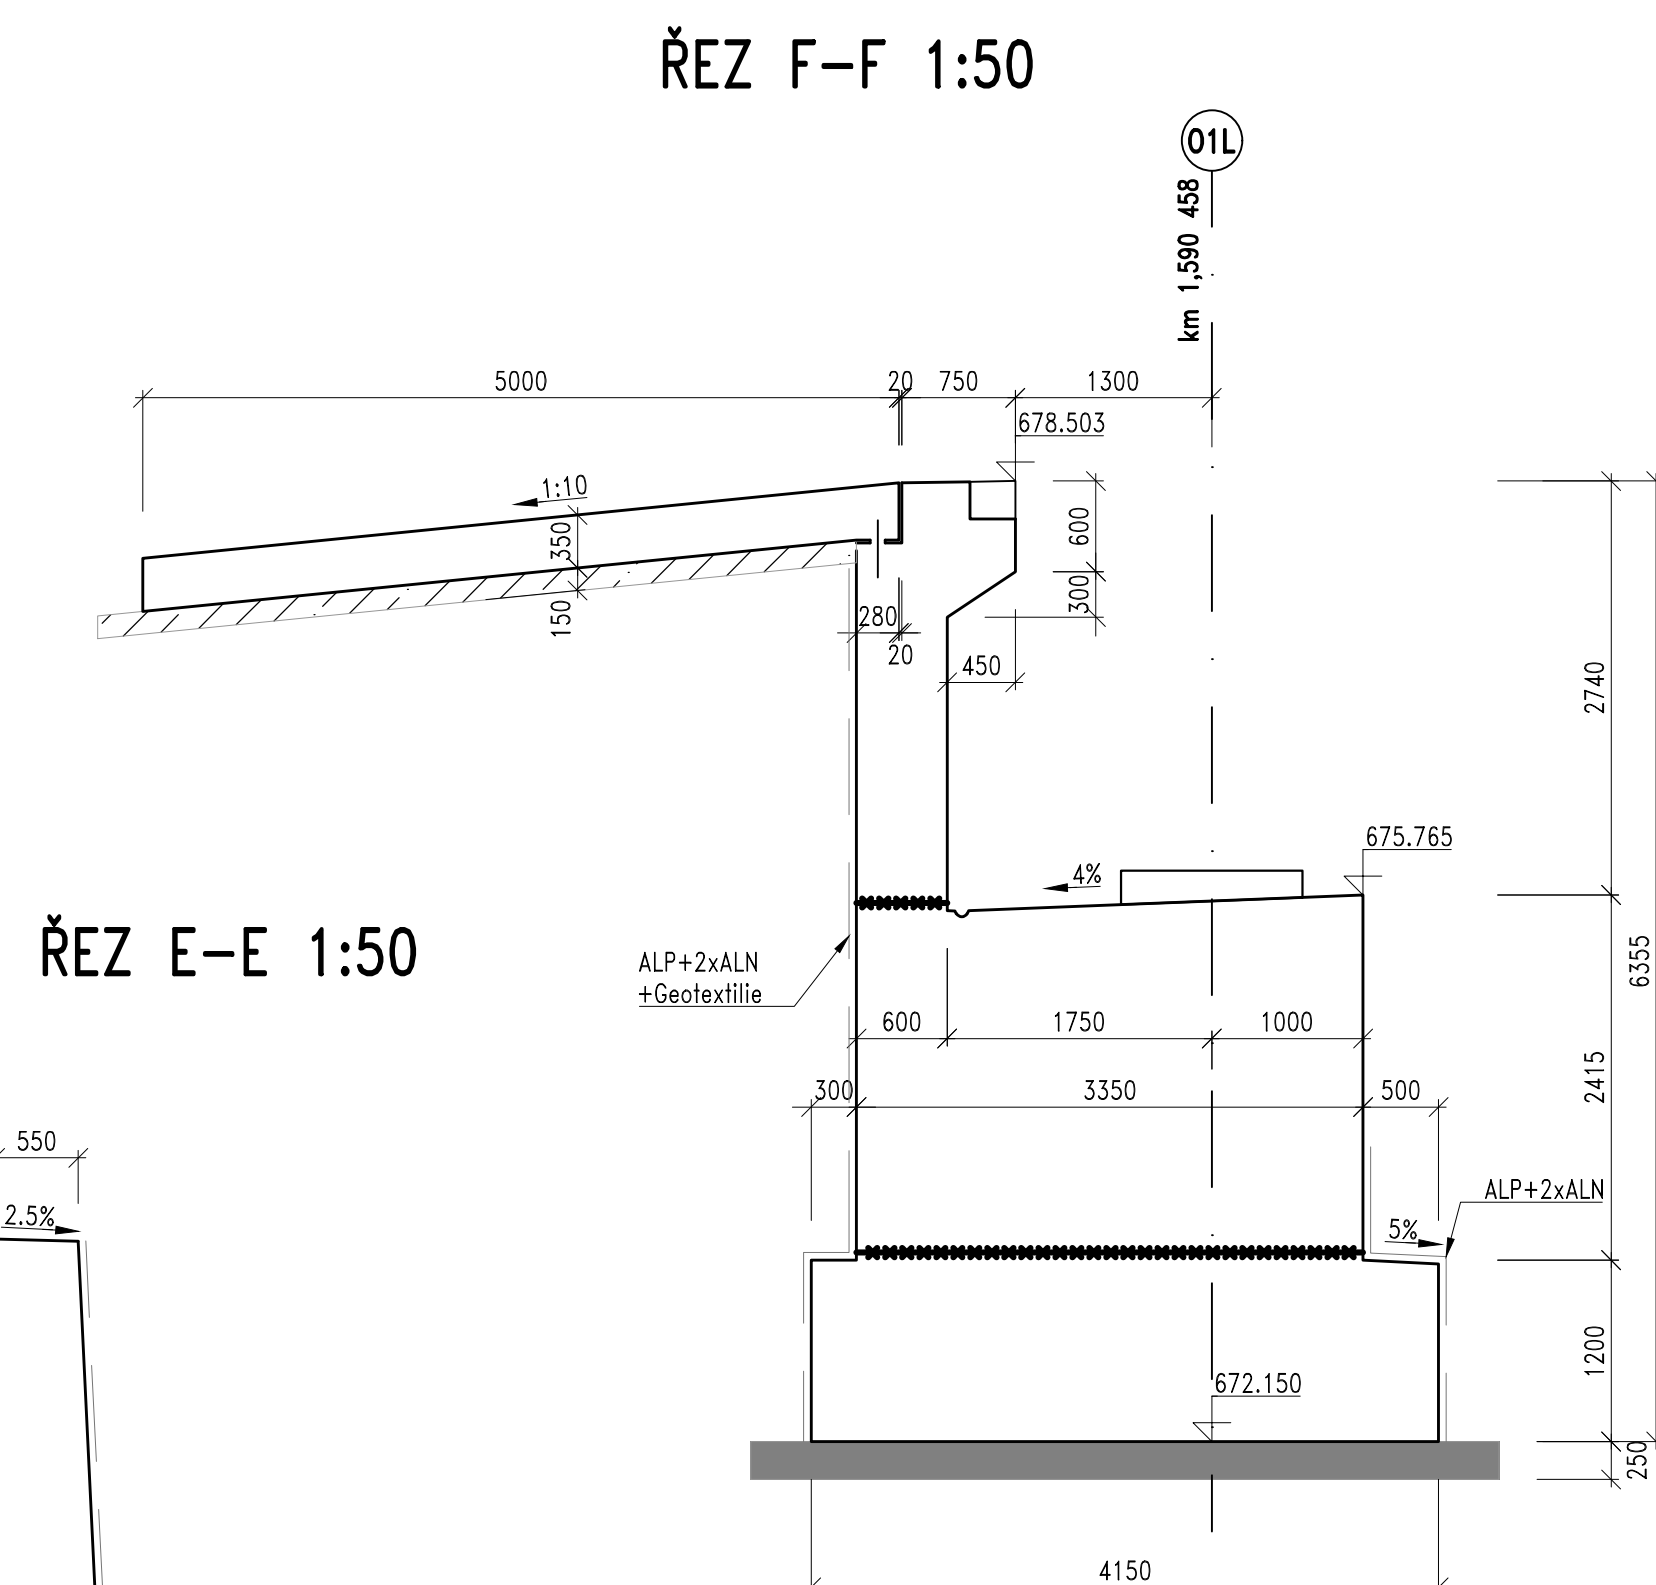
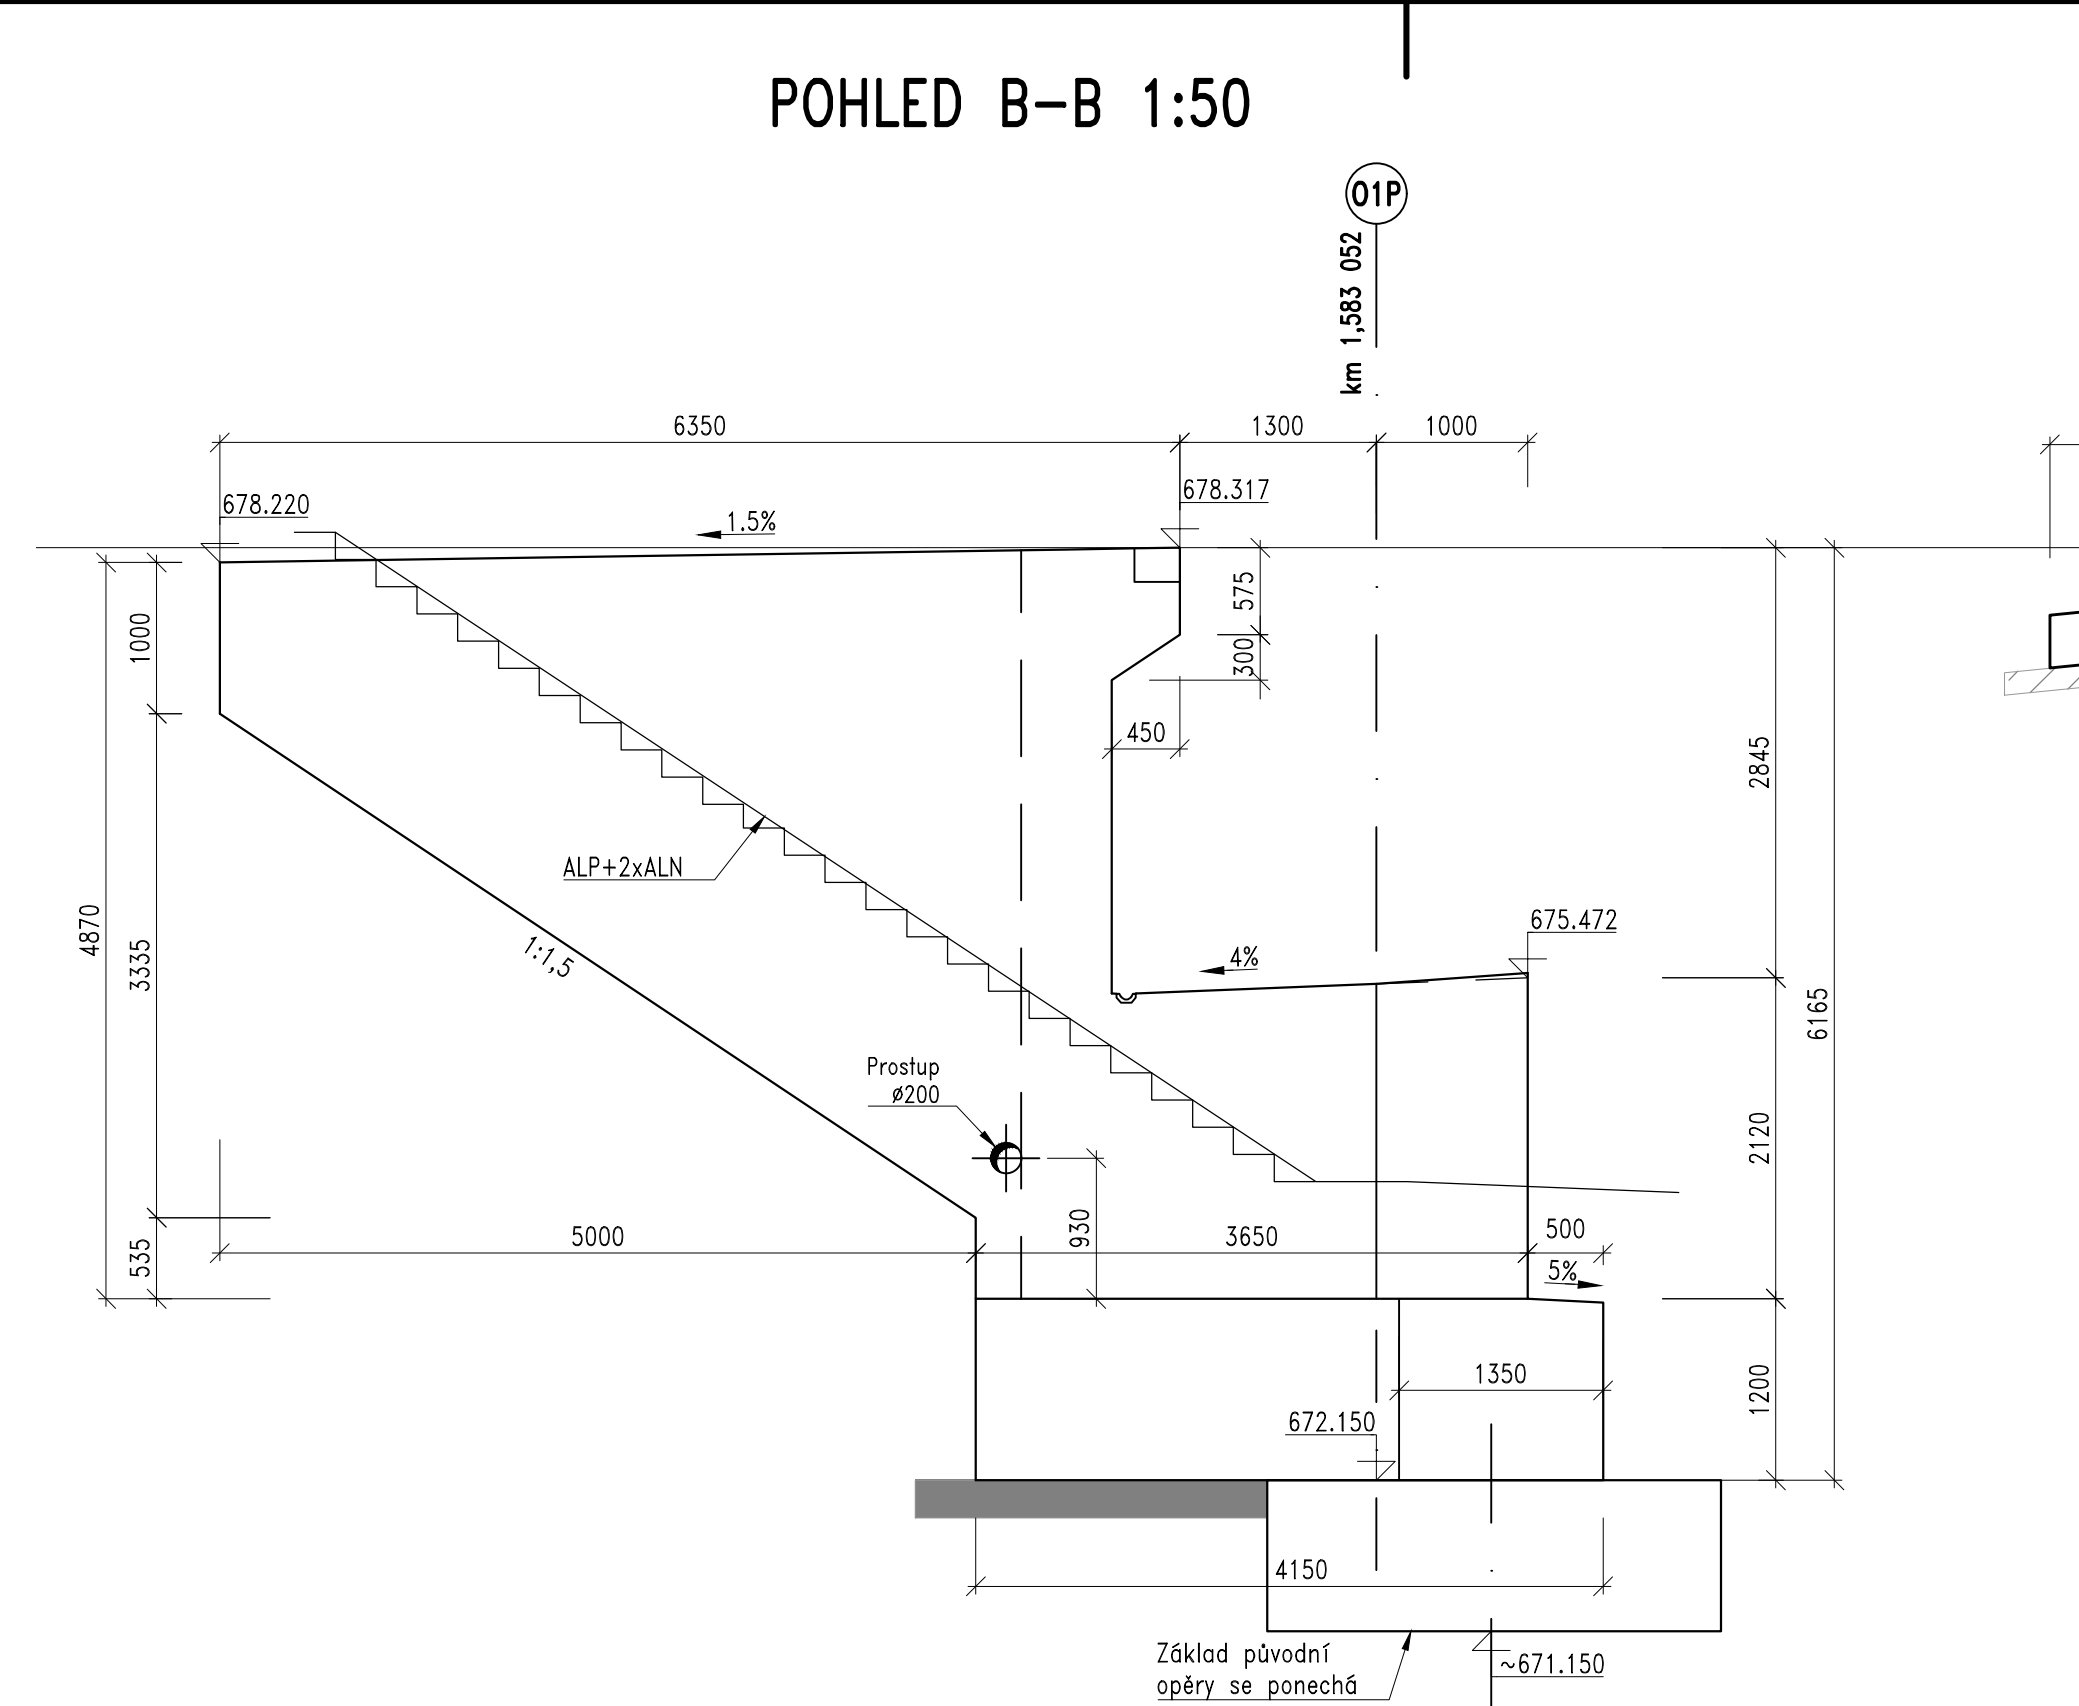


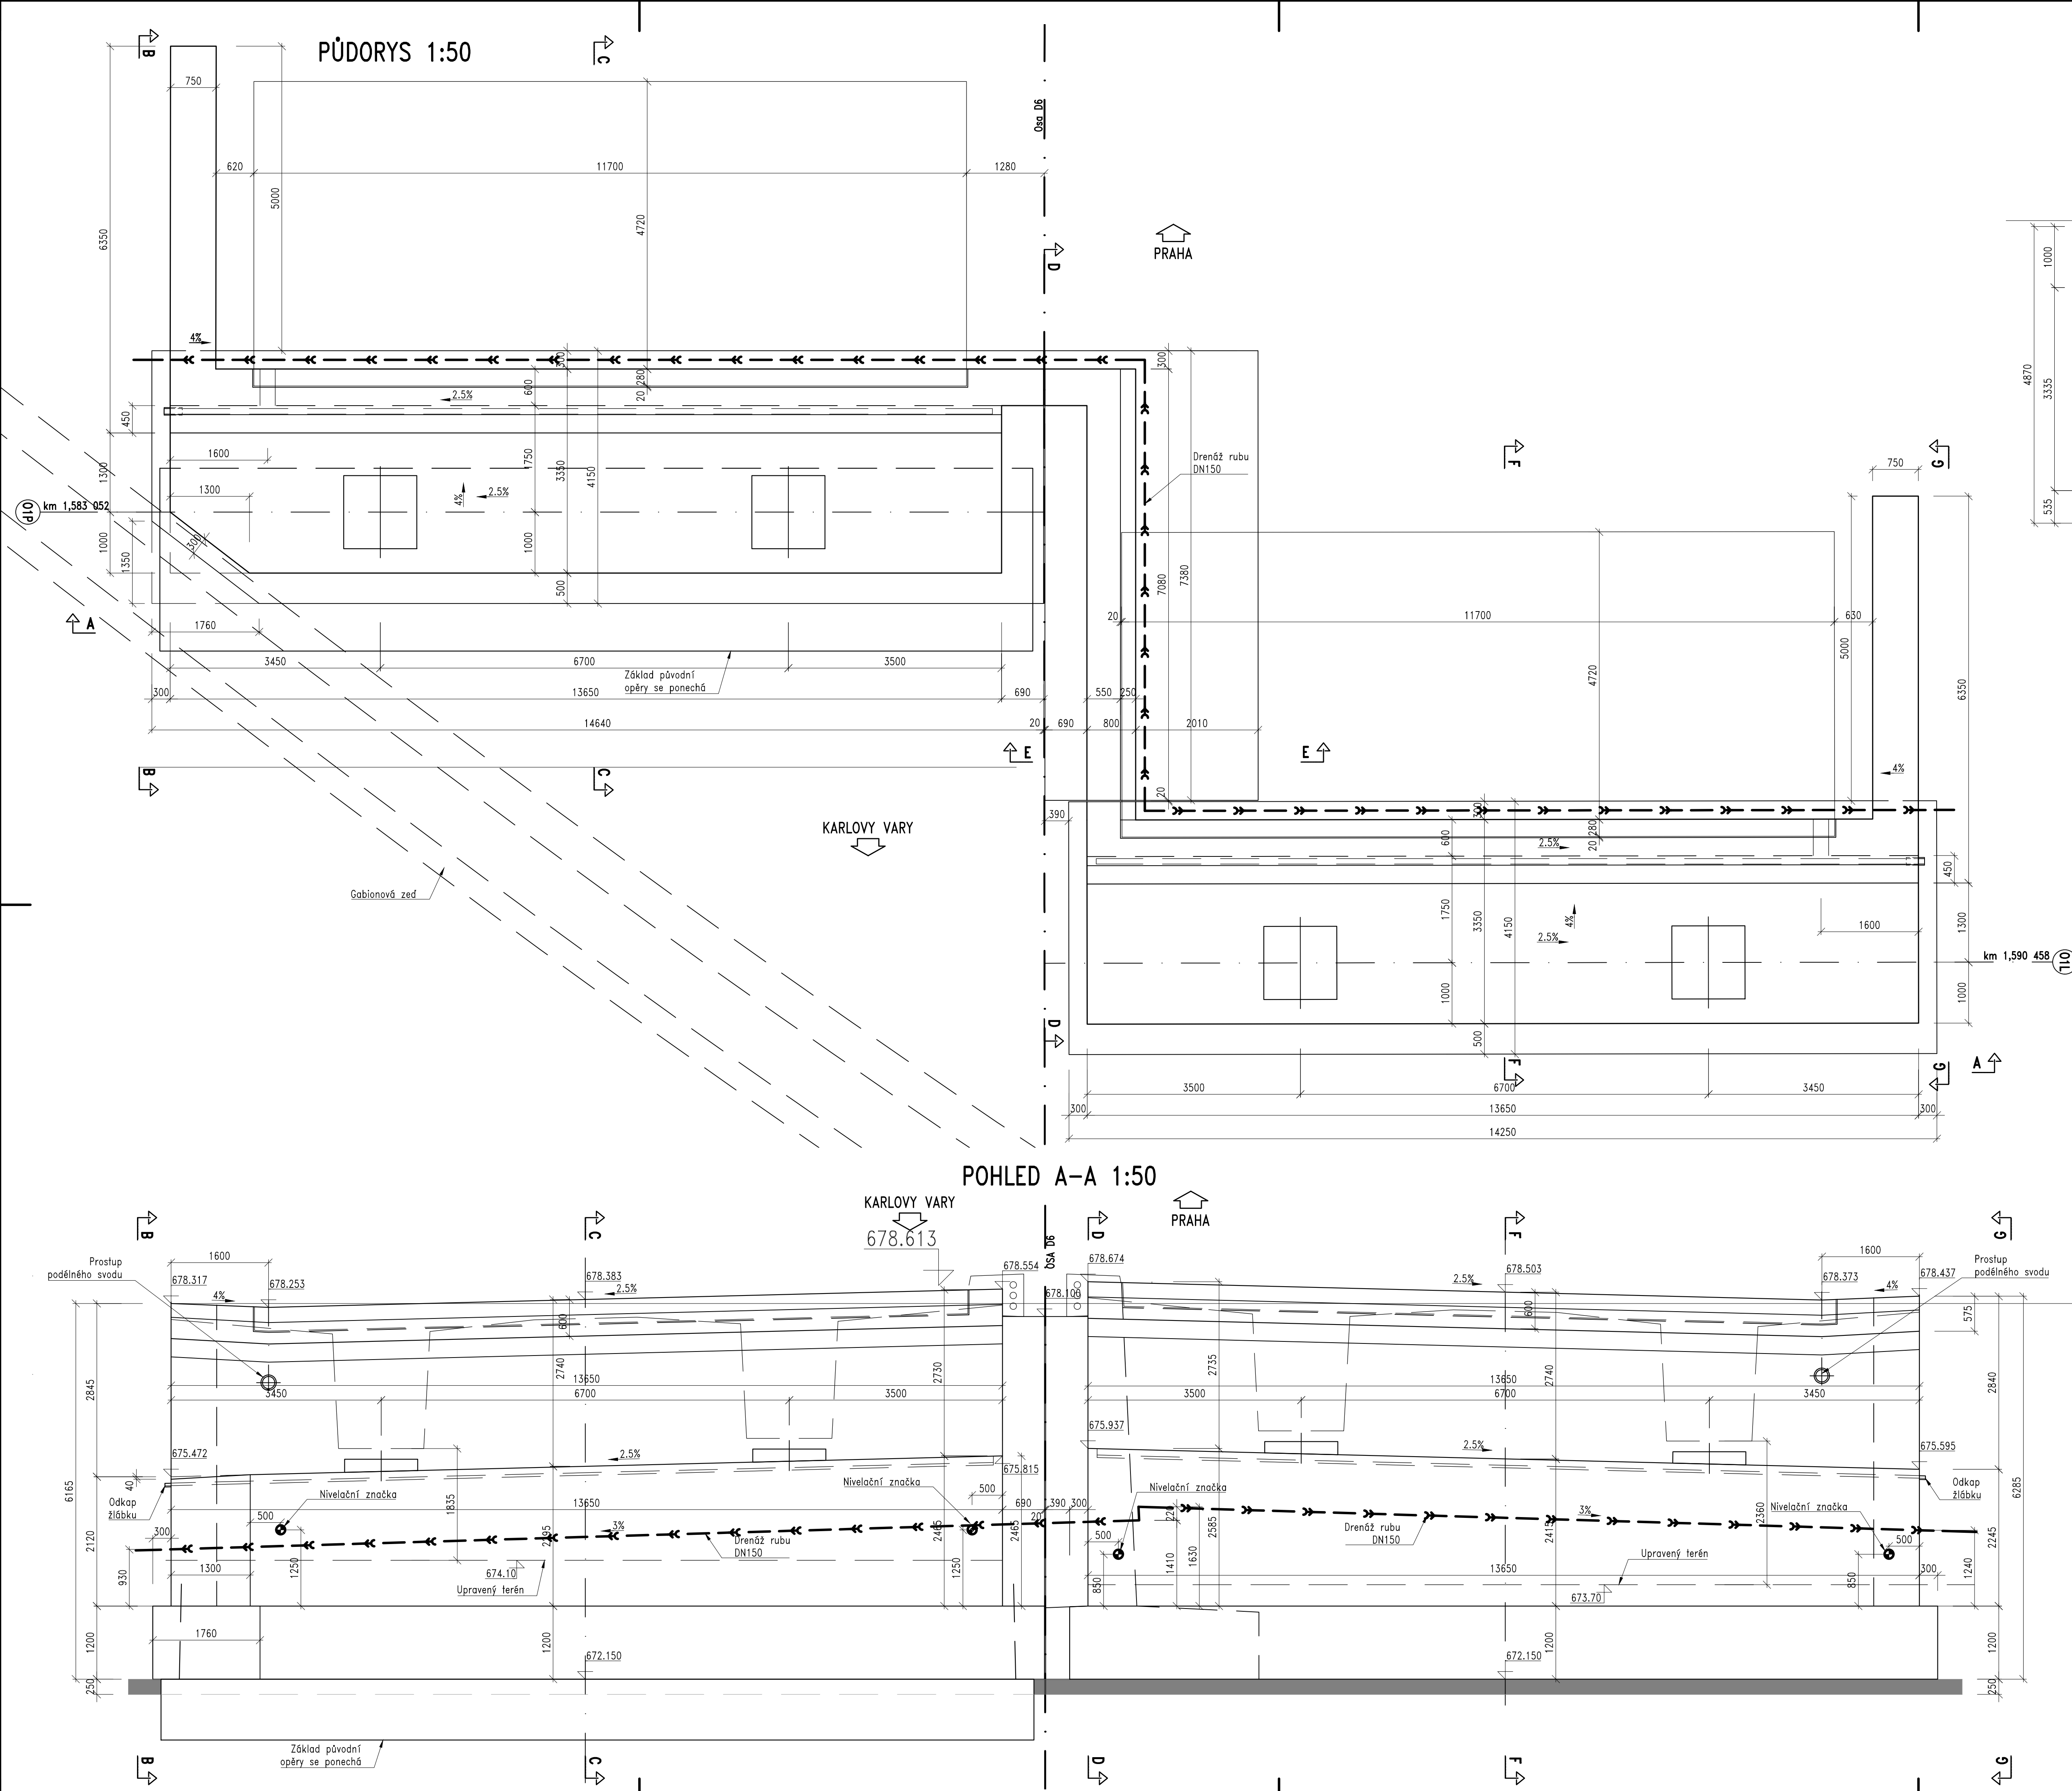

MATERIÁLY:

ZÁKLADY
DŘKY PULIHO
ODLOŽNÉ PRAMNY, ZÁV. ZDI, KŘÍDLA
OPĚRY
MOŠNÁ KONSTRUKCE

C30/37 - XF1+XA2+XC2
C35/45 - XF1+XD1+XC4
C30/37 - XF4+XD3+XC4
C30/37 - XF4+XD3+XC4
C35/45 - XF2+XD1+XC4

KATEGORIE POVRCH. ÚPRAVY:

Pohledové plochy C2d
Ostatní plochy C1a

Všechny plochy v trvalém kontaktu se zemínou budou opatřeny nátěry proti zemní vlhkosti
ALP+2xALN

ČÁST D.2
SO 202

ČISTOPIS

Ředitelství silnic a dálnic
Soutěžní systém S-JTSK, Výzkumný systém BpV
Objednatel: Ředitelství silnic a dálnic s. p.
Čestanské 2023/12
140 00 Praha 4 – Krč

Zhotovitel: PD PRAGOPROJEKT, a.s., K Rybáře 1668/16, 147 54 Praha 4, IČO: 45272387, www.pragoprojekt.cz, datová schránka: 44n154
Návrh/autor: Ing. Karolína Hladá
Zpracoval: Ing. Martin Blatný
Zkontroluje: Ing. Václav Dvořák
Technická kontrola: Ing. Karel Peřichal
Hodnotil: Ing. Pavel Sláma
Projekt: Ing. Radovan Stankovský

Proj.: KARLOVSKÝ KRAJ
Místní úřad: OLŠOVÁ VRATA, ANEŠKA HORA, ŽALMANOV, HORNÍ TÁŠOVCE, BOCHOV
Objednatel: RSD s. p., Čestanské 2023/12, 140 00 Praha 4, IČO 65983390
Město: Olšová
Číslo státní: 25-150-2
Číslo akce: 05-219
Datum: 03/2026
Forma: PDPS
Stupeň: 09
Průběh: 09