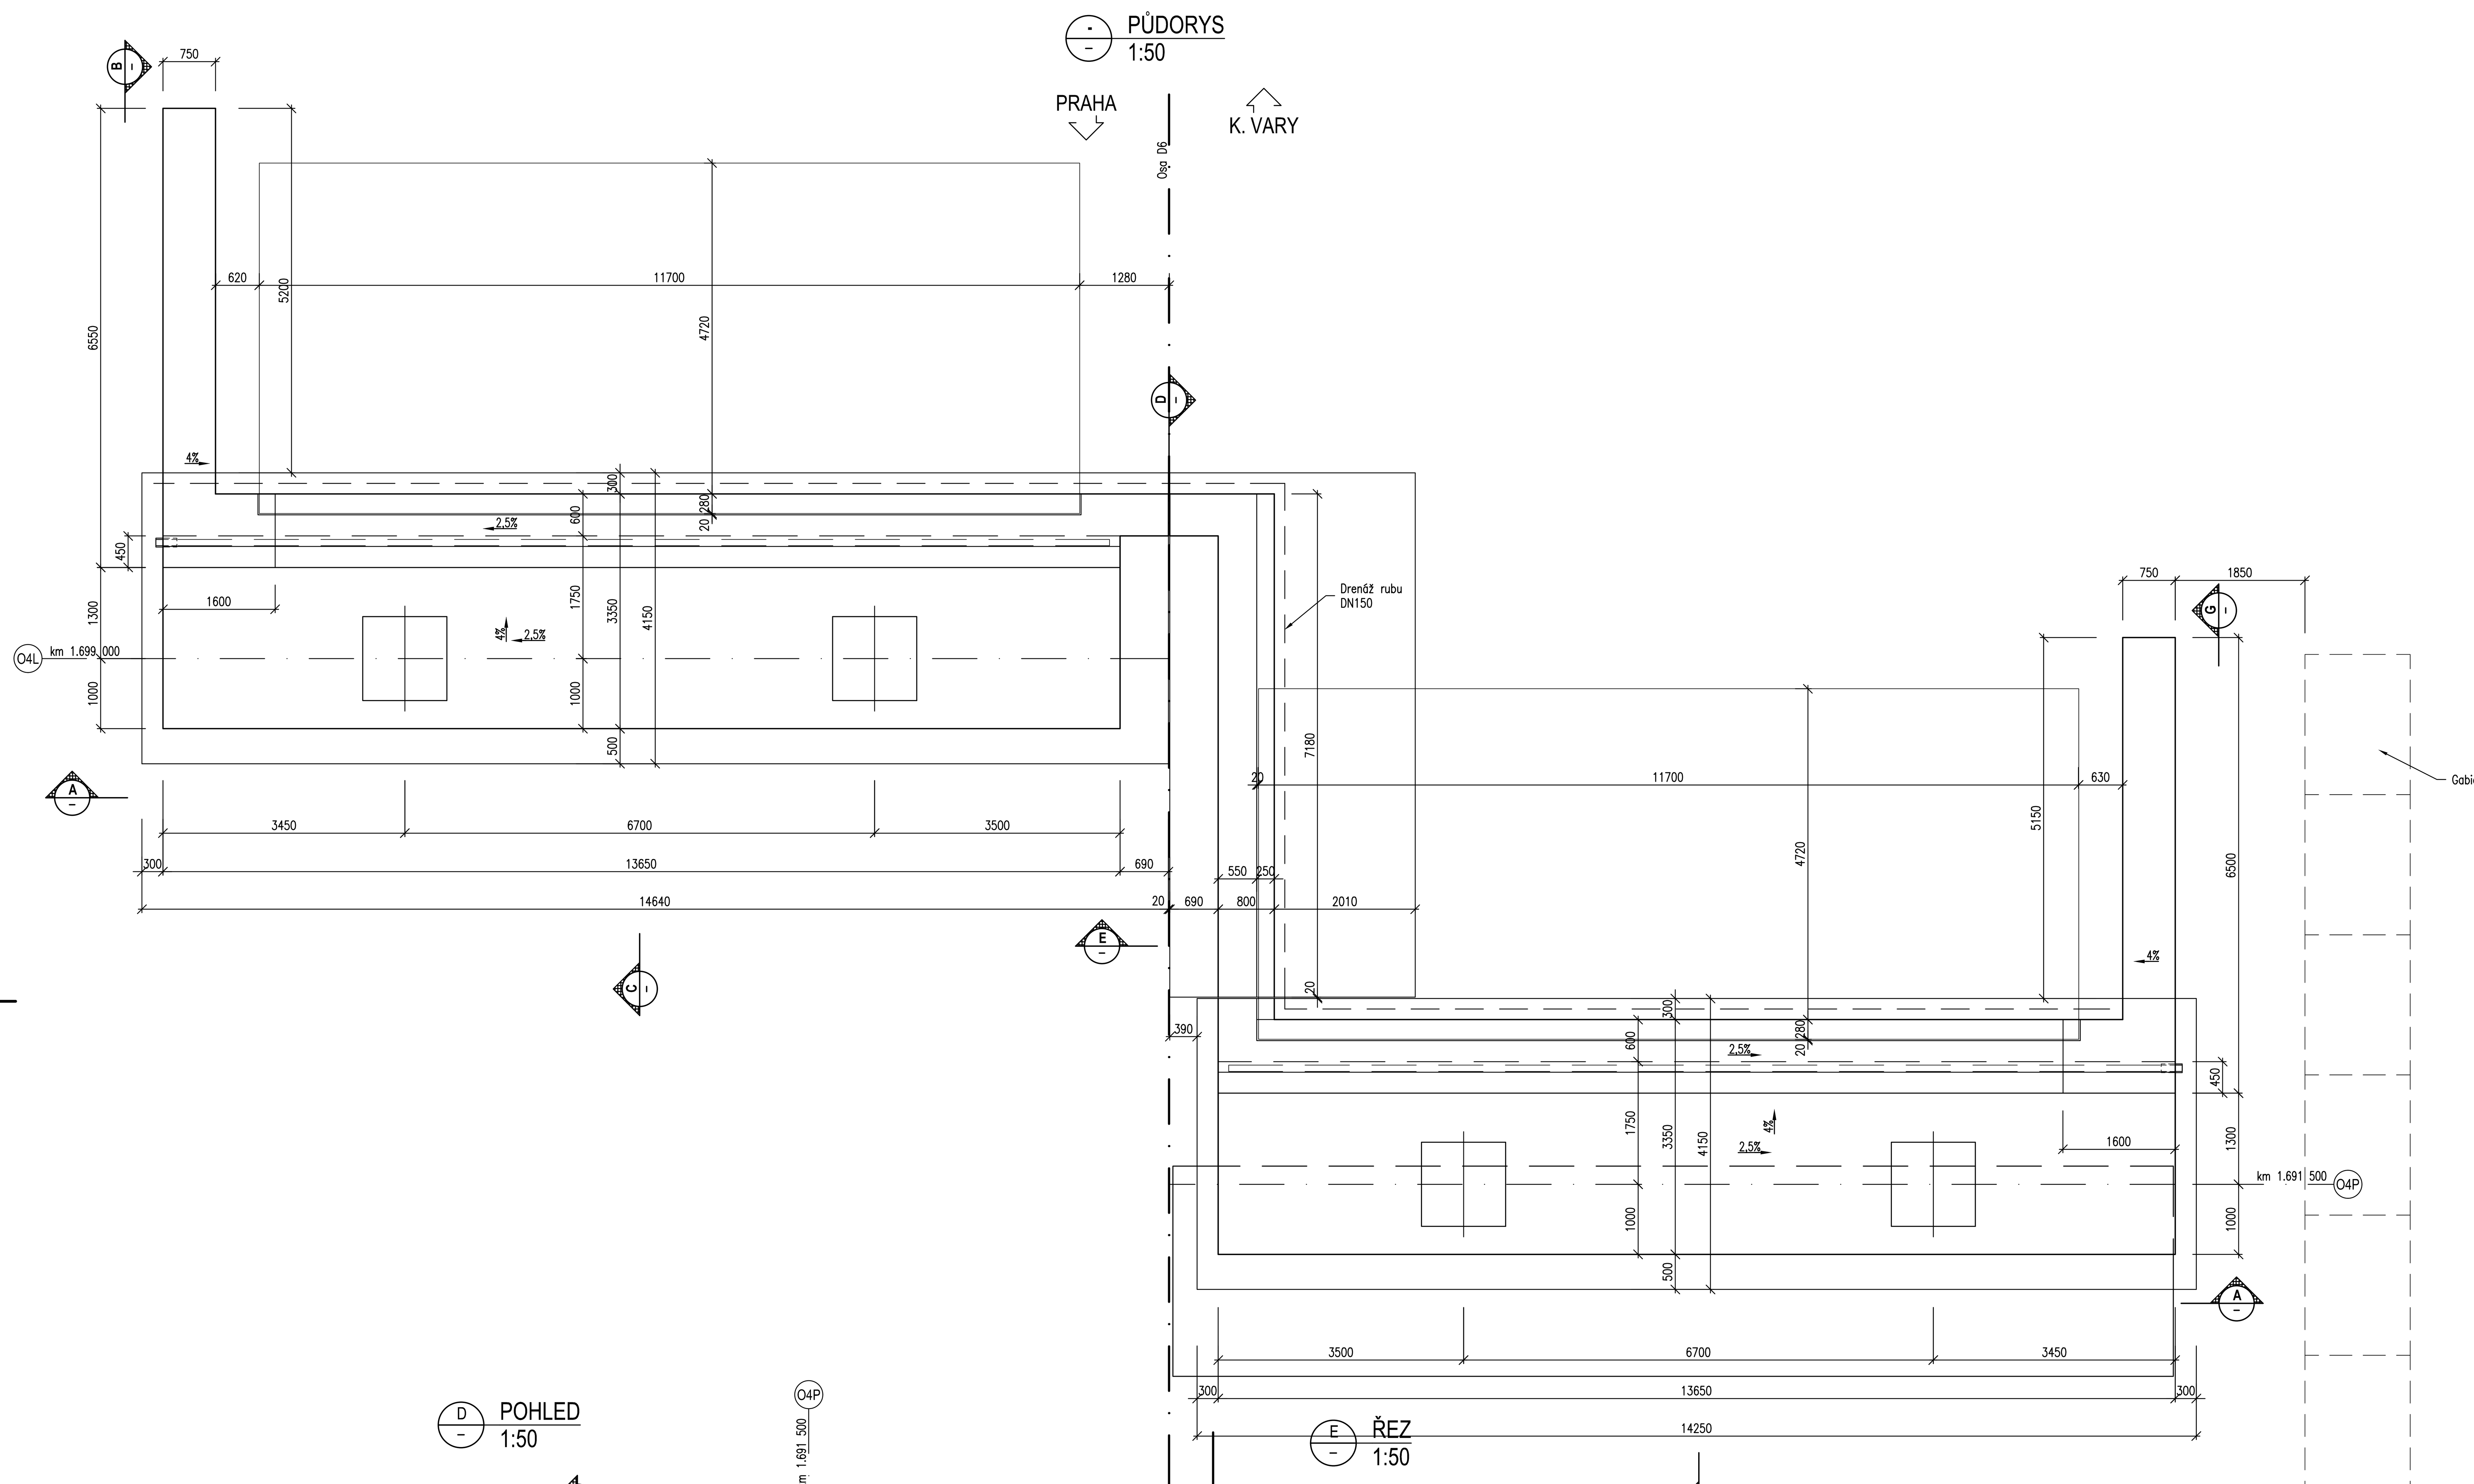

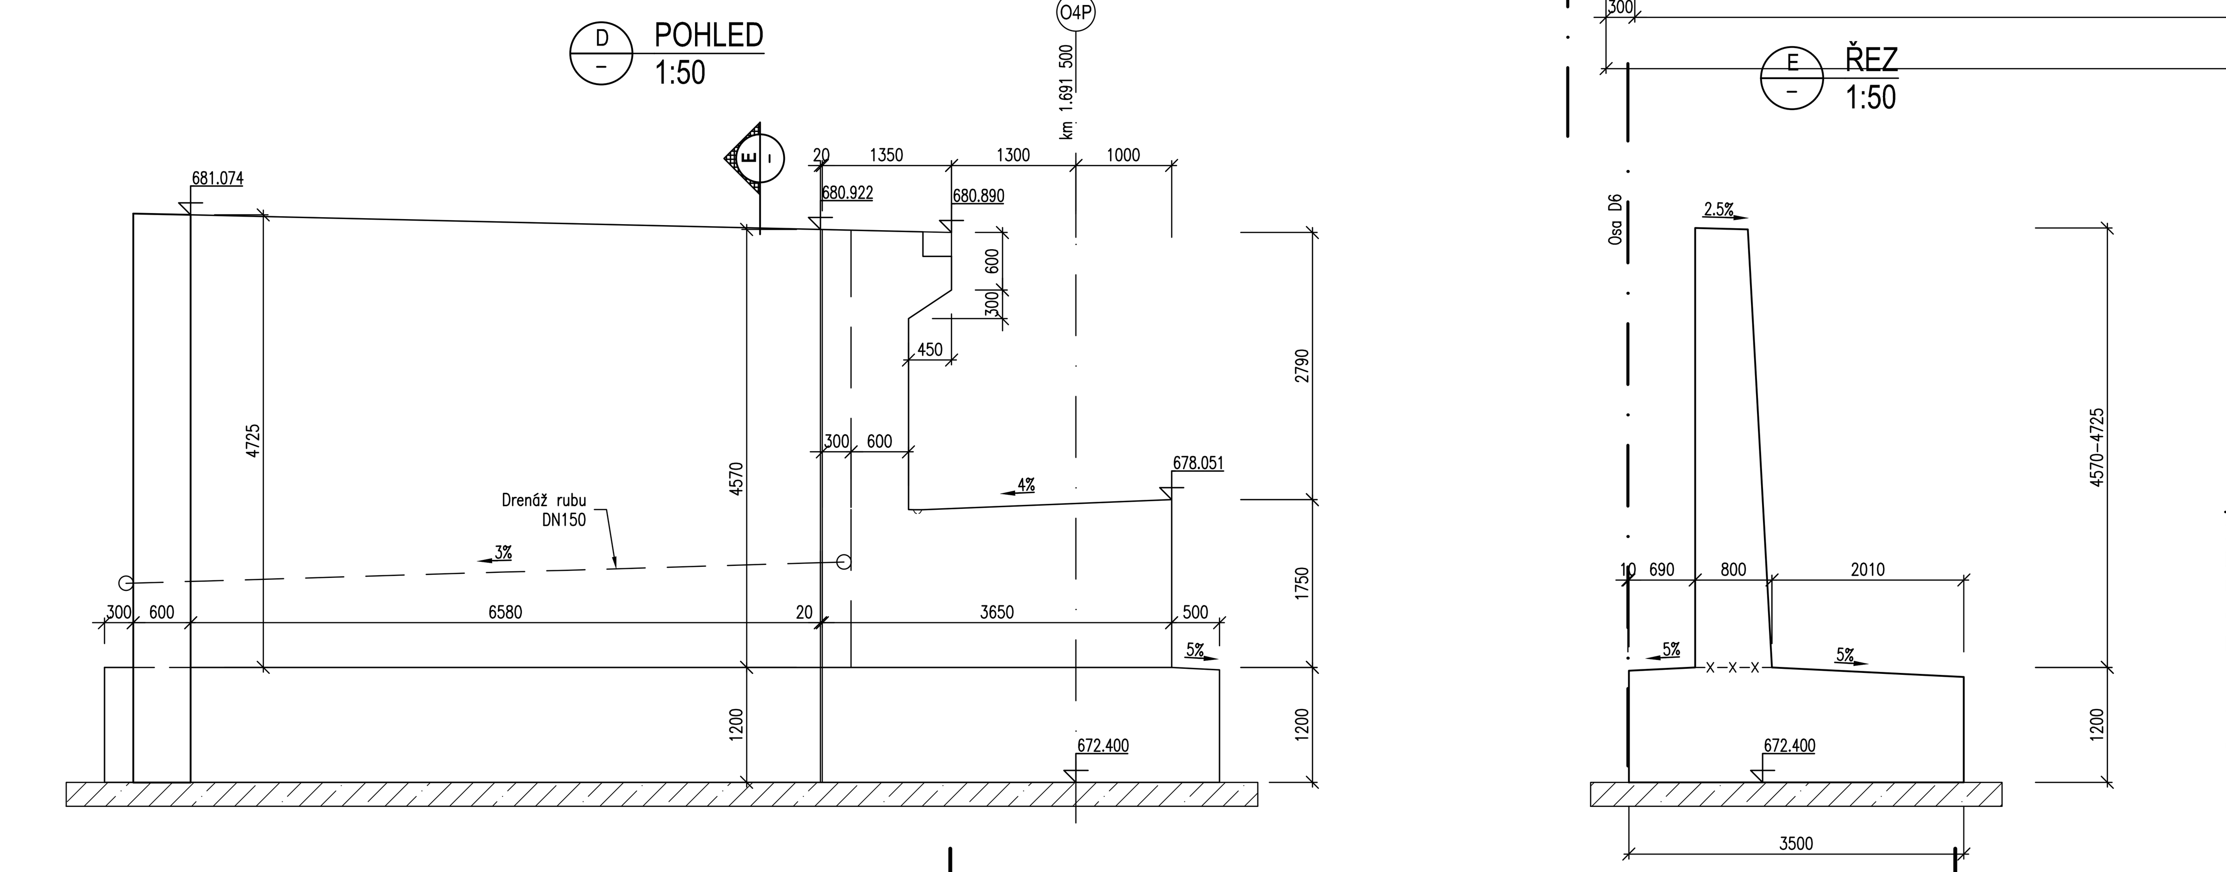

A Čepová nivelační značka

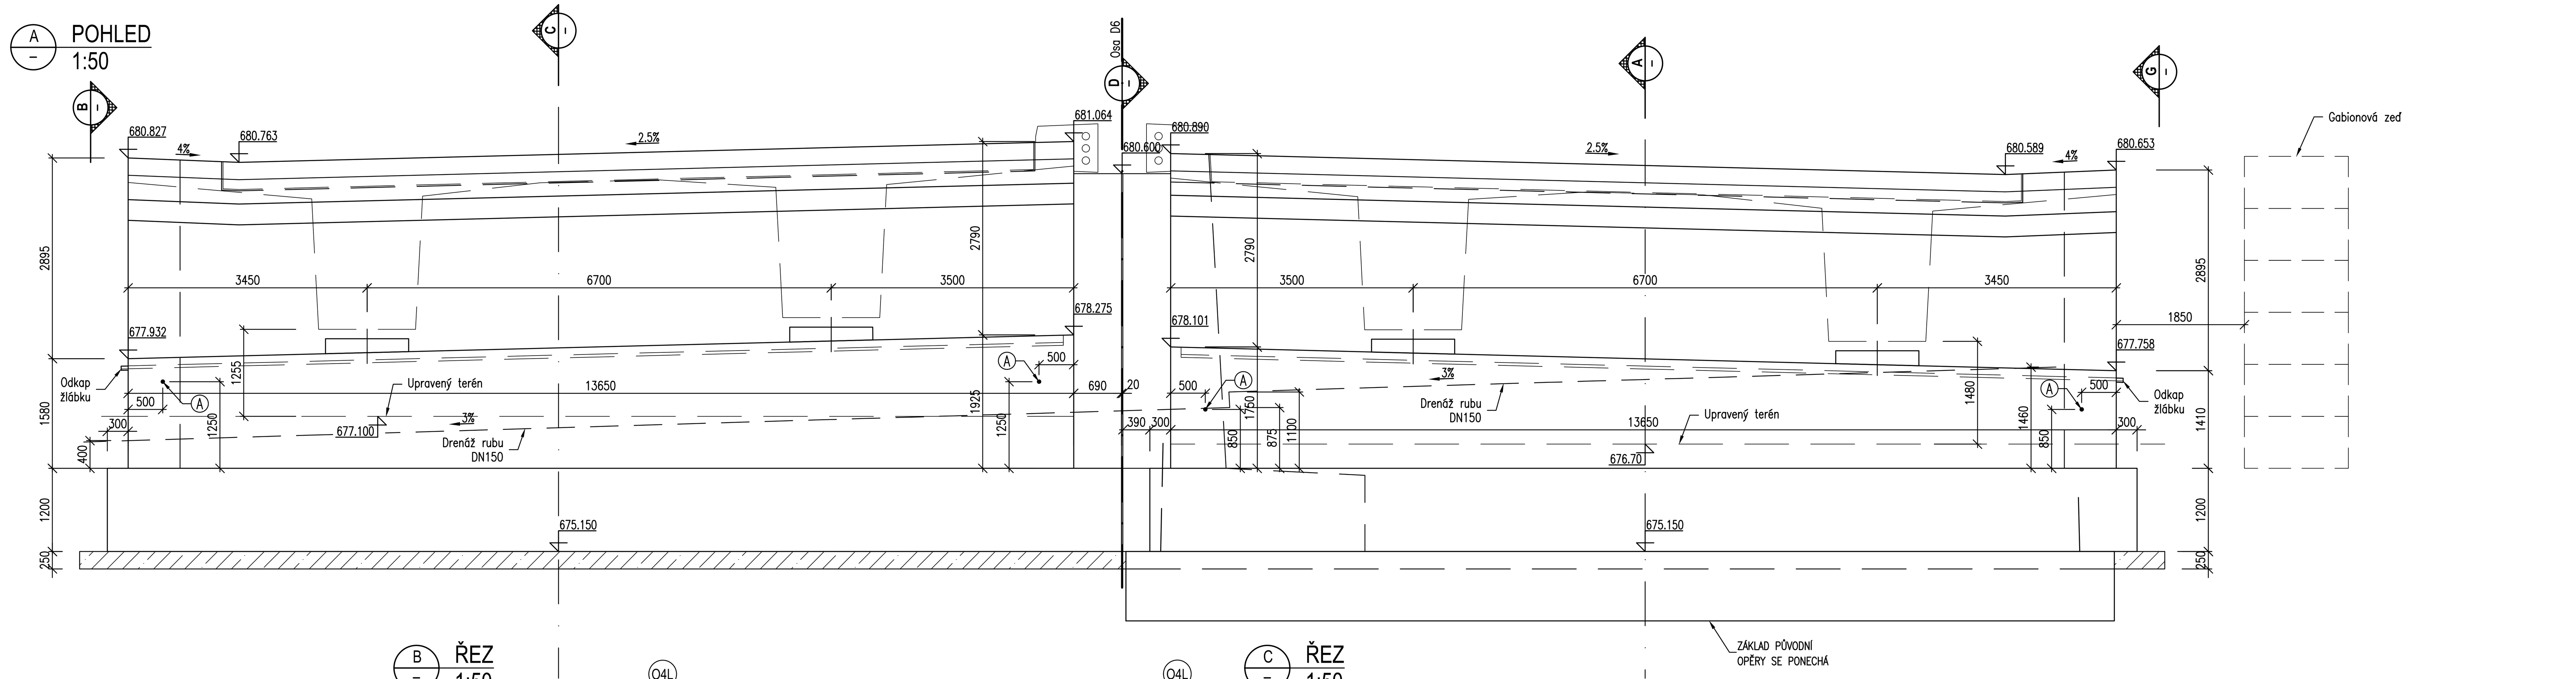

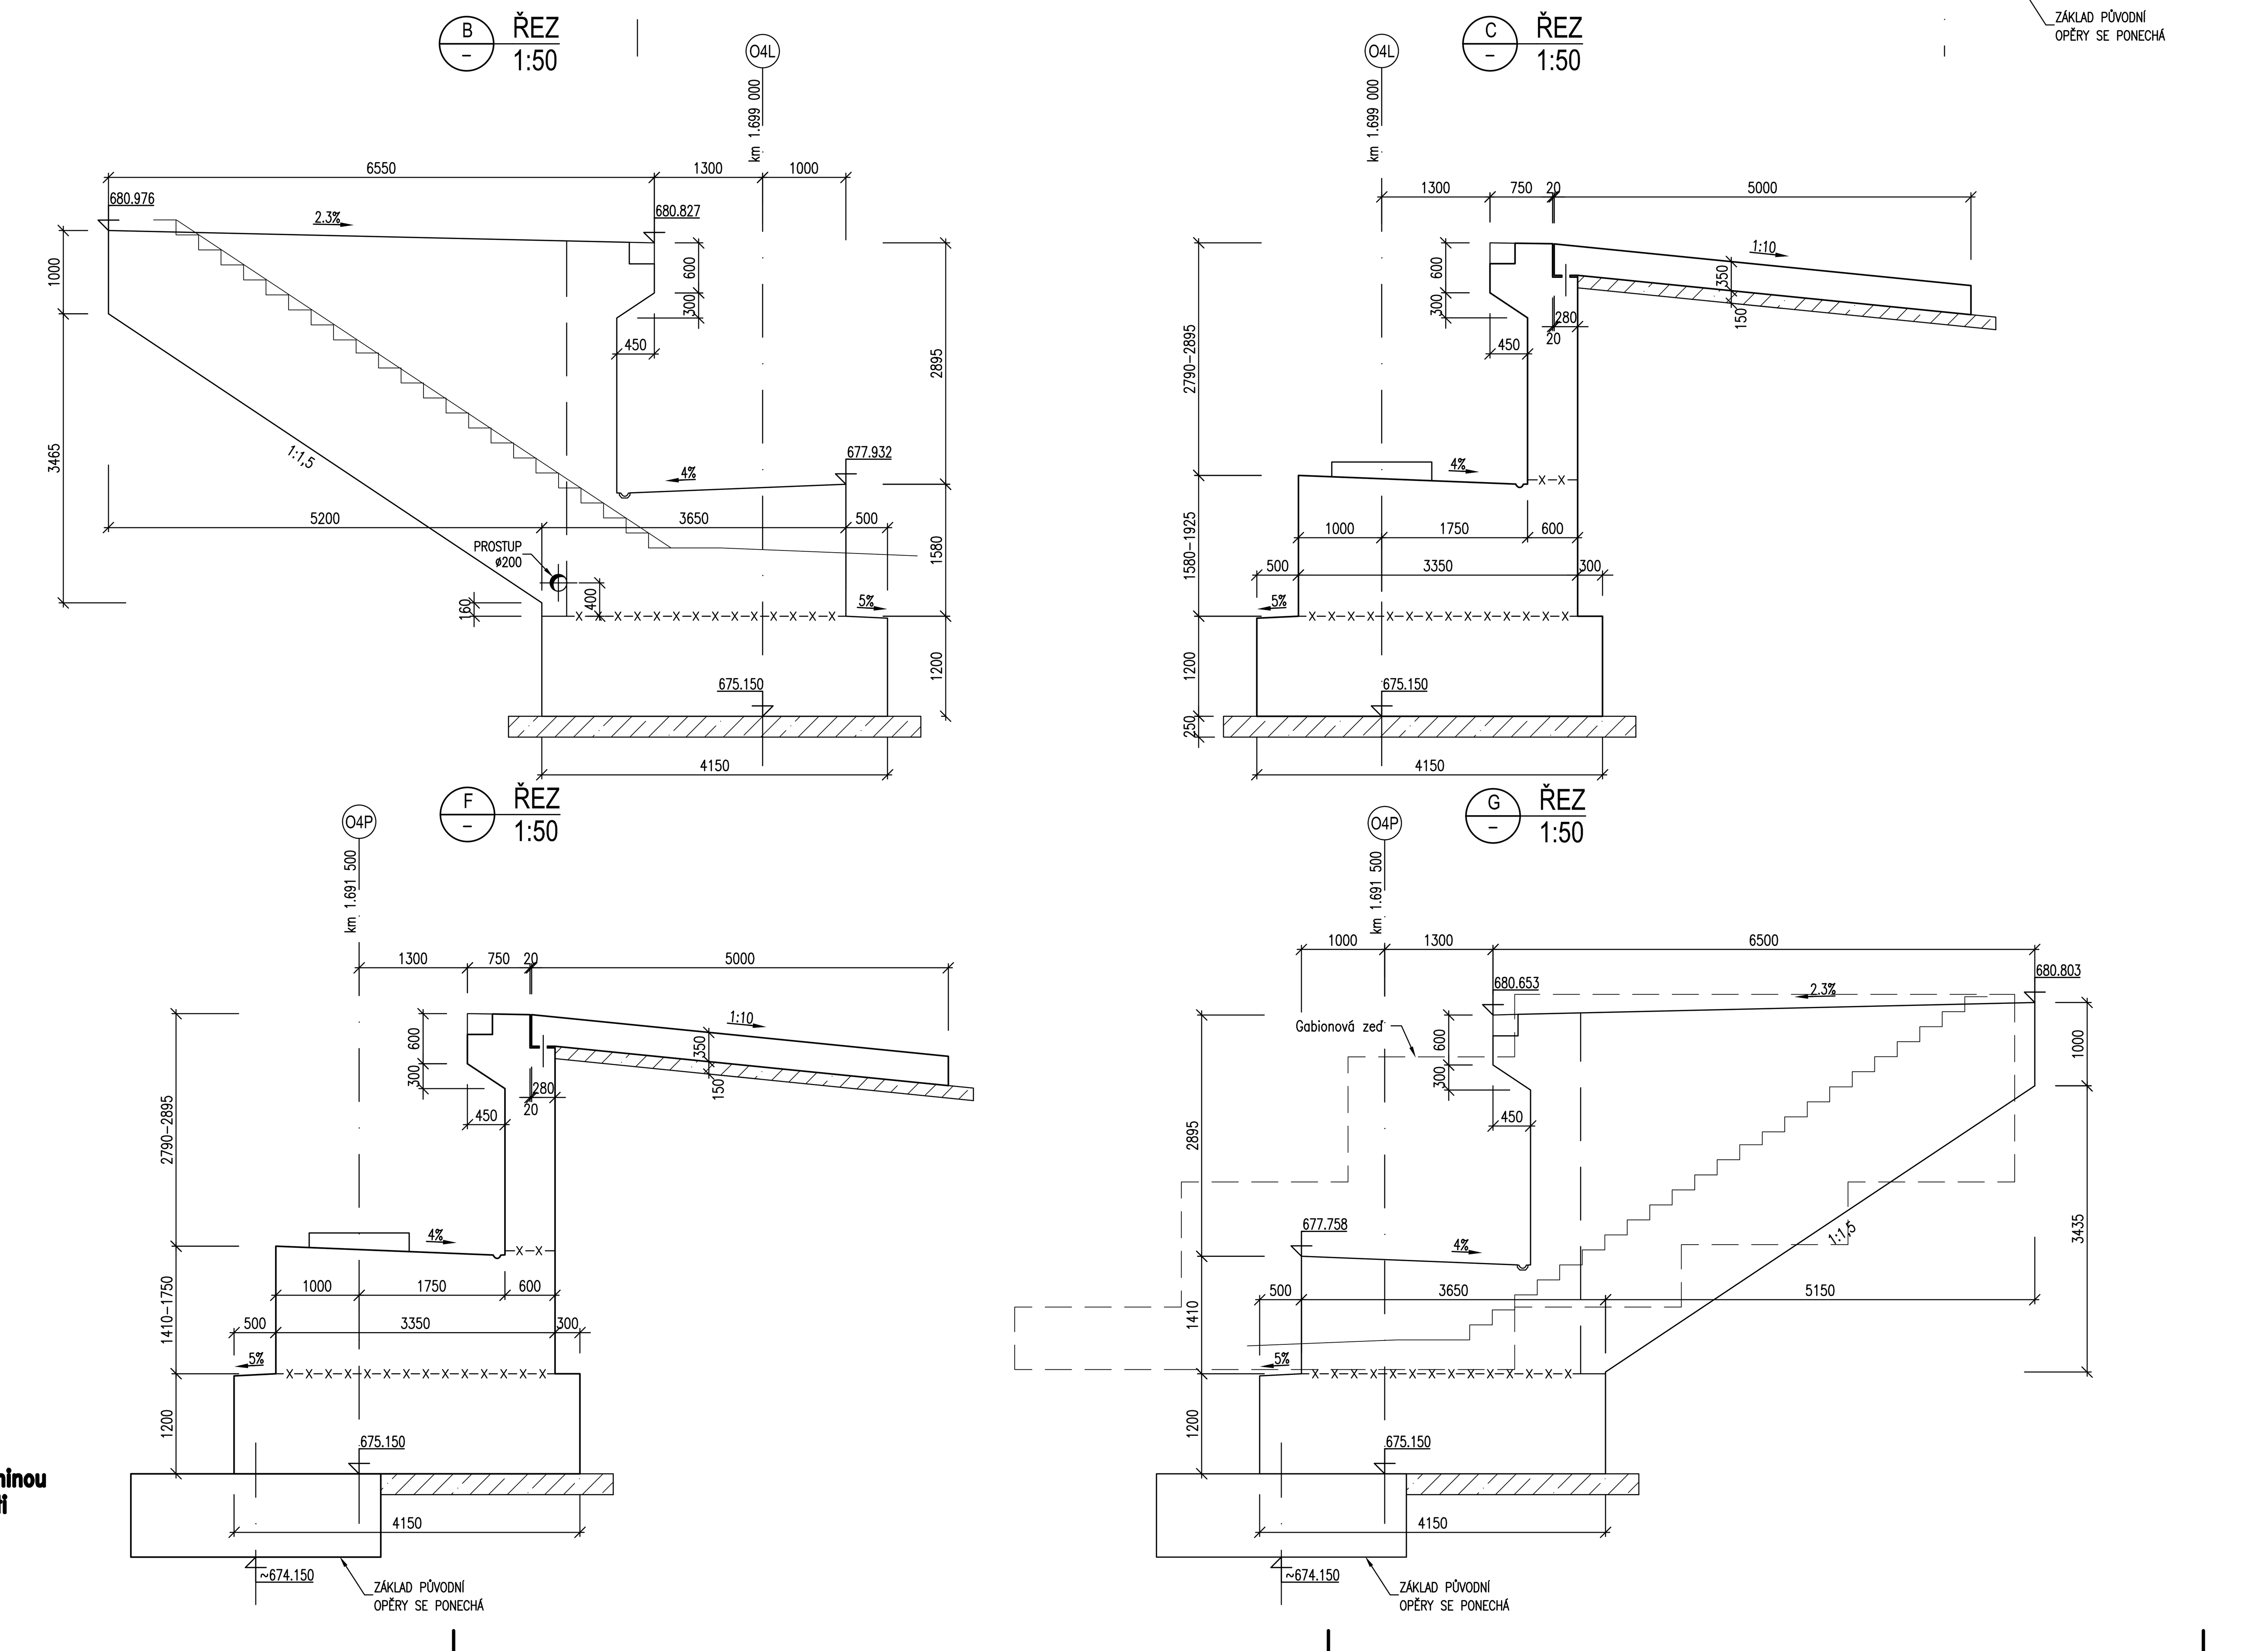

MATERIÁLY:

ZÁKLADY	C30/37 – XF1+XA2+XC2
DŘÍKY PILÍŘŮ	C35/45 – XF1+XD1+XC4
ÚLOŽNÉ PRAHY, ZÁV. ZDI, KŘÍDLA	C30/37 – XF4+XD3+XC4
OPĚRY	C30/37 – XF4+XD3+XC4
NOSNÁ KONSTRUKCE	C30/37 – XF4+XD3+XC4

TKP KAP 18 – BETONOVÉ KONSTRUKCE A MOSTY
ČSN EN 206+A2 – BETON – SPECIFIKACE, VLASTNOSTI, VÝROBA A SHODA

KATEGORIE POVRCH. ÚPRAVY:

Pohledové plochy C2d
Ostatní plochy C1a

Všechny plochy v trvalém kontaktu se zeminou budou opatřeny nátěry proti zemní vlhkosti ALP+2xALN

ČÁST D.2
SO 202

ČISTOPIS
Souřadnicový systém S-JTSK, Výškový systém Bpv

Objednatel:
ŘEDITELSTVÍ SILNIC A DÁLNIC
ŘEDITELSTVÍ SILNIC A DÁLNIC s. p.
Čerčanská 2023/12
140 00 Praha 4 – Krč

Zhotovitel PD: PRAGOPROJEKT, a.s., K Ryšánce 1668/16, 147 54 Praha 4, IČO: 45272387, www.pragoprojekt.cz, datová schránka: 4kifr54

Navrhl/vypracoval:	Zodpovědný projektant:	Zástupce zodpovědného projektanta:
Ing. Karolína Hédová	Ing. Martin BLATSKÝ	Ing. Jan BAŽIL
podpis:	podpis:	podpis:
Technická kontrola:	Hlavní inženýr projektu:	Zástupce hlavního inženýra projektu:
Ing. Kamil PEJCHAL	Ing. Pavel ŠLAPA	Ing. Radovan STANKOVEN
podpis:	podpis:	podpis:

PRAGOPROJEKT

Kraj:	KARLOVARSKÝ KRAJ	Číslo zakázky:	25–150–2
Místo stavby:	OLŠOVÁ VRATA, ANDĚLSKÁ HORA, ŽALMANOV, HORNÍ TAŠOVICE, BOCHOV	Číslo akce:	05–219
Objednatel:	ŘSD s. p., Čerčanská 2023/12, 140 00 Praha 4, IČO 65993390	Datum:	03/2026
Název stavby:	D6 OLŠOVÁ VRATA-ŽALMANOV, VD-ZDS	Formát:	
Objekt:	MOST NA D6 PŘES LOMNICKÝ POTOK V km 1,600 SO101	Měřítko:	
		Stupeň:	PDPS
		Souprava:	
Příloha:	TVAR OPĚRY OP4	Číslo přílohy:	13