
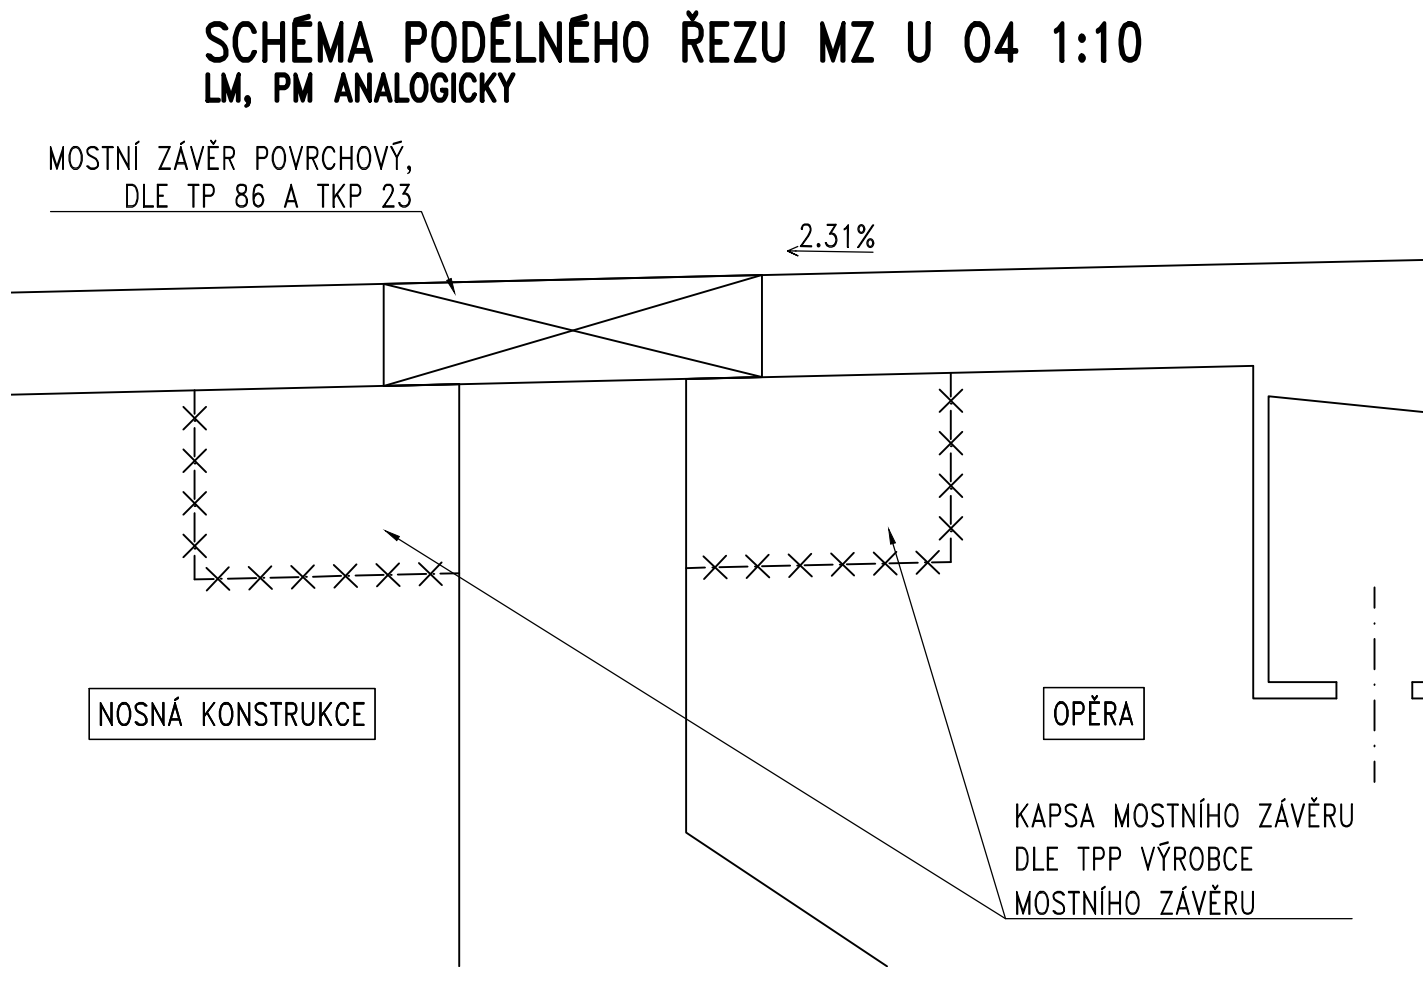


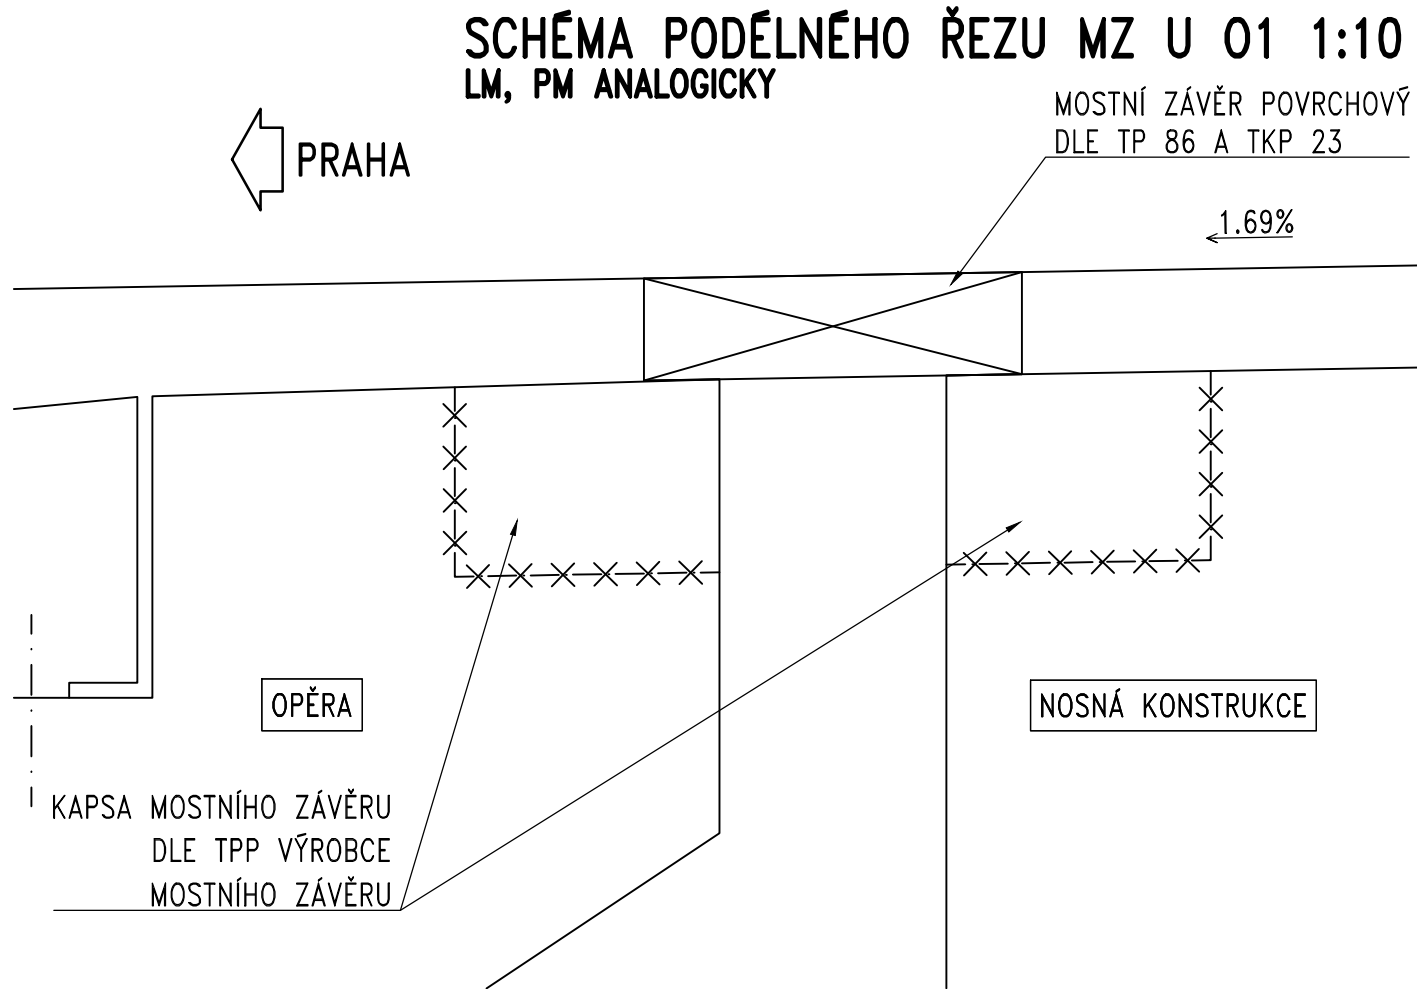

POZNÁMKY:

1. TYP MOSTNÍHO ZÁVĚRU: POVRCHOVÝ OCELOVÝ MOSTNÍ ZÁVĚR
2. POHYB NA 01: ±45 mm PODÉLNĚ, ±0 mm PŘÍČNĚ
3. POHYB NA 04: ±45 mm PODÉLNĚ, ±0 mm PŘÍČNĚ
4. ŠIKMOST MOSTNÍHO ZÁVĚRU K OSE MOSTU: 100g – KOLMÝ
5. TOLERANCE OSAZENÍ MOSTNÍHO ZÁVĚRU MUSÍ SPLŇOVAT TP86, KAP. 10.2
6. ŘEZ ZÁVĚREM JE VEDEN OSOU ZÁVĚRU
7. MOSTNÍ ZÁVĚRY BUDOU V PROSTŘEDÍ S VLIVEM BLUDNÝCH PROUDŮ Č. 4 DLE TP124
8. TŘÍDA PROVEDENÍ EXC3
9. MZ BUDE ZAPUŠTĚN MAX. 2 mm POD POVRCH PŘILEHLÉ VOZOVKY

PROTIKOROZNÍ OCHRANA:

- PKO JE NAVRŽENA V SOULADU S TKP KAP. 19B
- POUŽITÝ SYSTÉM MUSÍ BÝT SCHVÁLENÝ A UVEDENÝ NA www.pjpk.cz

STUPEŇ KOROZNÍ AGRESIVITY: C4


POŽADOVANÁ ŽIVOTNOST KONSTRUKCE: 30 let

POŽADOVANÁ ŽIVOTNOST PKO: 15 let

ODSTÍN RAL 7035 (LIGHT GREY)

NAVRŽENÁ SKLADBA PKO: IA

TRYSKÁNÍ NA Sa3	
ŽÁROVÝ Zn	100 μm
EPOXID DVOUKOMPONENTNÍ	200 μm
ALIFATICKÝ POLYURETAN	80 μm
CELKEM	380 μm

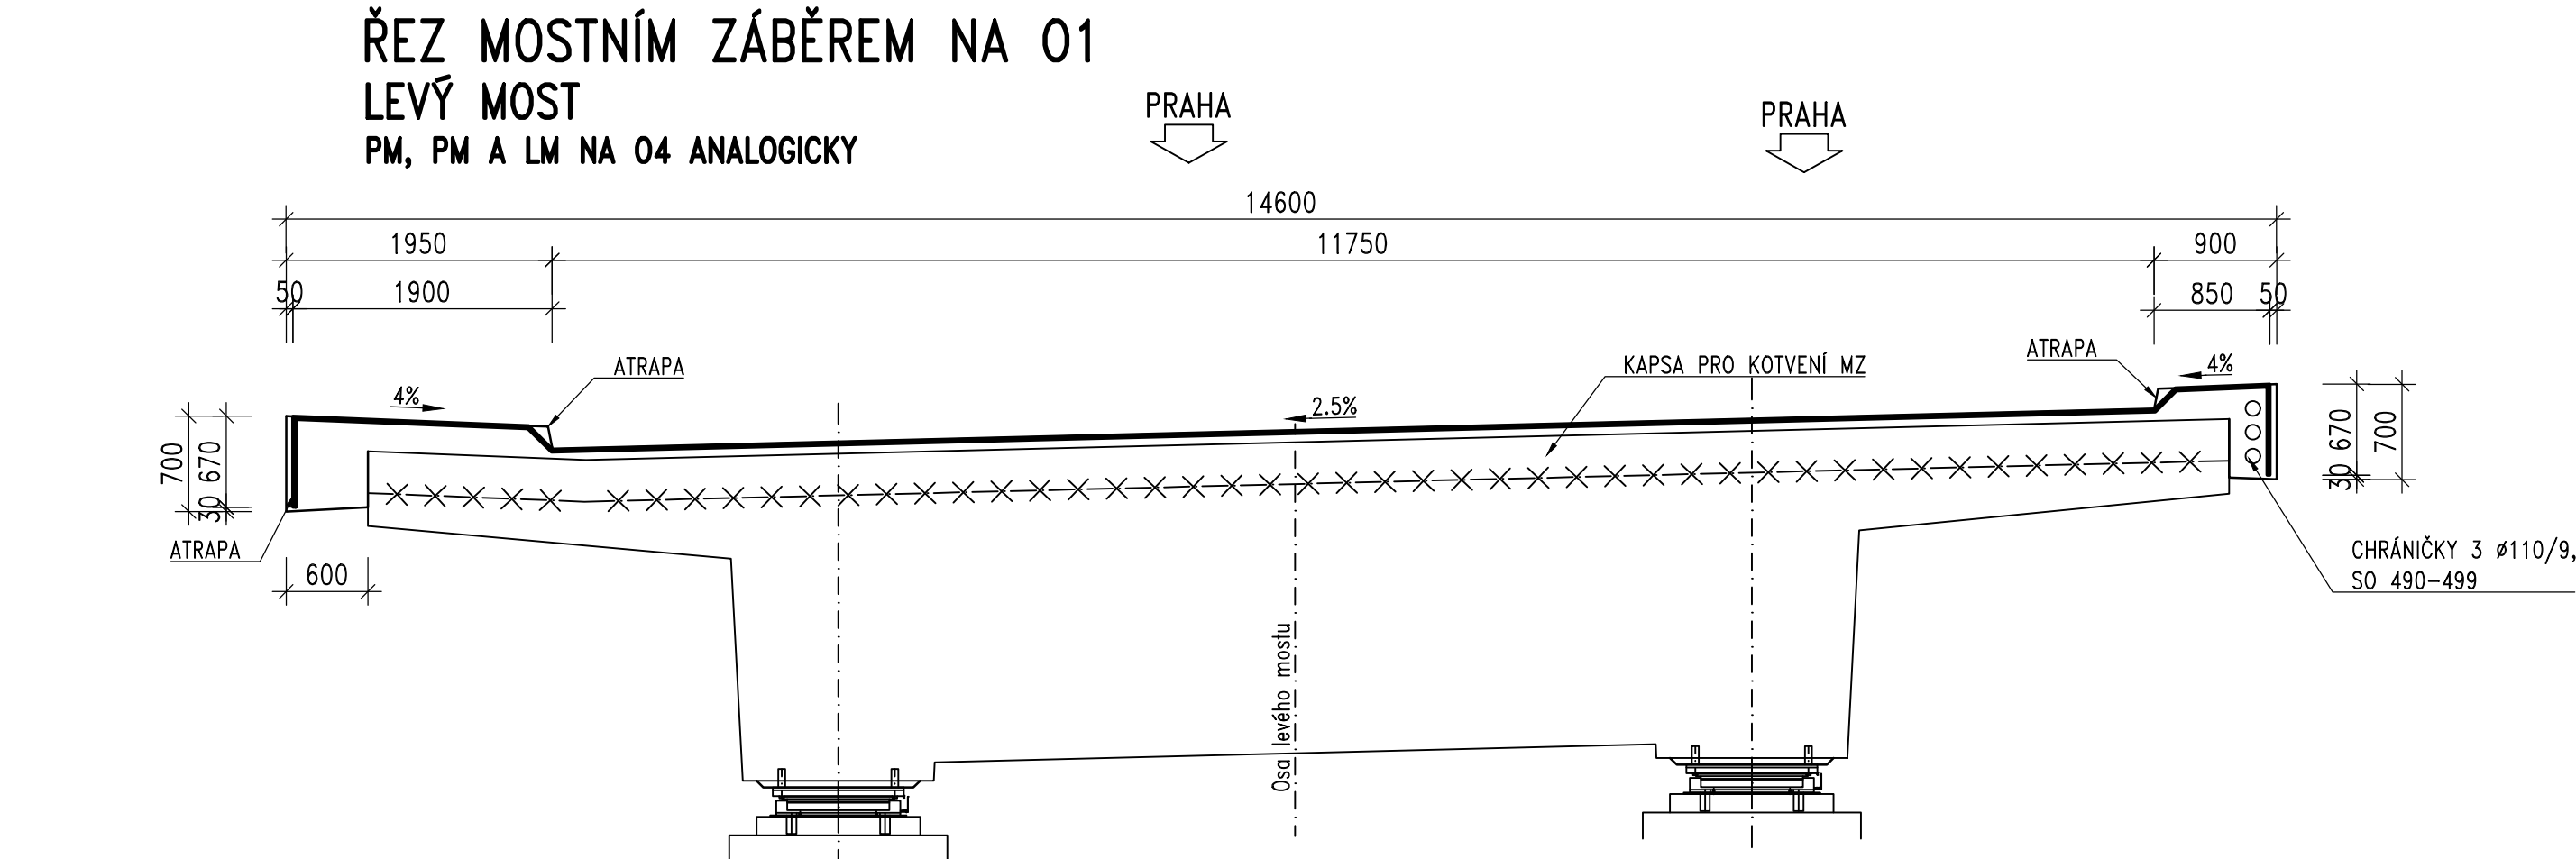

PŘEDPISY PRO PROVEDENÍ JEDNOTLIVÝCH KONSTRUKČNÍ ČÁSTÍ:

1. TKP KAP 23 – MOSTNÍ ZÁVĚRY
2. TP 89 – MOSTNÍ ZÁVĚRY
3. TKP KAP 19 – OCELOVÉ MOSTY A KONSTRUKCE – ČÁST B
4. TKP KAP 21 – IZOLACE PROTI VODĚ
5. ČSN EN 14188 – ZÁLIVKY A VLOŽKY DO SPÁR

ČÁST D.2
SO 202

ČISTOPIS


Souřadnicový systém S-JTSK, Výškový systém Bpv



ŘEDITELSTVÍ
SILNIC
A DÁLNIC

ŘEDITELSTVÍ SILNIC A DÁLNIC s. p.
Čerčanská 2023/12
140 00 Praha 4 – Krč

Objednatel:

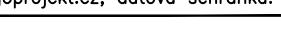Zhotovitel PD: PRAGOPROJEKT, a.s., K Ryšánce 1668/16, 147 54 Praha 4, IČO: 45272387, www.pragoprojekt.cz, datová schránka: 4kifr54			
Navrhl/vypracoval: Ing. Karolína HEDOVÁ podpis: <i>K. Hedová</i>	Zodpovědný projektant: Ing. Martin BLAŽSKÝ podpis: <i>Bl</i>	Zástupce zodpovědného projektanta: Ing. Jan BAZIL podpis: <i>Bazil</i>	
Technická kontrola: Ing. Kamil PEJCHAL podpis: <i>Kamil Pejchal</i>	Hlavní inženýr projektu: Ing. Pavel ŠLAPA podpis: <i>Slapa</i>	Zástupce hlavního inženýra projektu: Ing. Radovan STANKOVEN podpis: <i>Stankoven</i>	
PRAGOPROJEKT			

Kraj:	KARLOVARSKÝ KRAJ	Číslo zakázky:	25-150-2
Místo stavby:	OLŠOVÁ VRATA, ANDĚLSKÁ HORA, ŽALMANOV, HORNÍ TAŠOVICE, BOCHOV	Číslo akce:	05-219
Objednatel:	ŘSD s. p., Čerčanská 2023/12, 140 00 Praha 4, IČO 65993390	Datum:	03/2026
Název stavby:	D6 OLŠOVÁ VRATA-ŽALMANOV, VD-ZDS		
Objekt:	MOST NA D6 PŘES LOMNICKÝ POTOK V km 1,600 SO101		
Příloha:	MOSTNÍ ZÁVĚRY		
			Stupeň: PDPS
			Číslo přílohy: 16