





SCHÉMA PŘEDPĚTÍ 1:200/100

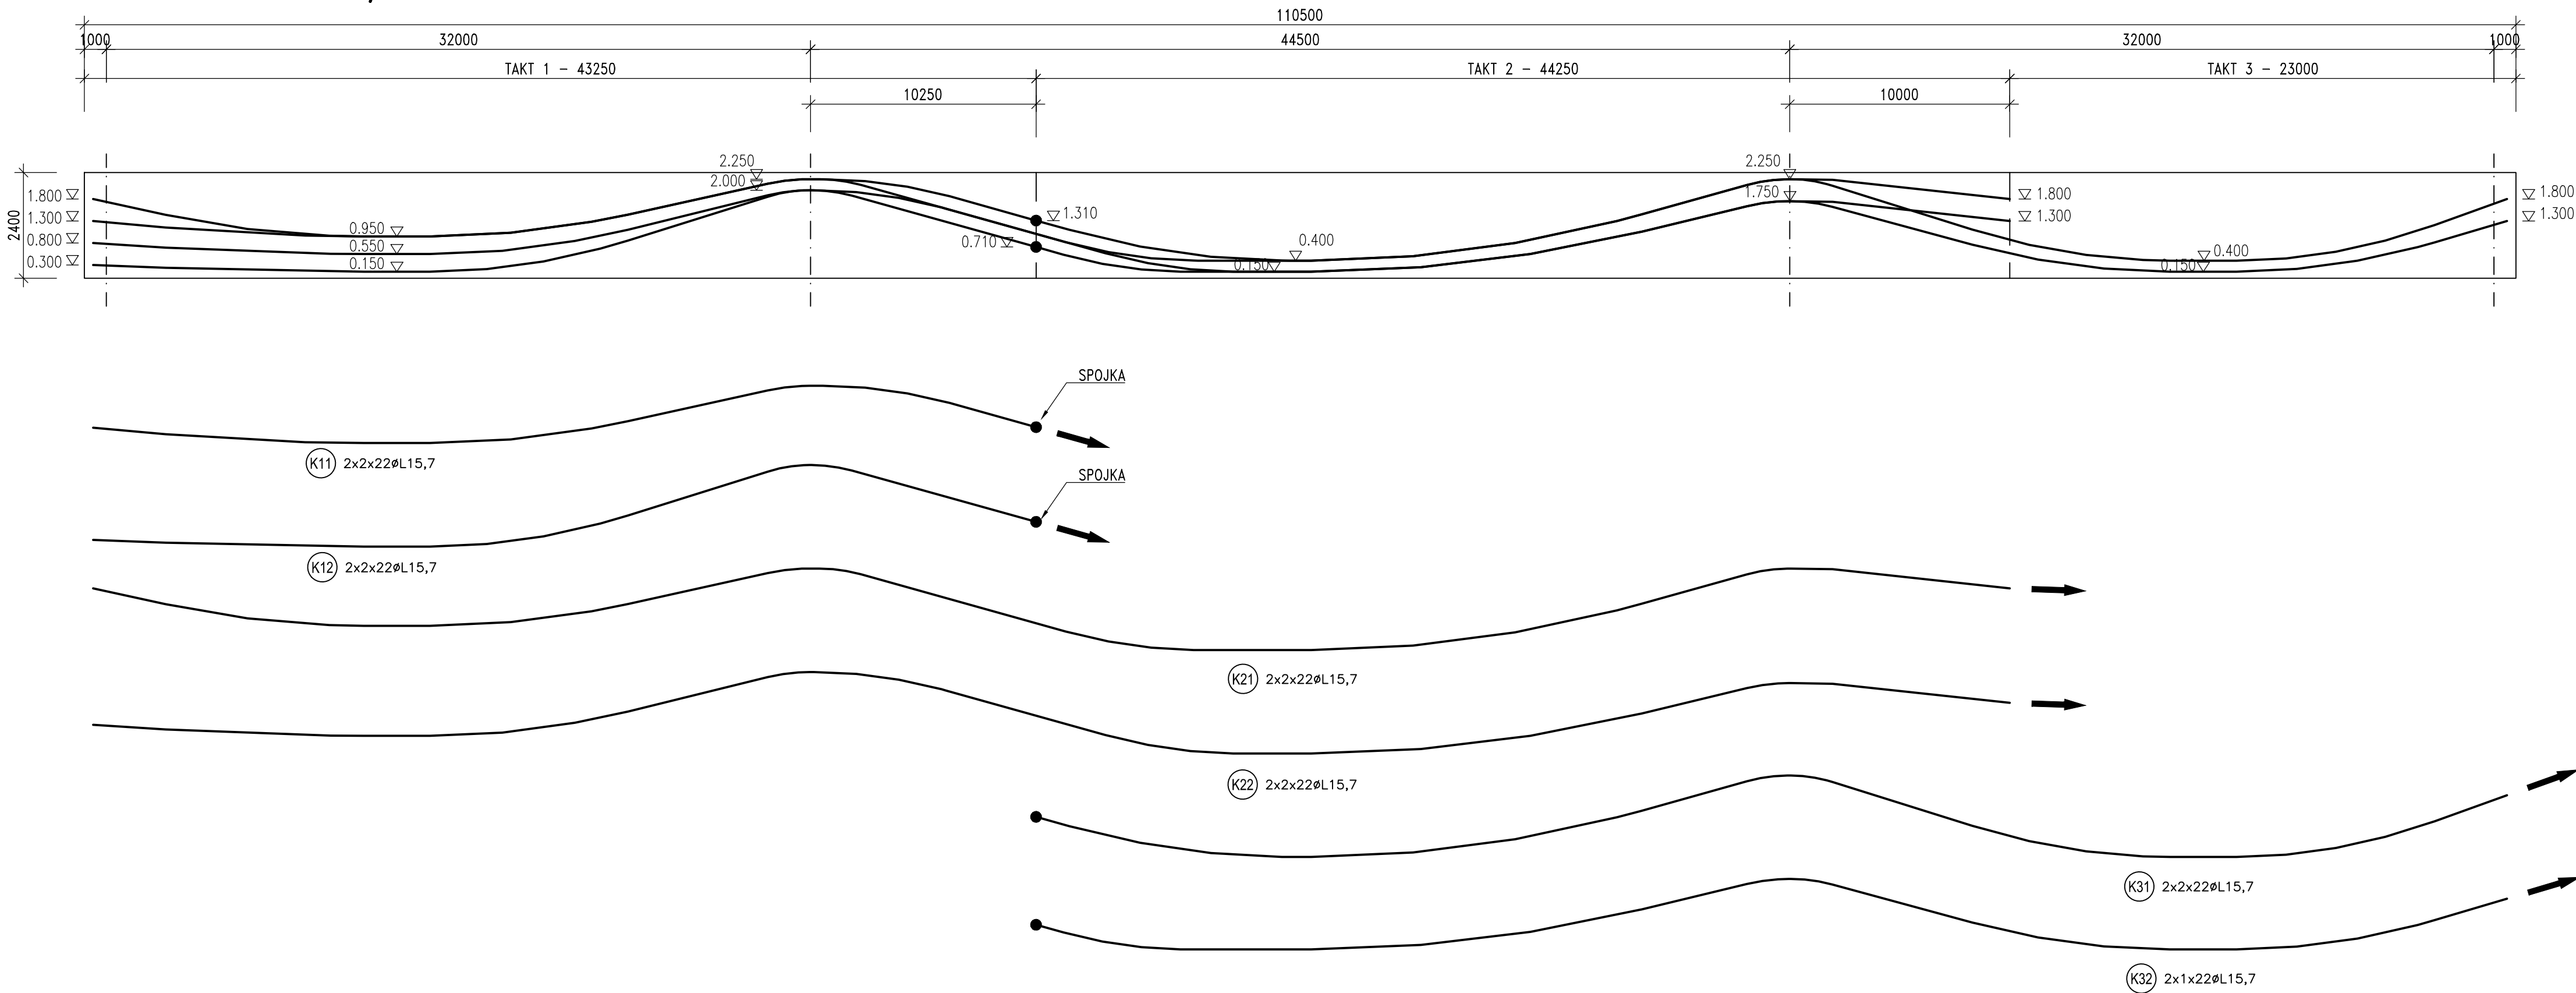

ŘEZ V POLI 1:50

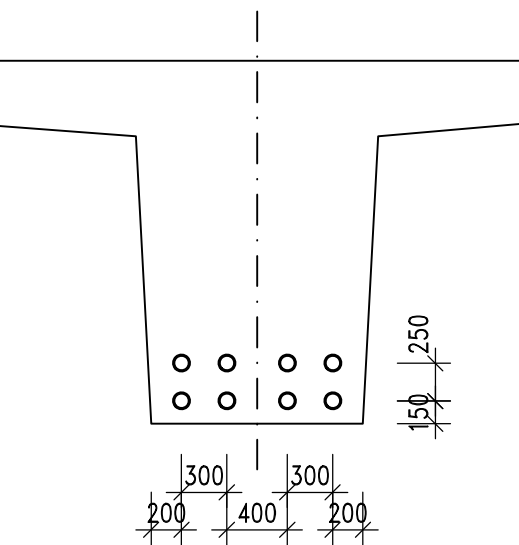

ŘEZ NAD PILÍŘEM 1:50

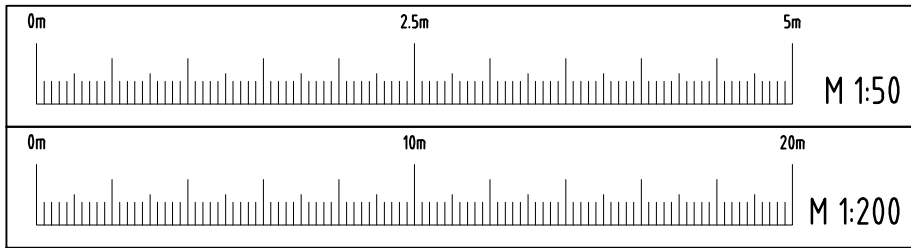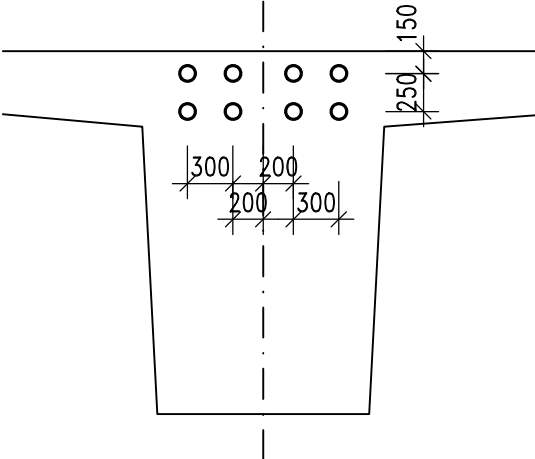

MATERIÁLY

BETON DLE TKP18
NOSNÁ KONSTRUKCE C35/45–XF2 (XD1, XC4)
DOBETONÁVKA KOTEV A MZ C30/37–XF4 (XD3, XC4)
BETONÁŘSKÁ VÝZTUŽ
B500 B V BĚŽNÝCH PROFILECH
PŘEDPÍNACÍ VÝZTUŽ
Y1860S7 15.7mm (150mm2) S VELMI NÍZKOU RELAXACÍ
STUPEŇ OCHRANY PL2
KOTEVNÍ NAPĚTÍ 1400 MPa

VÝKAZ PŘEDPÍNACÍ VÝZTUŽE

NÁZEV	K A B E L Y			
	L[m]	KS lan	KS kabelů	L*KS[m]
K11	43.33	22	4	173
K12	43.67	22	4	175
K21	88.38	22	4	354
K22	88.18	22	4	353
K31	68.30	22	4	273
K32	67.89	22	4	272
CELKEM				1599

HMOTNOST LAN CELKEM (t) - 1 MOST 41.42
HMOTNOST LAN CELKEM (t) - 2 MOSTY 82.84
UVAŽOVÁNA POUZE ČISTÁ DÉLKA KABELŮ BEZ PŘESAHŮ PRO NAPNUTÍ

ČÁST D.2
SO 202

ČISTOPIS

Souřadnicový systém S–JTSK, Výškový systém Bpv

ŘEDITELSTVÍ
SILNIC
A DÁLNIC

Objednatel:
ŘEDITELSTVÍ SILNIC A DÁLNIC s. p.
Čerčanská 2023/12
140 00 Praha 4 – Krč

Zhotovitel PD: PRAGOPROJEKT, a.s., K Ryšánce 1668/16, 147 54 Praha 4, IČO: 45272387, www.pragoprojekt.cz, datová schránka: 4kfr54

Navrh/vypracoval:
Ing. Karolína HEDVÁ
podpis: *KH*

Zodpovědný projektant:
Ing. Martin BLATSKÝ
podpis: *MB*

Zástupce zodpovědného projektanta:
Ing. Jan BAZIL
podpis: *JB*

Technická kontrola:
Ing. Kamil PEJCHAL
podpis: *KP*

Hlavní inženýr projektu:
Ing. Pavel SLÁPA
podpis: *PS*

Zástupce hlavního inženýra projektu:
Ing. Radovan STANKOVEN
podpis: *RS*

Kraj:	KARLOVARSKÝ KRAJ	Číslo zakázky:	25–150–2
Místo stavby:	OLŠOVÁ VRATA, ANDĚLSKÁ HORA, ŽALMANOV, HORNÍ TAŠOVICE, BOCHOV	Číslo akce:	05–219
Objednatel:	RSD s. p., Čerčanská 2023/12, 140 00 Praha 4, IČO 65993390	Datum:	03/2026
Název stavby:	D6 OLŠOVÁ VRATA-ŽALMANOV, VD-ZDS	Formát:	
Objekt:	Most na D6 přes Lomnický potok v km 1,600 SO 101	Měřítko:	
Příloha:	TVAR NOSNÉ KONSTRUKCE	Stupeň:	Souprava:
		Číslo přílohy:	