
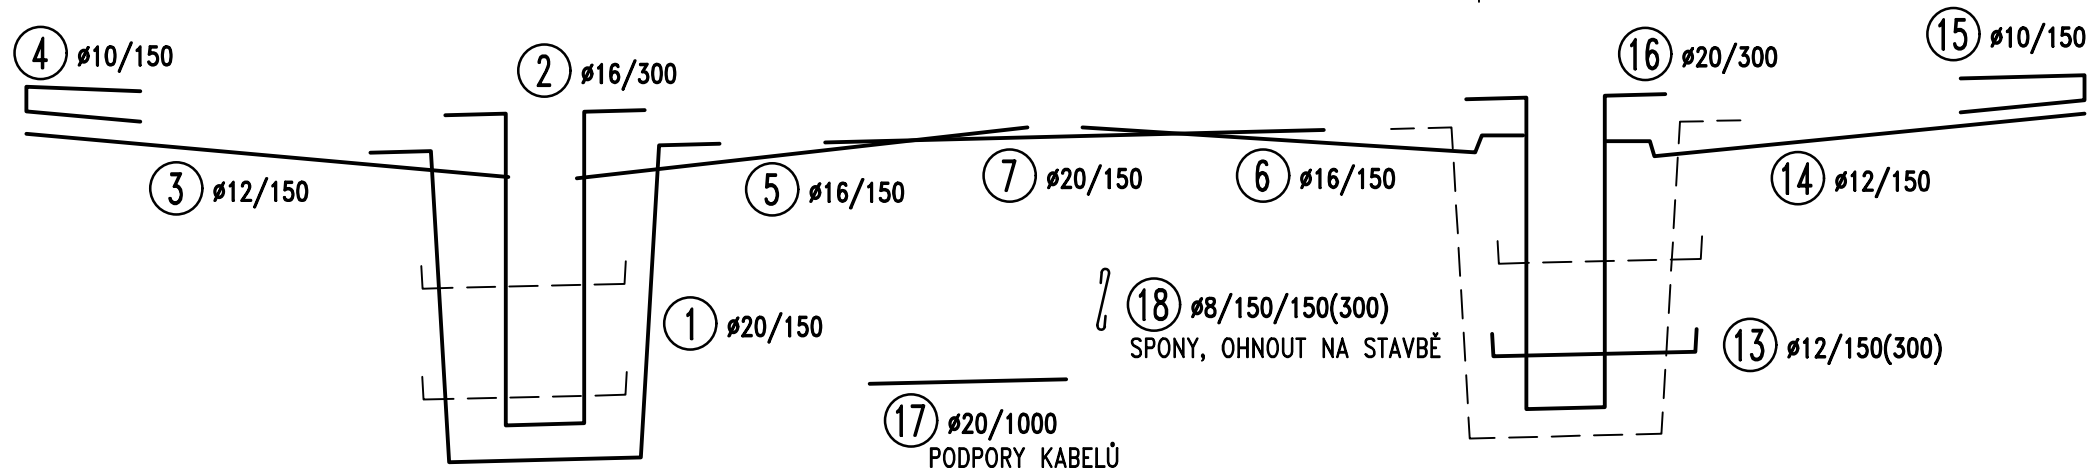


VZOROVÝ PŘÍČNÝ ŘEZ 1:50
V POLI

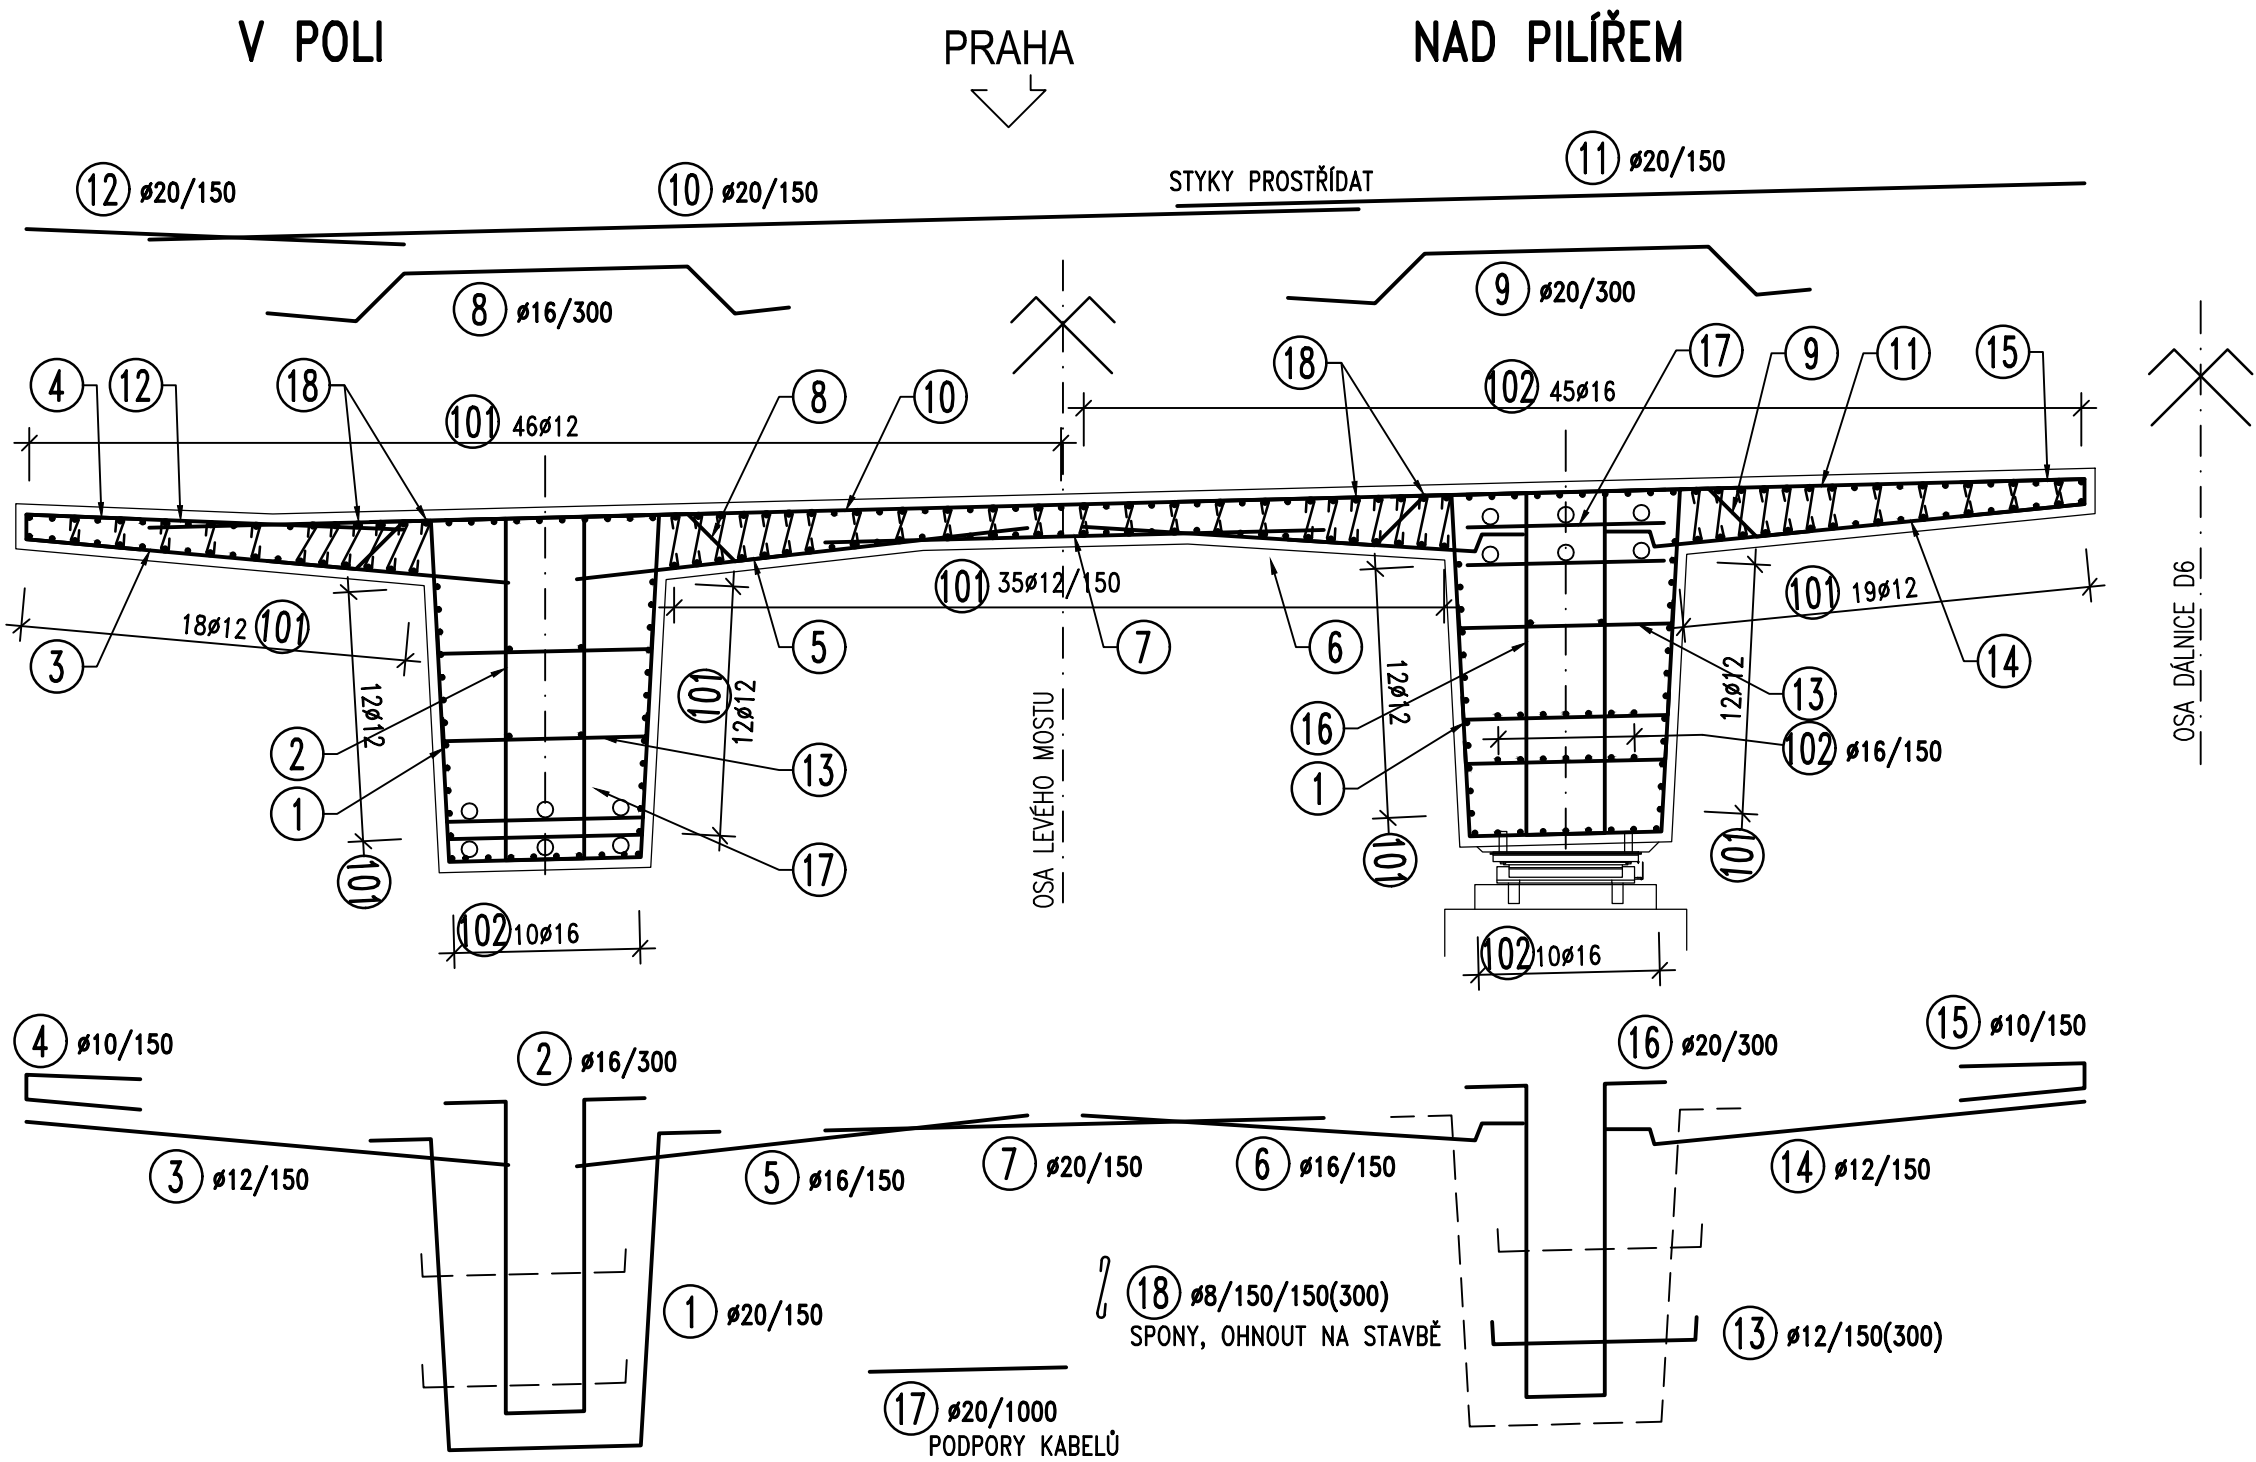

KRYTÍ VÝZTUŽE

Horní povrch: MINIMÁLNÍ 35 mm, JMENOVITÉ 45 mm
Jinde: MINIMÁLNÍ 45 mm, JMENOVITÉ 55 mm

POZNÁMKY:

- VEŠKERÁ VÝZTUŽ PROCHÁZEJÍCÍ PRACOVNÍ SPÁROU BUDE OPATŘENA OCHRANNÝM EPOX. NÁTĚREM VE VZDÁLENOSTI $\pm 100\text{mm}$ NA KAŽDOU STRANU OD PRACOVNÍ SPÁRY.
- VEŠKERÁ VÝZTUŽ JE VÁZANÁ. PROVAŘENÍ VÝZTUŽE KVŮLI BLUDNÝM PROUDŮM BUDE PROVEDENO DLE TP 124
- KRYTÍ VÝZTUŽE JE UVAŽOVÁNO NA SPONY.

PŘEDPISY PRO PROVEDENÍ JEDNOTLIVÝCH KONSTRUKČNÍ ČÁSTÍ:

- TKP KAP 18 – BETONOVÉ KONSTRUKCE A MOSTY
- ČSN EN 206+A2 – BETON – SPECIFIKACE, VLASTNOSTI, VÝROBA A SHODA
- TP 124 – ZÁKLADNÍ OCHRANNÁ OPATŘENÍ PRO OMEZENÍ VLIVU BLUDNÝCH PROUDŮ NA MOSTNÍ OBJEKTY A OSTATNÍ BETONOVÉ KONSTRUKCE POZEMNÍCH KOMUNIKACÍ
- TP 193 – SVAŘOVÁNÍ BETONÁŘSKÉ VÝZTUŽE A JINÉ DRUHY SPOJŮ ČSN EN ISO 17660–2
SVAŘOVÁNÍ – SVAŘOVÁNÍ BETONÁŘSKÉ OCELI ČÁST 2: NENOSNÉ SVAROVÉ SPOJE

= ROZMĚRY OHÝBANÝCH VLOŽEK JSOU ROZMĚRY NA VNĚJŠÍ POVRCH
= ZAKŘIVENÍ VLOŽEK JSOU UDÁVÁNA POLOMĚREM OHÝBACÍHO TRNU
= POKUD NENÍ NA VÝKRESE UVEDENO JINAK, JE UVAŽOVÁN MINIMÁLNÍ POLOMĚR OHYBU

VÝKAZ VÝZTUŽE - NOSNÁ KONSTRUKCE

průměr mm	DĚLKA DLE PROFILU										
	8 B500B	10 B500B	12 B500B	14 B500B	16 B500B	18 B500B	20 B500B	22 B500B	25 B500B	28 B500B	32 B500B
8	2148.2										
10		0.0									
12			10741.1								
14				0.0							
16					35445.7						
18						0.0					
20							42964.4				
22								0.0			
25									16111.7		
28										0.0	
32											0.0
	2148.2	0.0	10741.1	0.0	35445.7	0.0	42964.4	0.0	16111.7	0.0	0.0
Hm. 1 bm	0.395	0.617	0.888	1.209	1.579	1.998	2.467	2.985	3.854	4.834	6.314
Hm. prof.	848.5	0.0	9538.1	0.0	55968.7	0.0	105993.3	0.0	62094.4	0.0	0.0
HMOTNOST CELKEM 1 MOST (kg)											234443
HMOTNOST CELKEM 2 MOSTY (kg)											468886

ČÁST D.2
SO 202

ČISTOPIS

**ŘEDITELSTVÍ
SILNIC
A DÁLNIC**

Objednatel:
ŘEDITELSTVÍ SILNIC A DÁLNIC s. p.
Čerčanská 2023/12
140 00 Praha 4 – Krč

Zhotovitel PD: PRAGOPROJEKT, a.s., K Ryšánce 1668/16, 147 54 Praha 4, IČO: 45272387, www.pragoprojekt.cz, datová schránka: 4kifr54

Navrhl/vypracoval: Ing. Karolína HEDOVÁ podpis: <i>Karolína Hedová</i>	Zodpovědný projektant: Ing. Martin BLATSKÝ podpis: <i>Martin Blatský</i>	Zástupce zodpovědného projektanta: Ing. Jan BAZIL podpis: <i>Jan Bazil</i>	
Technická kontrola: Ing. Kamil PEJCHAL podpis: <i>Kamil Pechal</i>	Hlavní inženýr projektu: Ing. Pavel SLAPA podpis: <i>Pavel Slapa</i>	Zástupce hlavního inženýra projektu: Ing. Radovan STANKOVEN podpis: <i>Radovan Stankoven</i>	

Kraj: KARLOVARSKÝ KRAJ	Číslo zakázky: 25–150–2
Místo stavby: OLŠOVÁ VRATA, ANDĚLSKÁ HORA, ŽALMANOV, HORNÍ TAŠOVICE, BOCHOV	Číslo akce: 05–219
Objednatel: ŘSD s. p., Čerčanská 2023/12, 140 00 Praha 4, IČO 65993390	Datum: 03/2026
Název stavby: D6 OLŠOVÁ VRATA-ŽALMANOV, VD-ZDS	Formát: Měřítko: Stupeň: Souprava: PDPs
Objekt: Most na D6 přes Lomnický potok v km 1,600 SO 101	Číslo přílohy: 19
Příloha: SCHÉMA VÝZTUŽE NOSNÉ KONSTRUKCE	