


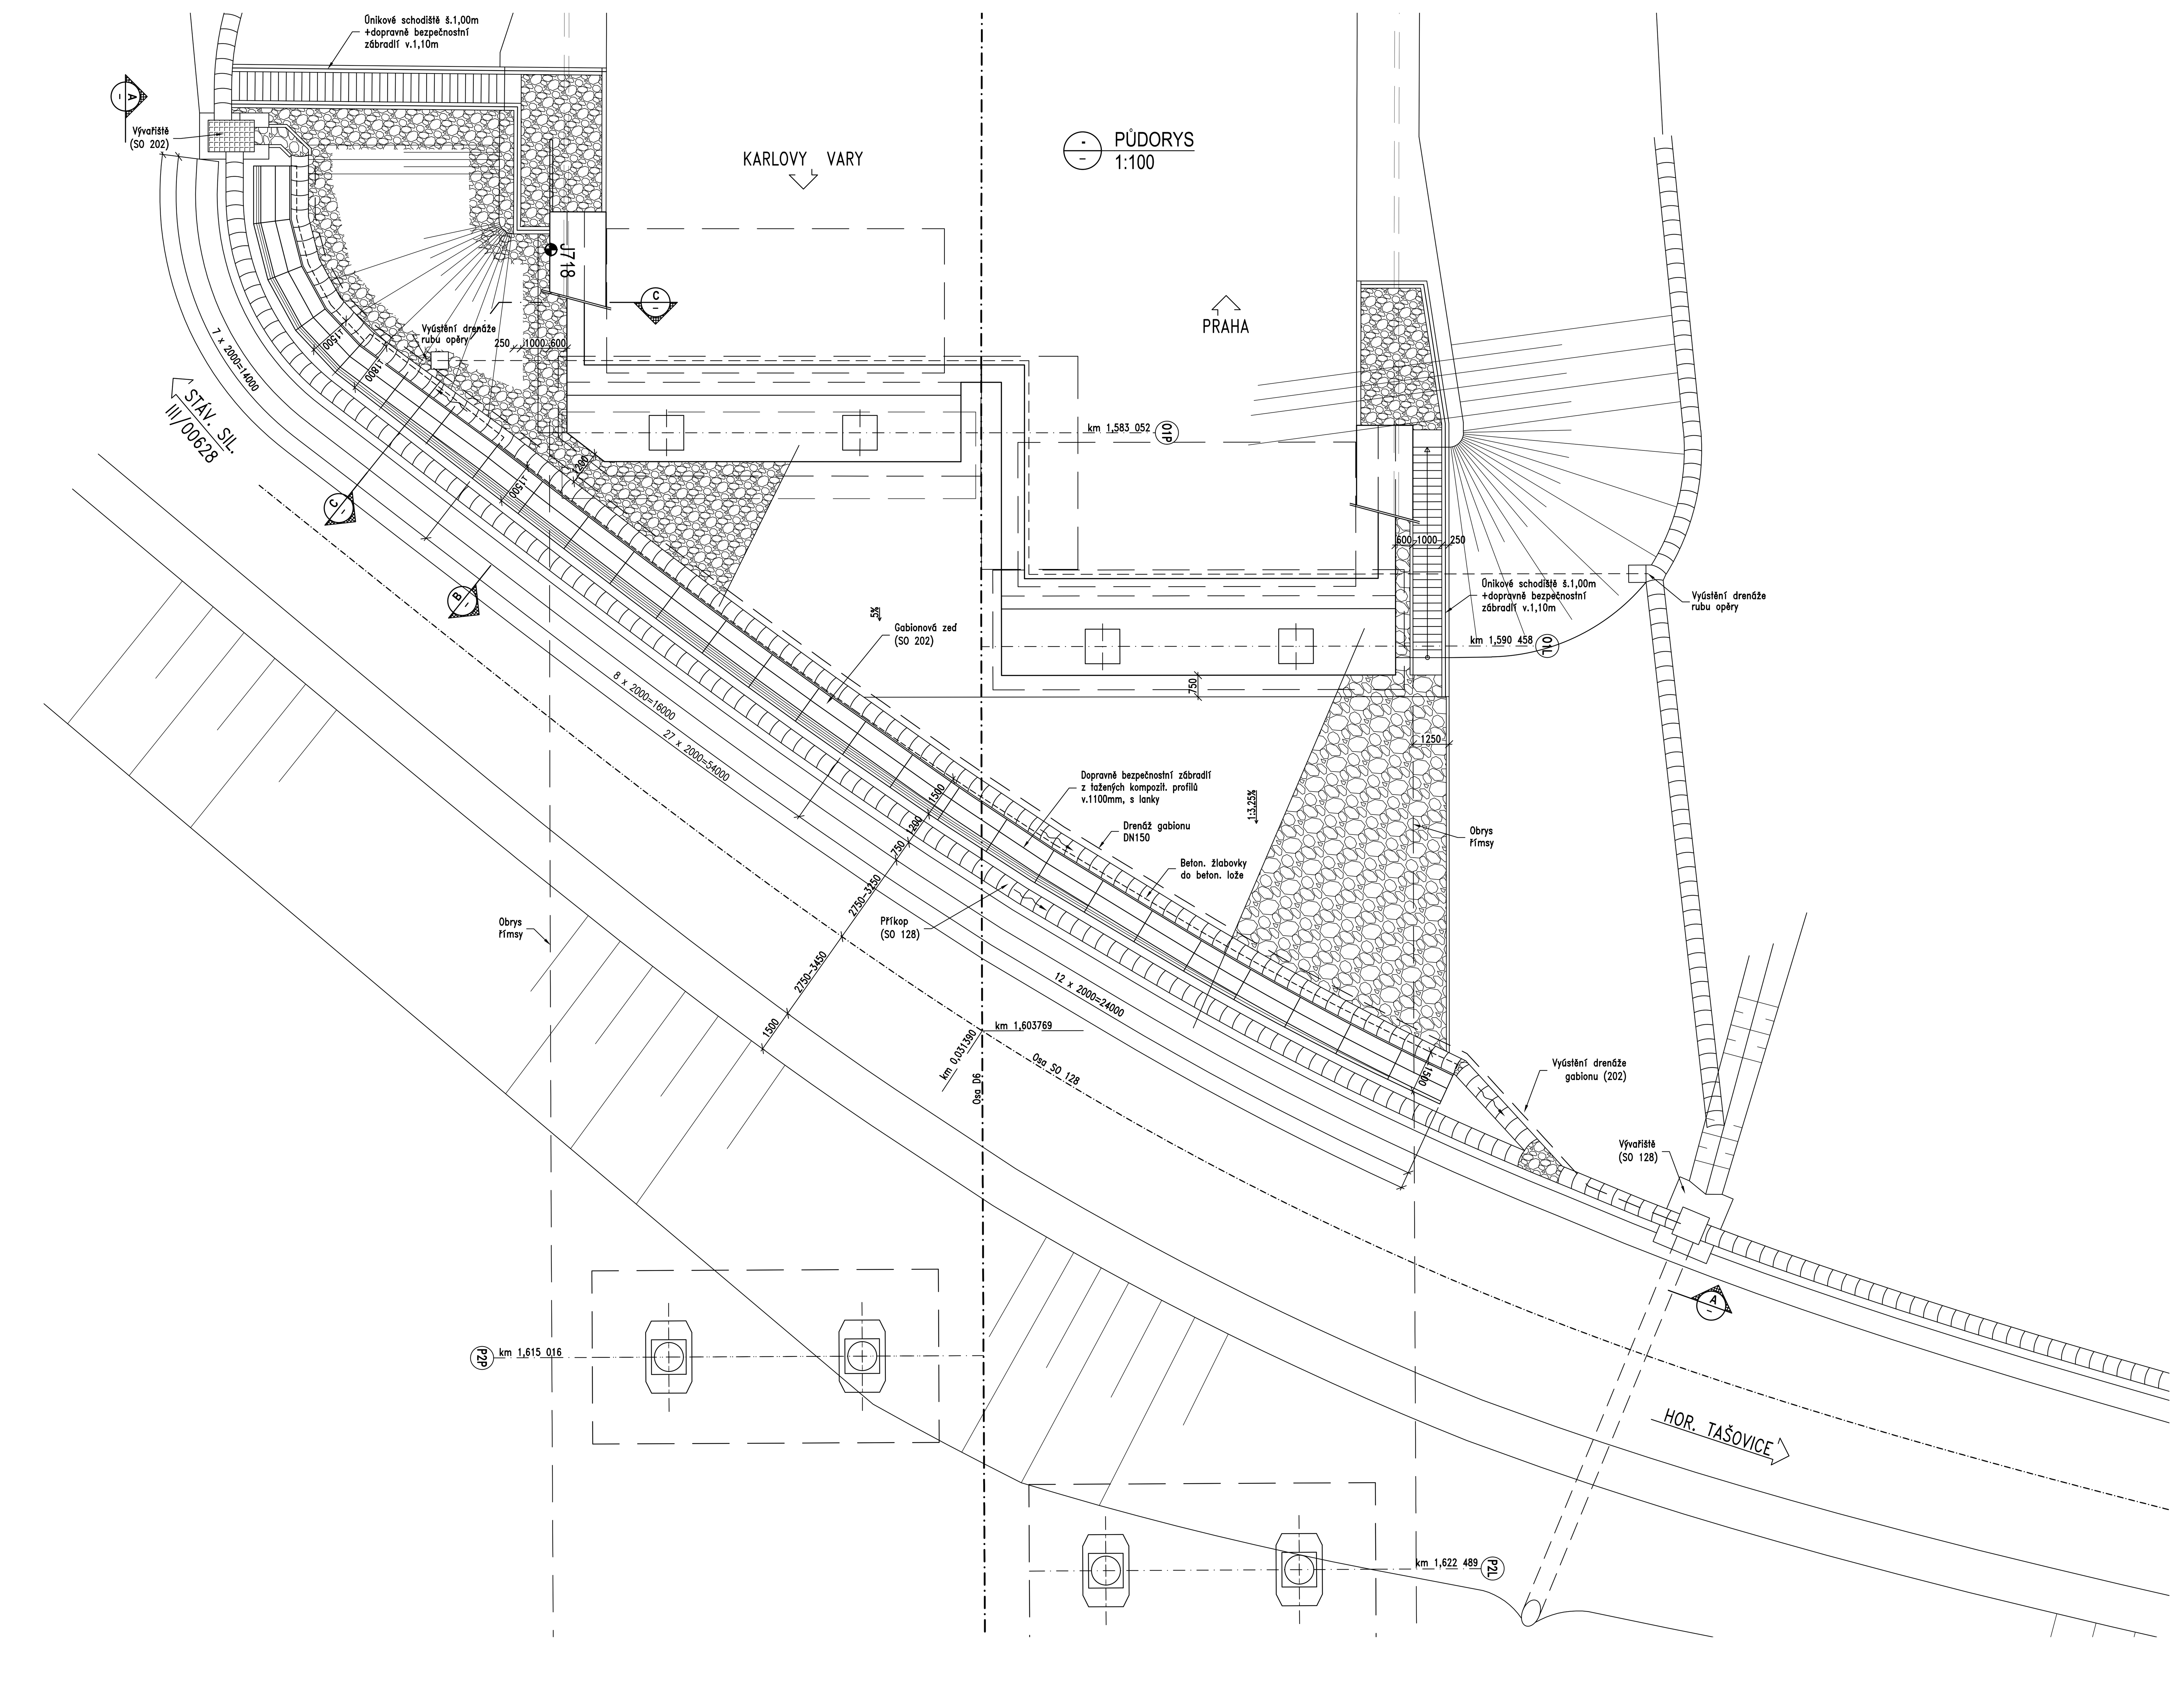


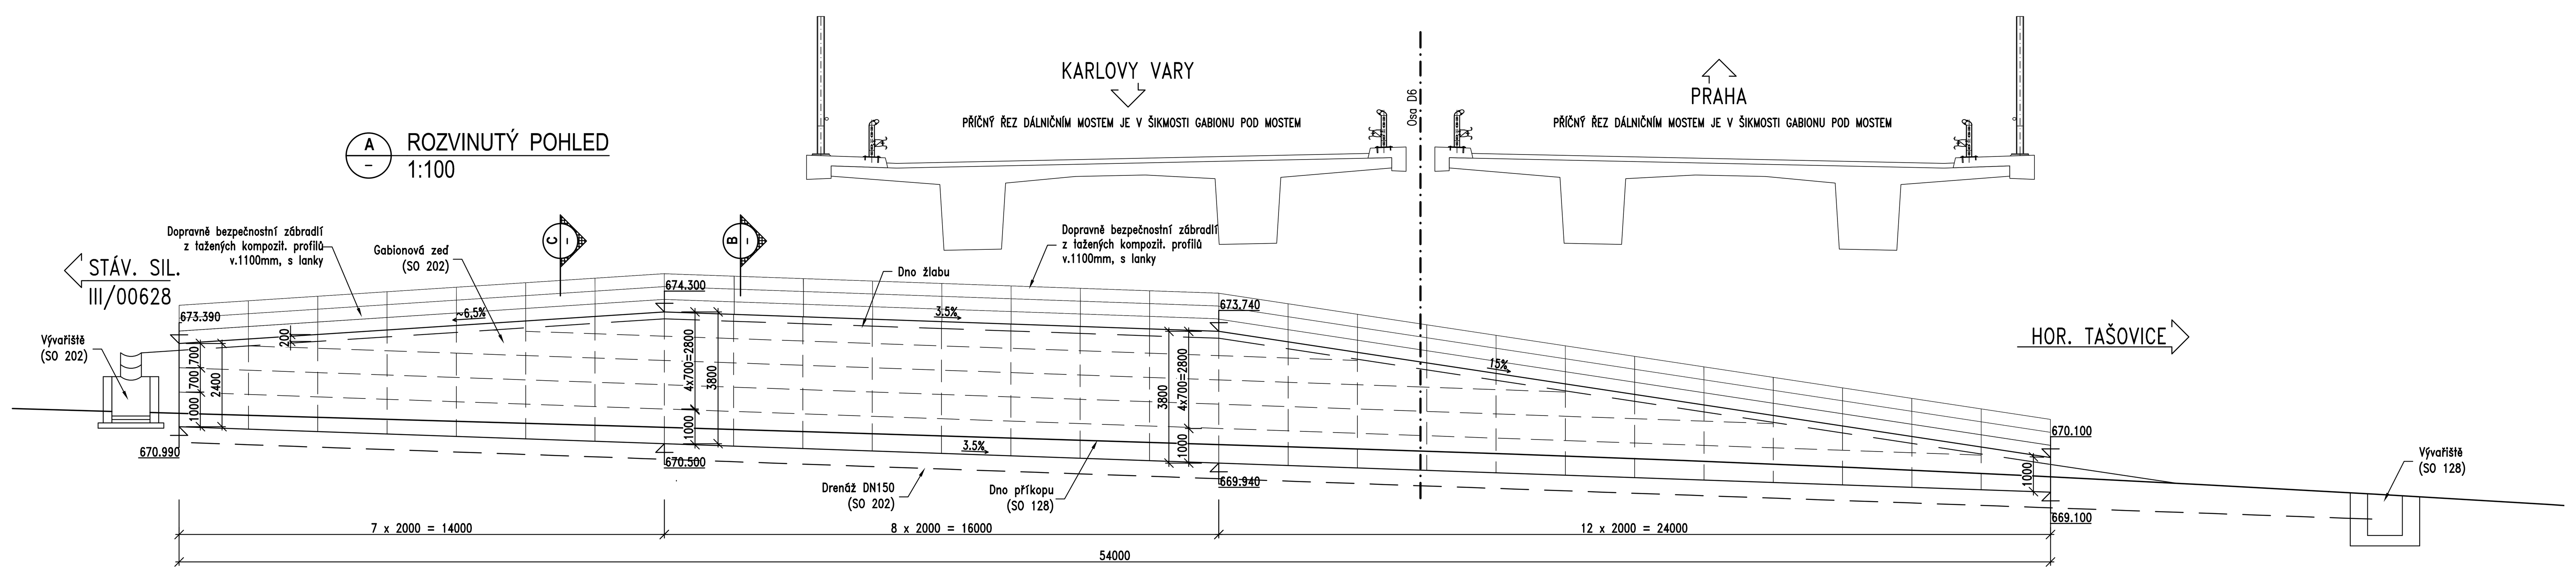

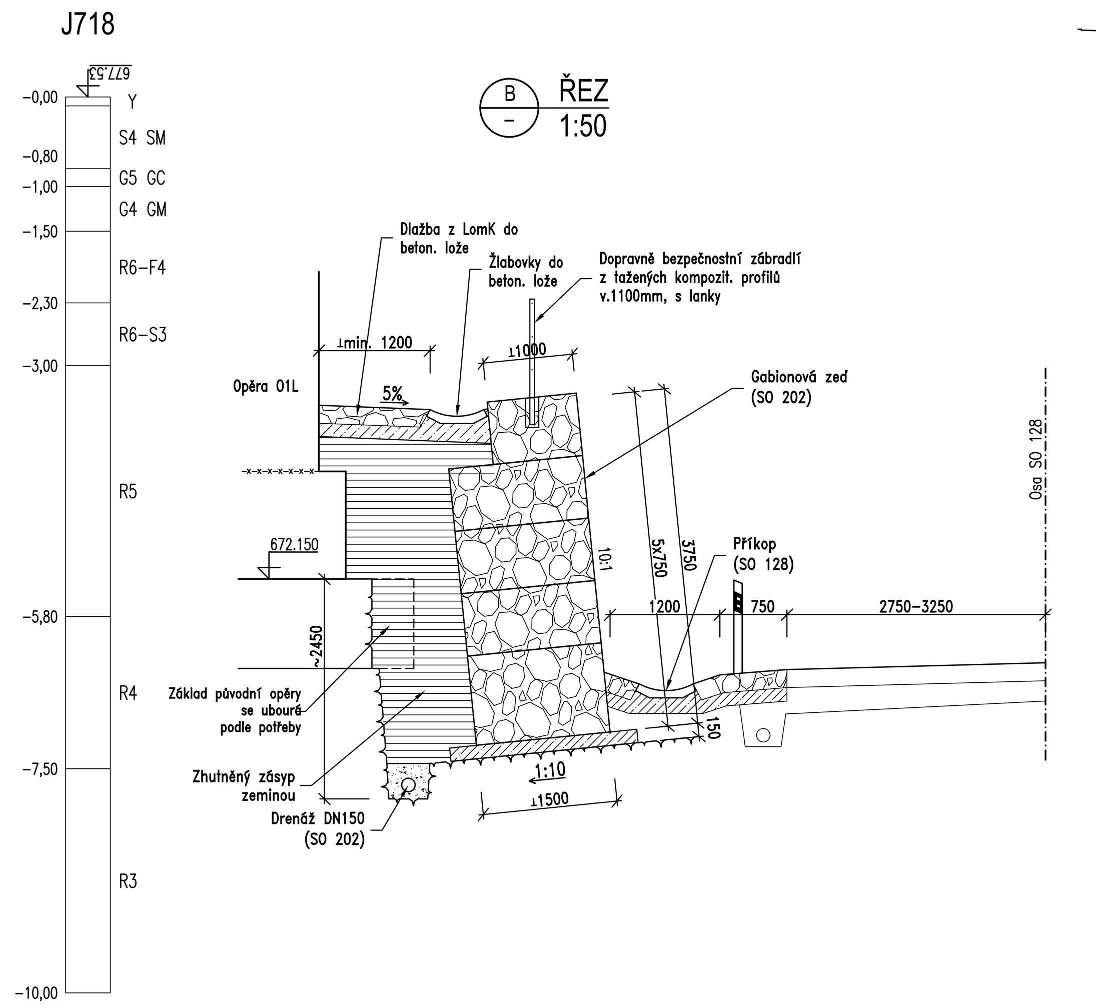

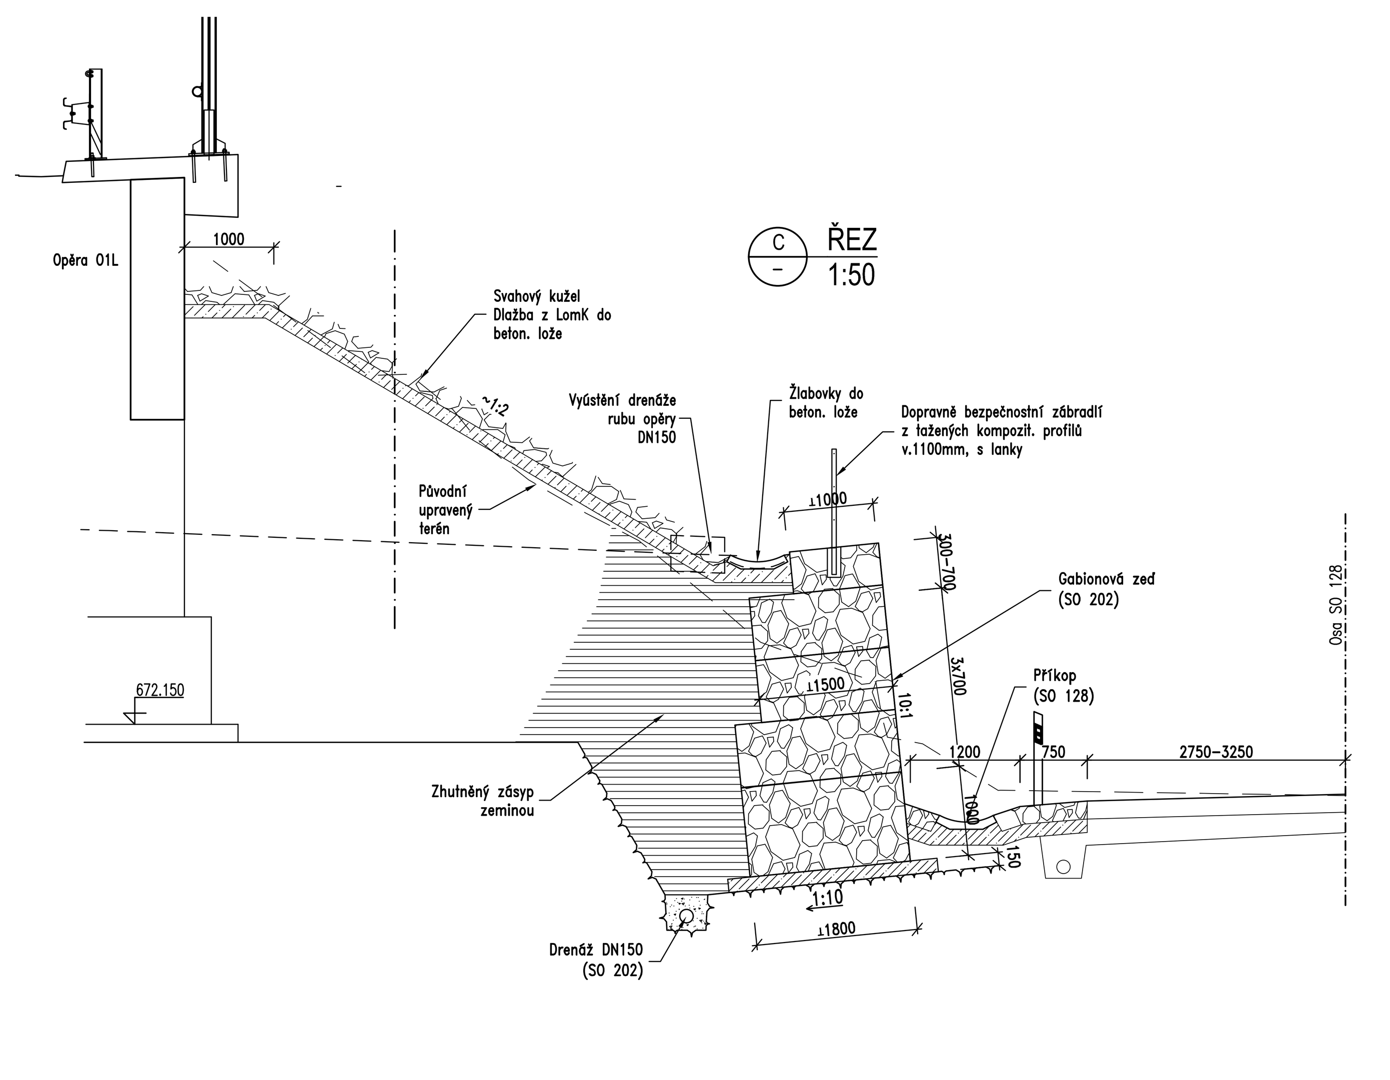

MATERIÁLY:

PODKLAD. BETON POD GABIONEM	C12/15-X0
ŽLABOVKY	min.C25/30-XF4, XD3
LOŽE DLAŽBY A ŽLABOVEK	C20/25N-XF3
VÝVAŘIŠTĚ	C25/30-XF4
SPÁROVÁNÍ DLAŽBY	MC25-XF4
LOM.KÁMEN	TŘÍDA JAKOSTI "I"

BETONY PODLE ČSN EN 206+A2
NEKONSTRUKČNÍ BETON PODLE TKP SKP KAP.18, TAB. 18-2N
LOMOVÝ KÁMEN PODLE ČSN 72 1860
CEM. MALTA PODLE ČSN EN 998-2

POZNÁMKY:

1. VLASTNOSTI, KONSTRUKČNÍ ZÁSADY, PROVÁDĚNÍ A PRŮKAZNÉ ZKOUŠKY MATERIÁLŮ MUSÍ BÝT V SOULADU S TKP 30.
2. GABIONY BUDOU ZE SVAŘOVANÉ SÍTĚ S OKY 100x100mm. TL. DRÁTU 4mm, POVRCHOVÁ ÚPRAVA ZnAl. PEVNOST SÍTÍ MIN. 40kN/m.
3. VÝPLŇOVÝ KÁMEN BUDE ODOLNÝ VŮČI POVĚTRNOSTNÍM VLIVŮM, NEŠTĚPIVÝ A DOSTATEČNĚ TVRDÝ. NA RUBU GABIONU BUDE POUŽITO KAMENIVO FRAKCE 32-63, PŘÍP. 63-125. DO POHLEDOVÉ STRANY BUDE POUŽIT LOMOVÝ KÁMEN VELIKOSTI 1.5-2 NÁSOBKU OKATOSTI SÍTĚ.
4. POSLEDNÍ ŘADA KOŠŮ BUDE PO ZAVÍKOVÁNÍ DOSYPÁNA DROBNĚJŠÍM KAMENIVEM.
5. RUB GABIONŮ BUDE OPATŘEN NETKANOU SEPARAČNĚ FILTRAČNÍ GEOTEXTILIÍ. ODOLNOST PROTI PROTRŽENÍ (CBR) min. 2,5kN, PLOŠNÁ HMOTNOST min. 400g/m2.
6. ZÁSYP OPĚRNÉ ZDI SE PROVEDE ZE ZEMIN VHODNÝCH NEBO PODMÍNEČNĚ VHODNÝCH DO NÁSYPU DLE ČSN 73 6133 S HUTNĚNÍM PO VRSTVÁCH TL. MAX. 300 mm NA ID=0.85 AŽ 0.90, RESP. D=100%PS

ČÁST D.2
SO 202

ČISTOPIS

Souřadnicový systém S-JTSK, Výškový systém Bpv

Objednatel:
ŘEDITELSTVÍ SILNIC A DÁLNIC
ŘEDITELSTVÍ SILNIC A DÁLNIC s. p.
Čerčanská 2023/12
140 00 Praha 4 – Krč

Zhotovitel PD: PRAGOPROJEKT, a.s., K Ryšánce 1668/16, 147 54 Praha 4, IČO: 45272387, www.pragoprojekt.cz, datová schránka: 4kifr54

Navrhl/vypracoval: Ing. Karolína Hédová, podpis:	Zodpovědný projektant: Ing. Martin BLATSKÝ, podpis:	Zástupce zodpovědného projektanta: Ing. Jan BAŽIL, podpis:
Technická kontrola: Ing. Kamil PEJCHAL, podpis:	Hlavní inženýr projektu: Ing. Pavel ŠLAPA, podpis:	Zástupce hlavního inženýra projektu: Ing. Radovan STANKOVEN, podpis:

PRAGOPROJEKT

Kraj:	KARLOVARSKÝ KRAJ	Číslo zakázky:	25-150-2
Místo stavby:	OLŠOVÁ VRATA, ANDĚLSKÁ HORA, ŽALMANOV, HORNÍ TAŠOVICE, BOCHOV	Číslo akce:	05-219
Objednatel:	ŘSD s. p., Čerčanská 2023/12, 140 00 Praha 4, IČO 65993390	Datum:	03/2026
Název stavby:	D6 OLŠOVÁ VRATA-ŽALMANOV, VD-ZDS	Formát:	
Objekt:	Most na D6 přes Lomnický potok v km 1,600 SO 101	Měřítko:	
		Stupeň:	PDPS
Příloha:	GABIONOVÁ ZEĎ U OP1	Číslo přílohy:	24
		Souprava:	