




 


ŘEZ VNĚJŠÍ ŘÍMSOU, LEVÝ MOST 1:25

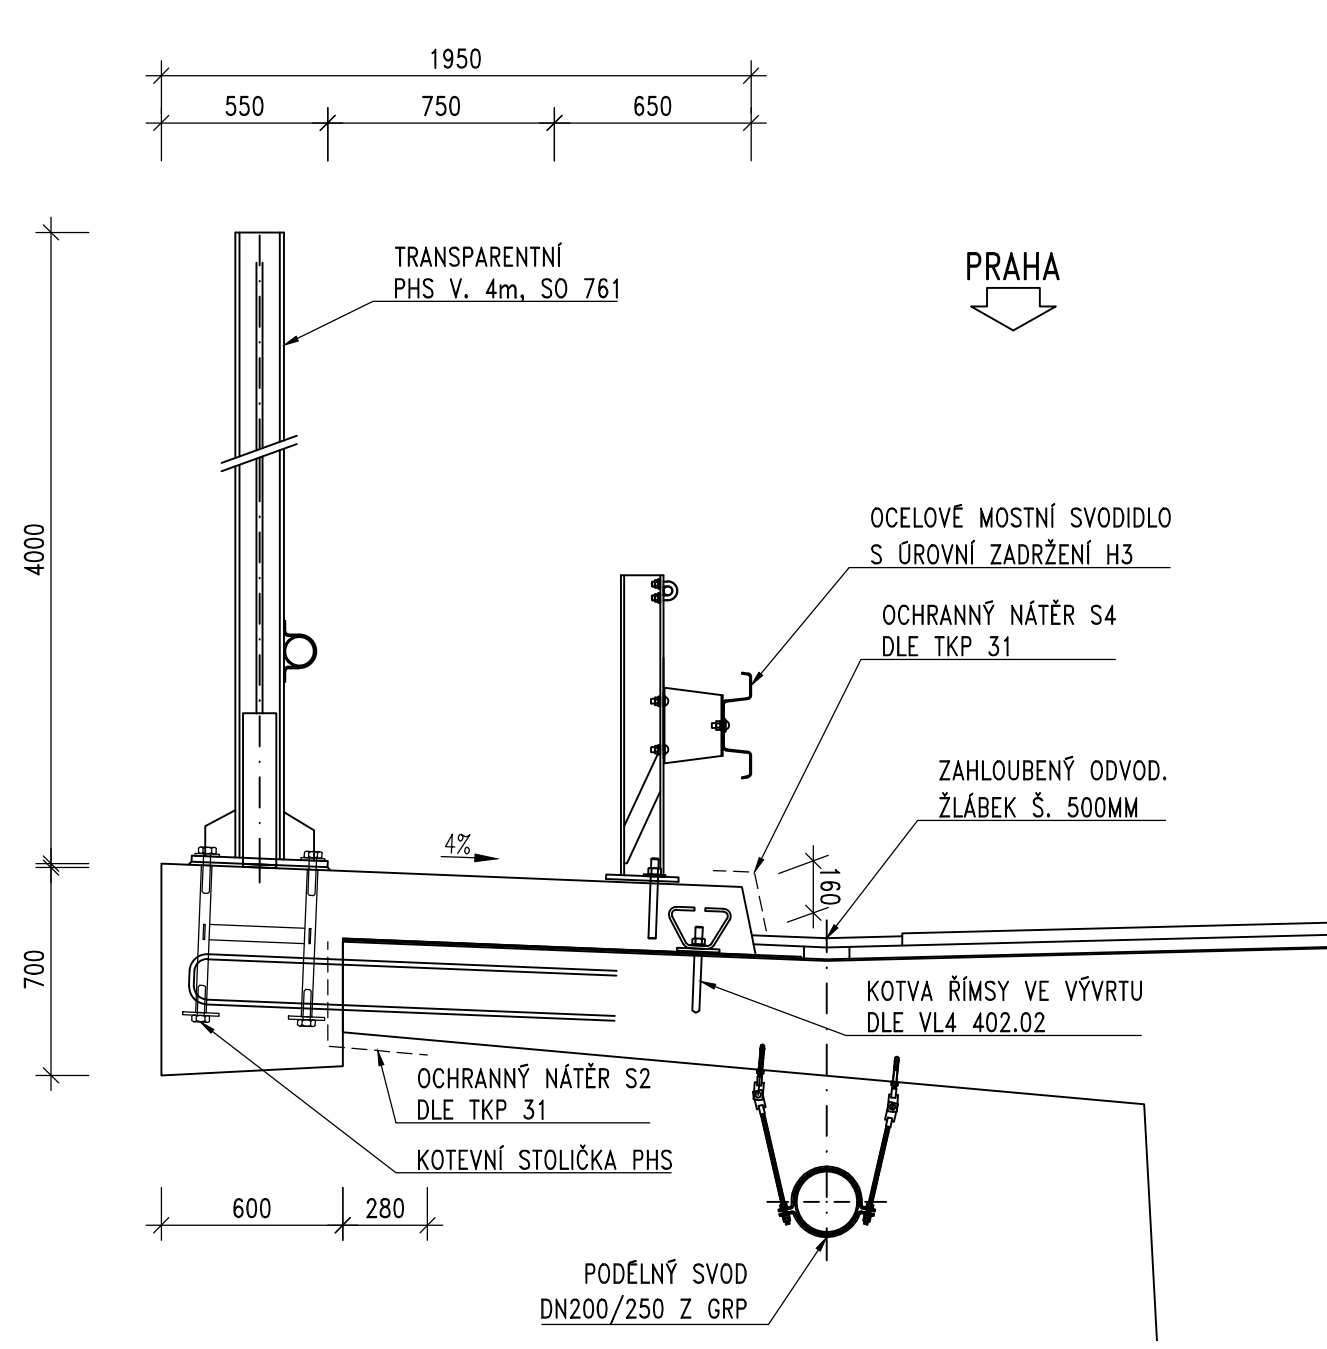


ŘEZ VNĚJŠÍ ŘÍMSOU, PRAVÝ MOST 1:25

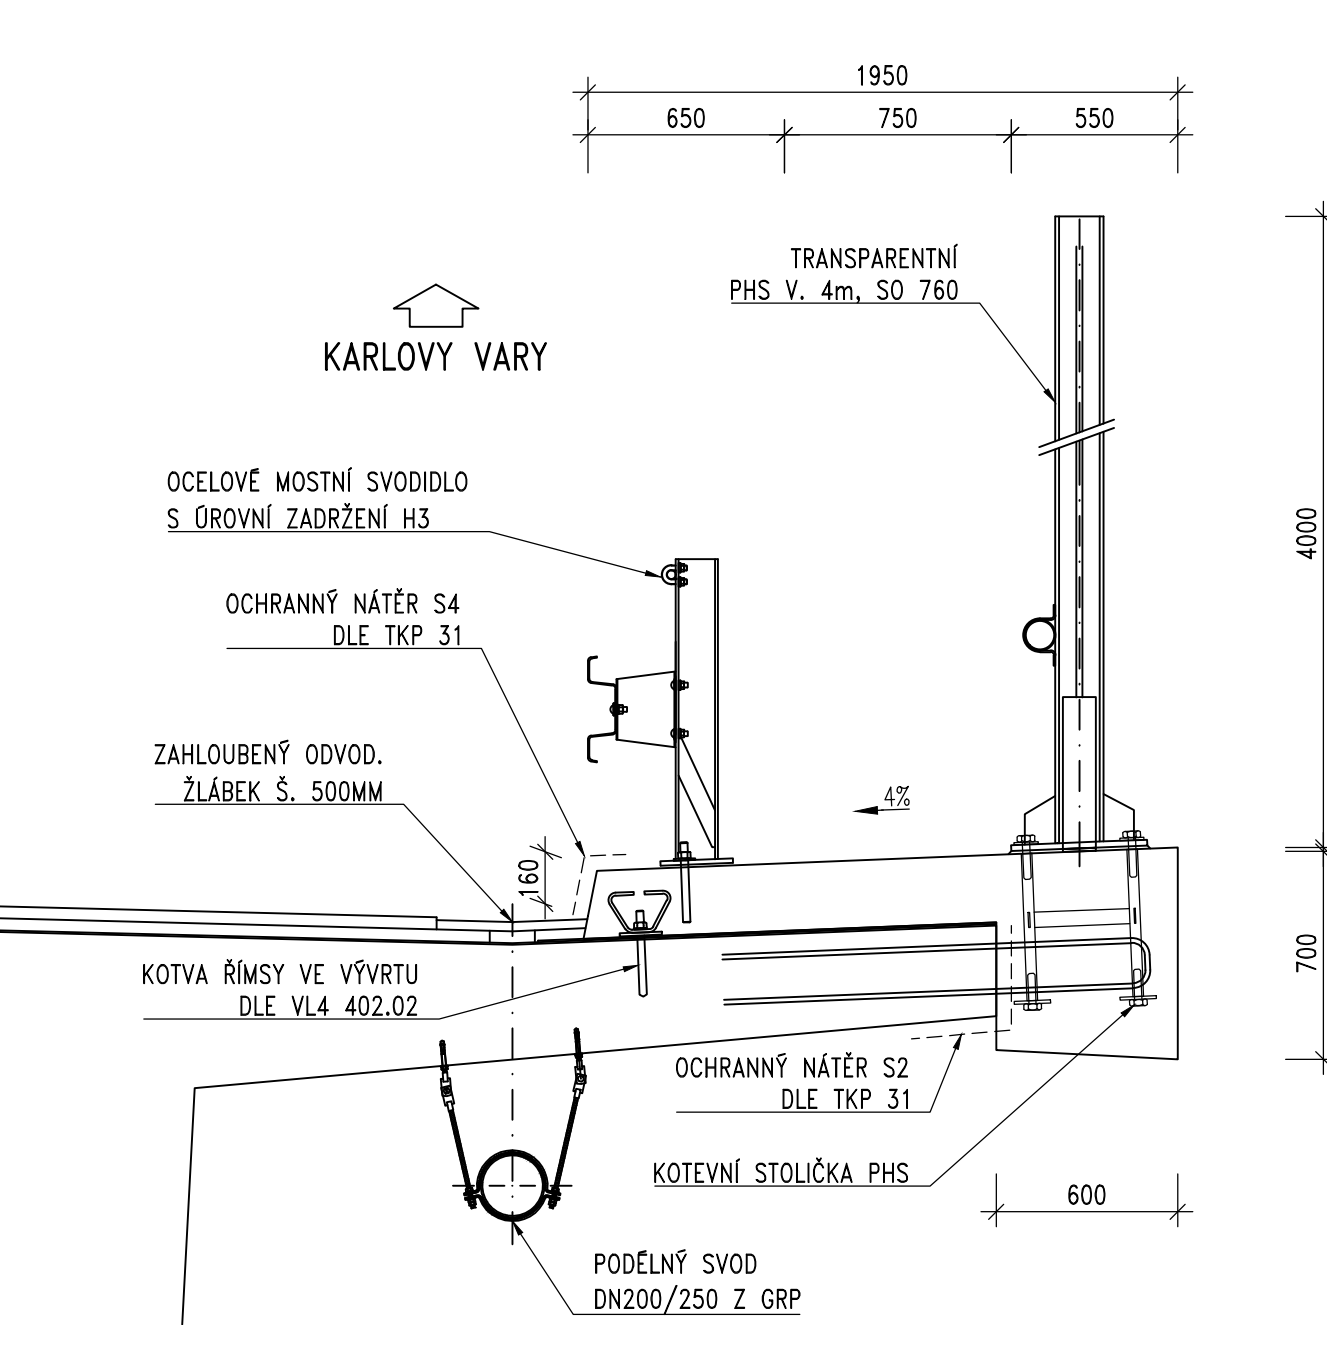

KOTEVNÍ PŘÍPRAVEK PHS 1:10

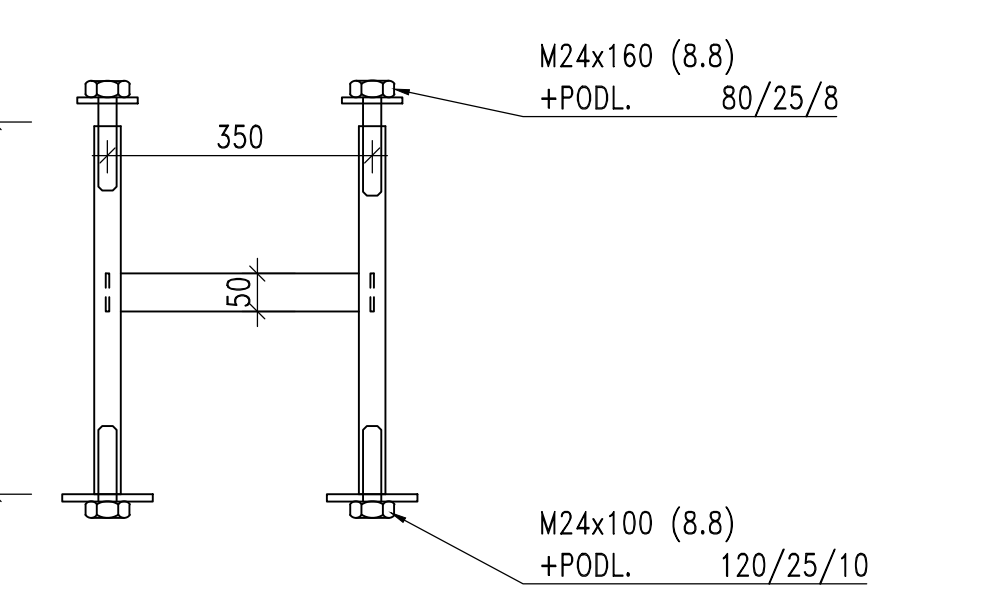

PŮDORYS 1:10

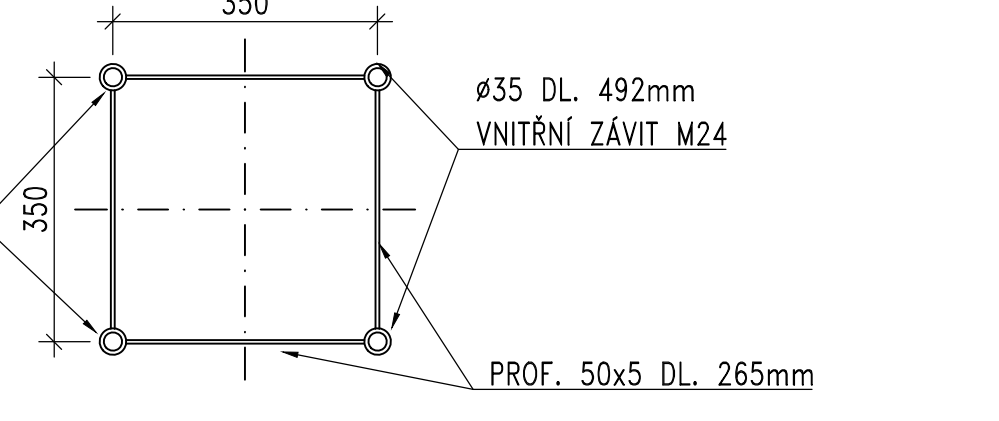

MATERIÁL

BETON DLE TKP18
NOSNÁ KONSTRUKCE
DOBETONÁVKA KOTEV A MZ
ŘÍMSY
BETONÁŘSKÁ VÝZTUŽ
B500 B V BĚŽNÝCH PROFILECH

PŘEDPISY PRO PROVEDENÍ JEDNOTLIVÝCH KONSTRUKČNÍCH ČÁSTÍ:

- TKP KAP 18 – BETONOVÉ KONSTRUKCE A MOSTY
- ČSN EN 206+A2 – BETON – SPECIFIKACE, VLASTNOSTI, VÝROBA A SHODA
- TKP KAP 21 – IZOLACE PROTI VODĚ
- ČSN EN 14188 – ZÁVLKY A VLOŽKY DO SPAR
- ČSN EN ISO 11600 – STAVEBNÍ KONSTRUKCE – TĚSNÍCÍ HMOTY – KLASIFIKACE A POŽADAVKY PRO TMELY
- TP 124 – ZÁKLADNÍ OCHRANNA OPATŘENÍ PRO OMEZENÍ VLIVU BLUDNÝCH PROUDŮ NA MOSTNÍ OBJEKTY A OSTATNÍ BETONOVÉ KONSTRUKCE POZEMNÍCH KOMUNIKACÍ
- TP 193 – SVAŘOVÁNÍ BETONÁŘSKÉ VÝZTUŽE A JINÉ DRUHY SPOJŮ ČSN EN ISO 17660-2 SVAŘOVÁNÍ – SVAŘOVÁNÍ BETONÁŘSKÉ OCELI ČÁST 2: NENOSNÉ SVAŘOVÉ SPOJE

ČÁST D.2
SO 202

ČISTOPIS
Souřadnicový systém S-JTSK, Výškový systém Bv
Objednatel: ŘEDITELSTVÍ SILNIC A DÁLNIC s. p.
Číslo zakázky: 05-219
Číslo výkresu: 03/2026
140 00 Praha 4 – Kře

Zhotovitel: PRAGOPROJEKT, s.r.o., IČ: 1688/16, 147 54 Praha 4, IČO: 45272387, www.pragoprojekt.cz, datová schránka: 444054	
Návrh/oprava: Ing. Karolína Heflová projekce: Ing. Jitka Bělá revize: Ing. Jitka Bělá kontrola: Ing. Jitka Bělá projekt: Ing. Jitka Bělá	Zpracování projektu: Ing. Martin Blatný projekce: Ing. Martin Blatný revize: Ing. Martin Blatný kontrola: Ing. Martin Blatný projekt: Ing. Martin Blatný
Technická zpráva: Ing. Kamil PEJCHAL projekce: Ing. Kamil PEJCHAL revize: Ing. Kamil PEJCHAL kontrola: Ing. Kamil PEJCHAL projekt: Ing. Kamil PEJCHAL	Zpracování projektu: Ing. Pavel ŠTĚPÁNEK projekce: Ing. Pavel ŠTĚPÁNEK revize: Ing. Pavel ŠTĚPÁNEK kontrola: Ing. Pavel ŠTĚPÁNEK projekt: Ing. Pavel ŠTĚPÁNEK

Kraj: KARLOVARSKÝ KRAJ	Číslo zakázky: 25-150-2
Město: OLŠOVÁ VRATA, ANDĚŠSKÁ HORA, ŽALMANOV, HORNÍ TAŠOVSKÉ, BOCHOV	Číslo výkresu: 05-219
Objednatel: ŘSD s. p., Čerňanská 2023/12, 140 00 Praha 4, IČO 65993590	Stav: 03/2026
Název stavby: D6 OLŠOVÁ VRATA-ŽALMANOV, VD-ZDS	Formát: A3
Objekt: Most na D6 přes Lomnický potok v km 1,600 SO 101	Stupeň: 28
Průběh: PHS	