


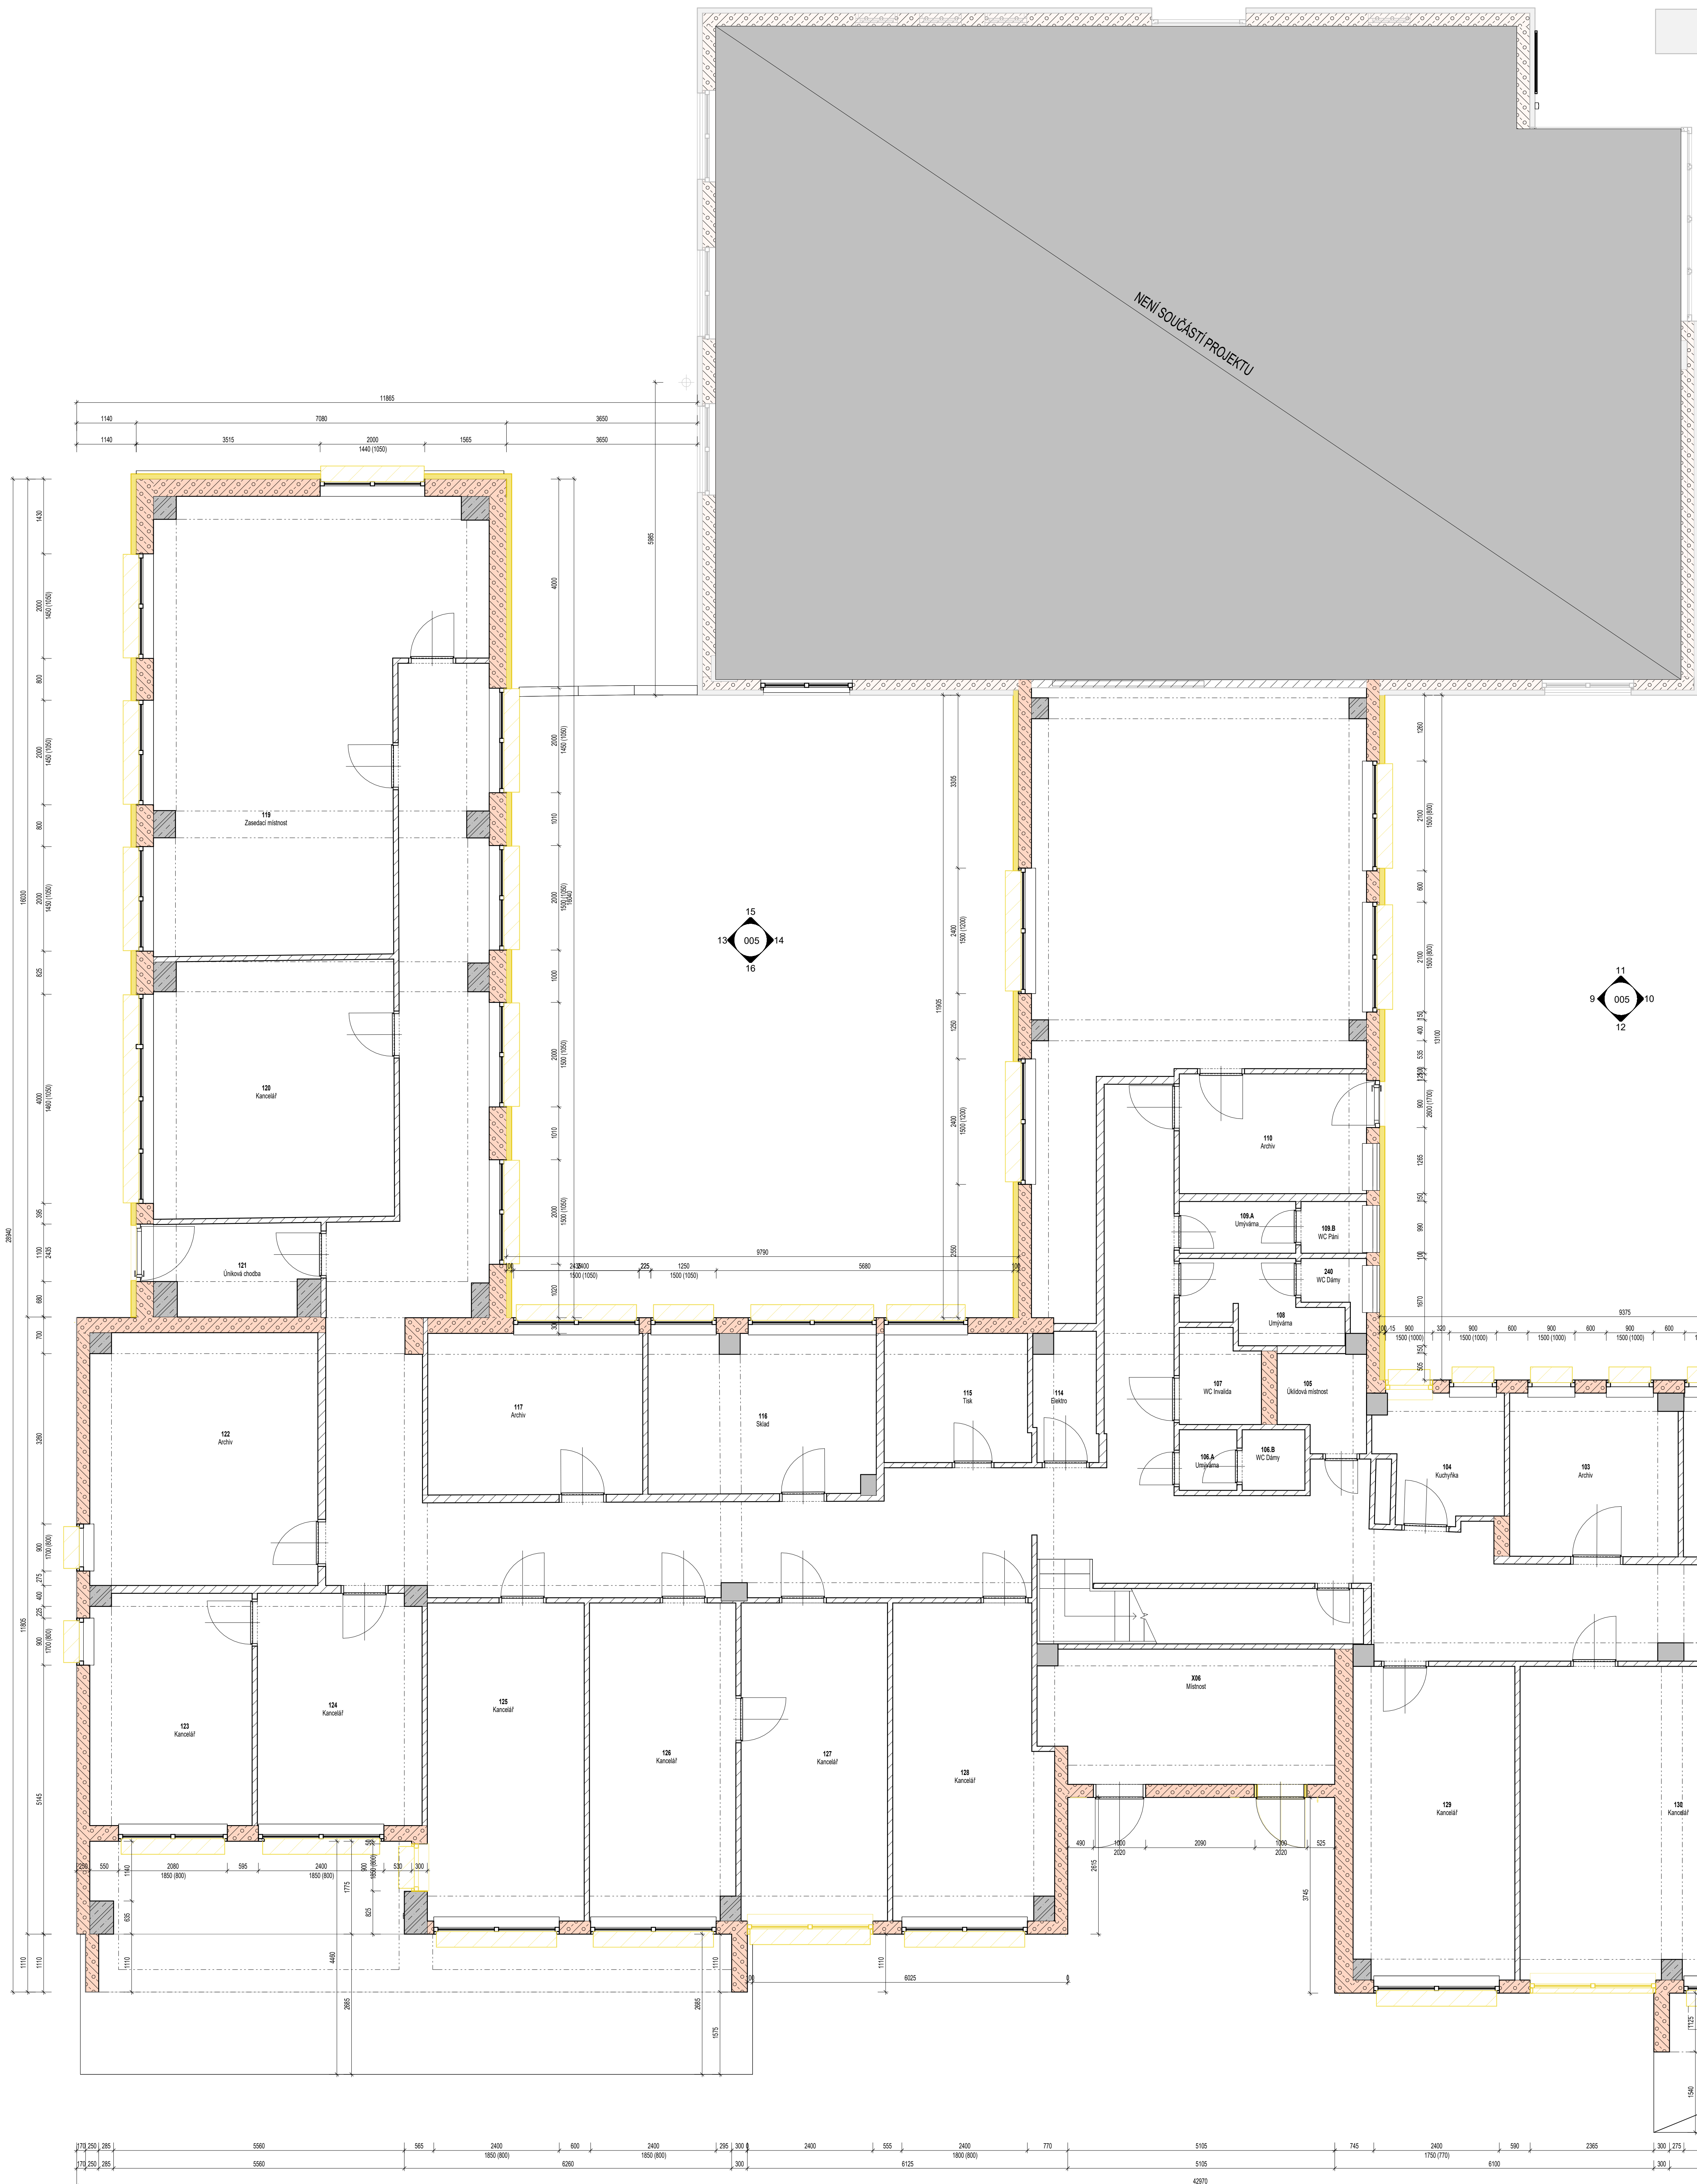

Výkaz místností 1NP A					
Číslo	Název	Podlaží	Objem	Plocha	Poznámka
5XX	Karlovo centrum	1NP A	326.00 m³	100 m²	
5XX	Kancelář	1NP A	270.47 m³	85 m²	
6AAA	Místnost	1NP A	1.96 m³	1 m²	
6BBB	Místnost	1NP A	3.35 m³	2 m²	
6CCC	Místnost	1NP A	3.26 m³	2 m²	
622	Místnost	1NP A	9.14 m³	3 m²	
100	Chodba	1NP A	0.00 m³	186 m²	
101	Archiv	1NP A	61.84 m³	22 m²	
102	Místnost	1NP A	36.90 m³	14 m²	
103	Archiv	1NP A	25.76 m³	10 m²	
104	Kuchyňka	1NP A	14.24 m³	5 m²	
105	Uklídková místnost	1NP A	7.57 m³	3 m²	
106.A	Umývárna	1NP A	3.31 m³	1 m²	
106.B	WC Dámy	1NP A	3.61 m³	1 m²	
107	WC Invalida	1NP A	6.94 m³	3 m²	
108	Umývárna	1NP A	10.67 m³	4 m²	
109.A	Umývárna	1NP A	6.15 m³	2 m²	
109.B	WC Páni	1NP A	3.46 m³	1 m²	
110	Archiv	1NP A	22.89 m³	8 m²	
111	Archiv	1NP A	145.76 m³	52 m²	
114	Elektro	1NP A	7.39 m³	3 m²	
115	Tisk	1NP A	19.04 m³	7 m²	
116	Sklad	1NP A	36.61 m³	13 m²	
117	Archiv	1NP A	35.38 m³	13 m²	
119	Zasedací místnost	1NP A	126.29 m³	45 m²	
120	Kancelář	1NP A	60.15 m³	22 m²	
121	Úniková chodba	1NP A	14.06 m³	5 m²	
122	Archiv	1NP A	58.37 m³	21 m²	
123	Kancelář	1NP A	38.19 m³	14 m²	
124	Kancelář	1NP A	38.61 m³	14 m²	
125	Kancelář	1NP A	50.92 m³	18 m²	
126	Kancelář	1NP A	47.13 m³	17 m²	
127	Kancelář	1NP A	47.53 m³	17 m²	
128	Kancelář	1NP A	48.57 m³	17 m²	
130	Kancelář	1NP A	86.40 m³	33 m²	
131	Kancelář	1NP A	46.54 m³	18 m²	
132	Kancelář	1NP A	38.02 m³	15 m²	
133	Kancelář	1NP A	58.19 m³	22 m²	
134.A	Větrnice	1NP A	19.74 m³	7 m²	
134.B	Sklad	1NP A	6.86 m³	3 m²	
135.A	Předstíh	1NP A	12.61 m³	5 m²	
135.B	Výměňková stanice / sklad	1NP A	120.82 m³	43 m²	
240	WC Dámy	1NP A	3.44 m³	1 m²	
507	Umývárna	1NP A	4.76 m³	2 m²	
508	WC Páni	1NP A	2.46 m³	1 m²	
509	WC Invalida	1NP A	6.08 m³	2 m²	
510	Umývárna	1NP A	4.63 m³	2 m²	
511	WC Dámy	1NP A	3.21 m³	1 m²	
512	WC Dámy	1NP A	2.37 m³	1 m²	
514	Sklad	1NP A	134.13 m³	39 m²	
601	Místnost	1NP A	19.18 m³	3 m²	
602	Místnost	1NP A	155.68 m³	58 m²	
603	Místnost	1NP A	235.46 m³	89 m²	
604	Místnost	1NP A	22.89 m³	9 m²	
605	Kancelář	1NP A	30.78 m³	12 m²	
606	Kancelář	1NP A	33.26 m³	13 m²	
607	Kuchyňka	1NP A	33.37 m³	13 m²	
608	Umývárna	1NP A	6.04 m³	2 m²	
609	TM	1NP A	7.70 m³	3 m²	
610	WC Páni	1NP A	3.66 m³	1 m²	
611	WC Dámy	1NP A	4.79 m³	2 m²	
612	Místnost	1NP A	3.97 m³	1 m²	
613	Místnost	1NP A	4.04 m³	1 m²	
614	WC Invalida	1NP A	7.17 m³	3 m²	
615	WC Invalida	1NP A	7.73 m³	3 m²	
X06	Místnost	1NP A	38.47 m³	14 m²	
Celkový součet					

POZNÁMKY:

VZHLÉDEM K CHARAKTERU STAVBY REKONSTRUKCE JE NUTNÉ VEŠKERÉ ROZMĚRY OVEŘOVAT NA STAVBĚ A ODCHYLKY OD PROJEKTOVÉ DOKUMENTACE ZJIŠTĚNÉ PŘI PROVEDENÍ STAVBY KONZULTOVAT S PROJEKTANTEM.

U BOURANÝCH KONSTRUKCÍ JE NUTNÉ OVEŘIT PRIMO NA STAVBĚ JEJICH NOSNOU FUNKCI, V PŘÍPADĚ NESROVNALOSTI NUTNĚ KONTAKTOVAT PROJEKTANTA STATIKA.

KÓTY BOURANÝCH KONSTRUKCÍ MAJÍ INFORMATIVNÍ CHARAKTER, OSAZENÍ NOVÝCH PRVKŮ DLE NAVRŽENÉHO ŘEŠENÍ.



VEŠKERÉ PROSTUPY A DŘÁŽKY PRO VEDENÍ INSTALACÍ BUDOU PROVEDENY DLE POŽADAVKŮ JEDNOTLIVÝCH PROFESÍ.

TATO DOKUMENTACE NENAHRAŽUJE DODATELSKOU A DÍLENSKOU DOKUMENTACI.

NEDÍLNOU SOUČÁSTÍ DOKUMENTACE JSOU DETAILY A TECHNICKÁ ZPRÁVA.

LEGENDA MATERIÁLŮ:

- KOVINOVÉ KONSTRUKCE - ŽELEZO
- OBLOKOVÉ PANELE - OKLÁSTĚNÍ OKEN
- OBLOKOVÉ KOVINOVÉ ŽELEZO
- WITNÍ NEMOVNÉ A PRŮVODNÉ ŽELEZO
- BOURNÉ ODBĚRNÉ KONSTRUKCE

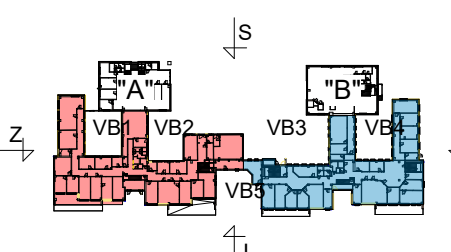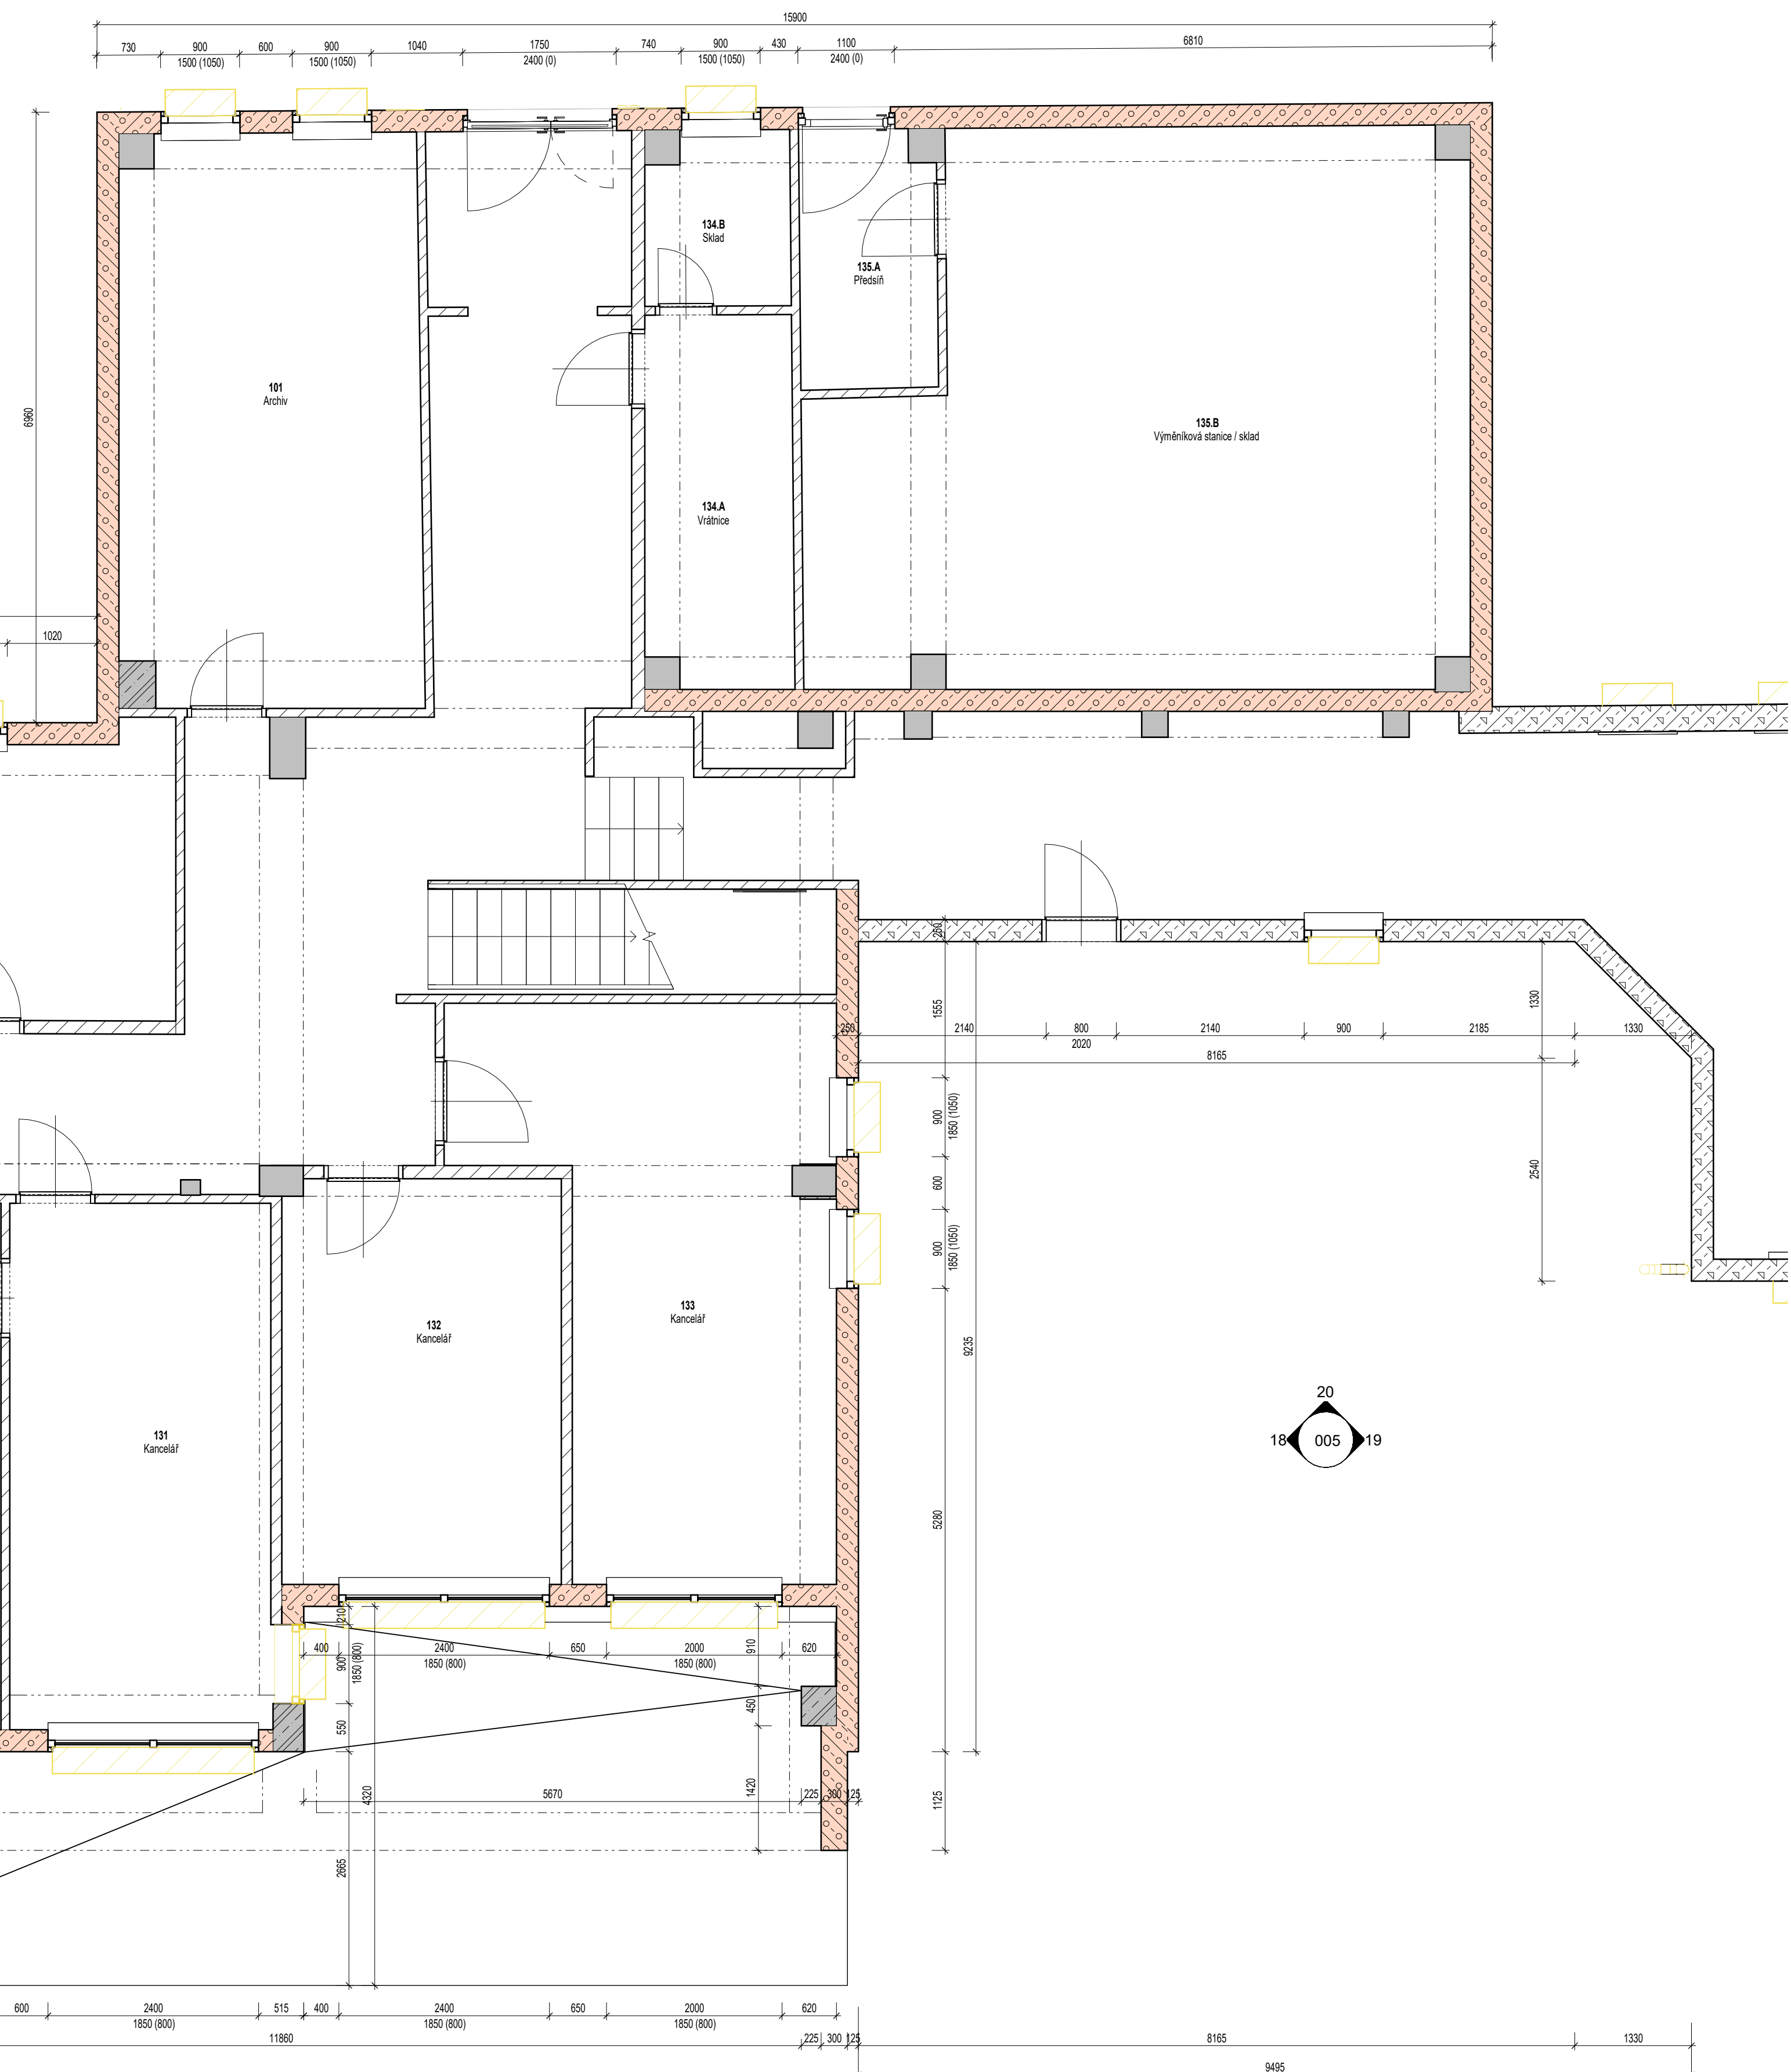

Snížení energetické
náročnosti MČ Praha 11
Výběrová 1024/4 a 1025/2, Praha-Chodov

STUPEŇ PROJEKTU +/- 0,000 ± 293,330 Bp.v.

DOKUMENTACE PRO PROVEDENÍ STAVBY
(DPS)

ODPOVĚDNÝ PROJEKTANT
Ing. arch. Janek Vědra, DiA 63961
733 575 363, jank.vodka@seznam.cz

VYPRACOVANÉ

INVESTOR
Městská část Praha 11
Opatřová 672/1, 143 41, Praha 4

Díl
D ČÁST DOKUMENTACE

1.1

OBSAH VÝKRESU

"A" PŮDORYS NP - BOURÁNÍ

MĚŘÍTKO
1:100
DÁLKA
02/2024
STUPEŇ
DPS

FORMÁT
A4
LÝŽNÍ
3/2024
REVIZE
1.1 101

ZPRACOVATEL ČÁSTI
Janek Vědra
V Praze 11015
110 00, Praha 1
www.janekvedra.cz

GENERALNÍ PROJEKTANT
Janek Vědra
V Praze 11015
110 00, Praha 1
www.janekvedra.cz