


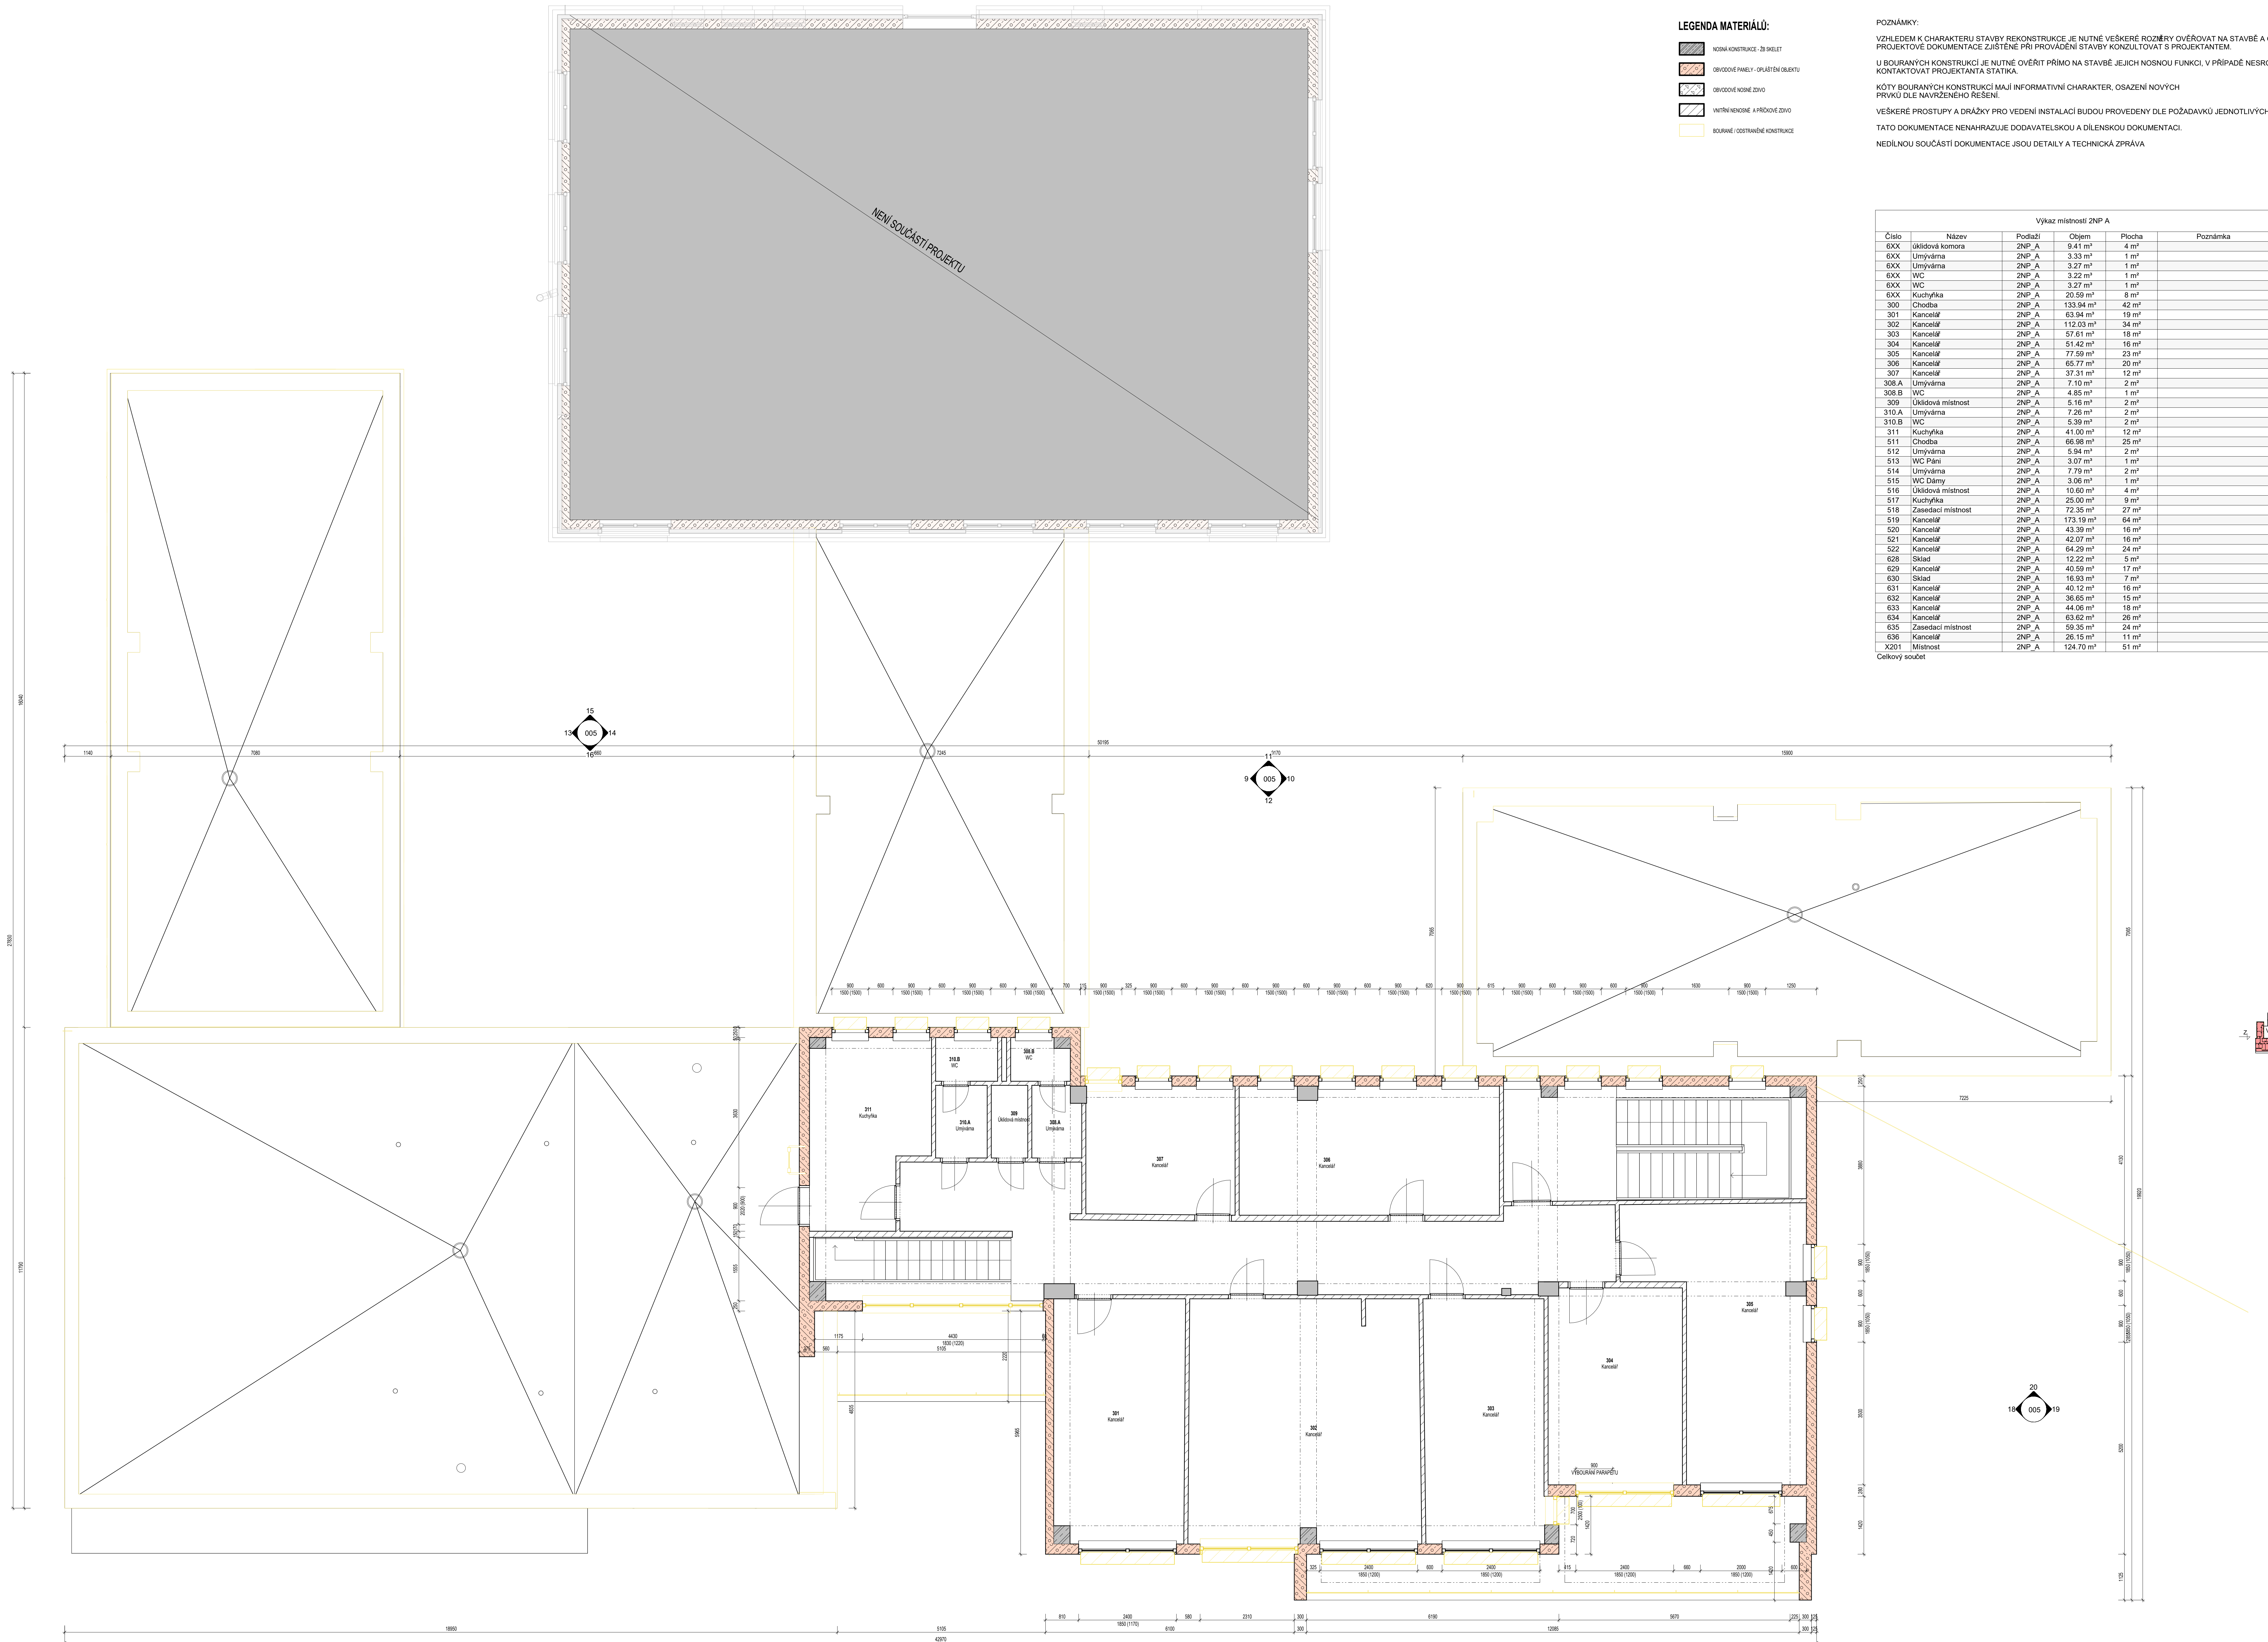

Snižování energetické
náročnosti MC Praha 11

STUPĚŇ PROJEKTU - J.Č. 0.000 - 293.338 B.9.v.

DOKUMENTACE PRO PROVEDENÍ STAVBY
(DPS)

OSPODOVNÍ PROJEKTANT
Ing. arch. Janek Vojta, ČKA 03943
723 591 983, janek.vojta@asapoint.cz

VYPRACOVAL

INVESTOR
Město Praha 11
Čestná 102/1, 102 01, Praha 11

ČÍSLO
0

ČÁST DOKUMENTACE
1.1

OBSEK VÝKRESU
"A" PŮDORYS 2NP - BOURÁNÍ

HOŘKOV
158
SATURN
11.11.2020

STUPĚŇ ČÍSLO ČÁST ČÍSLO PŘÍLOHA REVIZE
DPS D 1.1 103

ZPRACOVATEL ČÁSTI
Ing. arch. Janek Vojta
F. Boudník 102/1
www.asapoint.cz

GENÉRALNÍ PROJEKTANT
Ing. arch. Janek Vojta
F. Boudník 102/1
www.asapoint.cz