

Výkaz mírostnosti NNP B					
Číslo	Název	Podtři	Oyem	Plocha	Poznámka
497	Schödtst	NNP B	52,28 m ³	18 m ²	
49X	Schödtst	NNP B	51,13 m ³	18 m ²	
400	Chorba	NNP B	223,16 m ³	76 m ²	
401	Severovra	NNP B	22,33 m ³	7 m ²	
402	Kancelář	NNP B	110,33 m ³	38 m ²	
403	Kancelář	NNP B	55,76 m ³	19 m ²	
404	Kancelář	NNP B	54,46 m ³	19 m ²	
405	Kancelář	NNP B	69,97 m ³	24 m ²	
406	Kancelář	NNP B	40,50 m ³	14 m ²	
407	Kancelář	NNP B	31,97 m ³	11 m ²	
408	Kancelář	NNP B	68,18 m ³	23 m ²	
409	Kancelář	NNP B	54,46 m ³	19 m ²	
410	Kancelář	NNP B	54,12 m ³	19 m ²	
411	Kancelář	NNP B	46,83 m ³	16 m ²	
412	Zasedací místnost	NNP B	59,98 m ³	21 m ²	
413	Sklad	NNP B	23,56 m ³	8 m ²	
414	Kancelář	NNP B	32,76 m ³	11 m ²	
415	Kancelář	NNP B	33,96 m ³	12 m ²	
416	Kuchyňka	NNP B	14,69 m ³	5 m ²	
417 A	Umývárna	NNP B	7,36 m ³	3 m ²	
417 B	WC Dámy	NNP B	6,42 m ³	2 m ²	
418	Uklízková místnost	NNP B	5,17 m ³	2 m ²	
419 A	Umývárna	NNP B	5,91 m ³	2 m ²	
419 B	WC Páni	NNP B	6,09 m ³	2 m ²	
420	Kancelář	NNP B	32,77 m ³	11 m ²	
421	Kancelář	NNP B	31,74 m ³	11 m ²	
422	Kancelář	NNP B	17,59 m ³	6 m ²	
423	NNP B	NNP B	29,75 m ³	10 m ²	

POZNÁMKY:

VÝZKUM K CHARAKTERU STAVBY REKONSTRUKCE JE NUTNÉ VĚSTŘE ROZMĚRY OVĚŘOVAT NA STAVBĚ A ODCHYLKY OD
PŘEDPISŮ A DOKUMENTACE ZUŠENĚ PŘI PROVÁDĚNÍ STAVBY KONZULTOVAT S PROJEKTOVATEM

U BOURÁNÝCH KONSTRUKCÍ JE NUTNÉ OVĚŘIT PŘÍMO NA STAVBĚ JEJICH NOSNOST KAPITULY, V PŘÍPADĚ NESROVNALOSTI NUTNĚ
KONTAKTOVAT KONSTRUKČNÍ STATIKA

KOTVĚ BOURANÝCH KONSTRUKCÍ MAJÍ INFORMATIVNÍ CHARAKTER, OSAZENÍ NOŽNÍ
PRÁVKY DLE NAVRŽENÉHO ŘEŠENÍ



VEŠKÉ BOURÁNÍ PROSTUPU A DRAŽKY PRO VEŠENÍ INSTALACÍ BUDOU PROVÁDĚNY DLE POŽADÁVKŮ JEJEDNOTLIVÝCH PROFESÍ

TUO DOKUMENTACE NENAHRAŽUJE DODATELSKOU A DILENSKOU DOKUMENTACÍ

NEDÍLNOST SOUČASTI DOKUMENTACE JSOU DETAILY A TECHNICKÁ ZPRÁVA

LEGENDA MATERIÁLŮ:

	MOBNÁ KONSTRUKCE - ŽS SKELET
	OBVODOVÉ PANELE - OPLÁŠTĚNÍ OBJEKTU
	OBVODOVÉ MOBNÉ ŽIVO
	VNITŘNÍ NEKONCE A PŘÍCHOVÉ ŽIVO
	BOURANÉ / ODBRAVNĚNÉ KONSTRUKCE

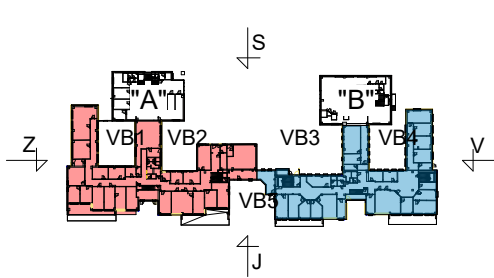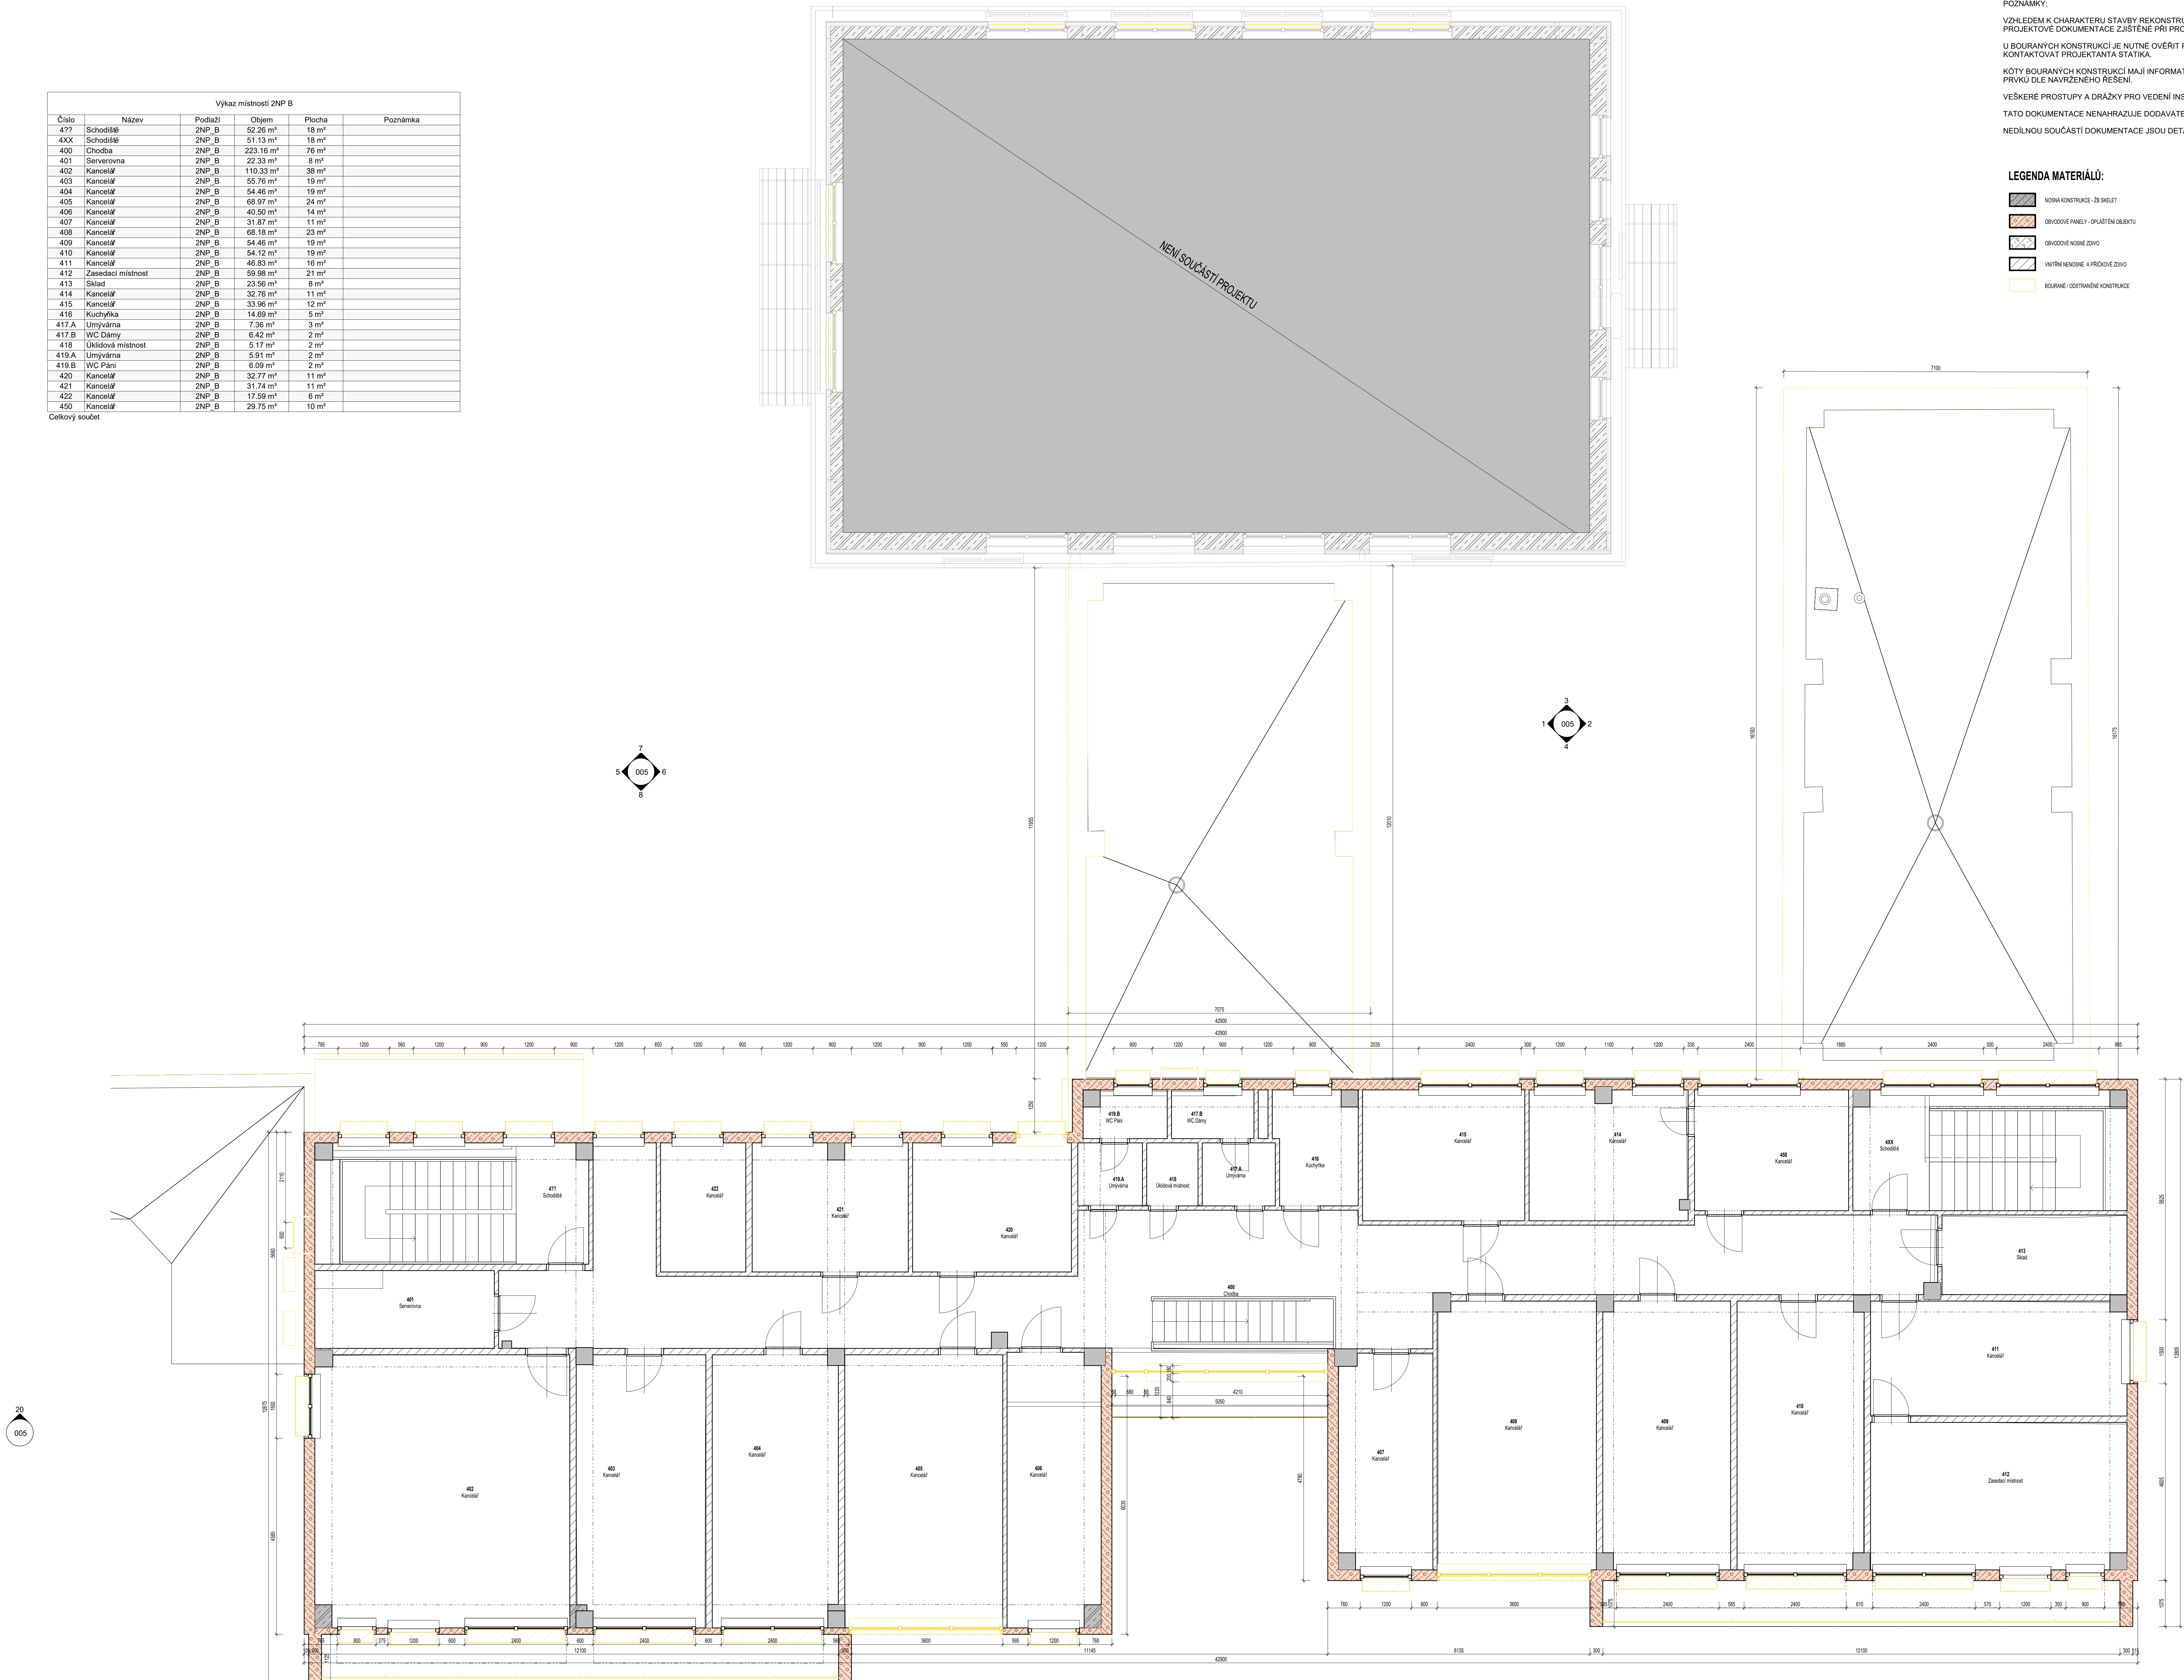

Snížení energetické náročnosti MČ Praha 11

STUPEŇ PROJEKTU +/- 0,000 = 299,330 B.p.v.

DOKUMENTACE PRO PROVEDENÍ STAVBY
(DPS)

ing arch. Jakub Voška, ČKA 03947
733 535 363, jakub.voška@basepoint.cz

VYPRACOVAL

INVESTOR:
Městská část Praha 11
Cetlíková 672/3, 169 43, Praha 6

011
0
ČAST DOKUMENTACE
1,1

B* PŮDORYS 2NP - BOURÁNÍ					
MĚŘÍTKO				FORMÁT	
1:50				A	
DATUM				1.VYDÁNÍ	
02/2026				2/2026	
STUPEŇ	DÍL	ČÁST	ČÍSLO	PRÍLOHA	REVIZ
0PS	0	1.1	104		

ZPRACOVATEL ČÁSTI
basepoint s.r.o.
V Benátskách 1250/4
N9 00, Praha 4
www.basepoint.cz

GENERÁLNÍ PROJEKTANT
basepoint s.r.o.
V Benátskách 1250/4
N9 00, Praha 4
www.basepoint.cz