

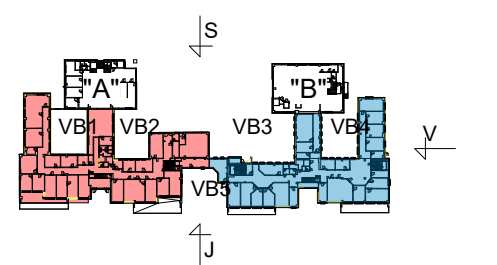
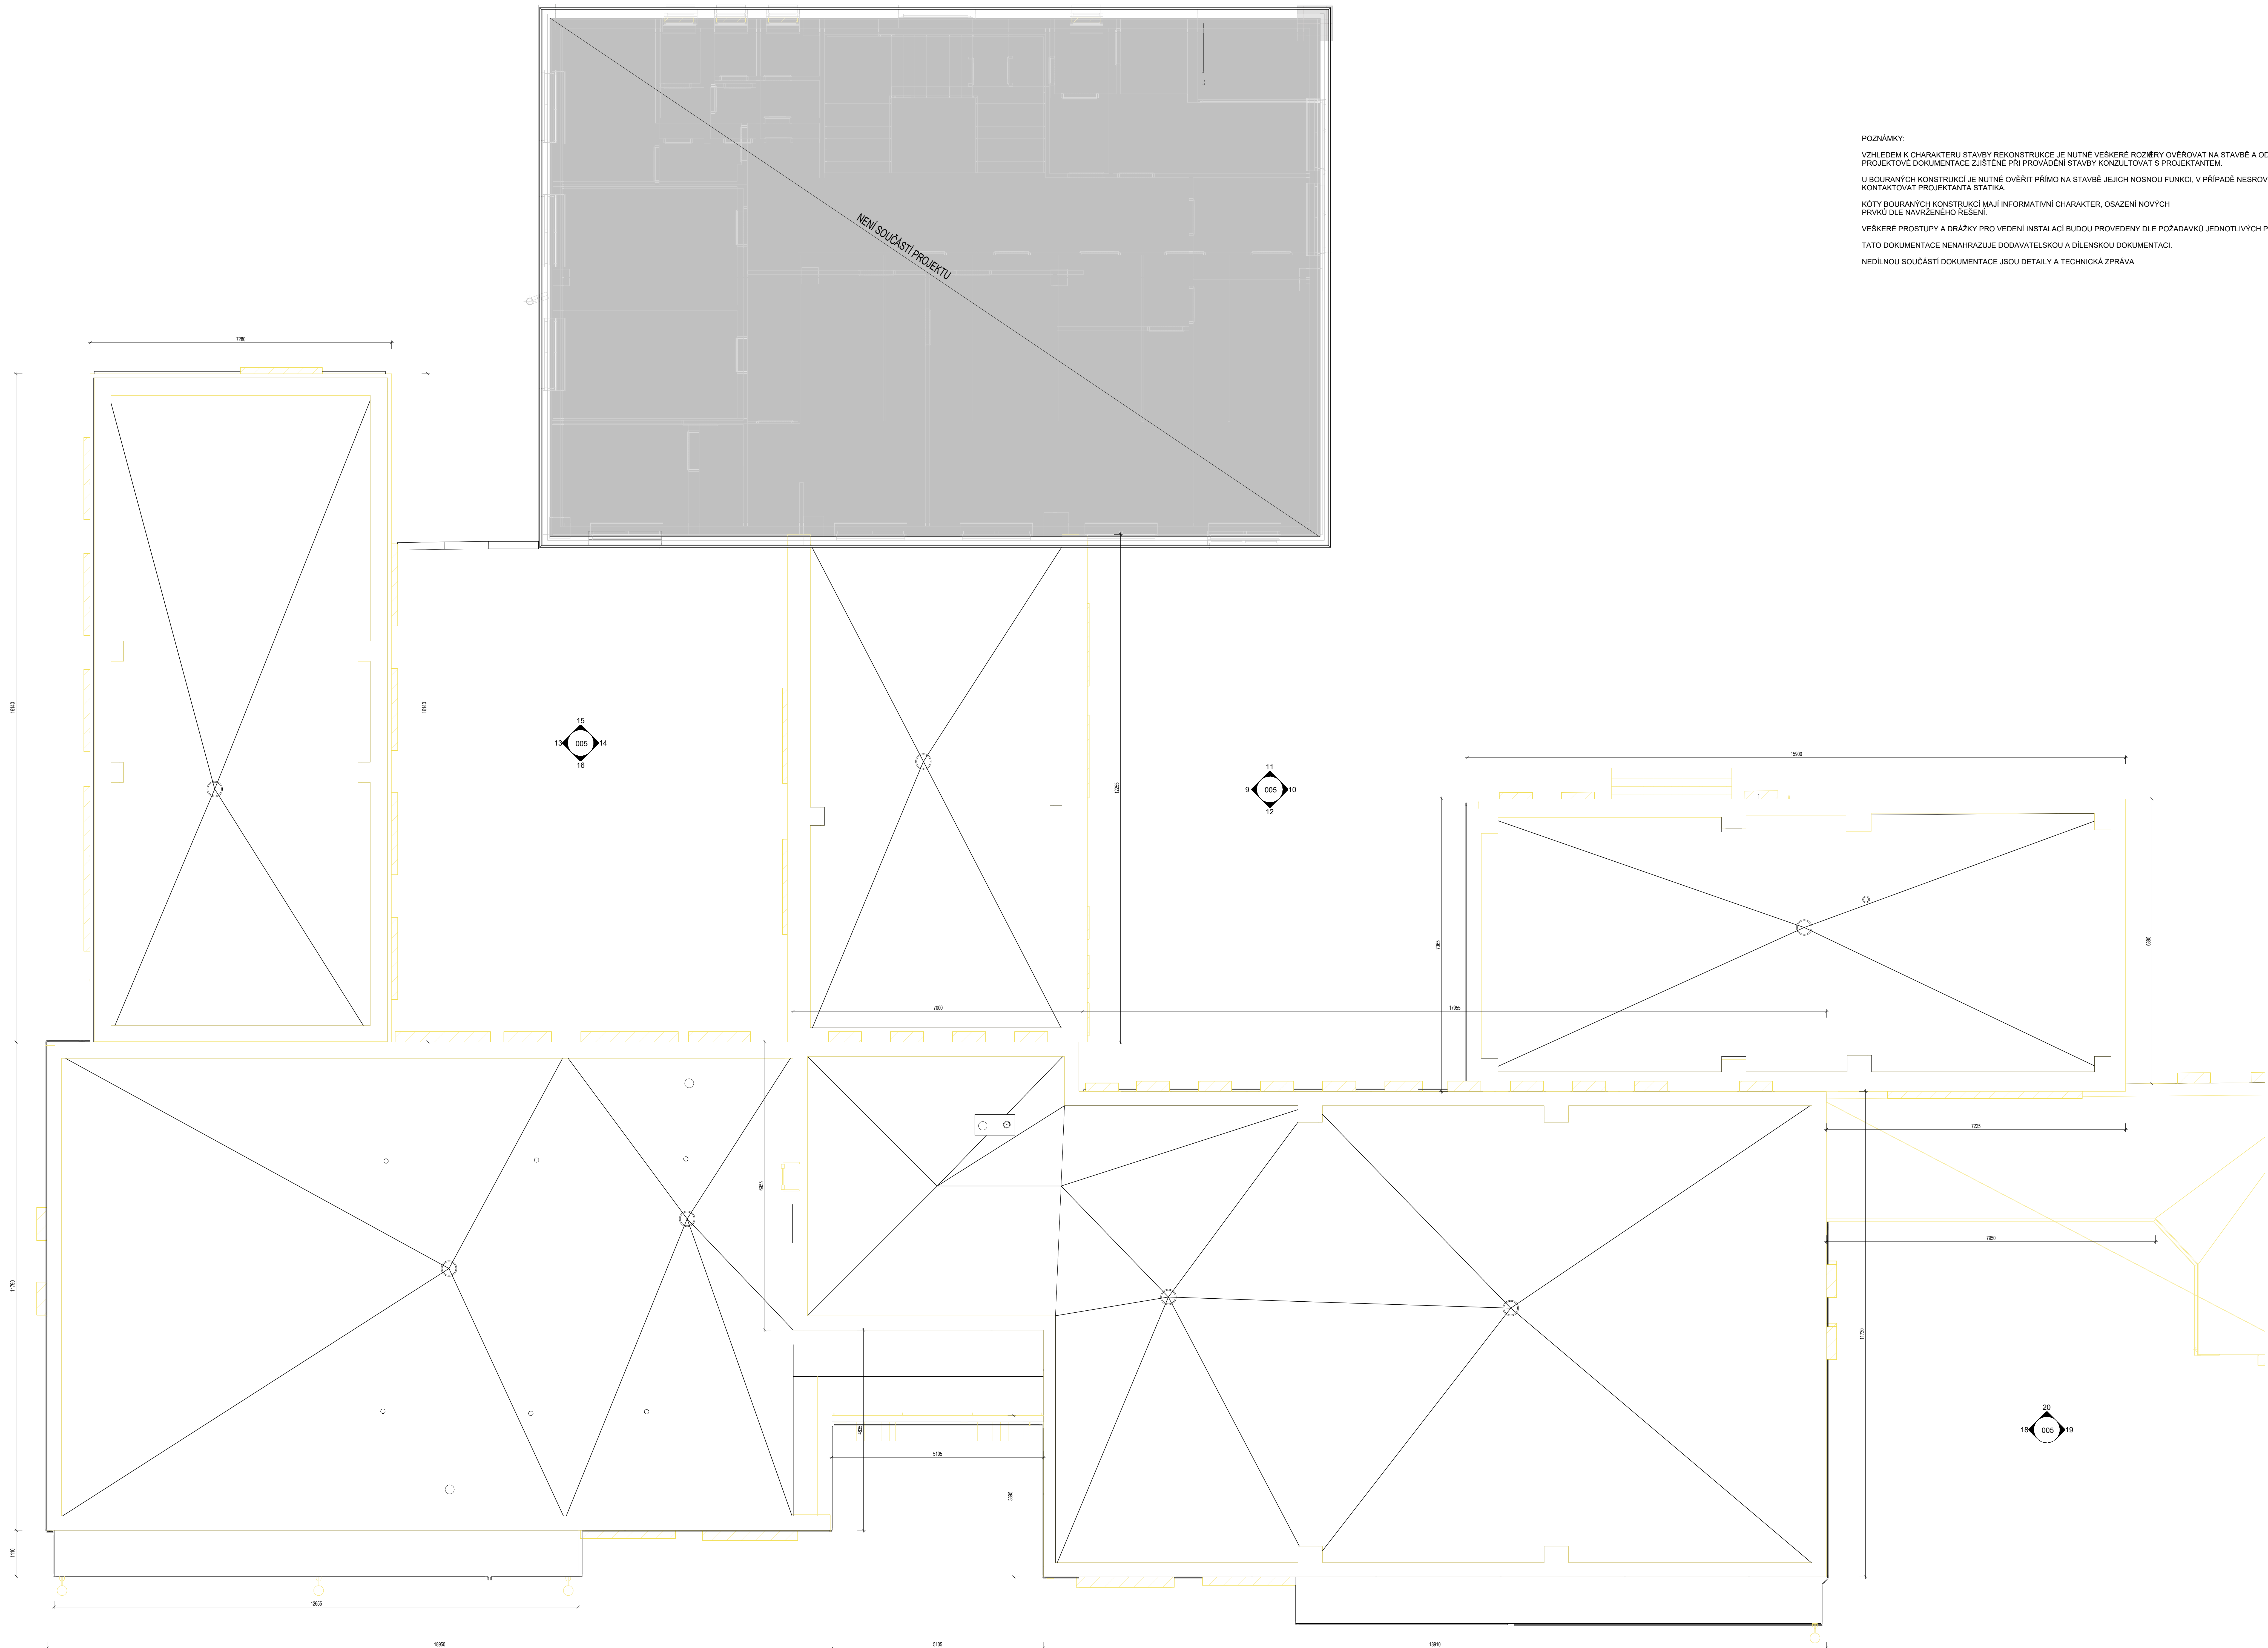
VZHEDEM K CHARAKTERU STAVBY REKONSTRUKCE JE NUTNÉ VEŠKERÉ ROZÍŘY OVĚŘOVAT NA STAVBĚ A OOOHYLYK OD PROJEKTOVÉ DOKUMENTACE ZJISTĚNĚ PŘI PROVÁDĚNÍ STAVBY KONZULTOVAT S PROJEKTANTEM.

U BOURANÝCH KONSTRUKCÍ JE NUTNÉ OVĚŘIT PŘÍMO NA STAVBĚ JEJICH NOSNOU FUNKCI, V PŘÍPADĚ NESROVNALOSTÍ NUTNĚ KONTAKTOVAT PROJEKTANTA STATIKA.

KÓTY BOURANÝCH KONSTRUKCÍ MAJÍ INFORMATIVNÍ CHARAKTER, OSAZENÍ NOVÝCH PRVKŮ LE NAVRŽENÉHO ŘEŠENÍ.

TATO DOKUMENTACE NENAHAZUJE DODAVATELSKOU A DÍLENSKOU DOKUMENTACI.

NEDÍLNOU SOUČÁSTÍ DOKUMENTACE JSOU DETAILS A TECHNICKÁ ZPRÁVA

nížení energetické
ročnosti MČ Praha 11

linova 1324/4 a 1325/2, Praha-Chodov.

UPEN PROJEKTU +/- 0,000 = 299,330 B.p.v.

KUMENTACE PRO PROVEDENÍ STAVBY
(PS)

POVĚRNÝ PROJEKTANT
arch. Jakub Volka, ČKA 83947
8 595 363, jakub.volka@basepoint.cz

PRACCOVAL

PESTOR
ntská část Praha 11
líková 672/1, 169 43, Praha 4

SAH VÝKRESU

* - PŮDORYS STŘECHY - BOURÁNÍ

FORMAT	28 X
--------	------

TUM	1VYDĀNĪ
-----	---------

UPRN 011 ČAST ČÍSLO PRÍLOHA REVIZIE

\$	0	11	115
----	---	----	-----

april s.r.l.
mittwoch 21.05.11

00, Praha 4
www.baspoint.cz

VERÄLMÉ PROJEKTANT
spol s r. o.

base • point
