


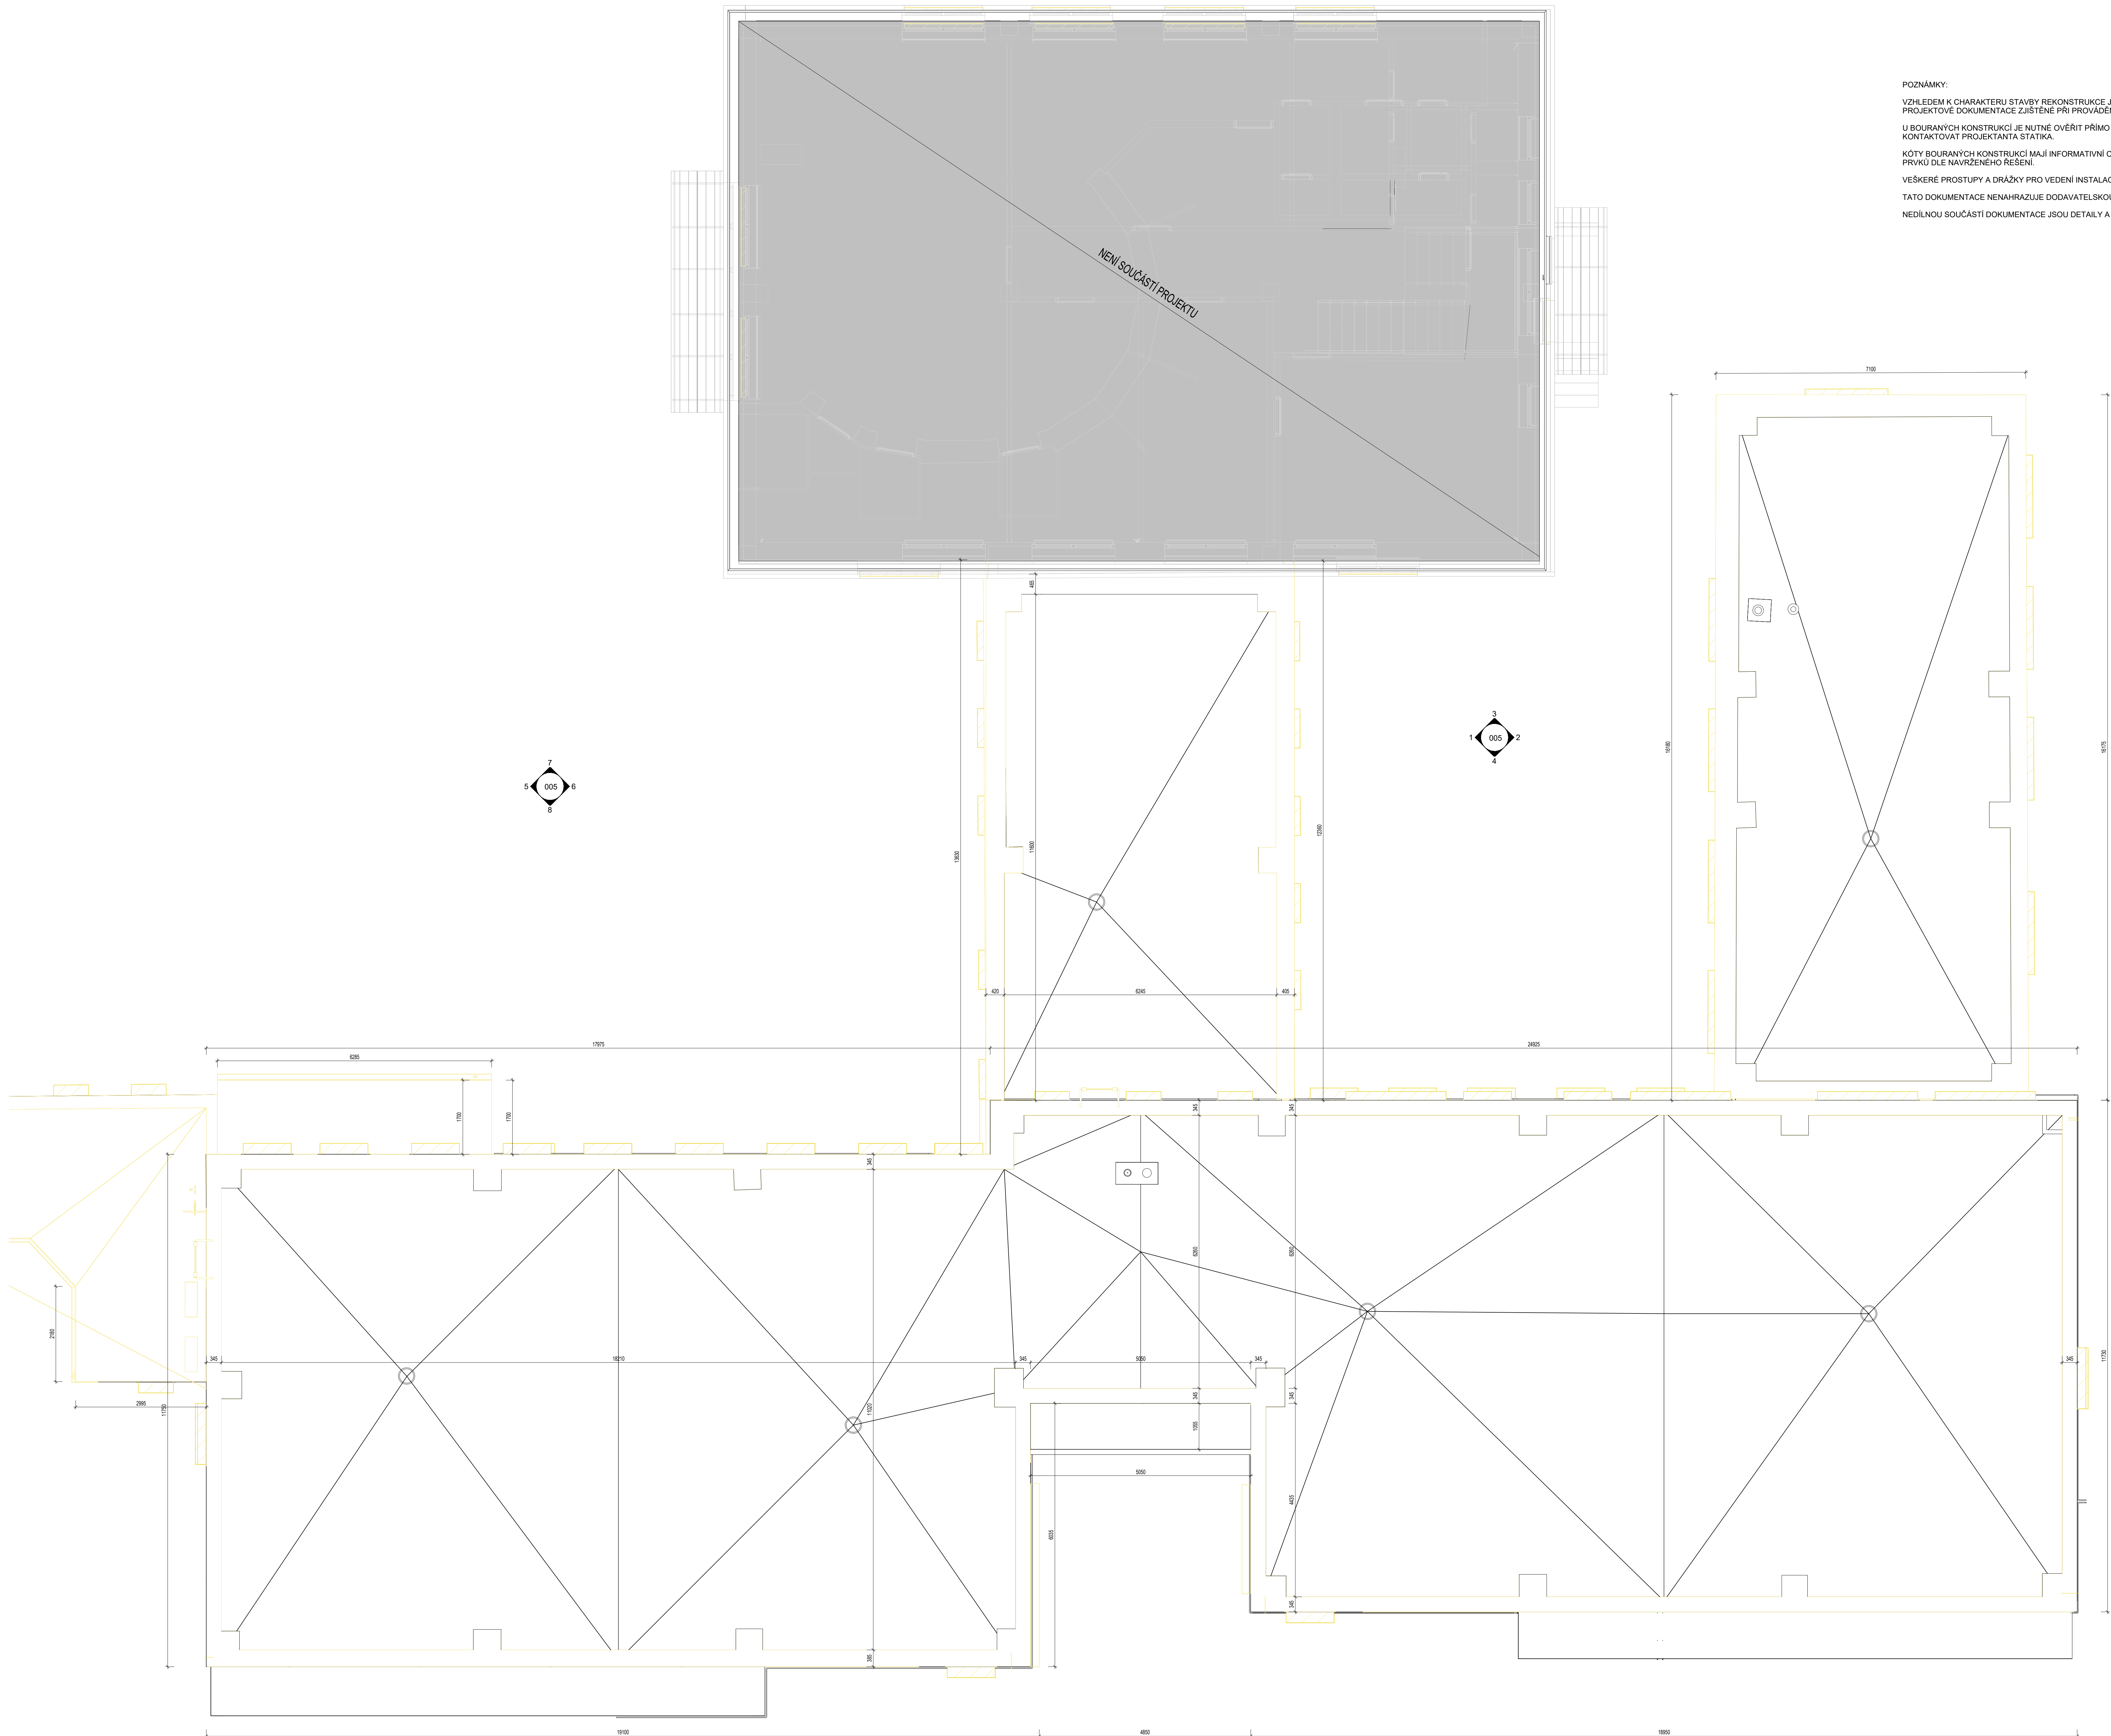

POZNÁMKY:

VZHLEDEM K CHARAKTERU STAVBY REKONSTRUKCE JE NUTNÉ VEŠKERÉ ROZMĚRY OVĚROVAT NA STAVBĚ A ODCHYLKY OD PROJEKTOVÉ DOKUMENTACE ZJIŠTĚNÉ PŘI PROVÁDĚNÍ STAVBY KONZULTOVAT S PROJEKTANTEM.


U BOURANÝCH KONSTRUKCÍ JE NUTNÉ OVĚRIT PŘÍMO NA STAVBĚ JEJICH NOSNOU FUNKCI, V PŘÍPADĚ NESROVNALOSTI NUTNĚ KONTAKTOVAT PROJEKTANTA STAVBAŘA.

KÓTY BOURANÝCH KONSTRUKCÍ MAJÍ INFORMATIVNÍ CHARAKTER, OSAZENÍ NOVÝCH PRVKŮ DLE NAVRŽENÉHO ŘEŠENÍ.

VEŠKERÉ PROSTUPY A DŘÁŽKY PRO VEDENÍ INSTALACÍ BUDOU PROVEDENY DLE POŽADAVKŮ JEDNOTLIVÝCH PROFESÍ.

TATO DOKUMENTACE NENAHRAŽUJE DODAVATELSKOU A DÍLENSKOU DOKUMENTACI.

NEDÍLNOU SOUČÁSTÍ DOKUMENTACE JSOU DETAILY A TECHNICKÁ ZPRÁVA

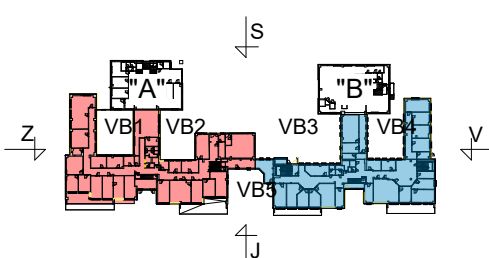

Snížení energetické náročnosti MČ Praha 11

Viděnská 1024/4 a 1025/2, Praha-Chodov

STUPEŇ PROJEKTU: 1.1 - 0.000 - 293.330 B.p.v.

DOKUMENTACE PRO PROVEDENÍ STAVBY (DPS)

ODPOVĚDNÝ PROJEKTANT
Ing. arch. Jakub Větroš, ČKA 63641
733 575 363, jakub.vetrosh@basepoint.cz

VYPRACOVAL:

INVESTOR:
Městská část Praha 11
Opatřilská 672/1, 163 41, Praha 4

DĚL:
D - ČÁST DOKUMENTACE
1.1

OBSAH VÝKRESU:
"B" - PŘÍPOJEK STŘECHY - BOURÁNÍ

MĚŘÍTKO: 1:100
FORMÁT: A4
DATUM: 11/2024
ZPRACOVATEL: 2/2024
STUPEŇ: DĚL - ČÁST (ČÍSLO PRŮLOHA, REVIZE)
DPS: D 1.1 106

ZPRACOVATEL ČÁSTI:
basepoint s.r.o.
Větrošská 1024/4
163 41, Praha 4
www.basepoint.cz

GENERÁLNÍ PROJEKTANT:
basepoint s.r.o.
Větrošská 1024/4
163 41, Praha 4
www.basepoint.cz