




Pohled "S" - severní, M 1:100

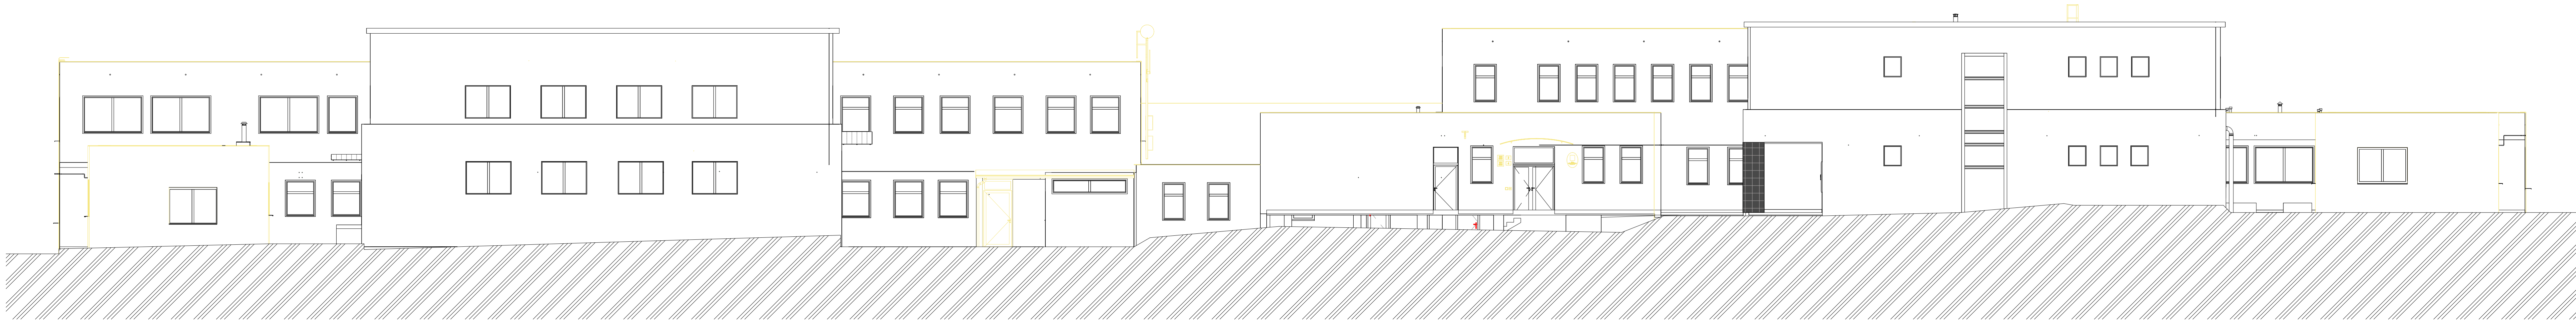



Pohled "J" - jižní, M 1:100

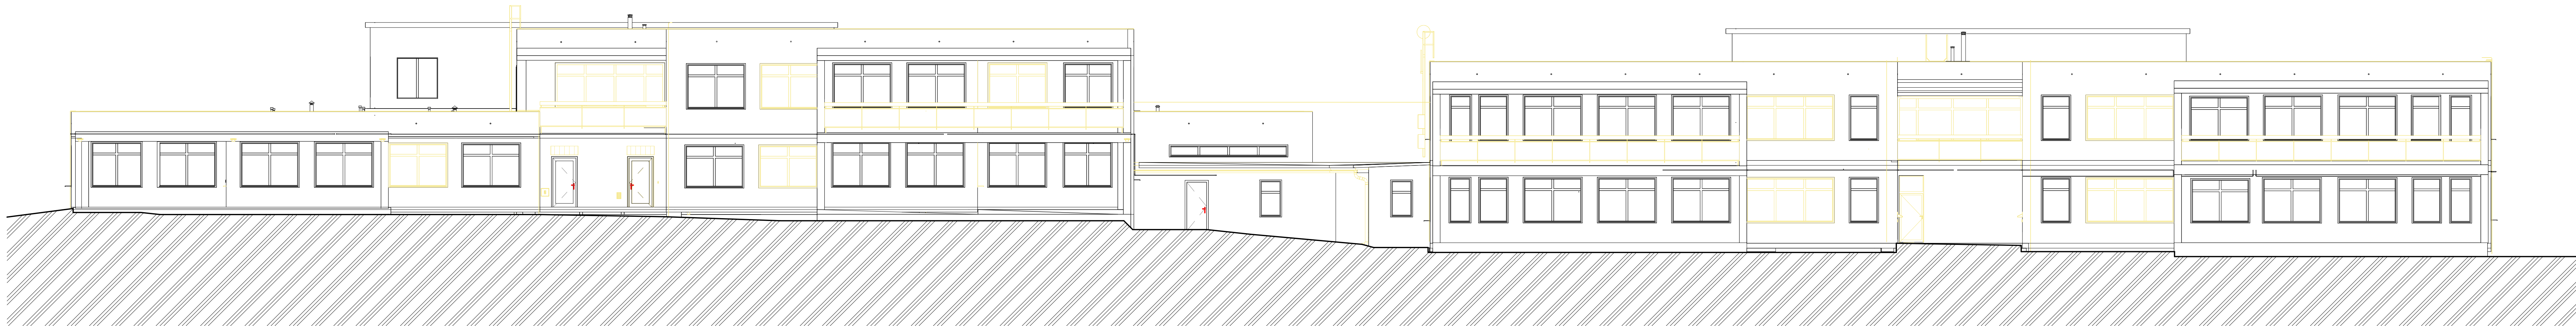

Pohled "V" - východní, M 1:100

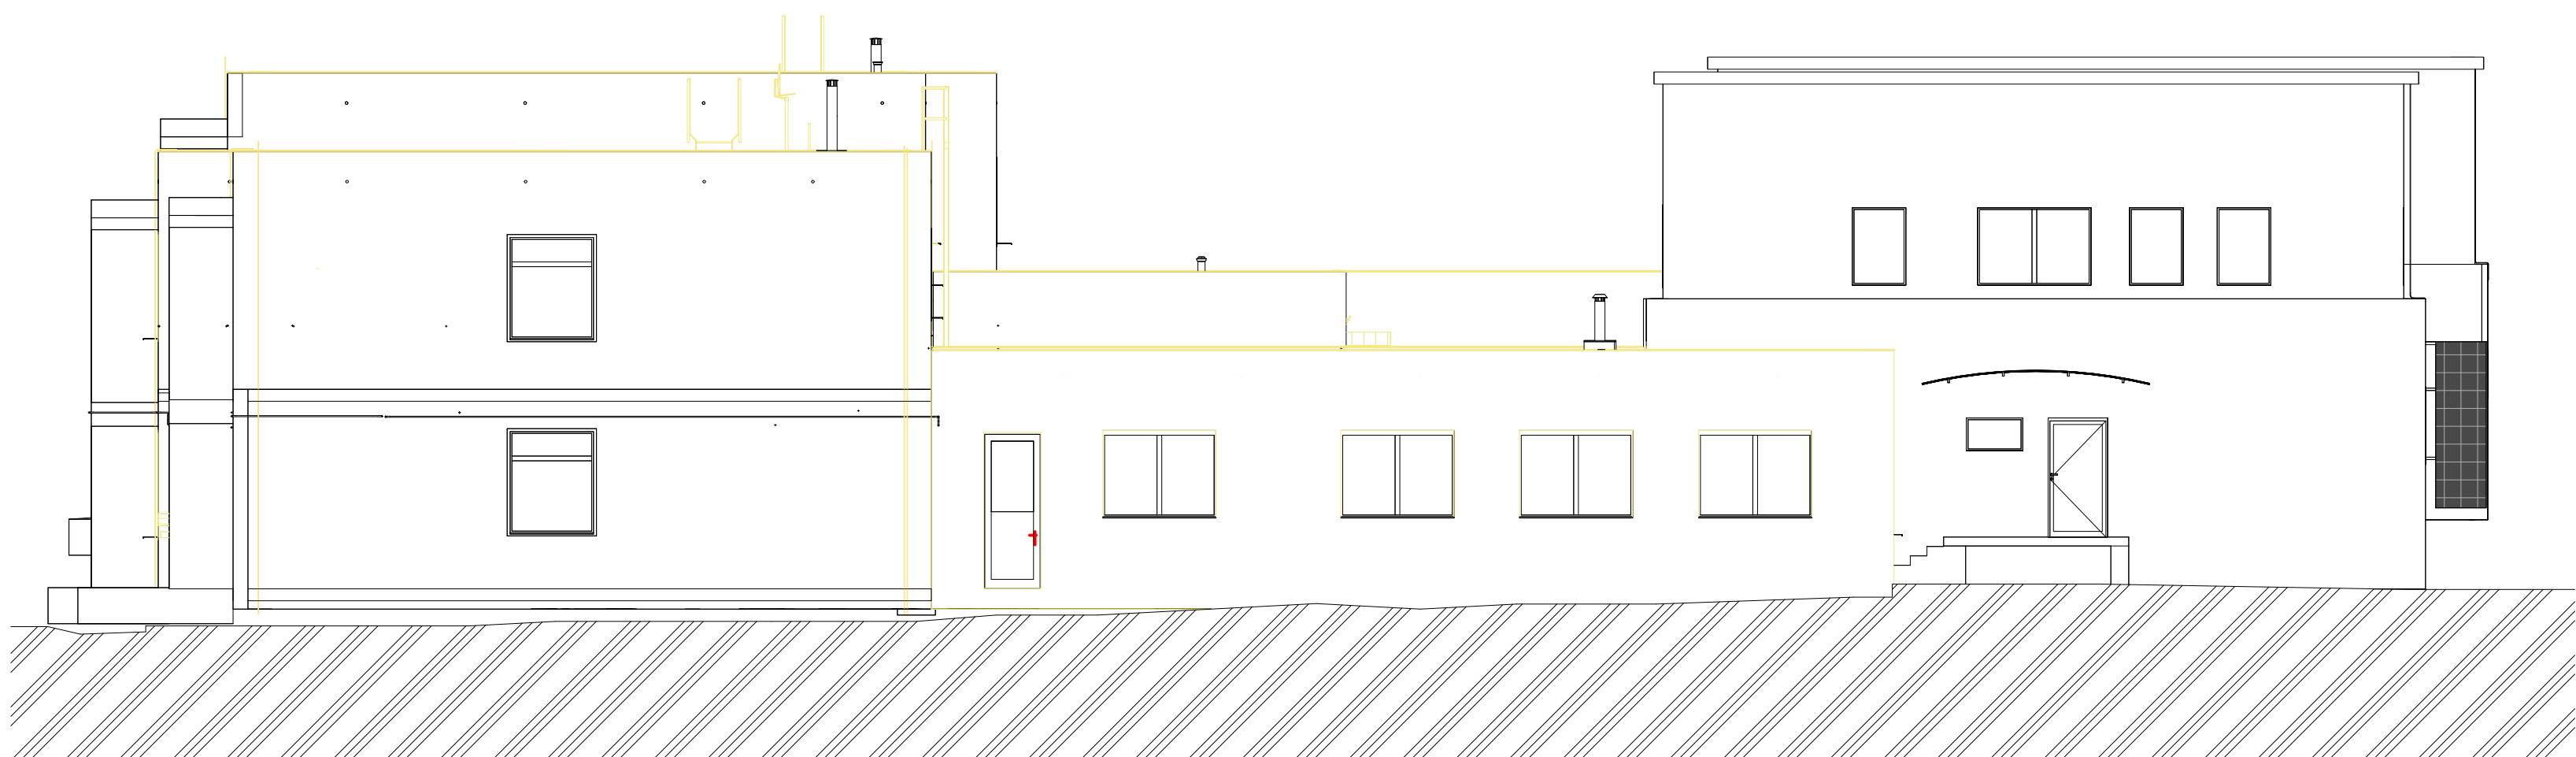

Pohled "Z" - západní, M 1:100

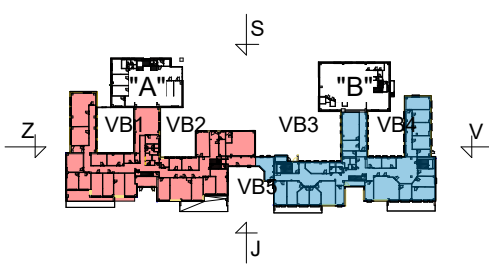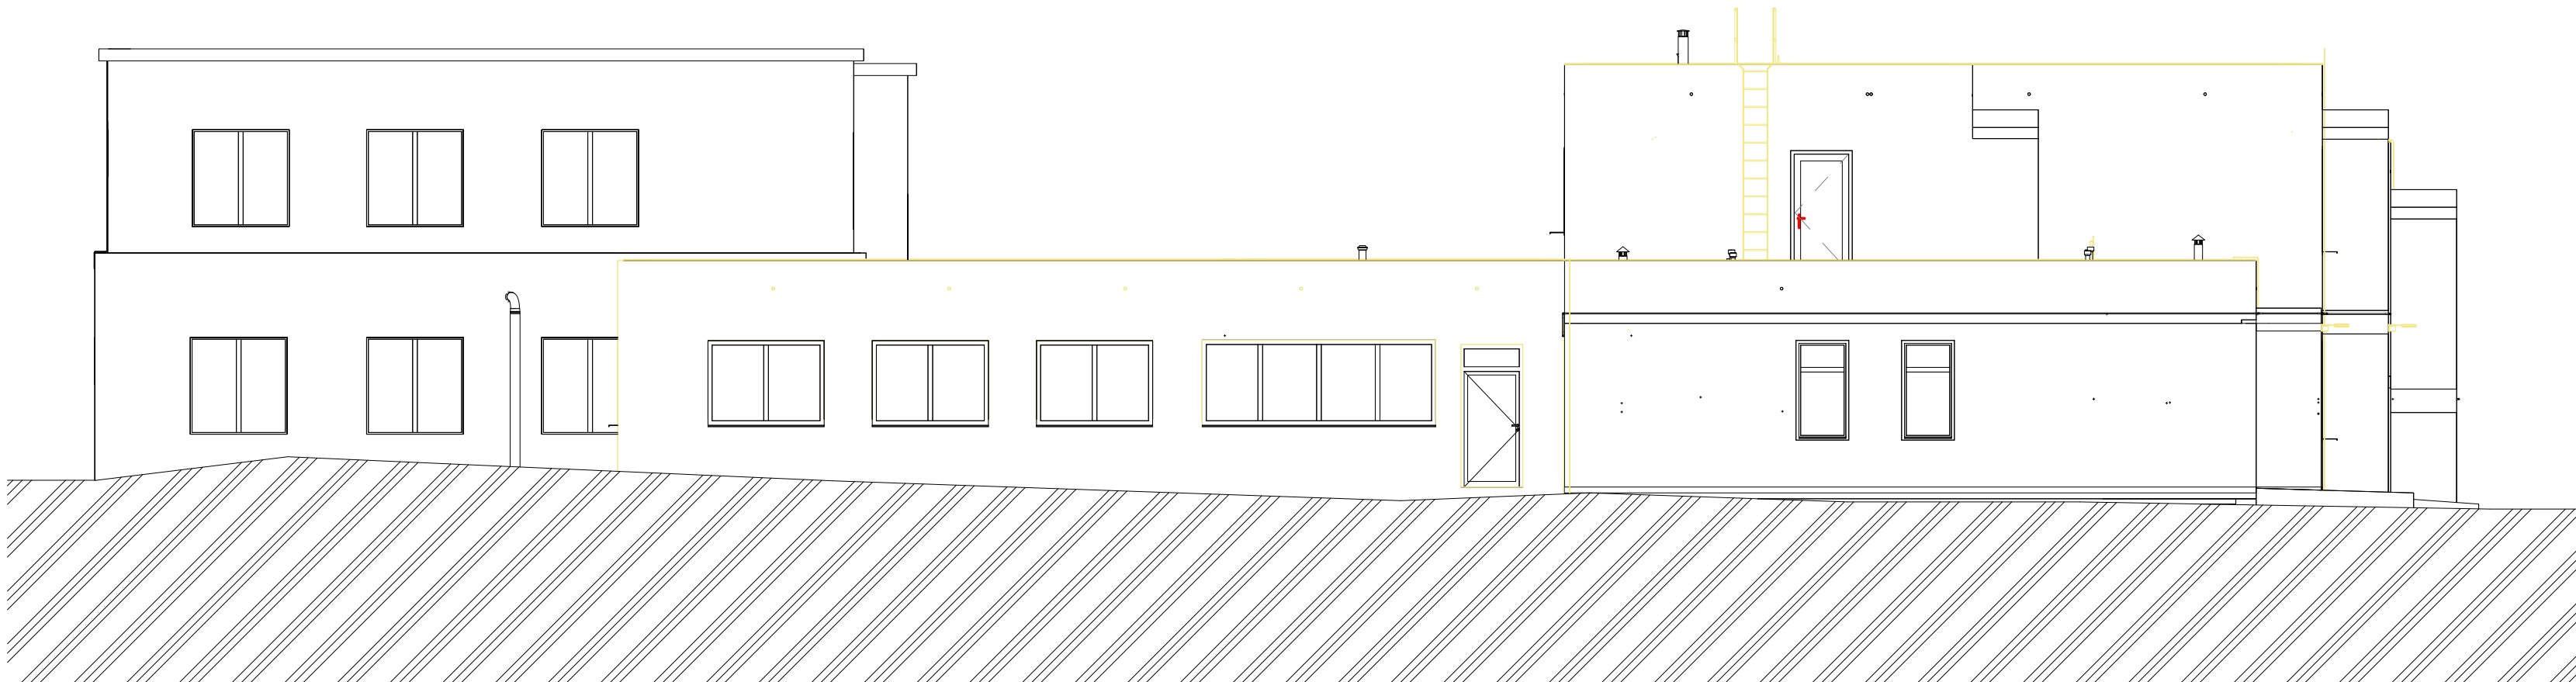

Snížení energetické
náročnosti MČ Praha 11

Vodňova 1324/1 a 1325/2, Praha-City

STUPEŇ PROJEKTU 1:100
DOKUMENTACE PRO PROVEDENÍ STAVBY (DPS)

ODPOVĚDNÝ PROJEKTANT
Ing. arch. Janek Vojtek, ECA 0363
133 575 343, janek.vojtek@casapoint.cz

VYPRACOVAL
INVESTOR
Městská část Praha 11
Dobřelešská 472/1, 161 01, Praha 4

Díl	D
Část dokumentace	1.1
Obsah výkresu	POHLEDY - S, J, V, Z, - BOURÁNÍ
Měřítko	Formát
1:100	B x A4
Datum	Vydání
17.12.2024	1/1
Stupeň	Díl
DPS	D 1.1 101

ZPRACOVATEL ČÁSTI
Ing. arch. Janek Vojtek, ECA 0363
133 575 343, janek.vojtek@casapoint.cz
www.casapoint.cz
INVESTOR
Ing. arch. Janek Vojtek, ECA 0363
133 575 343, janek.vojtek@casapoint.cz
www.casapoint.cz