


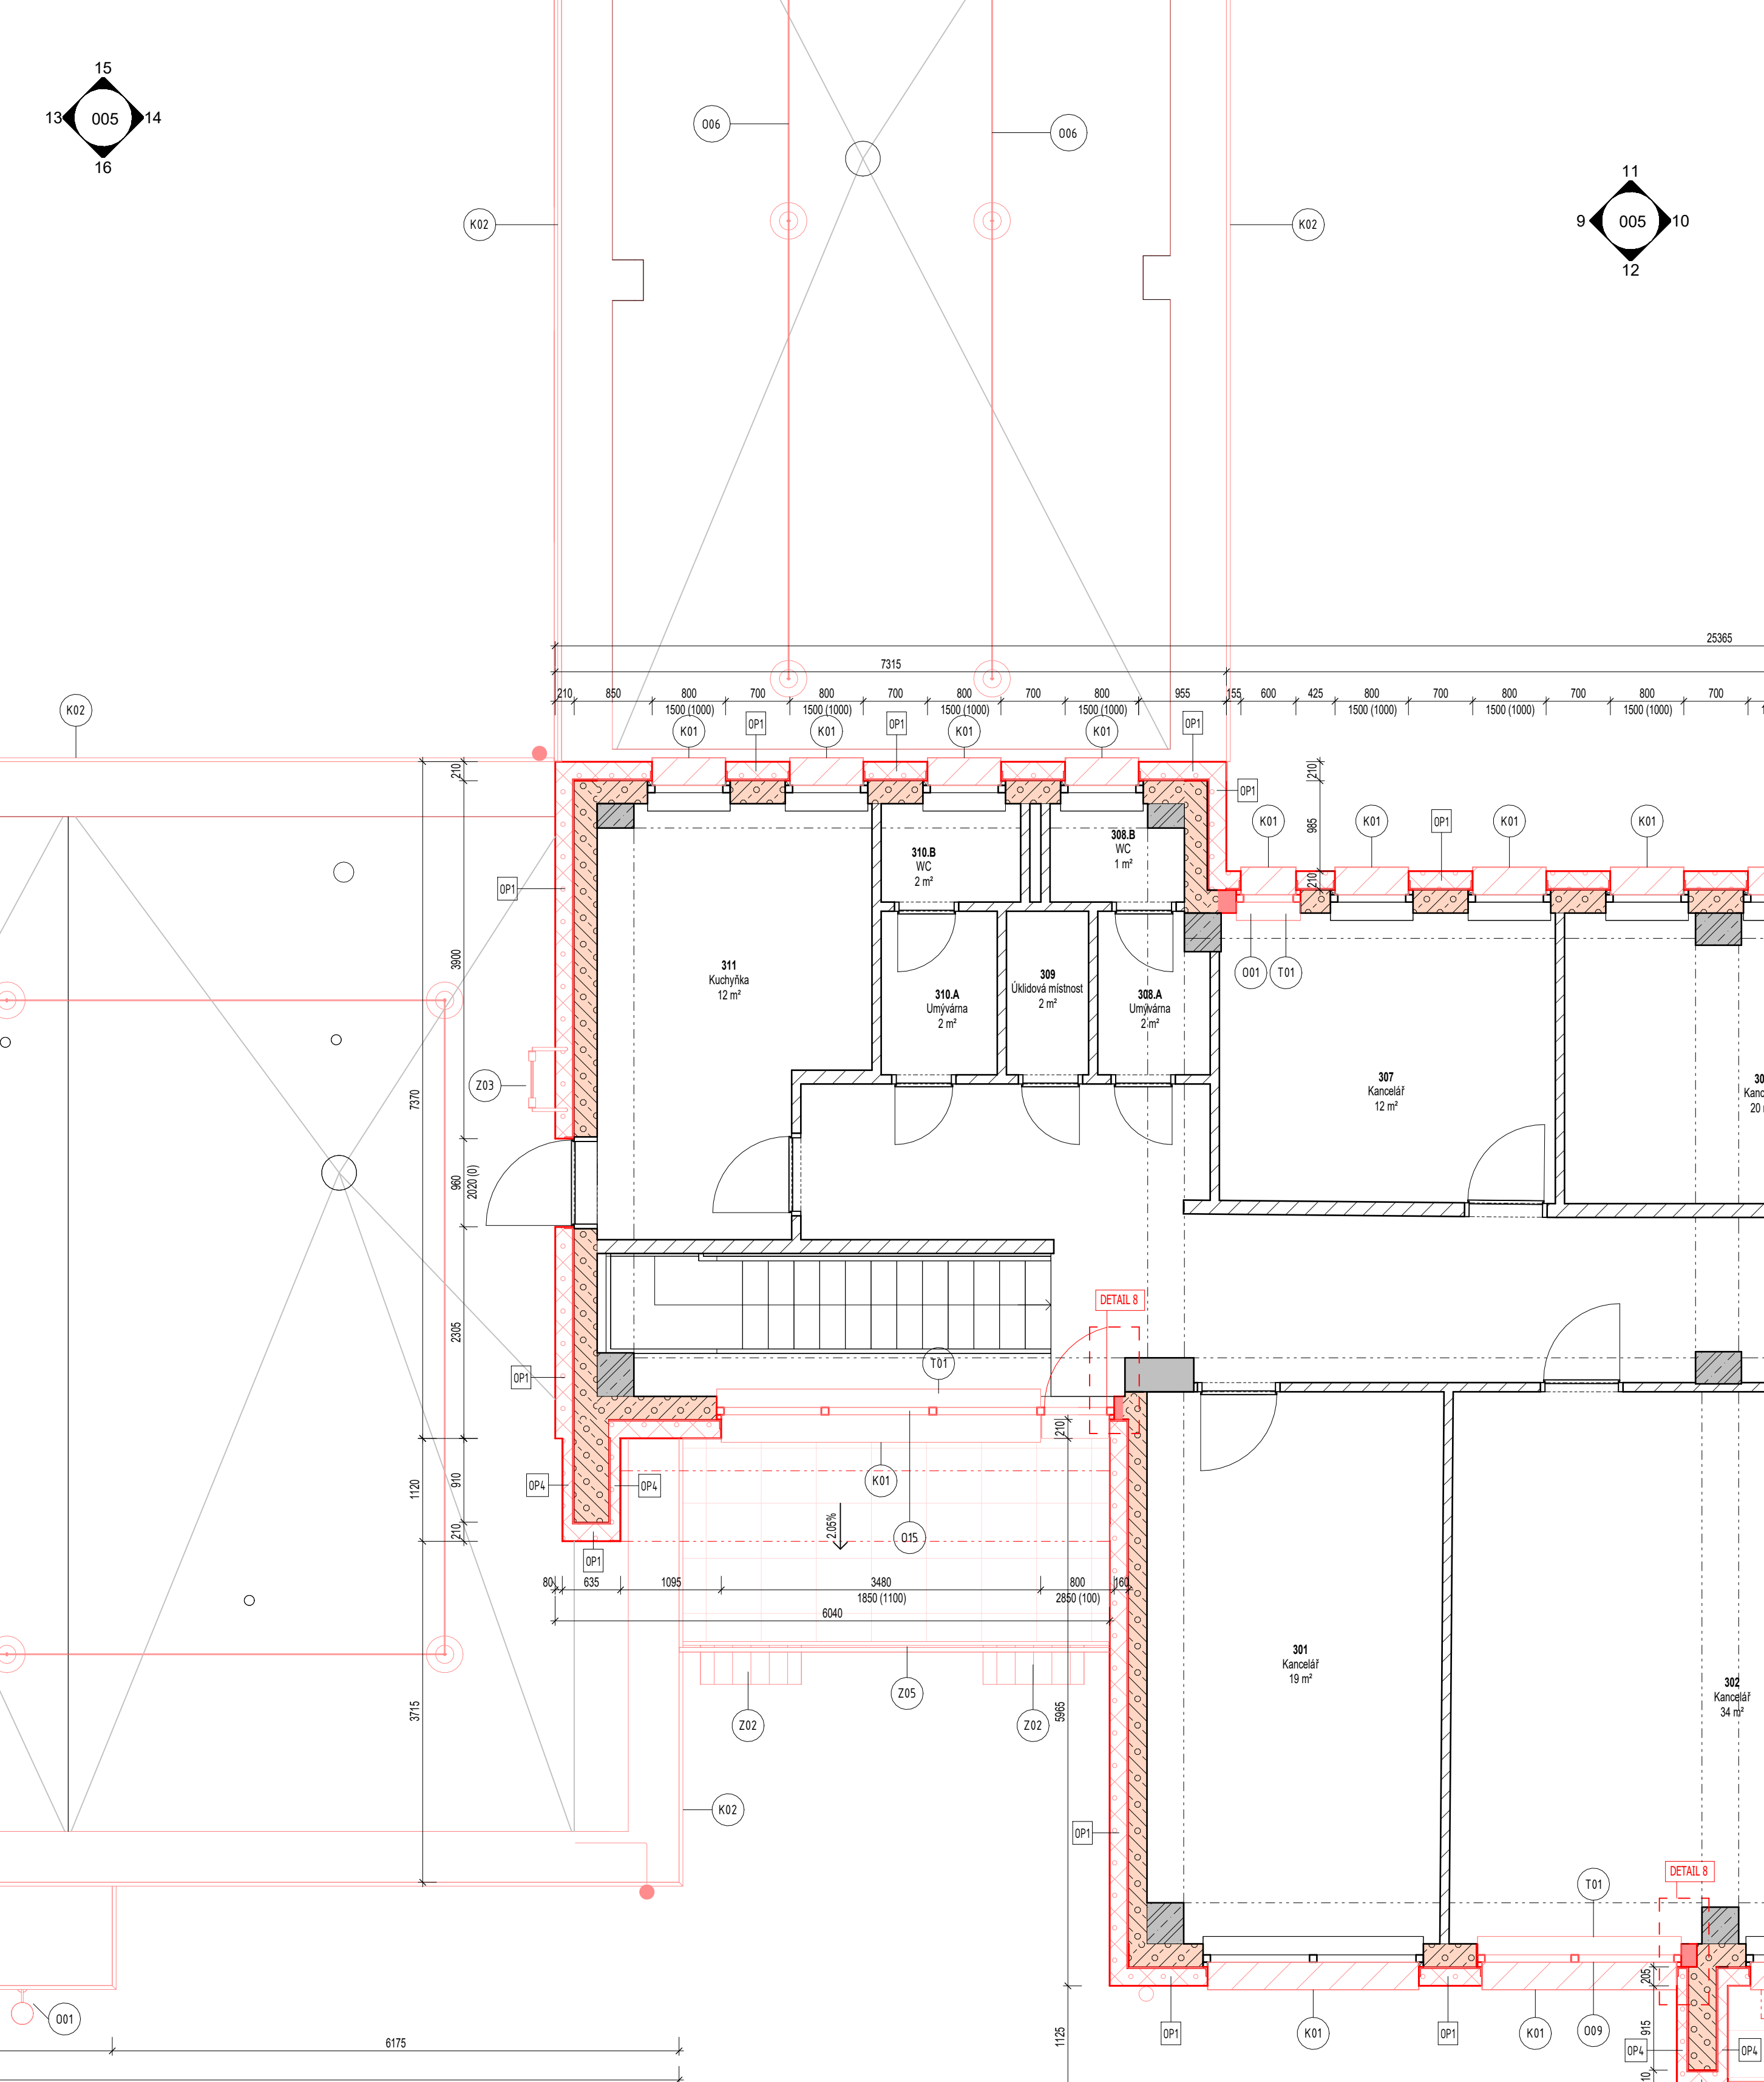

Výkaz miestností ZNP A					
Číslo	Názov	Plocha	Objem	Plocha	Poznámka
6XX	Ukľidová komora	ZNP A	9,41 m ³	4 m ²	
6XX	Umyvárna	ZNP A	3,33 m ³	1 m ²	
6XX	Umyvárna	ZNP A	3,22 m ³	1 m ²	
6XX	WC	ZNP A	3,22 m ³	1 m ²	
6XX	WC	ZNP A	3,27 m ³	1 m ²	
6XX	Kuchyňa	ZNP A	20,59 m ³	8 m ²	
300	Chodba	ZNP A	133,94 m ³	42 m ²	
301	Kanceliá	ZNP A	65,94 m ³	19 m ²	
302	Kanceliá	ZNP A	112,93 m ³	34 m ²	
303	Kanceliá	ZNP A	57,61 m ³	18 m ²	
304	Kanceliá	ZNP A	51,42 m ³	16 m ²	
305	Kanceliá	ZNP A	77,59 m ³	23 m ²	
306	Kanceliá	ZNP A	65,77 m ³	20 m ²	
307	Kanceliá	ZNP A	37,31 m ³	12 m ²	
308 A	Umyvárna	ZNP A	7,10 m ³	2 m ²	
308 B	WC	ZNP A	4,85 m ³	1 m ²	
309	Ukľidová miestnosť	ZNP A	2,16 m ³	2 m ²	
310 A	Umyvárna	ZNP A	7,26 m ³	2 m ²	
310 B	WC	ZNP A	5,39 m ³	2 m ²	
311	Kuchyňa	ZNP A	41,00 m ³	12 m ²	
511	Chodba	ZNP A	68,98 m ³	25 m ²	
512	Umyvárna	ZNP A	5,94 m ³	2 m ²	
513	WC Páni	ZNP A	3,07 m ³	1 m ²	
514	Umyvárna	ZNP A	7,79 m ³	2 m ²	
515	WC Dámy	ZNP A	3,09 m ³	1 m ²	
516	Ukľidová miestnosť	ZNP A	10,60 m ³	4 m ²	
517	Kuchyňa	ZNP A	25,00 m ³	9 m ²	
518	Zásedací miestnosť	ZNP A	72,35 m ³	27 m ²	
519	Kanceliá	ZNP A	173,19 m ³	54 m ²	
520	Kanceliá	ZNP A	43,39 m ³	16 m ²	
521	Kanceliá	ZNP A	42,07 m ³	16 m ²	
522	Kanceliá	ZNP A	64,29 m ³	24 m ²	
528	Šklad	ZNP A	12,22 m ³	5 m ²	
629	Kanceliá	ZNP A	40,59 m ³	17 m ²	
630	Šklad	ZNP A	16,93 m ³	7 m ²	
631	Kanceliá	ZNP A	40,12 m ³	16 m ²	
632	Kanceliá	ZNP A	36,65 m ³	15 m ²	
633	Kanceliá	ZNP A	44,06 m ³	18 m ²	
634	Kanceliá	ZNP A	63,62 m ³	26 m ²	
635	Zásedací miestnosť	ZNP A	59,35 m ³	24 m ²	
636	Kanceliá	ZNP A	26,15 m ³	11 m ²	
X201	Miestnosť	ZNP A	124,70 m ³	51 m ²	

