
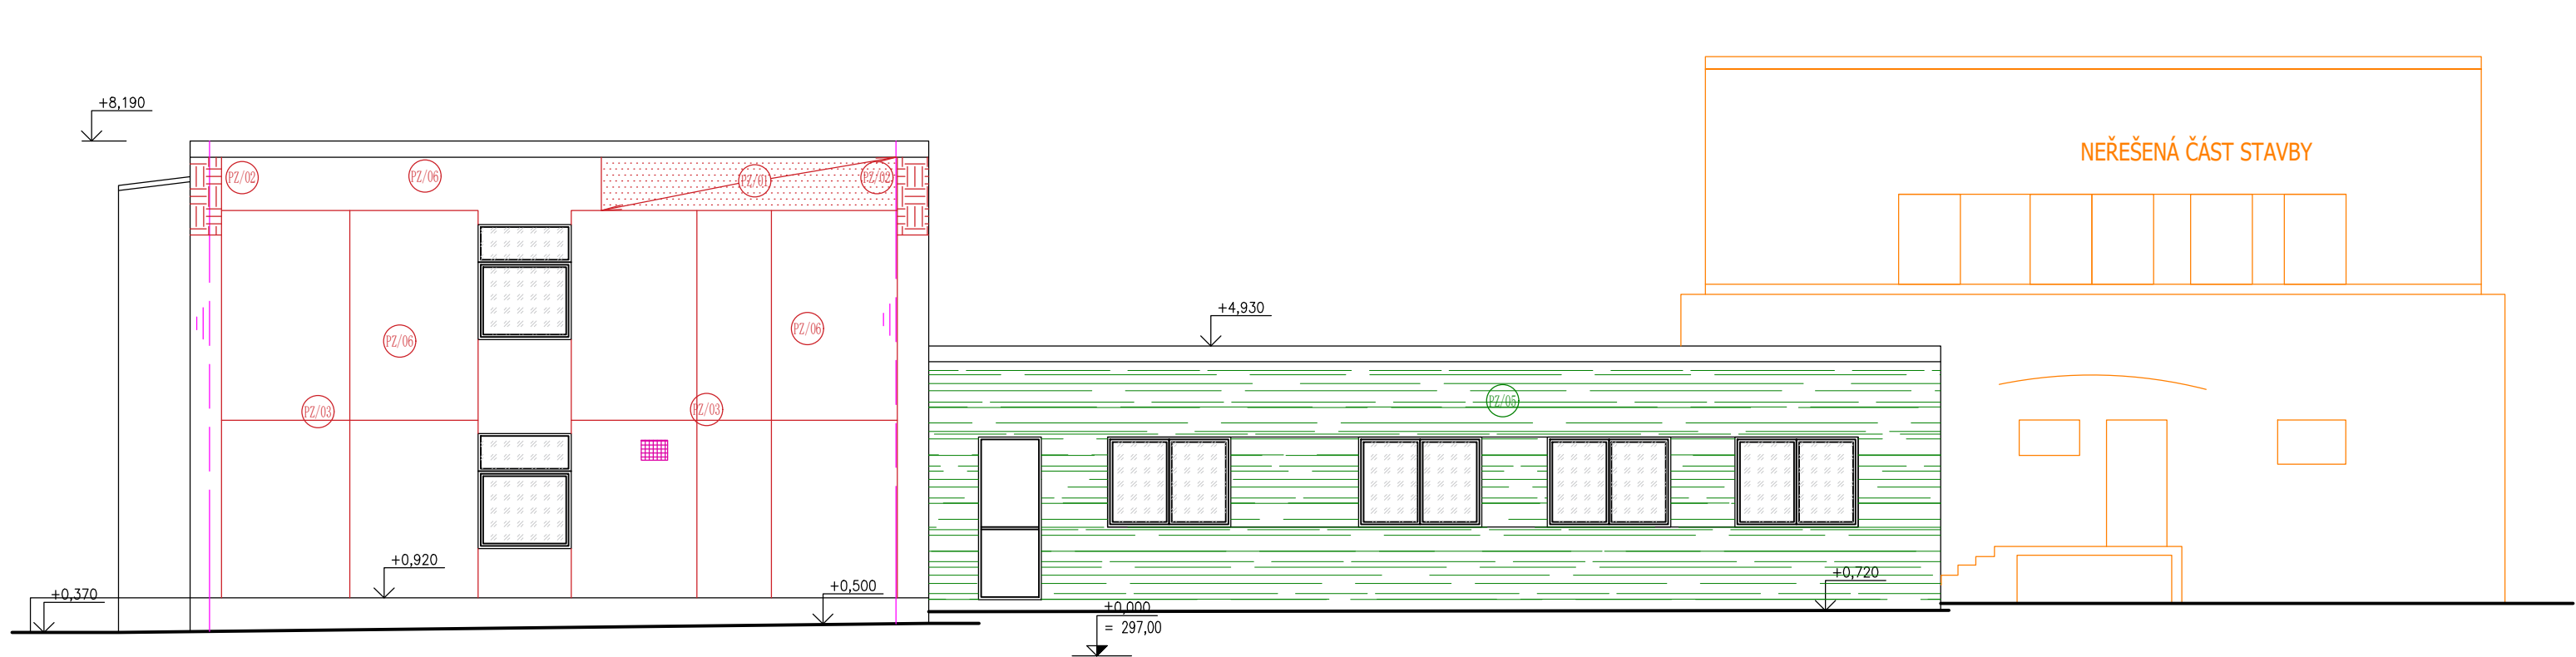


Pohled Západní

Pohled Východní

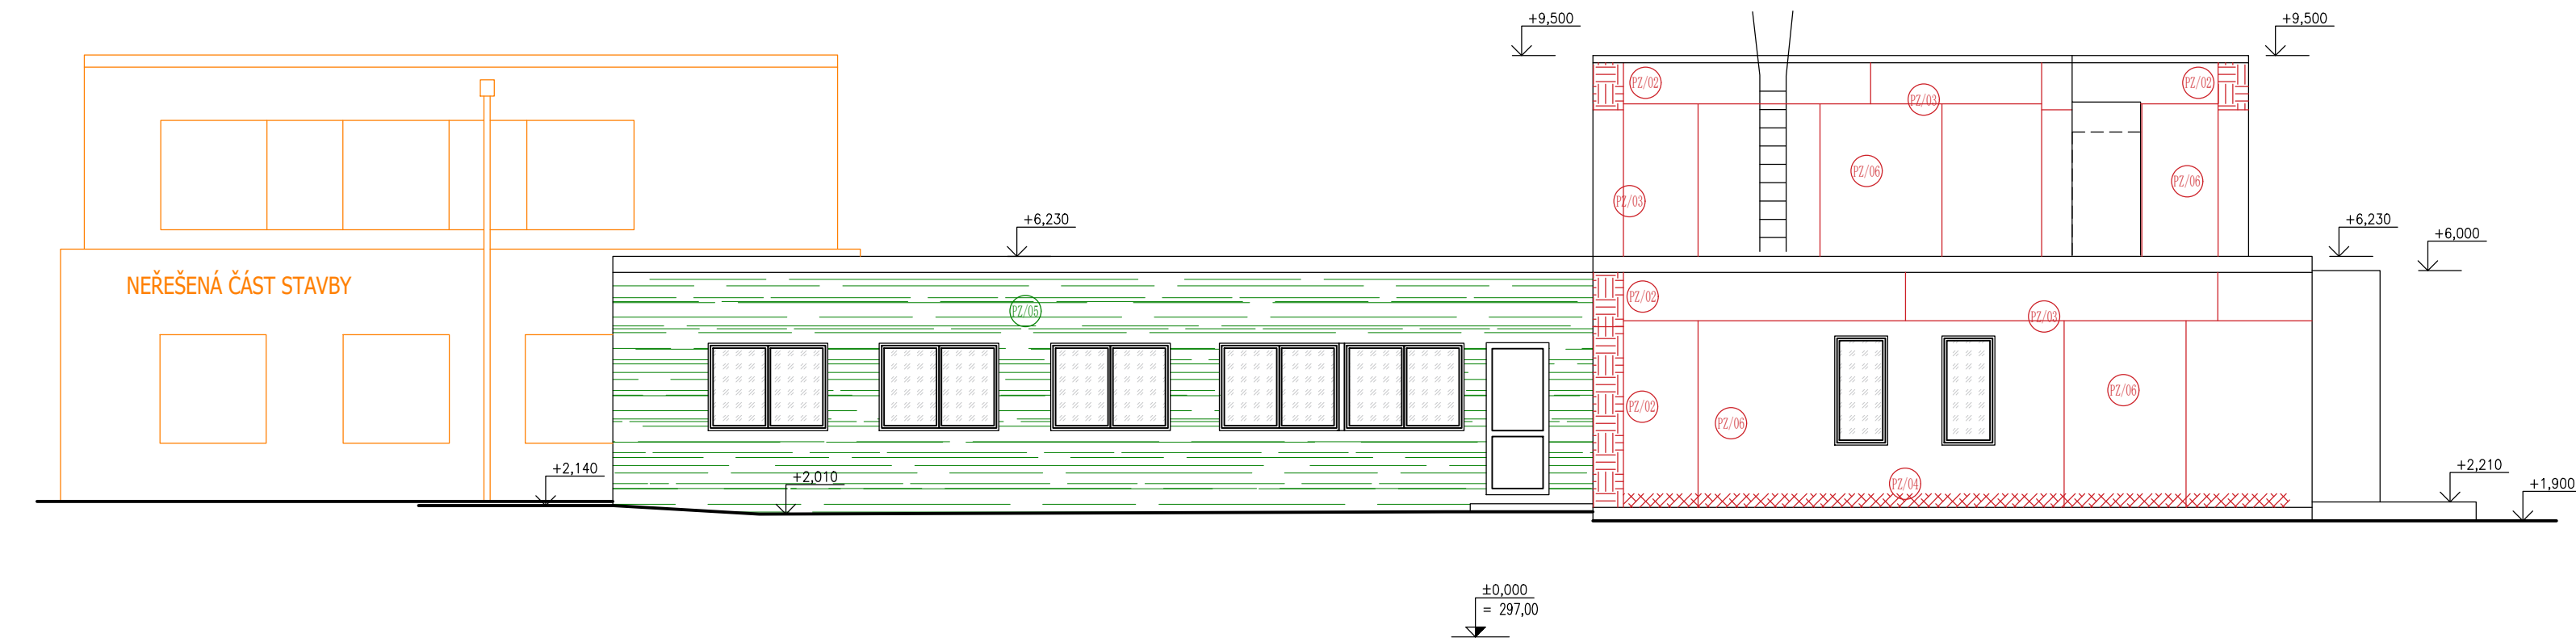

POZNÁMKA – PZ/01
– VYBOČUJÍCÍ ATIKOVÉ ZDIVO – JEDNÁ SE O ATIKOVÉ SENDVIČOVÉ PANELE, KTERÉ JSOU PŘÍVAŘENÉ K ŽB SKELETU. PŘEDPOKLÁDÁ SE, ATIKOVÉ PANELE NEJSOU ODDILATOVANÉ OD BETONOVÉ STROPNÍ DESKY A VLIVEM TEPELNÉ ROZTAŽNOSTI DOŠLO K POSUNUTÍ ATIKOVÝCH PANELŮ. STAVEBNÍMI ÚPRAVAMI DOJDE K ODHALENÍ SPOJŮ ATIKOVÉHO ZDIVA S ŽB SKELETEM A OVĚŘENÍ ŽE NEDOŠLO K DESTRUKCI SPOJE (SVÁRU) MEZI KONSTRUKCE. DODATEČNĚ BUDE PROVEDENO ODDILATOVÁNÍ ATIKOVÉHO PANELU ODESKÁNÍ BETONOVÉ DESKY, KTERÁ TVOŘÍ SPÁDOVÁNÍ NA STŘEŠE V ŠÍŘCE SPÁRY MIN. 20MM. NÁSLEDNÝM ZATEPLENÍM OBÁLKY BUDOVY DOJDE K OCHRANĚ KONSTRUKCI PŘE VLIVY TEPELNÝCH ROZTAŽNOSTÍ A TÍM DOJDE K ZAMEZENÍ POHYBŮ KONSTRUKCÍ.

POZNÁMKA – PZ/03
– SPÁRY OBVODOVÝCH PANELŮ – SPÁRY MEZI JEDNOTLIVÝMI OBVODOVÝMI PANELE VYKAZUJÍ NEDOSTATEČNOU OCHRANU PŘED POVĚTRNOSTNÍMI VLIVY. SPÁRY JSOU VYPLNĚNÉ CEMENTOVOU MALTOU KDE PO ČASE DOCHÁZÍ K DEGRADACI VÝPLŇOVÉHO MATERIÁLU A JAKO OCHRANA JSOU V NĚKTERÝCH MÍSTECH ZALITÉ ASFALTOVOU ZÁLIVKOU. SPÁRA BUDE STAVEBNÍMI ÚPRAVAMI KOMPLETNĚ OBNOVENA. DOJDE K PROŠKRÁBNUTÍ A ODSTRANĚNÍ STÁVAJÍCÍ VÝPLŇOVÉ HMOTY, KTERÁ BUDE NAHRAZENA VODNOU VÝPLŇOVOU HMOTOU S OBDOBNOU PEVNOSTÍ JAKO OBVODOVÉ PANELE. NAPŘ. VYSYPKOU MALTOU NA BETON K VYPLNĚNÍ SPÁR.

POZNÁMKA – PZ/04
– ODHALENÁ VÝZTUŽ BETONOVÝCH PANELŮ – V NĚKTERÝCH MÍSTECH DOCHÁZÍ VLIVEM ZATĚKÁNÍ VODY A POVĚTRNOSTNÍCH PODMÍNEK K DEGRADACI OBVODOVÝCH PANELŮ ROZPADEM BETONU A ODHALENÍ VÝZTUŽE. STAVEBNÍMI ÚPRAVAMI DOJDE K OŠETŘENÍ TĚCHTO MÍST, NESOUDRŽNÉ VRSTVY MUSÍ BÝT ODSTRANĚNY A NA PEVNOU ČÁST. STÁVAJÍCÍ OCELOVÁ VÝZTUŽ BUDE DŮKLADNĚ OČIŠTĚNA A OPATŘENA ANTIKOROZNÍM NÁTĚREM S ADHÉZNÍM MŮSTKEM. NÁSLEDNĚ BUDE OBVODOVÝ PANELE REPROFILOVÁN POMOCÍ VYSYPÁVKOVÉ POLYMERCEMENTOVÉ VÁLKY ZUŠLECHTĚNÉ MALTY NA BETON S INHIBITOREM KORÓZE.

POZNÁMKA – PZ/05
– STÁVAJÍCÍ KZS – NĚKTERÉ ČÁSTI FASÁDY (VIZ. VYZNAČENÍ) JSOU JIŽ ZATEPLENÉ KZS Z PĚNOVÉHO POLYSTYRENU O TL. 80MM. ZATEPLENÍ BUDE KOMPLETNĚ ODSTRANĚNO, VČ. STÁVAJÍCÍ OMÍTKY AŽ NA PEVNÝ PODKLAD. PŘÍPADNĚ VADY FASÁDY BUDOU ŘEŠENY OBDOBNE JAKO NAVRŽENÉ OPATŘENÍ VIDITELNÝCH VAD NA FASÁDĚ. POVRCH FASÁDY BUDE PENETROVÁN, OPATŘEN POSTŘÍKEM CEMENTOVOU MALTOU A JÁDROVOU OMÍTKOU O TL. 10–35MM. NÁSLEDNĚ BUDE PROVEDENO ZATEPLENÍ KZS.

– BAREVNÉ OZNAČENÍ VE VÝKRESE


POZNÁMKA – PZ/06
– FASÁDA OBJEKTU BUDE CELOPLOŠNĚ OSEKÁNA. STÁVAJÍCÍ OMÍTKA BUDE KOMPLETNĚ ODSTRANĚNA AŽ NA NOSNÝ POVRCH BETONOVÉHO OBVODOVÉHO PANELU. OBVODOVÉ PANELE VYKAZUJÍ VELKOU MÍRU NEROVNOSTÍ VLIVEM ŠPATNÉ PROVEDENÉ MONTÁŽE. Z TOHO DŮVODU BUDE ZVOLENA TLOUŠŤKA VYROVŇAVACÍ VRSTVY OMÍTKY PŘÍPŮSOBENA JEDNOTLIVÉ FASÁDĚ TAK, ABY BYL PODKLAD VYROVNANÝ PRO NÁSLEDNĚ PROVEDENÍ KZS. POVRCH BETONOVÉHO PANELU BUDE PENETROVÁN, OPATŘEN POSTŘÍKEM CEMENTOVOU MALTOU A JÁDROVOU OMÍTKOU O TL. 10–25MM, V PŘÍPADĚ VĚTŠÍCH NEROVNOSTÍ SE NAVRHUJE, LOKÁLNĚ V MÍSTĚ ODSKOKU SNÍŽENÍ TL. TEPELNÉHO IZOLANTU O 20MM . NÁSLEDNĚ BUDE PROVEDENO ZATEPLENÍ KZS.

POZNÁMKA – PZ/07
– VYBOURÁNÍ OTVORU PRO NOVÉ NEBO ROZŠÍŘENÍ VÝPLNÍ OTVORŮ

– BAREVNÉ OZNAČENÍ VE VÝKRESE



BAREVNÉ OZNAČENÍ VE VÝKRESE

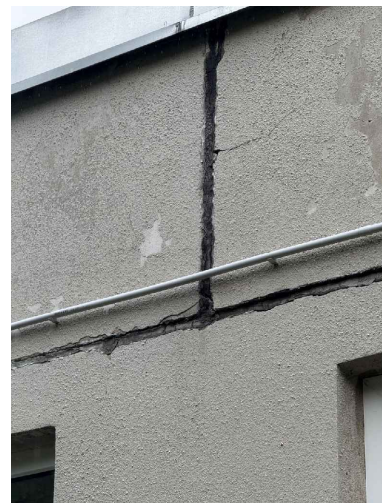

– BAREVNÉ OZNAČENÍ SPÁR VE VÝKRESE



– BAREVNÉ OZNAČENÍ VE VÝKRESE

– BAREVNÉ OZNAČENÍ VE VÝKRESE

POZNÁMKA – PZ/02
– DOZDÍVKY NÁROŽÍ – NÁROŽÍ FASÁDY JSOU DOZDÍVANÉ Z PLYNOSILIKÁTOVÝCH TVÁRNIC. NĚKTERÉ DOZDÍVKY VYKAZUJÍ POSUNUTÍ A NESOUDRŽNOST S PODKLADEM. STAVEBNÍMI ÚPRAVAMI DOJDE K OVĚŘENÍ KOTVENÍ DOZDÍVEK NÁROŽÍ A JEJICH SOUDRŽNOSTI. PŘÍPADNĚ DOJDE K VYBOURÁNÍ DOZDÍVKY A NAHRAZENÍ ZDIVA NOVÝMI OHĚLNÝMI BLOKY O TL. 250MM, KTERÁ BUDE KOTVENA SYSTÉMOVÝMI KOTVAMI K OBVODOVÝM PANELE. NÁSLEDNĚ DOJDE K PROVEDENÍ OPATŘENÍ POSTŘÍKEM CEMENTOVOU MALTOU A JÁDROVOU OMÍTKOU PRO VYROVNÁNÍ S OSTATNÍMI POVRCHY. NÁSLEDNĚ BUDE PROVEDENO ZATEPLENÍ KZS.