

POZNÁMKA – PZ/01
– VYBOČUJÍCÍ ATIKOVÉ ZDIVO – JEDNÁ SE O ATIKOVÉ SENDVIČOVÉ PANELE, KTERÉ JSOU PŘIVAŘENÉ K ŽB SKELETU. PŘEDPOKLÁDÁ SE, ATIKOVÉ PANELE NEJSOU ODDILATOVANÉ OD BETONOVÉ STROPNÍ DESKY A VLIVEM TEPELNÉ ROZTAŽNOSTI DOŠLO K POSUNUTÍ ATIKOVÝCH PANELŮ. STAVEBNÍMI ÚPRAVAMI DOJDE K ODHALENÍ SPOJŮ ATIKOVÉHO ZDIVA S ŽB SKELETEM A OVĚŘENÍ ŽE NEDOŠLO K DESTRUKCI SPOJE (SVÁRU) MEZI KONSTRUKCE. DODATEČNĚ BUDE PROVEDENO ODDILATOVÁNÍ ATIKOVÉHO PANELU ODSEKÁNÍ BETONOVÉ DESKY, KTERÁ TVOŘÍ SPÁDOVÁNÍ NA STŘEŠE V ŠÍŘCE SPÁRY MIN. 20MM. NÁSLEDNÝM ZATEPLENÍM OBÁLKY BUDOVY DOJDE K OCHRANĚ KONSTRUKCI PŘE VLIVY TEPELNÝCH ROZTAŽNOSTÍ A TÍM DOJDE K ZAMEZENÍ POHYBŮ KONSTRUKCÍ.




POZNÁMKA – PZ/02
– DOZDÍVKY NÁROŽÍ – NÁROŽÍ FASÁDY JSOU DOZDÍVANÉ Z PLYNOSILIKÁTOVÝCH TVÁRNIC. NĚKTERÉ DOZDÍVKY VYKAZUJÍ POSUNUTÍ A NESOUDRŽNOST S PODKLADEM. STAVEBNÍMI ÚPRAVAMI DOJDE K OVĚŘENÍ KOTVENÍ DOZDÍVEK NÁROŽÍ A JEJICH SOUDRŽNOSTI. PŘÍPADNĚ DOJDE K VYBOURÁNÍ DOZDÍVKY A NAHRAZENÍ ZDIVA NOVÝMI CIHELNÝMI BLOKY O TL. 250MM, KTERÁ BUDE KOTVENA SYSTÉMOVÝMI KOTVAMI K OBVODOVÝM PANELŮ. NÁSLEDNĚ DOJDE K PROVEDENÍ OPATŘENÍ POSTŘÍKEM CEMENTOVOU MALTOU A JÁDROVOU OMÍTKOU PRO VYROVNÁNÍ S OSTATNÍMI POVRCHY. NÁSLEDNĚ BUDE PROVEDENO ZATEPLENÍ KZS.



POZNÁMKA – PZ/03
– SPÁRY OBVODOVÝCH PANELŮ – SPÁRY MEZI JEDNOTLIVÝMI OBVODOVÝMI PANELE VYKAZUJÍ NEDOSTATEČNOU OCHRANU PŘED POVĚTRNOSTNÍMI VLIVY. SPÁRY JSOU VYPLNĚNÉ CEMENTOVOU MATLOU KDE PO ČASE DOCHÁZÍ K DEGRADACI VÝPLŇOVÉHO MATERIÁLU A JAKO OCHRANA JSOU V NĚKTERÝCH MÍSTECH ZALITÉ ASFALTOVOU ZÁLIVKOU. SPÁRA BUDE STAVEBNÍMI ÚPRAVAMI KOMPLETNĚ OBNOVENA. DOJDE K PROŠKRÁBNUTÍ A ODSTRANĚNÍ STÁVAJÍCÍ VÝPLŇOVÉ HMOTY, KTERÁ BUDE NAHRAZENA VHDNOU VÝPLŇOVOU HMOTOU S OBDOBNOU PEVNOSTÍ JAKO OBVODOVÉ PANELE. NAPŘ. VYSPRÁVKOU MATLOU NA BETON K VYPLNĚNÍ SPÁR.



Pohled 7

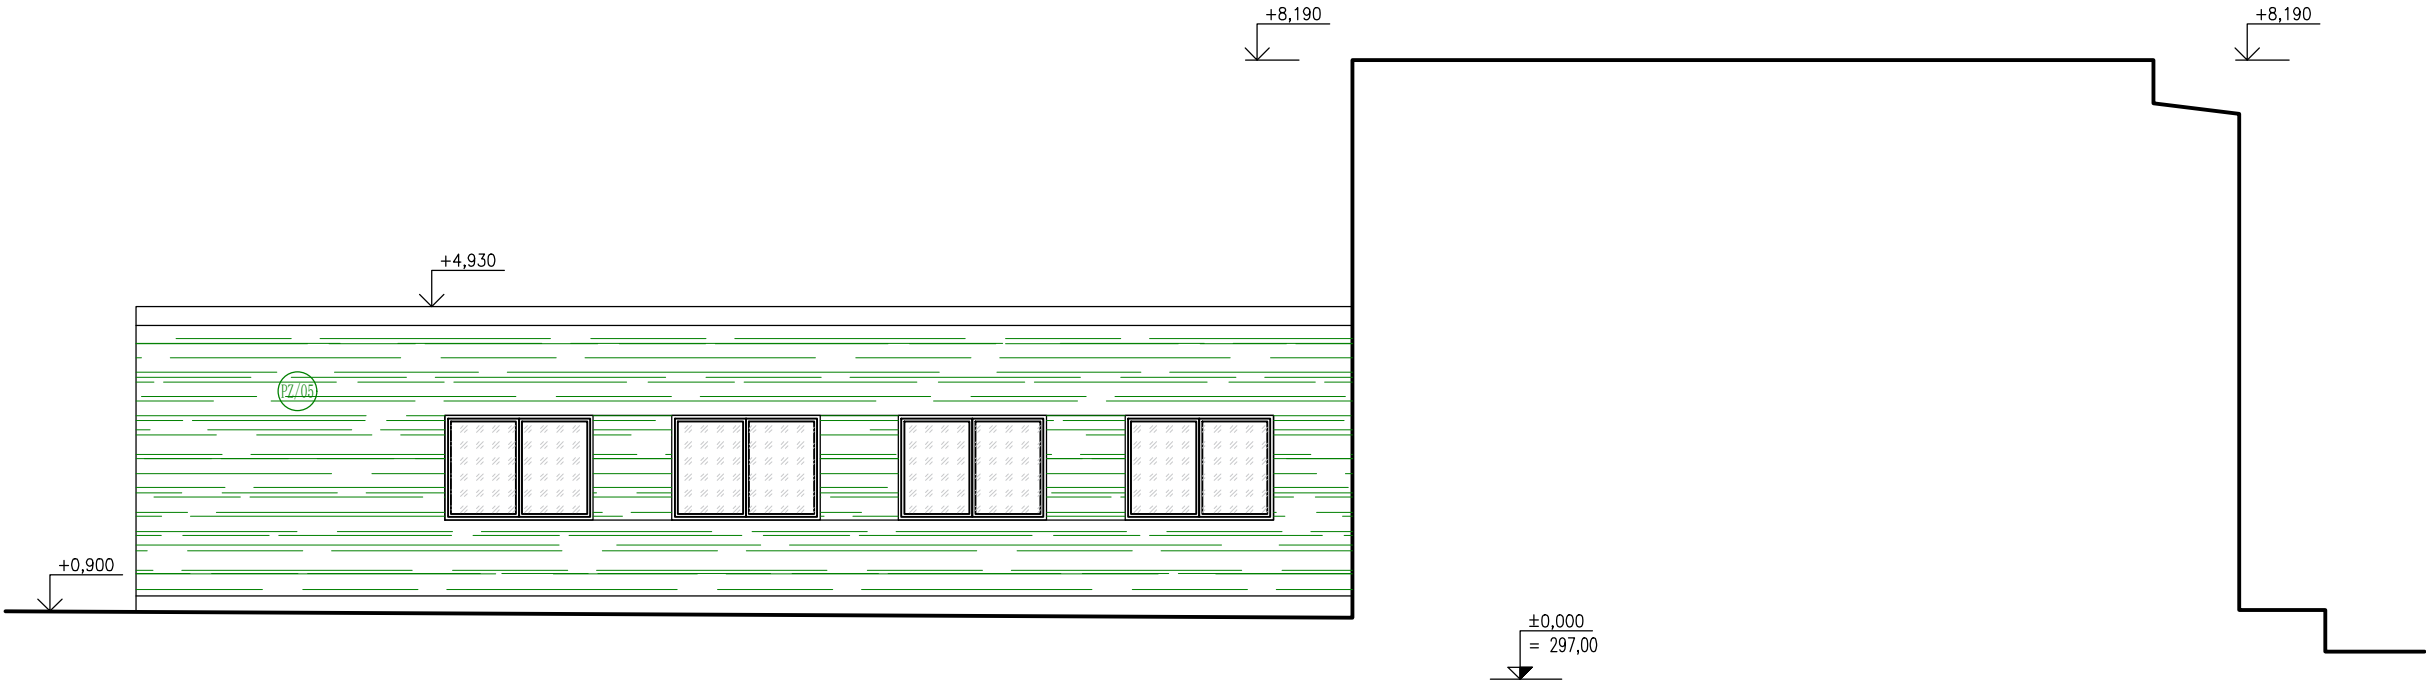

POZNÁMKA – PZ/04
– ODHALENÁ VÝZTUŽ BETONOVÝCH PANELŮ – V NĚKTERÝCH MÍSTECH DOCHÁZÍ VLIVEM ZATÉKÁNÍ VODY A POVĚTRNOSTNÍCH PODMÍNEK K DEGRADACI OBVODOVÝCH PANELŮ ROZPADEM BETONU A ODHALENÍ VÝZTUŽE. STAVEBNÍMI ÚPRAVAMI DOJDE K OŠETŘENÍ TĚCHTO MÍST, NESOUDRŽNÉ VRSTVY MUSÍ BÝT ODSTRANĚNY A NA PEVNOU ČÁST. STÁVAJÍCÍ OCELOVÁ VÝZTUŽ BUDE DŮKLADNĚ OČIŠTĚNA A OPATŘENA ANTIKOROZNÍM NÁTĚREM S ADHÉZNÍM MŮSTKEM. NÁSLEDNĚ BUDE OBVODOVÝ PANEL REPROFILOVÁN POMOCÍ VYSPRÁVKOVÉ POLYMERCEMENTOVÉ VÁLKY ZUŠLECHTĚNÉ MALTY NA BETON S INHIBITOREM KOROZE.



POZNÁMKA – PZ/05
– STÁVAJÍCÍ KZS – NĚKTERÉ ČÁSTI FASÁDY (VIZ. VYZNAČENÍ) JSOU JIŽ ZATEPLENÉ KZS Z PĚNOVÉHO POLYSTYRENU O TL. 80MM. ZATEPLENÍ BUDE KOMPLETNĚ ODSTRANĚNO, VČ. STÁVAJÍCÍ OMÍTKY AŽ NA PEVNÝ PODKLAD. PŘÍPADNÉ VADY FASÁDY BUDOU ŘEŠENY OBDOBNĚ JAKO NAVRŽENÉ OPATŘENÍ VIDITELNÝCH VADA NA FASÁDĚ. POVRCH FASÁDY BUDE PENETROVÁN, OPATŘĚN POSTŘÍKEM CEMENTOVOU MALTOU A JÁDROVOU OMÍTKOU O TL. 10–35MM. NÁSLEDNĚ BUDE PROVEDENO ZATEPLENÍ KZS.



POZNÁMKA – PZ/06
– FASÁDA OBJEKTU BUDE CELOPLOŠNĚ OSEKÁNA. STÁVAJÍCÍ OMÍTKA BUDE KOMPLETNĚ ODSTRANĚNA AŽ NA NOSNÝ POVRCH BETONOVÉHO OBVODOVÉHO PANELU. OBVODOVÉ PANELE VYKAZUJÍ VELKOU MÍRU NEROVNOSTÍ VLIVEM ŠPATNÉ PROVEDENÉ MONTÁŽE. Z TOHO DŮVODU BUDE ZVOLENA TLOUŠŤKA VYROVŇAVACÍ VRSTVY OMÍTKY PŘÍZPŮSOBENA JEDNOTLIVÉ FASÁDĚ TAK, ABY BYL PODKLAD VYROVNANÝ PRO NÁSLEDNĚ PROVEDENÍ KZS. POVRCH BETONOVÉHO PANELU BUDE PENETROVÁN, OPATŘĚN POSTŘÍKEM CEMENTOVOU MALTOU A JÁDROVOU OMÍTKOU O TL. 10–25MM, V PŘÍPADĚ VĚTŠÍCH NEROVNOSTÍ SE NAVRHUJE, LOKÁLNĚ V MÍSTĚ ODSKOKU SNÍŽENÍ TL. TEPELNÉHO IZOLANTU O 20MM . NÁSLEDNĚ BUDE PROVEDENO ZATEPLENÍ KZS.

POZNÁMKA – PZ/07
– VYBOURÁNÍ OTVORU PRO NOVÉ NEBO ROZŠÍŘENÍ VÝPLNÍ OTVORŮ



STUPEŇ PROJEKTU
DOKUMENTACE PRO PROVEDENÍ STAVBY

ODPOVĚDNÝ PROJEKTANT
Ing.arch. Jakub Volka ČKA 03947

INVESTOR
Úřad městské části Praha 11
Ocelíkova 672/1, Praha 149 41

ČÁST DOKUMENTACE
D_STAVEBNÍ ČÁST

OBSAH VÝKRESU
D.1.1- SANACE – POHLED 7

MĚŘÍTKO
1:100

FORMÁT
5xA4

DATUM
01/2026

REVIZE
XXX

ČÍSLO VÝKRESU / REVIZE
ČÍSLO PARÉ

D.1.1.124