

Snížení energetické
náročnosti MČ Praha 11

Vidimova 1324/4 a 1325/2, Praha-Chodov.

STUPEŇ PROJEKTU +/- 0,000 = 299,330 B.p.v.

ODPOVĚDNÝ PROJEKTANT

Ing.arch. Jakub Volka, ČKA 03947
733 575 363, jakub.volka@basepoint.cz

VYPRACOVAL

INVESTOR

Městská část Praha 11
Ocelíková 672/1, 149 41, Praha 4

DÍL

ČÁST DOKUMENTACE

OBSAH VÝKRESU

Detail_03 - Okno - parapet

MĚŘÍTKO	FORMÁT
	2 X A4

DATUM	1.VYDÁNÍ
02/2026	


STUPEŇ	DÍL	ČÁST	ČÍSLO	PŘÍLOHA	REVIZE
DPS	D	1.1.	131.3		

ZPRACOVATEL ČÁSTI

basepoint s.r.o.
V Benátkách 2350/6
149 00, Praha 4
www.basepoint.cz

GENERÁLNÍ PROJEKTANT

basepoint s.r.o.
V Benátkách 2350/6
149 00, Praha 4
www.basepoint.cz

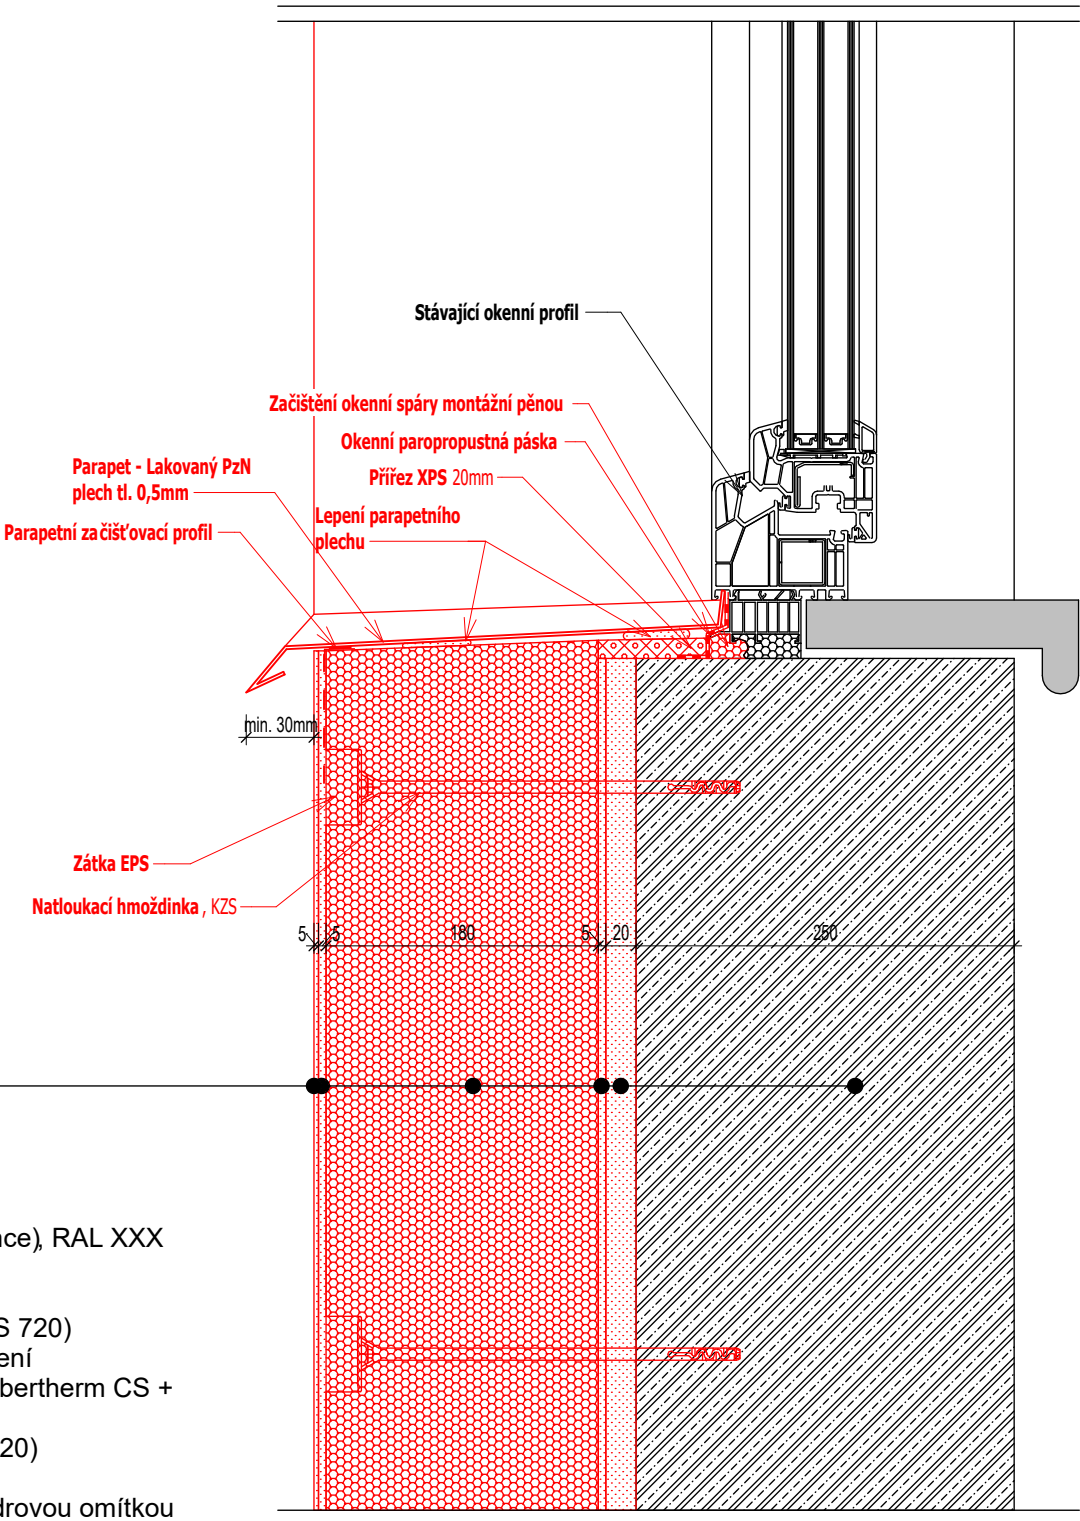

Skladba OP1 (fasáda):

Skladba systému – ucelená dodávka

- silikonová omítka tl. 3mm (např. Weberpas aquabalance), RAL XXX
- podkladní nátěr šedý (např. Weberpas podklad UNI)
- armovací tkanina (např. Webertherm 131)
- základní vrstva tl. 5mm (např. Webertherm elastik LZS 720)
- tepelná izolace z šedého EPS GREY tl. 180mm - kotvení hmoždinkami s ocelovým šroubovacím trnem (např. webertherm CS + zátka ze šedého EPS)
- lepicí vrstva tl. 5mm (např. Webertherm elastik LZS 720)
- penetrační nátěr (např. Weberpodklad A)
- vyrovnávací omítka - postřík cementovou maltou a jádrovou omítkou (např. weberdur podhoz + weberdur JRU), tl.10 - 25mm
- STÁVAJÍCÍ ZDIVO - obvodový panel (očištěné, zbavené nesoudržných částí, vyspáované, reprofilované)

- FASÁDA JE UCELENÝ SYSTÉM DODÁVANÝ JAKO CELEK SE ZÁRUKOU OD DODAVATELE, PROVEDENÍ DLE TYPOVÝCH ŘEŠENÍ VYBRANÉHO SYSTÉMU, DODÁVKA KOMPLETIZOVANÁ VČETNĚ SOUVISEJÍCÍCH KLEMPÍŘSKÝCH PRVKŮ, KOTEVNÍHO A SPOJOVACÍHO MATERIÁLU