


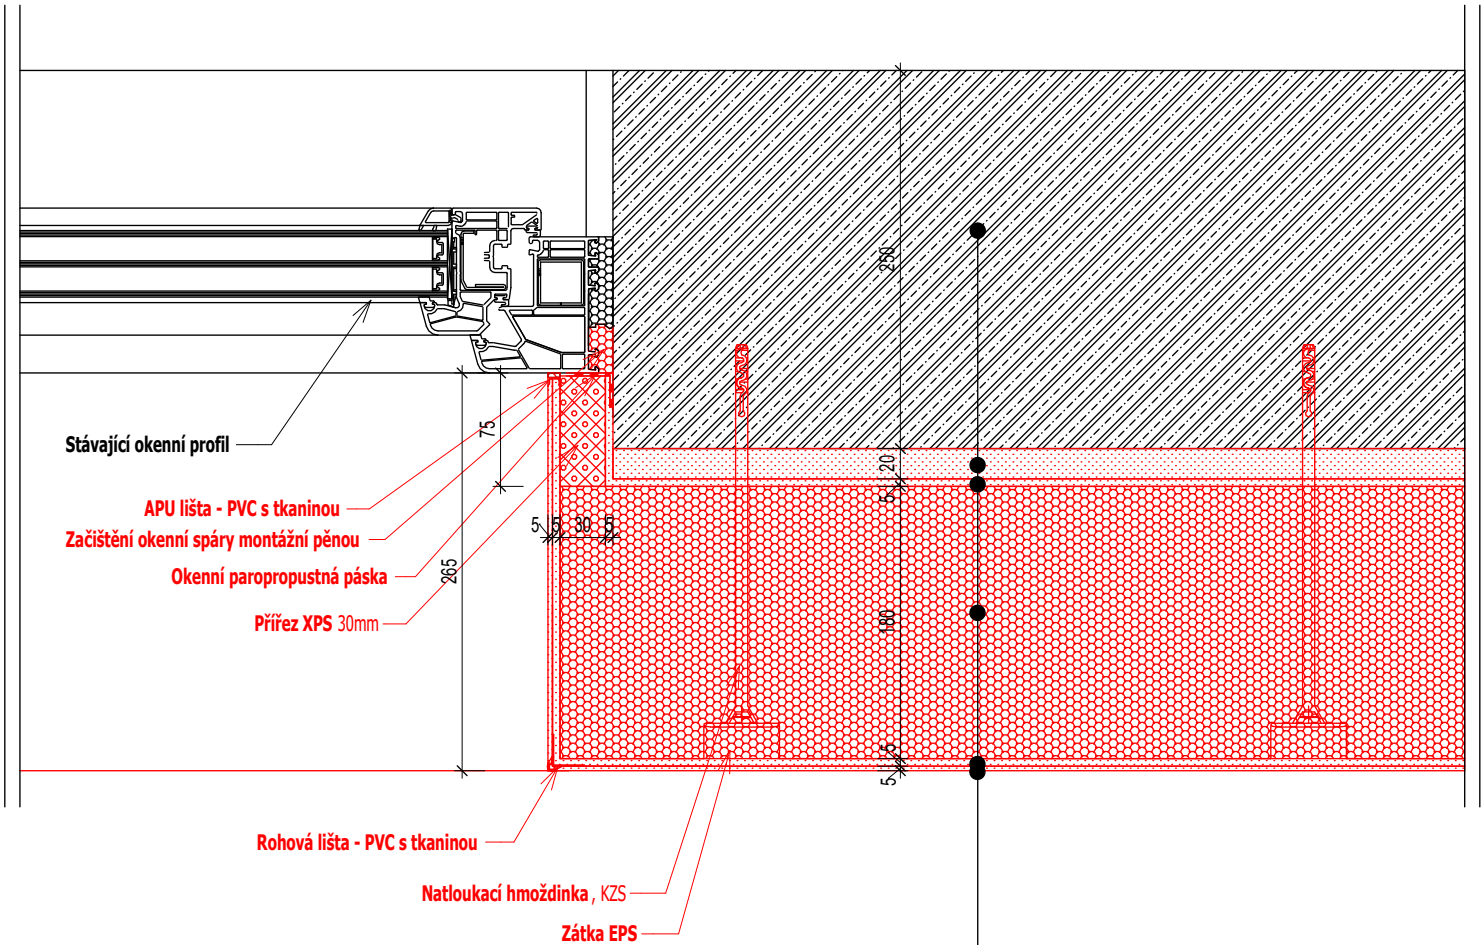

Skladba OP1 (fasáda):

Skladba systému – ucelená dodávka

- silikonová omítka tl. 3mm (např. Weberpas aquabalance), RAL XXX
- podkladní nátěr šedý (např. Weberpas podklad UNI)
- armovací tkanina (např. Webertherm 131)
- základní vrstva tl. 5mm (např. Webertherm elastik LZS 720)
- tepelná izolace z šedého EPS GREY tl. 180mm - kotvení hmoždinkami s ocelovým šroubovacím trnem (např. webertherm CS + zátka ze šedého EPS)
- lepicí vrstva tl. 5mm (např. Webertherm elastik LZS 720)
- penetrační nátěr (např. Weberpodklad A)
- vyrovnávací omítka - postřík cementovou maltou a jádrovou omítkou (např. weberdur podhoz + weberdur JRU), tl.10 - 25mm
- STÁVAJÍCÍ ZDIVO - obvodový panel (očistěné, zbavené nesoudržných částí, vyspávané, reprofilované)

- FASÁDA JE UCELENÝ SYSTÉM DODÁVANÝ JAKO CELEK SE ZÁRUKOU OD DODAVATELE, PROVEDENÍ DLE TYPOVÝCH ŘEŠENÍ VYBRANÉHO SYSTÉMU, DODÁVKA KOMPLETIZOVANÁ VČETNĚ SOUVISEJÍCÍCH KLEMPÍŘSKÝCH PRVKŮ, KOTEVNÍHO A SPOJOVACÍHO MATERIÁLU