

Snížení energetické
náročnosti MČ Praha 11

Vidimova 1324/4 a 1325/2, Praha-Chodov.

STUPEŇ PROJEKTU +/- 0,000 = 299,330 B.p.v.

ODPOVĚDNÝ PROJEKTANT

Ing.arch. Jakub Volka, ČKA 03947
733 575 363, jakub.volka@basepoint.cz

VYPRACOVAL

INVESTOR

Městská část Praha 11
Ocelíková 672/1, 149 41, Praha 4

DÍL

ČÁST DOKUMENTACE

OBSAH VÝKRESU

Detail_07 - Záchytný systém -
střecha

MĚŘÍTKO FORMÁT
2 X A4

DATUM 1.VYDÁNÍ
02/2026


STUPEŇ	DÍL	ČÁST	ČÍSLO	PŘÍLOHA	REVIZE
DPS	D	1.1.	131.7		

ZPRACOVATEL ČÁSTI

basepoint s.r.o.
V Benátkách 2350/6
149 00, Praha 4
www.basepoint.cz

GENERÁLNÍ PROJEKTANT

basepoint s.r.o.
V Benátkách 2350/6
149 00, Praha 4
www.basepoint.cz

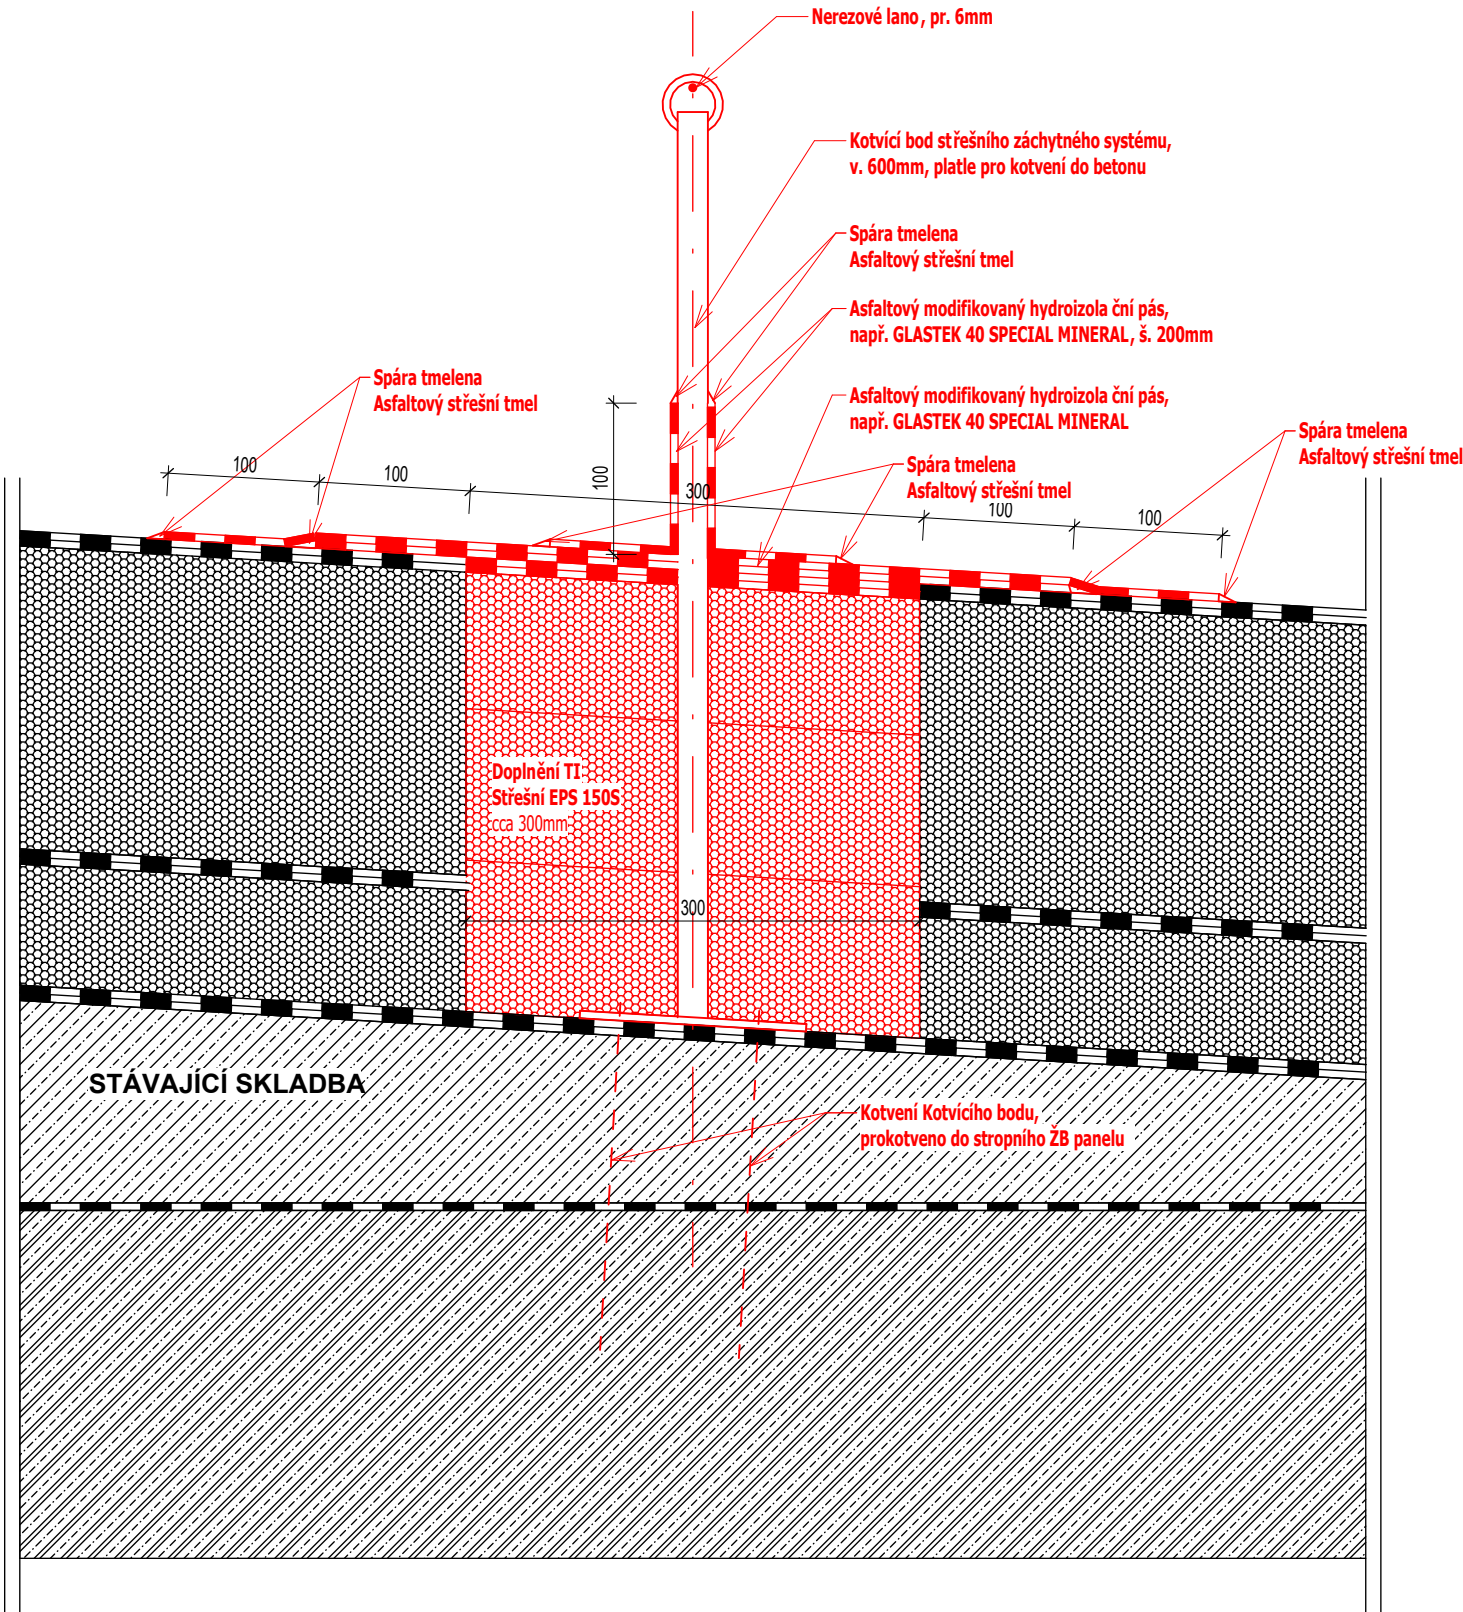

- STŘEŠNÍ SYSTÉM JE UCELENÝ SYSTÉM DODÁVANÝ JAKO CELEK SE ZÁRUKOU OD DODAVATELE, PROVEDENÍ DLE TYPOVÝCH ŘEŠENÍ
VYBRANÉHO SYSTÉMU, DODÁVKA KOMPLETIZOVANÁ VČETNĚ SOUVISEJÍCÍCH PRVKŮ, KOTEVNÍHO A SPOJOVACÍHO MATERIÁLU