


PŮDORYS V ÚROVNI NÁSTUPIŠTĚ (ŘEZ 1-1)

1:100

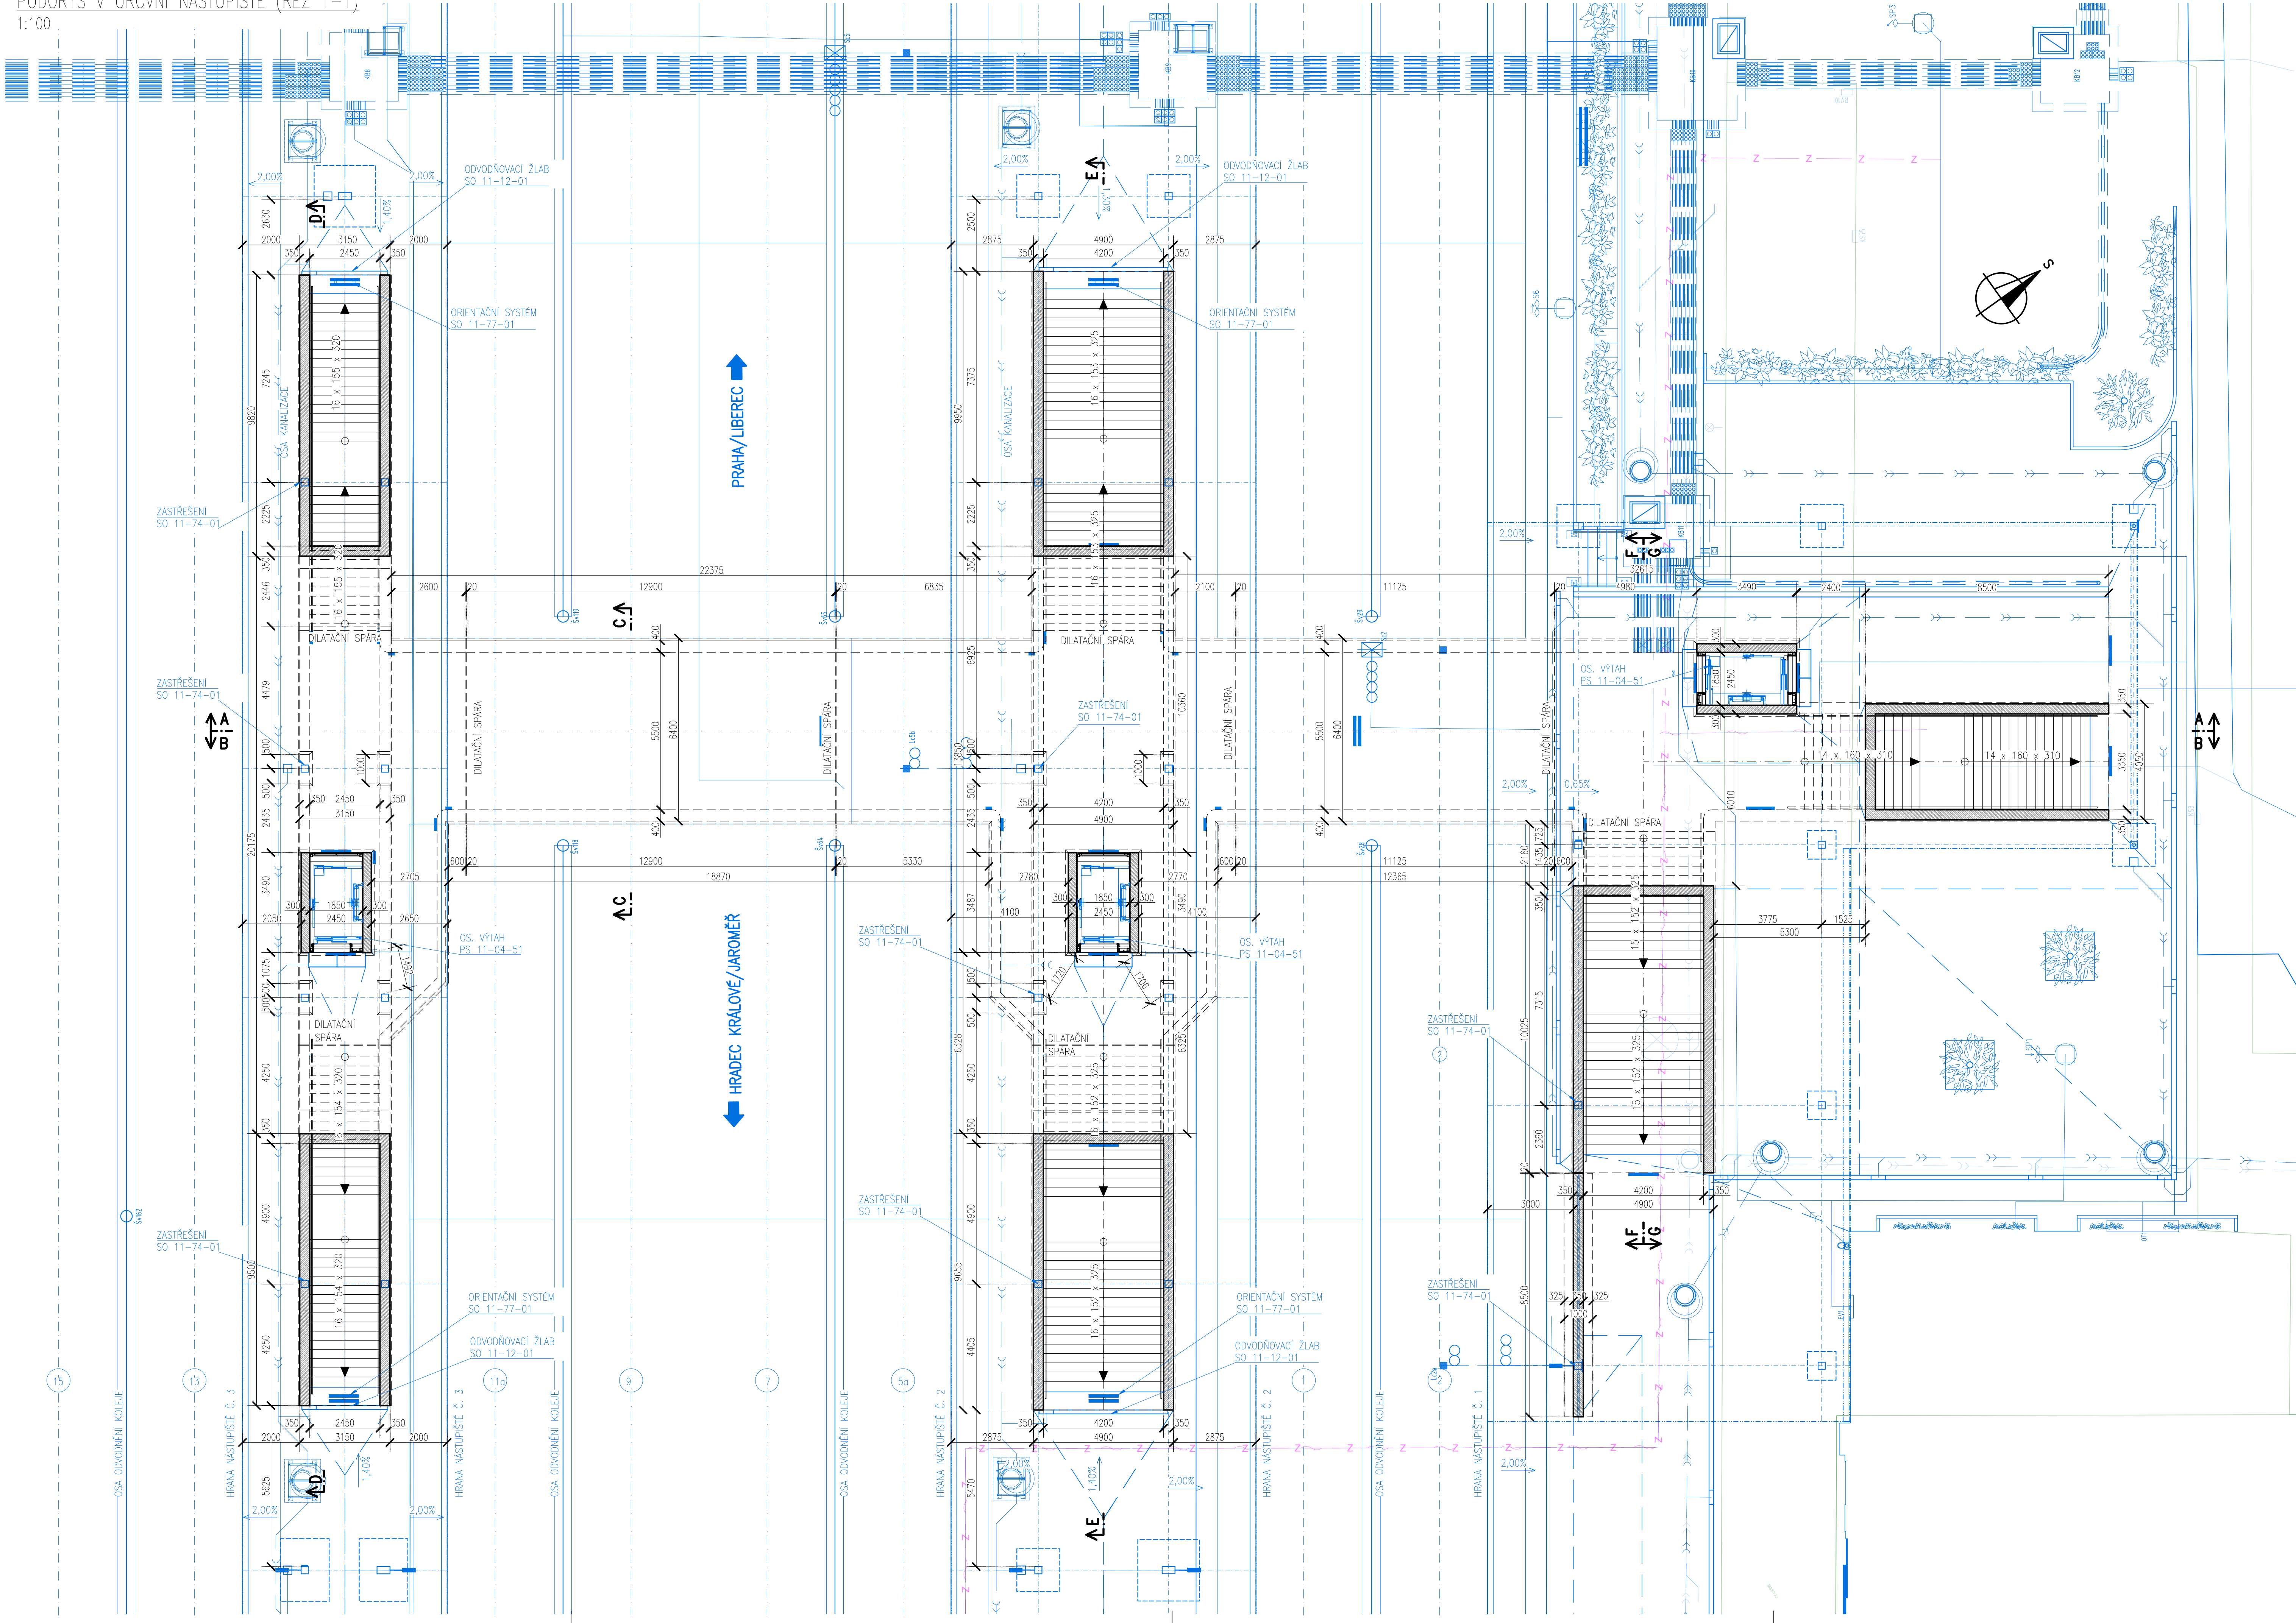

MATERIÁL:	
BETON:	C30/37 XC4, XD1, XF2, XA1
PODCHOD	- CI 0,4 - Dmax 22, max. průsak 35 mm
	C25/30 XC2, XF1
	- CI 0,4 - Dmax 16
PODKLADNÍ BETON	C16/20 X0
SPÁDOVÝ BETON	C20/25 XF2
VYROVNÁVACÍ MAZANINA	C20/25 XF2
PŘEBETONOVÁNÍ ZPĚTNÉHO SPOJE	C20/25n
OCEL:	
VÝZTUŽ	B500B

POZNÁMKY:
v PŮDORYSE POD ÚROVNÍ NÁSTUPIŠTĚ NEJSOU ZOBRAZENY NIKY PRO MONITORY,
KABELOVÉ SKŘÍNĚ APOD.
TYTO JSOU ZOBRAZENY POUZE NA VÝKRESECH TVARU S OHLEDEM NA PŘEHLEDNOST
DOKUMENTACE.

Ministerstvo dopravy Státní fond dopravní infrastruktury	
Jiná ověření:	Paré:
Orientační schéma:	Razítko oprávněné osoby:
Podpis: Datum:	
Revize:	Datum:
-	-
-	-
-	-
-	-
000	31.08.2025
Odevzdání OSP+PDPS v čístopisu	
Ing. Barbora mužiková, Ph.D.	
Stavebník/Investor:	Správa železnic, státní organizace
Adresa:	Diálská 1003/7, 110 00 Praha 1
Zástupce investora:	Stavební správa západ
Adresa:	Ke Štvanici 656/3, 186 00 Praha 8 - Karlín
Zhotovitel díla:	Ps + SB + A4 - ŽST Turnov DSP, PDPS
Adresa:	U Elektrky 830/2b, 198 00 Praha 9
Kontakt:	T: +420 281 090 860 E: firma@projekt-servis.cz
Zhotovitel objektu:	PROJEKT servis spol. s r.o.
Adresa:	U Elektrky 830/2b, 198 00 Praha 9
Kontakt:	T: +420 281 090 860 E: firma@projekt-servis.cz
Hlavní projektant (HIP):	Ing. Martin Koudełka
Specialista:	Ing. Radomír Hanák
Název stavby/akce:	Rekonstrukce žst. Turnov
Název části:	Mosty, propustky a zdi
Název objektu/díle části:	Železniční most v km 123,980 (Podchod)
Název přílohy:	Půdorys v úrovni nástupiště (řez 1-1)
Název dílčí části přílohy:	-
Odpovědný projektant:	Ing. Aleš Menšík
Kraj:	Liberecký
Stupeň dokumentace:	PDPS
Smluvní datum zpracování:	31.08.2025