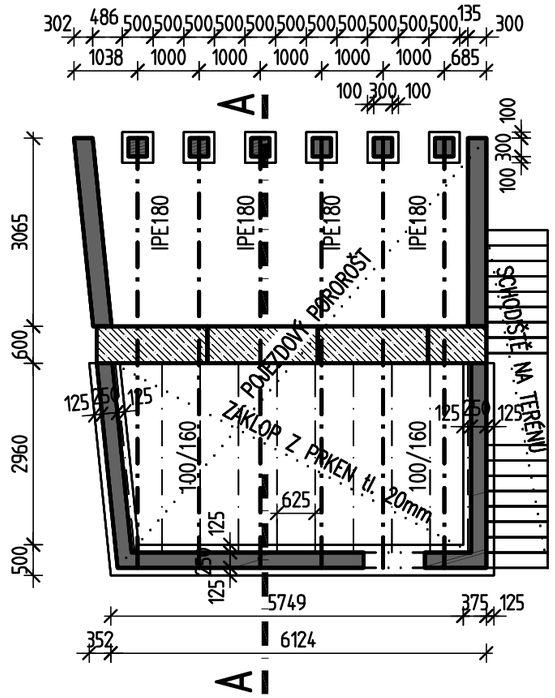

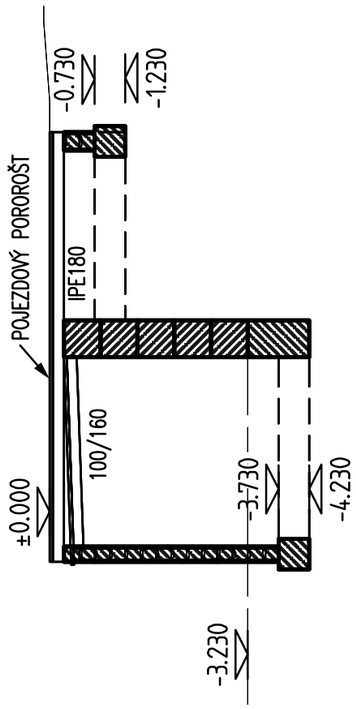

MATERIÁL:

BETON VYZTUŽENÝCH KONSTRUKCÍ
C25/30 XC3,XF1,XA1 - CL 0.4 - Dmax. 22-S3

BETON PROSTÝCH PASŮ
C16/20 XC0

TVAROVKY ZTRACENÉHO BEDNĚNÍ
BETONOVÉ KVÁDRY H-BLOK STANDARD

KONSTRUKČNÍ OCEL
S235 - žárový pozink

SPOJ. MATERIÁL
8.8 - žárový pozink

ŘEZIVO
C24

LEGENDA:

- SVISLÁ KONSTRUKCE PŘÍSLUŠNÉHO PODLAŽÍ, PŘILÉHAJÍCÍ K DOLNÍ HRANĚ VODOROVNÉ KONSTRUKCE ŽELEZOBETON/TVAROVKY ZTRACENÉHO BEDNĚNÍ
- SVISLÁ KONSTRUKCE PŘÍSLUŠNÉHO PODLAŽÍ, PŘILÉHAJÍCÍ K DOLNÍ HRANĚ VODOROVNÉ KONSTRUKCE BETONOVÉ KVÁDRY
- SVISLÁ KONSTRUKCE VYŠŠÍHO PODLAŽÍ, PŘILÉHAJÍCÍ K HORNÍMU LÍCI STROPNÍ DESKY PŘÍSLUŠNÉHO PODLAŽÍ
- DOLNÍ OBRYS VODOROVNÉ KONSTRUKCE PŘÍSLUŠNÉHO PODLAŽÍ
- HORNÍ OBRYS VODOROVNÉ KONSTRUKCE PŘÍSLUŠNÉHO PODLAŽÍ
- OTVOR VE VODOROVNÉ KONSTRUKCI
- PROSTUP SVISLOU KONSTRUKCÍ PŘÍSLUŠNÉHO PODLAŽÍ
  vvv – VÝŠKA [mm], k.kkk – VÝŠKOVÁ KÓTA [m]
  vvv HH-k.kkk DH – DOLNÍ HRANA, HH – HORNÍ HRANA, OSA – OSA PROSTUPU
- OTVOR VE SVISLÉ KONSTRUKCÍ PŘÍSLUŠNÉHO PODLAŽÍ
  vvv – VÝŠKA [mm], k.kkk – VÝŠKOVÁ KÓTA [m]
  vvv DH-k.kkk DH – DOLNÍ HRANA, HH – HORNÍ HRANA, OSA – OSA PROSTUPU
- XXX KÓTA KONSTRUKCE VZTAŽENÁ K ±0,000 OBJEKTU
  ŘEZ NEBO SKLOPENÝ ŘEZ
  XXX KÓTA KONSTRUKCE VZTAŽENÁ K ±0,000 OBJEKTU

Ing. JAN TVARDÍK
Autorizovaný inženýr pro statiku a dynamiku staveb
ČKAIT - 0012219

Digitálně podepsal Ing. Jan Tvardík
Datum: 2026.02.16 16:19:20 +01'00'

±0,000=+673,30 m n.m. Bpv

projekt:
Zahradní sklad a přístupové schodiště k RD
parc. č. 1094/16, st.1022
k.ú. Jáchymov [656437]

stavebník:
Mgr. Jindřich Volný
Fibichova 733
Jáchymov
362 51

dodavatel:
TeAnau s.r.o.
Čerčanská 624/8
140 00 Praha 4
IČ: 01828894

vypracoval:
Ing. Václav Bendík

zodpovědný projektant:
Ing. Jan Tvardík

stupeň: DSP

část: SKR

datum: 01/2026

název výkresu:
ZAHRADNÍ SKLAD
VÝKRES TVARU

měřítko: 1:100

číslo paré:

číslo výkresu: D.2.3.01

index: 00

Dokumentace je autorským dílem společnosti TeAnau s.r.o., IČ: 01828894, teanau@teanau.cz. VŠECHNA PRÁVA VYHRAZENA