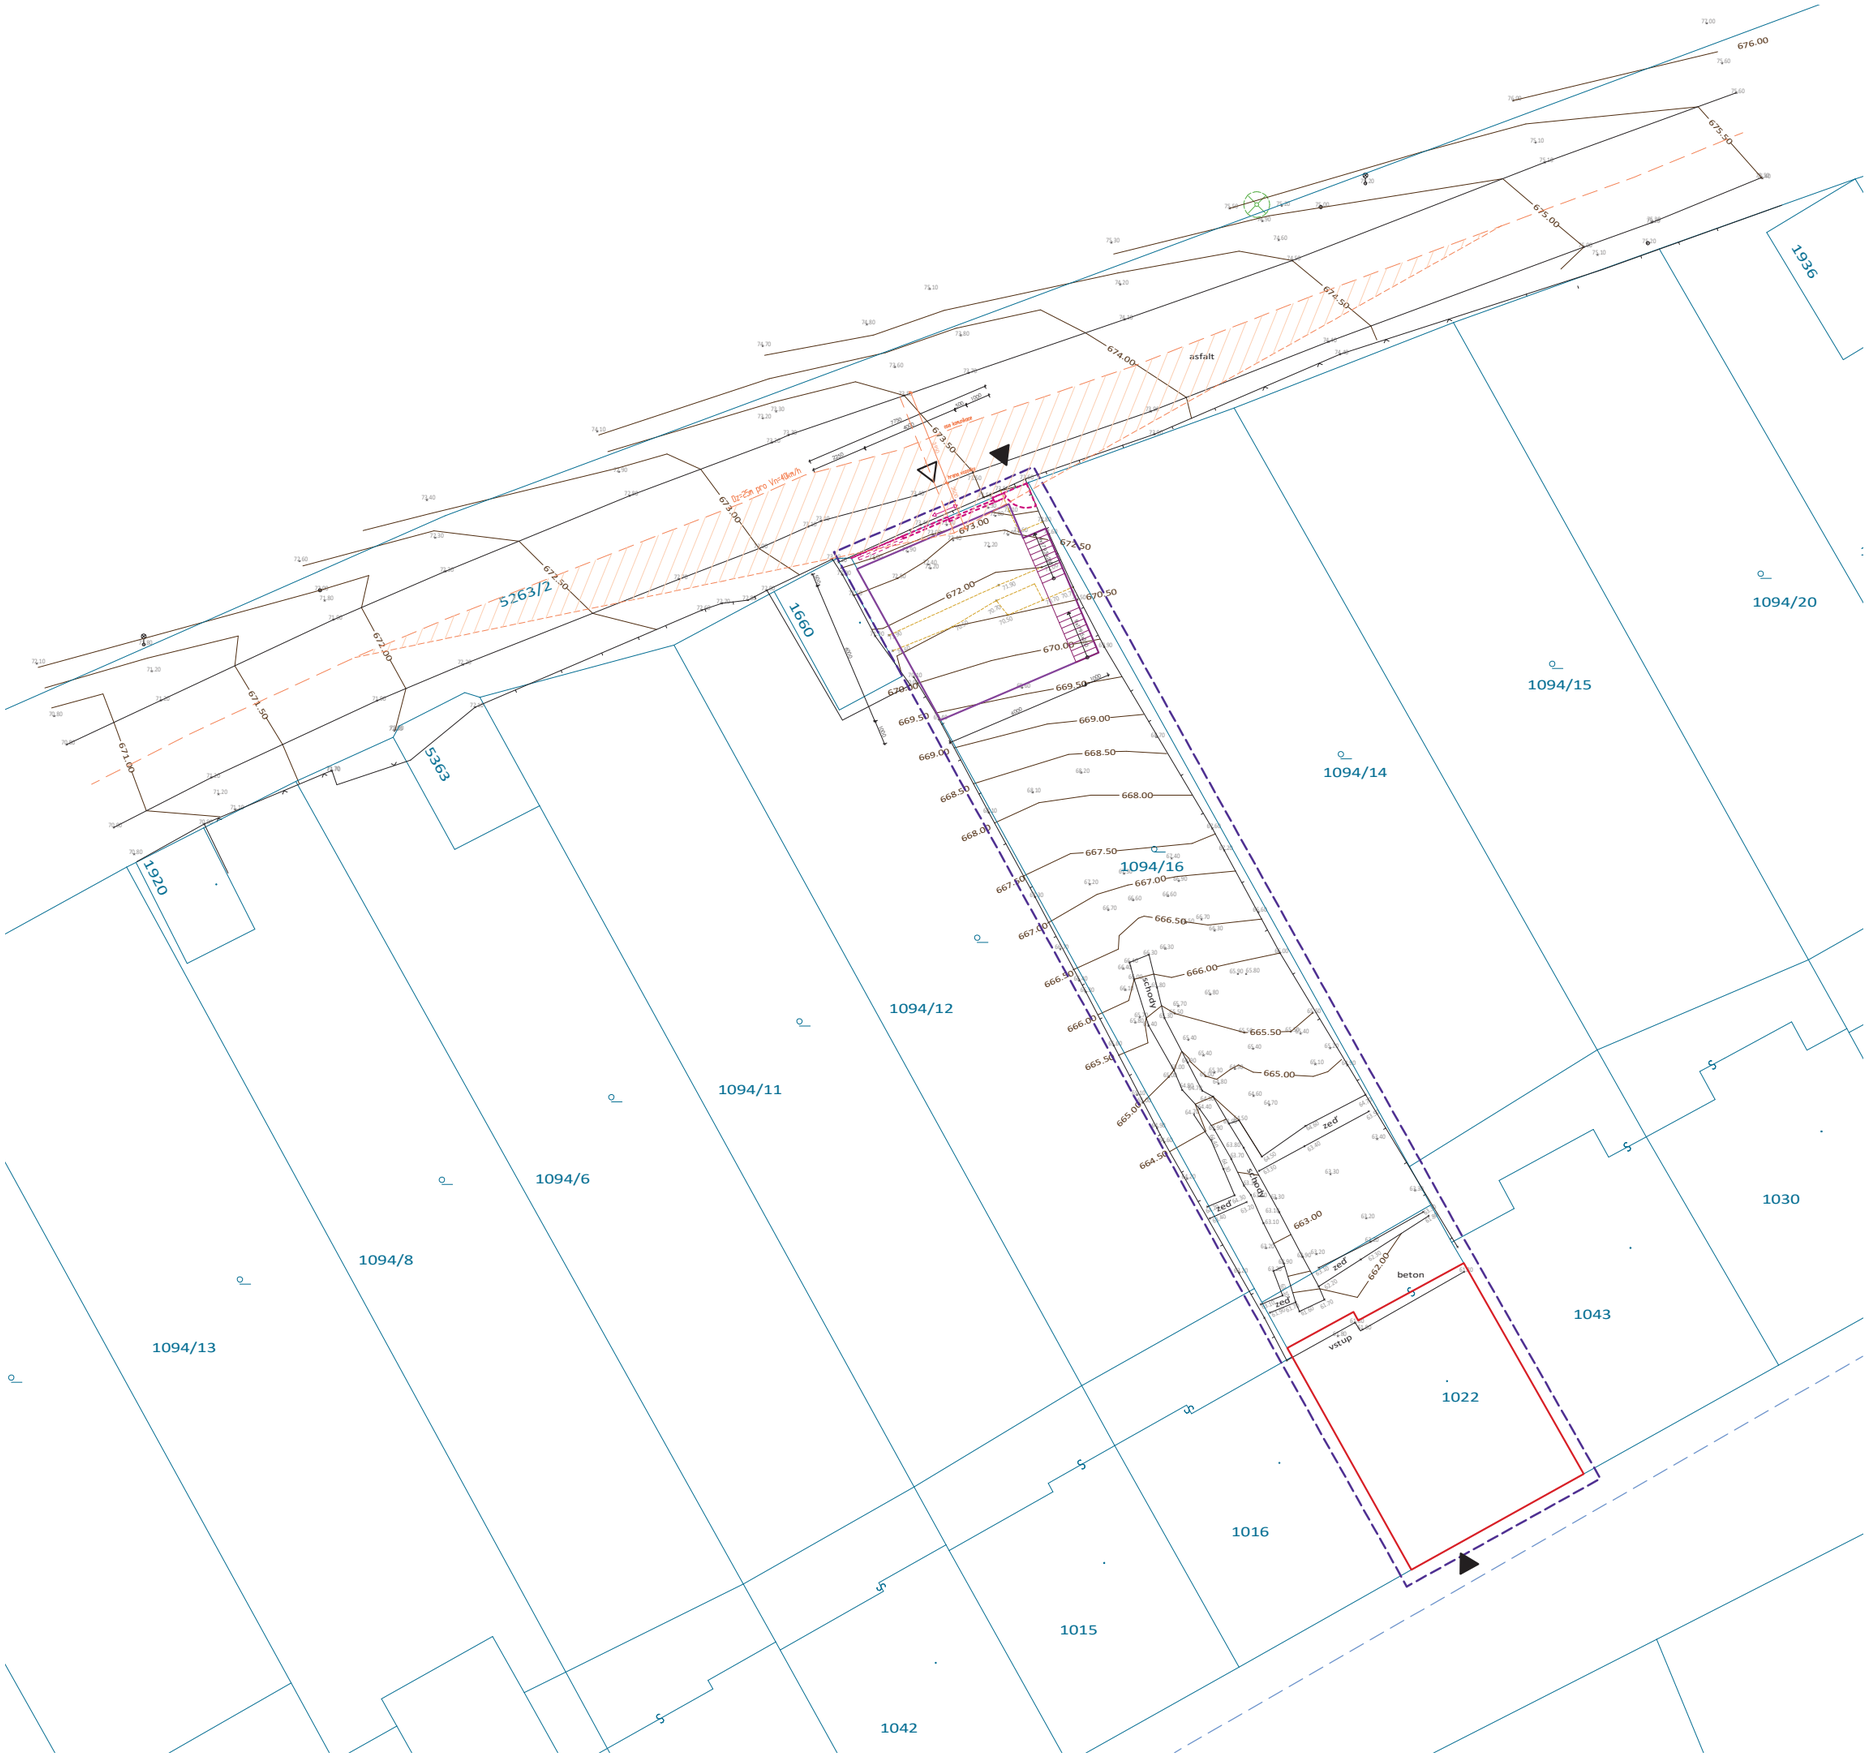

legenda

- stávající objekt RD - stavebně upravovaný
- navrhovaný objekt parkovacího stání
- hranice podzemní části navrhované budovy
- dotčený pozemek
- katastrální mapa
- Ploty
- bourané konstrukce původního uspořádání zahrady
- vstup / vjezd
- navrhovaný plot a vjezd / vstup
- zpevněné plochy
- rozhledové trojúhelníky

legenda - sítě

- silnoproud - stávající
- EP elektroinstalační pilířek - stávající
- silnoproud vedení - sloup - stávající
- RE rozvaděč elektroměrový - stávající
- vodovod - stávající
- vodovod - objekty na povrchu
- studna - stávající
- kanalizace splašková - návrh
- kanalizace dešťová - návrh
- plynovod - stávající
- slaboproud - stávající

revize	datum	popis
02	02/2026	úprava schodiště po zapracování statiky
01	10/2025	doplnění rozhledových poměrů
00	09/2025	vydání dokumentace

Zahradní sklad a přístupové schodiště k RD

č.p. 733, Jáchymov,

parc. č. 1094/16, st.1022, k.ú. Jáchymov [656437]

razítko/podpis
autorizovaný projektant

Ing. arch. Marek Smolka
tel.: +420 732 618 505, email: smolka@smasharch.cz
autorizace: 05394

AUTORIZOVANÝ ARCHITEKT (A1) Ing. arch. Marek Smolka ČKA 05 394 ČESKÁ REPUBLIKA

Digitálně podepsal Ing. arch. Marek Smolka
Datum: 2026.02.05 10:50:07 +01'00'

paré

investor
Volný Jindřich Mgr.
Fibichova 733, 36251 Jáchymov

zpracovatel projektové dokumentace/generální projektant
SMASH architekti s.r.o.
Vodňanského 1008/2, Břevnov, 169 00 Praha 6
IČO: 17666902

projektový stupeň
dokumentace pro povolení záměru

část
C Situační výkresy

projektant části
Ing. arch. Marek Smolka
tel.: +420 732 618 505, email: smolka@smasharch.cz

název výkresu
Koordinační situační výkres

datum	měřítko	číslo výkresu
09/2025	1:200	**C.3**