Dokumentace je autorským dílem společnosti TeAnau s.r.o., IČ: 01828894, teanau@teanau.cz. VŠECHNA PRÁVA VYHRAZENA

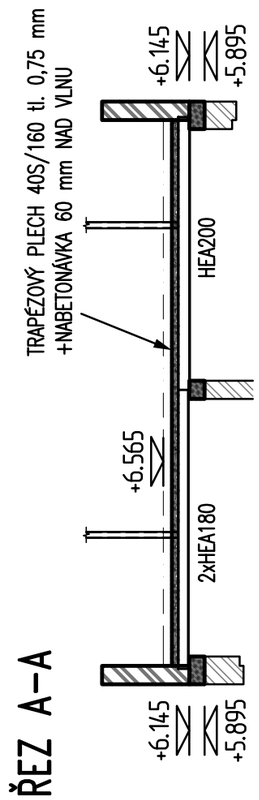

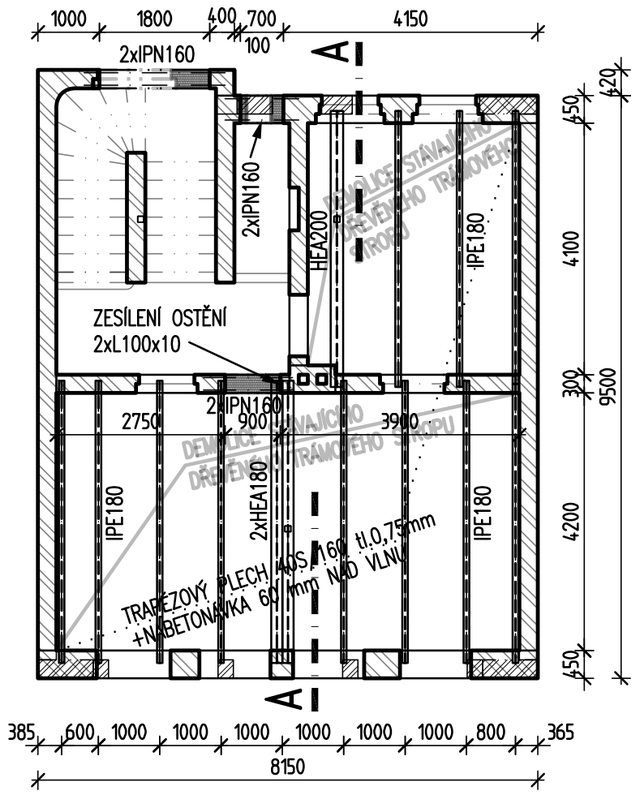

MATERIÁL:

BETON CHRÁNĚNÝCH KONSTRUKCÍ

C25/30 XC1 - CL 0.4 - Dmax. 22-S3

ZDIVO

CIHLA PLNÁ PÁLENÁ P10 NA MALTU M10

KONSTRUKČNÍ OCEL

S235

SPOJ. MATERIÁL

8.8

±0,000=+662,05 m n.m. Bpv

LEGENDA:

- SVISLÁ KONSTRUKCE PŘÍSLUŠNÉHO PODLAŽÍ, PŘILÉHAJÍCÍ K DOLNÍ HRANĚ VODOROVNÉ KONSTRUKCE ŽELEZOBETON/TVAROVKY ZTRACENÉHO BEDNĚNÍ
- SVISLÁ KONSTRUKCE PŘÍSLUŠNÉHO PODLAŽÍ, PŘILÉHAJÍCÍ K DOLNÍ HRANĚ VODOROVNÉ KONSTRUKCE NOVÉ ZDIVO
- DEMOLOVANÁ KONSTRUKCE
- SVISLÁ KONSTRUKCE PŘÍSLUŠNÉHO PODLAŽÍ, PŘILÉHAJÍCÍ K HORNÍMU LÍCI DESKY PŘÍSLUŠNÉHO PODLAŽÍ STÁVAJÍCÍ ZDIVO
- SVISLÁ KONSTRUKCE VYŠŠÍHO PODLAŽÍ, PŘILÉHAJÍCÍ K HORNÍMU LÍCI STROPNÍ DESKY PŘÍSLUŠNÉHO PODLAŽÍ
- DOLNÍ OBRYS VODOROVNÉ KONSTRUKCE PŘÍSLUŠNÉHO PODLAŽÍ
- HORNÍ OBRYS VODOROVNÉ KONSTRUKCE PŘÍSLUŠNÉHO PODLAŽÍ
- OTVOR VE VODOROVNÉ KONSTRUKCI
- PROSTUP SVISLOU KONSTRUKCÍ PŘÍSLUŠNÉHO PODLAŽÍ — vvv – VÝŠKA [mm], k.kkk – VÝŠKOVÁ KÓTA [m]; DH – DOLNÍ HRANA, HH – HORNÍ HRANA, OSA – OSA PROSTUPU (vvv HH-k.kkk)
- OTVOR VE SVISLÉ KONSTRUKCÍ PŘÍSLUŠNÉHO PODLAŽÍ — vvv – VÝŠKA [mm], k.kkk – VÝŠKOVÁ KÓTA [m]; DH – DOLNÍ HRANA, HH – HORNÍ HRANA, OSA – OSA PROSTUPU (vvv DH-k.kkk)
- XXX KÓTA KONSTRUKCE VZTAŽENÁ K ±0,000 OBJEKTU; ŘEZ NEBO SKLOPENÝ ŘEZ; XXX KÓTA KONSTRUKCE VZTAŽENÁ K ±0,000 OBJEKTU

Ing. JAN TVARDÍK – Autorizovaný inženýr pro statiku a dynamiku staveb – ČKAIT - 0012219

Digitálně podepsal Ing. Jan Tvardík
Datum: 2026.02.16 16:17:49 +01'00'

projekt:

Řadový rodinný dům
Fibichova č.p. 733

parc. č. 1094/16, st.1022
k.ú. Jáchymov [656437]

stavebník:

Mgr. Jindřich Volný
Fibichova 733
Jáchymov
362 51

dodavatel:

TeAnau s.r.o.
Čerčanská 624/8
140 00 Praha 4
IČ: 01828894

TeAnau

vypracoval: Ing. Václav Bendík

zodpovědný projektant: Ing. Jan Tvardík

stupeň: DSP

část: SKR

datum: 01/2026

název výkresu:

2. NADZEMNÍ PODLAŽÍ
VÝKRES TVARU

měřítko: 1:100

číslo paré:

číslo výkresu: D.2.3.03

index: 00